

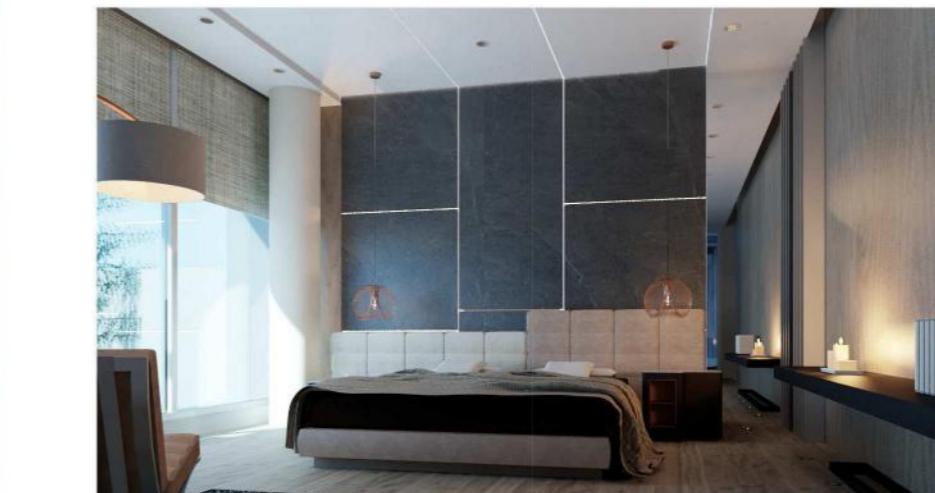
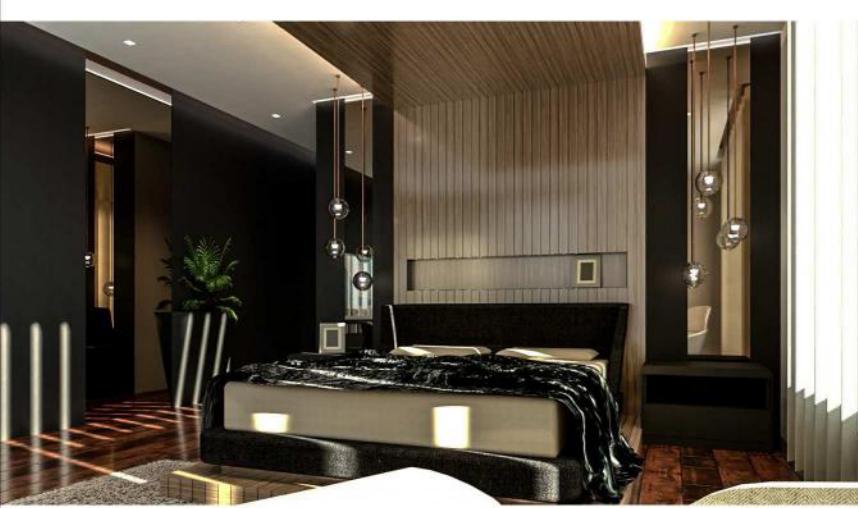
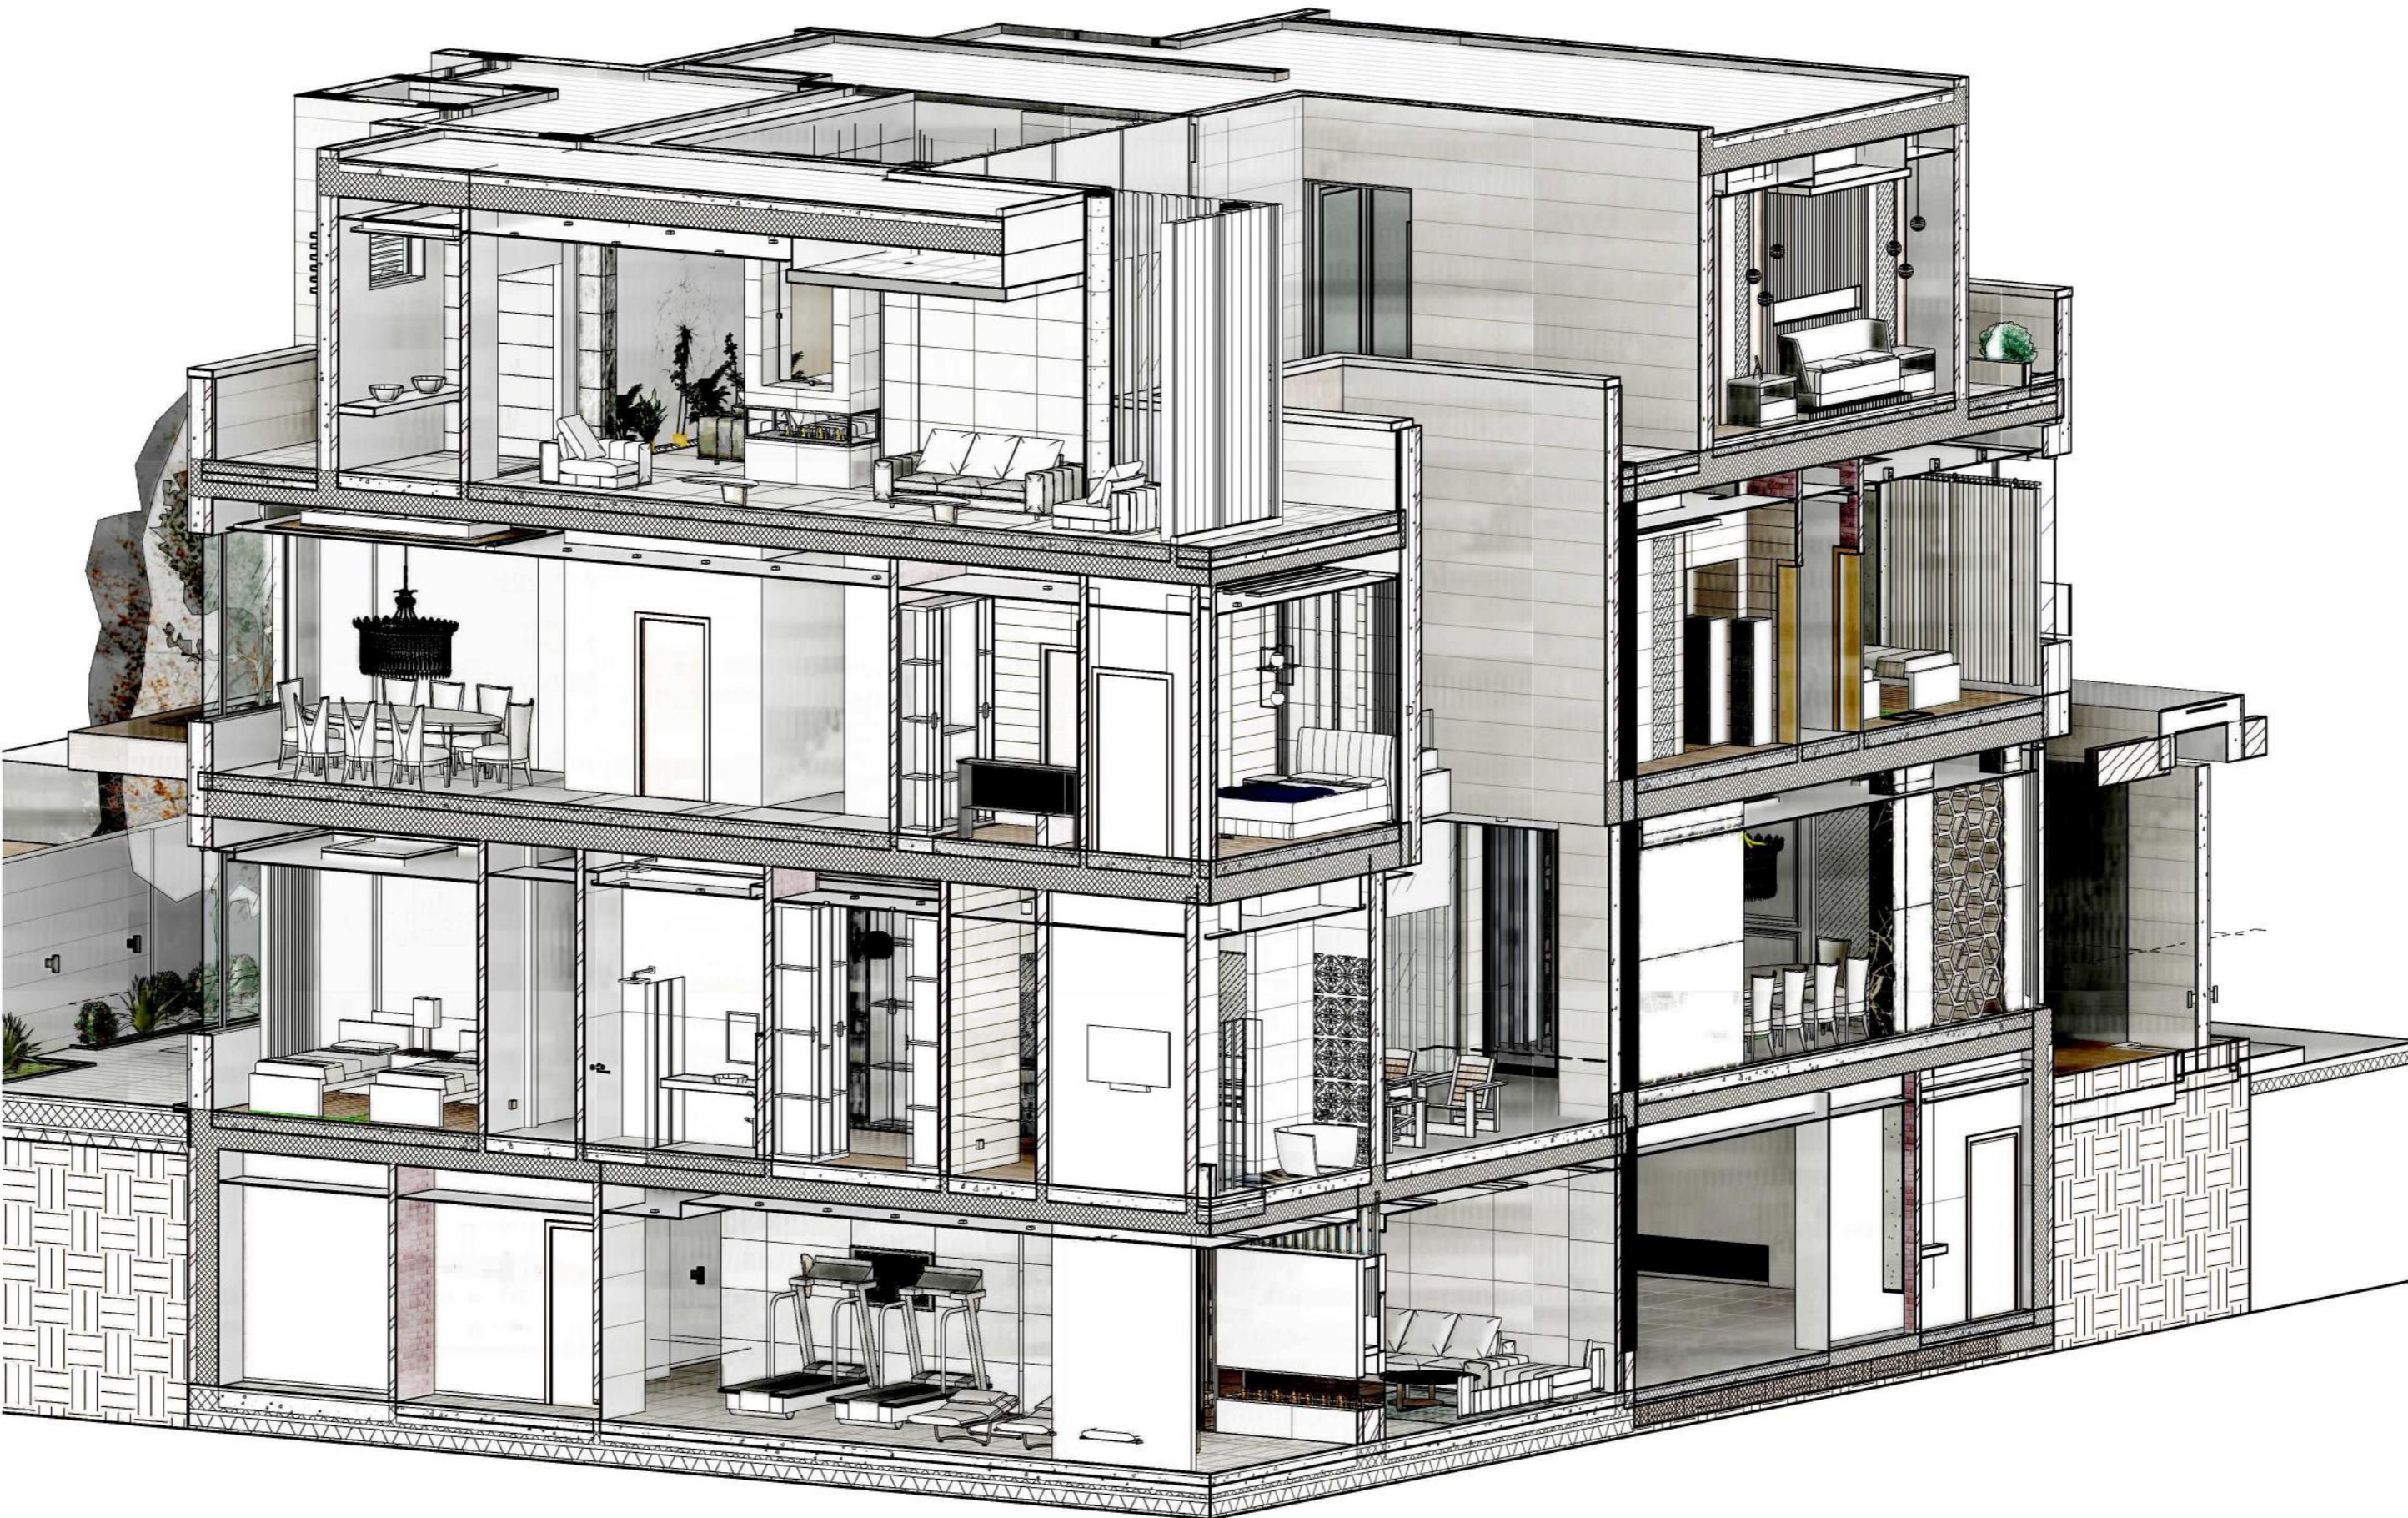


THE SHADOWS RESIDENCE

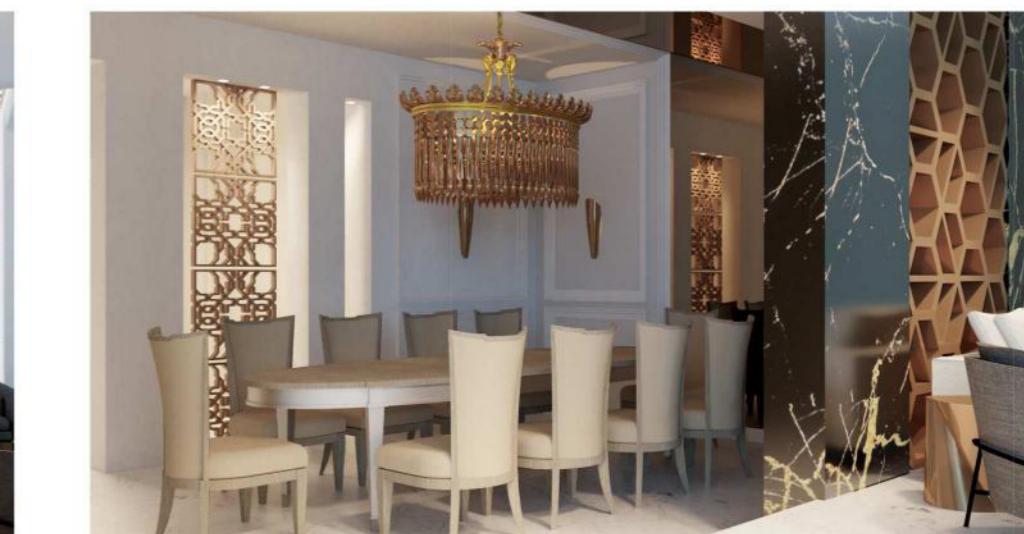

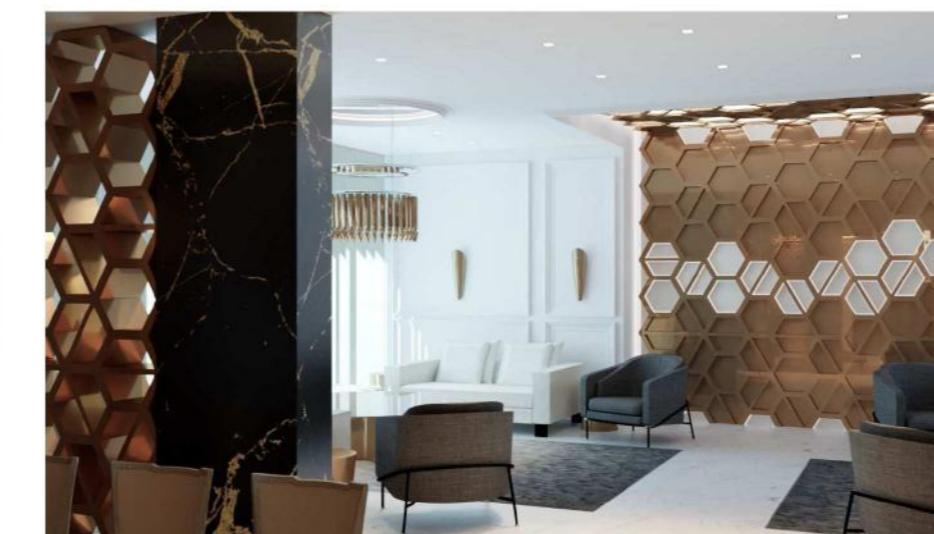

AL-BOUCA'I
ENGINEERING CONSULTING BUREAU
مكتب البقاعي
للاستشارات الهندسية

BIM
lab
Engineering Services

ID PACKAGE -LIST OF DRWAINGS	
Sheet Name	Sheet Number
COVER PAGE	ID-0000
LIST OF DRAWINGS	ID-0001
BASEMENT FLOOR-OVERALL TILING PLAN	ID-1010
GROUND FLOOR-OVERALL TILING PLAN	ID-1020
FIRST FLOOR-OVERALL TILING PLAN	ID-1030
ROOF FLOOR-OVERALL TILING PLAN	ID-1040
BASEMENT FLOOR -OVERALL FURNISHED PLAN	ID-1110
GROUND FLOOR -OVERALL FURNISHED PLAN	ID-1120
FIRST FLOOR -OVERALL FURNISHED PLAN	ID-1130
ROOF FLOOR -OVERALL FURNISHED PLAN	ID-1140
BASEMENT FLOOR-OVERALL FINISHES PLAN	ID-1210
GROUND FLOOR-OVERALL FINISHES PLAN	ID-1220
FIRST FLOOR-OVERALL FINISHES PLAN	ID-1230
ROOF FLOOR-OVERALL FINISHES PLAN	ID-1240
BASEMENT FLOOR-OVERALL CEILING PLAN	ID-1310
GROUND FLOOR-OVERALL CEILING PLAN	ID-1320
GROUND FLOOR-OVERALL CEILING PLAN-PART01	ID-1321
GROUND FLOOR-OVRALL CEILING PLAN-PART 02	ID-1322
FIRST FLOOR-OVERALL CEILING PLAN	ID-1330
FIRST FLOOR-OVERALL CEILING PLAN-PART01	ID-1331
FIRST FLOOR-OVERALL CEILING PLAN-PART02	ID-1332
ROOF FLOOR-OVERALL CEILING PLAN	ID-1340
LIVING ROOM- SHOTS	ID-4000
BASEMENT FLOOR-LIVING ROOM	ID-4001
BASEMENT FLOOR-LIVING ROOM	ID-4002
BASEMENT FLOOR-LIVING ROOM	ID-4003
BASEMENT FLOOR-LIVING ROOM	ID-4004
SWIMMING POOL -SHOT	ID-4010
BASEMENT FLOOR-SWIMING POOL	ID-4011
BASEMENT FLOOR-SWIMING POOL	ID-4012
BASEMENT FLOOR- GUEST BATHROOM 1	ID-4020
BASEMENT FLOOR- GUESTS BATHROOM 2	ID-4030
BASEMENT FLOOR- GUESTS BATHROOM 2 ELEVATIONS	ID-4031
BASEMENT FLOOR- TOILET	ID-4040
SALON & DINING-SHOTS	ID-4100
GROUND FLOOR- SALON & DINING ROOM	ID-4101
GROUND FLOOR- SALON & DINING ROOM	ID-4102
GROUND FLOOR- SALON & DINING ROOM	ID-4103
GROUND FLOOR- SALON & DINING ROOM	ID-4104
GROUND FLOOR- SALON & DINING ROOM	ID-4105
LIVING ROOM-SHOT	ID-4110
GROUND FLOOR- LIVING ROOM	ID-4111
GROUND FLOOR- LIVING ROOM	ID-4112

ID PACKAGE -LIST OF DRWAINGS	
Sheet Name	Sheet Number
MASTER BEDROOM &BATHROOM-SHOTS	ID-4120
MASTER BEDROOM &BATHROOM-SHOTS	ID-4121
GROUND FLOOR- MASTER BEDROOM &BATHROOM	ID-4122
GROUND FLOOR- MASTER BEDROOM &BATHROOM	ID-4123
GROUND FLOOR- MASTER BEDROOM &BATHROOM	ID-4124
GROUND FLOOR- MASTER BEDROOM &BATHROOM	ID-4125
GROUND FLOOR - MASTER BEDROOM 2 & BATHROOM-SHOTS	ID-4130
GROUND FLOOR - MASTER BEDROOM 2 & BATHROOM	ID-4131
GROUND FLOOR - MASTER BEDROOM 2 & BATHROOM	ID-4132
GROUND FLOOR - MASTER BEDROOM 2 & BATHROOM ELEVATIONS	ID-4133
GROUND FLOOR - MASTER BEDROOM 2 & BATHROOM ELEVATIONS	ID-4134
GROUND FLOOR-BATHROOM 03	ID-4140
GROUND FLOOR - GUEST BATHROOM	ID-4150
LIVING ROOM-SHOT	ID-4200
FIRST FLOOR - LIVING ROOM	ID-4201
FIRST FLOOR- LIVING ROOM	ID-4202
FIRST FLOOR BATHROOM 1	ID-4210
FIRST FLOOR BATHROOM 2	ID-4220
FIRST FLOOR TOILET 1	ID-4230
FIRST FLOOR TOILET 2	ID-4240
MASTER BEDROOM-SHOT	ID-4250
FIRST FLOOR- MASTER BEDROOM & BATHROOM 01	ID-4251
FIRST FLOOR- MASTER BEDROOM & BATHROOM 01	ID-4252
FIRST FLOOR- MASTER BEDROOM & BATHROOM 01	ID-4253
LIVING ROOM & SALON-SHOT	ID-4300
ROOF FLOOR -LIVING ROOM AND SALON	ID-4301
ROOF FLOOR -LIVING ROOM &SALON CEILING PLAN	ID-4302
ROOF FLOOR LIVING ROOM AND SALOON	ID-4303
ROOF FLOOR LIVING ROOM AND SALOON	ID-4304
MASTER BEDROOM -SHOT	ID-4310
ROOF FLOOR MASTER BEDROOM PLAN	ID-4311
ROOF FLOOR MASTER BEDROOM RCP	ID-4312
ROOF FLOOR MASTER BEDROOM ELEVATIONS-PART 01	ID-4313
ROOF FLOOR MASTER BEDROOM ELEVATIONS-PART 02	ID-4314
ROOF FLOOR BATHROOM	ID-4320
ROOF FLOOR TOILET	ID-4330
ROOF FLOOR TOILET ELEVATIONS	ID-4331
WALL FINISHES	ID-6000
FLOOR FINISHES	ID-6001

PROJECT NAME	APARTMENTS BUILDING
NOTES	
Project Type	Residential
Owner	Khalid Khadir Hasan AL-Saeed
Location	Amman
Plot No.	1659
Basin No.	19
Designed by	A.Shaker Khulief 4809
SHEET NAME	LIST OF DRAWINGS
ID-0001	
Date	10/03/19
Scale	

PROJECT NAME

APARTMENTS BUILDING

NOTES


FOR FINISHES REFER TO SHEETS:
ID-6000
ID-6001

Project Type	Residential
Owner	Khalid Khadir Hasan AL-Saeed
Location	Amman
Plot No.	1659
Basin No.	19
Designed by	A.Shaker Khulief 4809

SHEET NAME
BASEMENT FLOOR-OVERALL TILING PLAN

ID-1010

Date	05/20/19
Scale	1 : 100

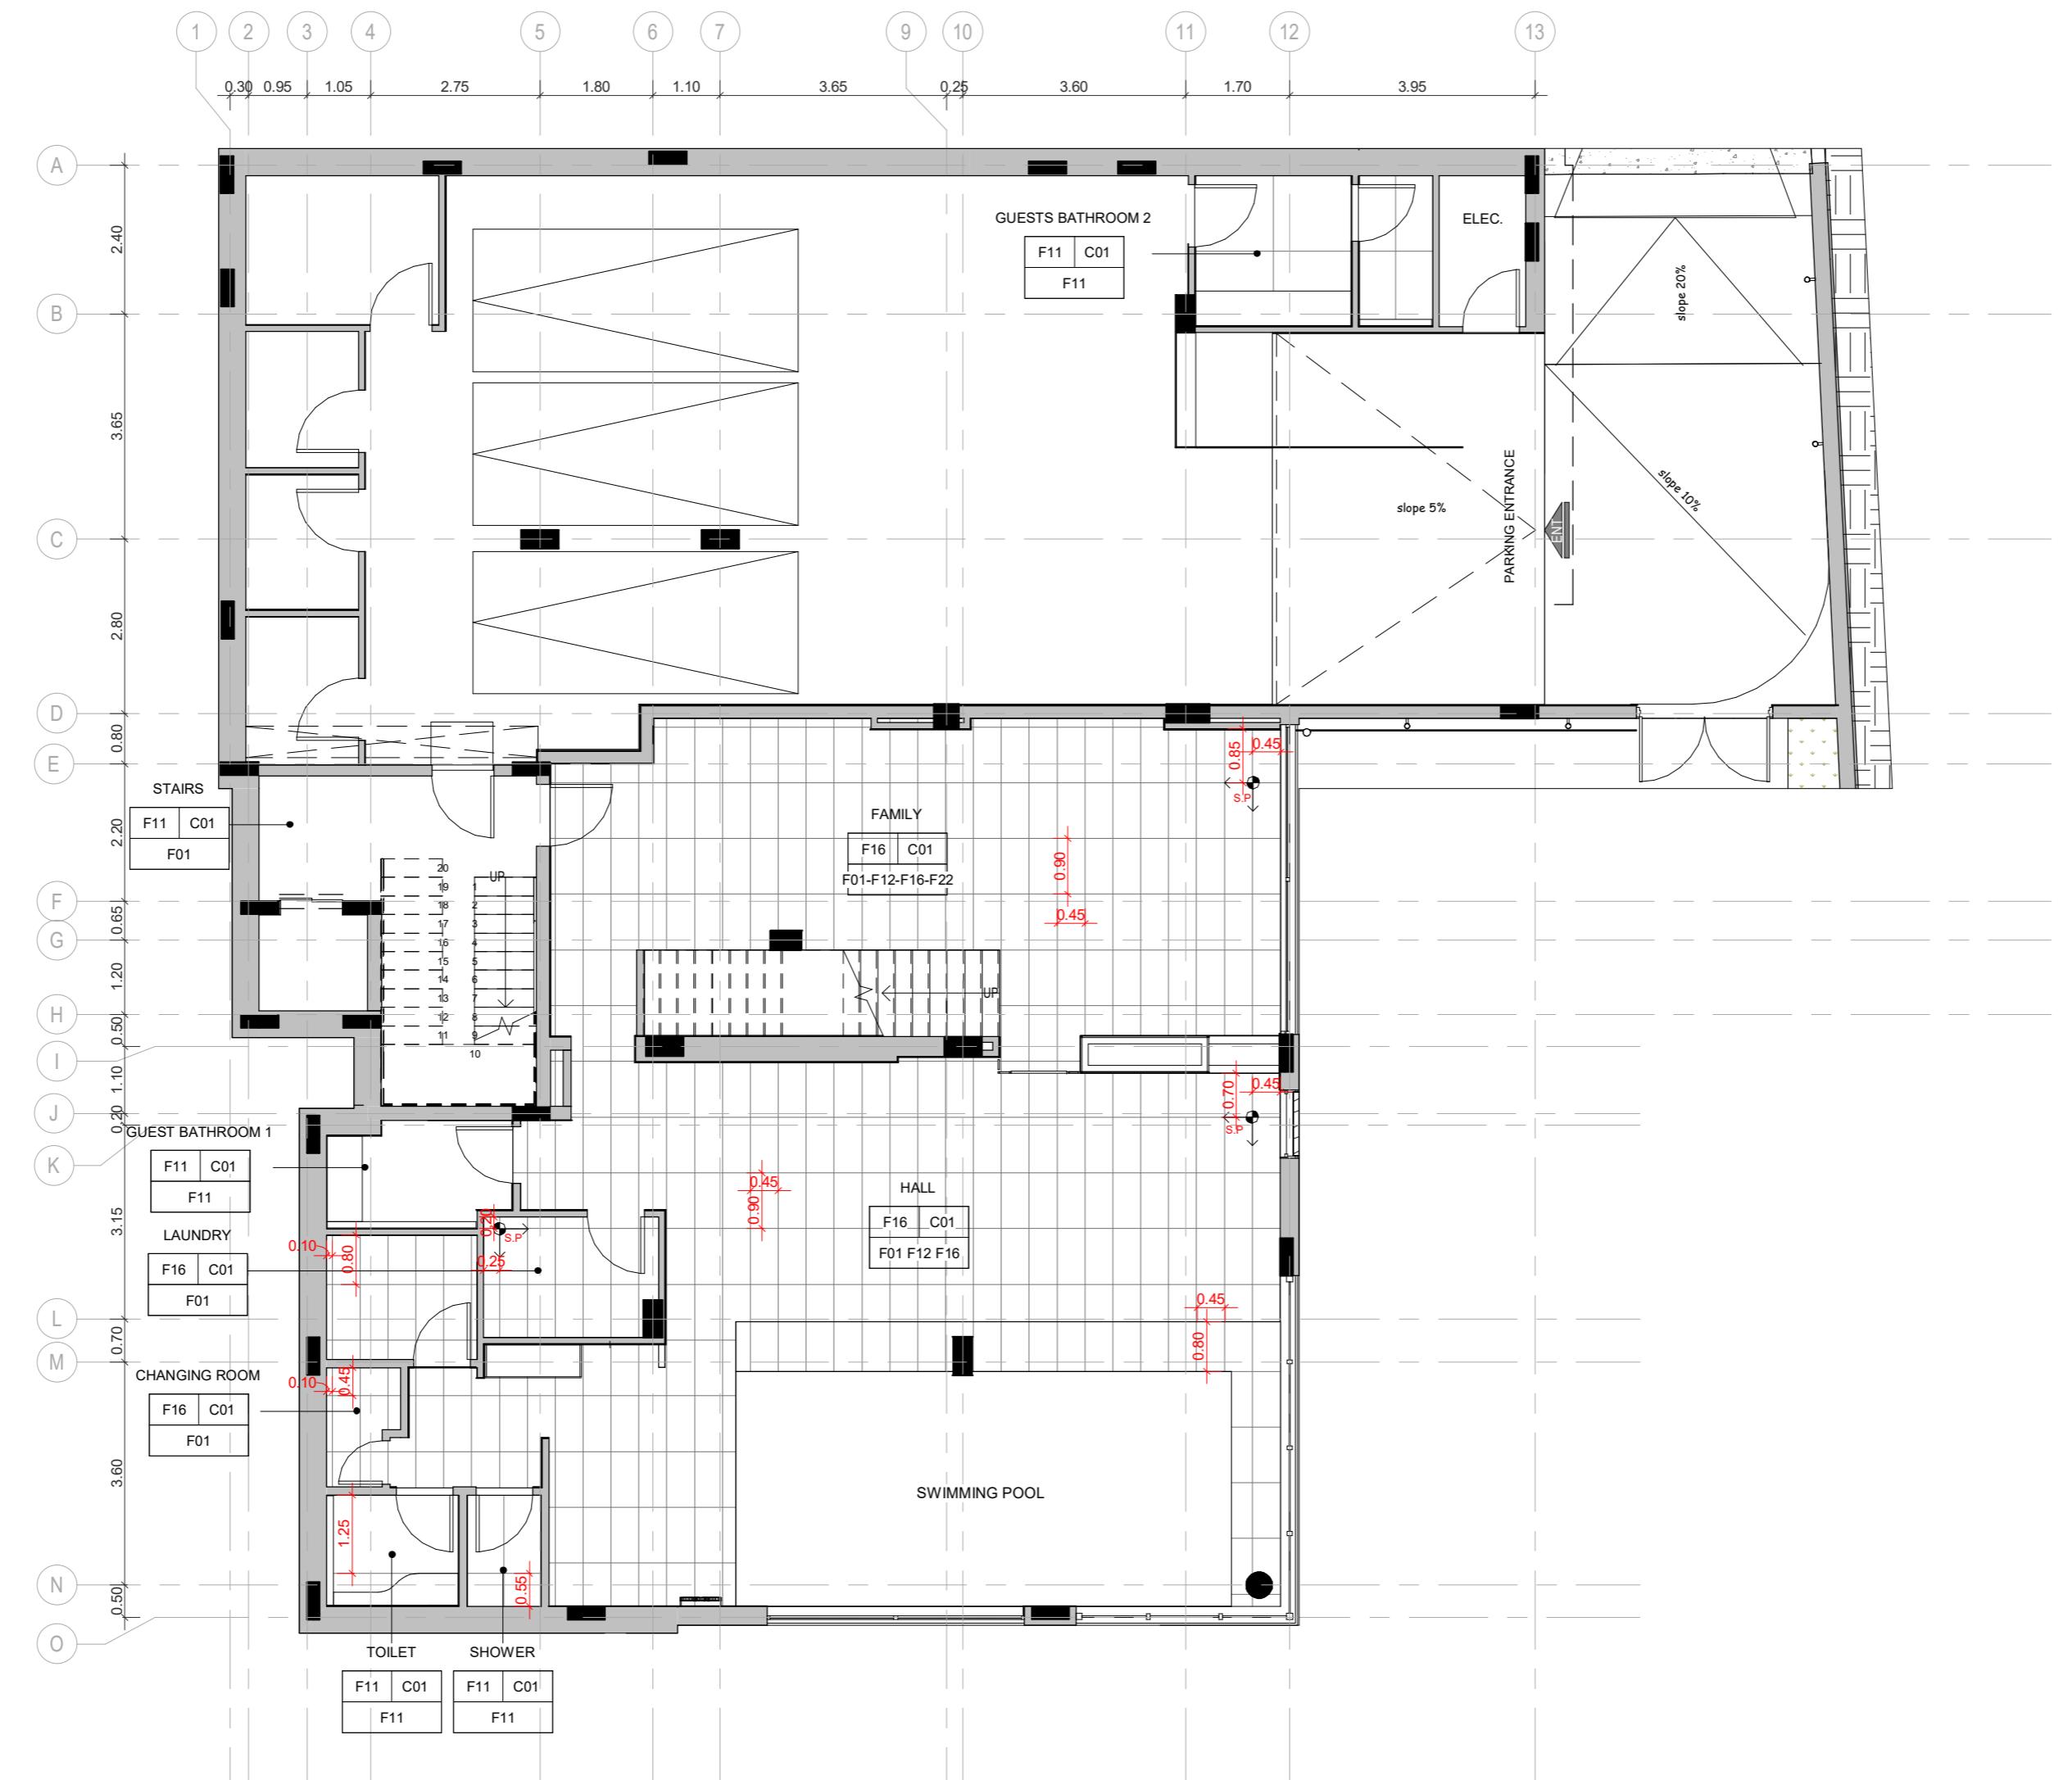

PROJECT NAME

APARTMENTS BUILDING

NOTES


FOR FINISHES REFER TO SHEETS:
ID-6000
ID-6001

Project Type	Residential
Owner	Khalid Khadir Hasan AL-Saeed
Location	Amman
Plot No.	1659
Basin No.	19
Designed by	A.Shaker Khulief 4809

SHEET NAME
**GROUND FLOOR-OVERALL
TILING PLAN**

ID-1020

Date	05/20/19
Scale	1 : 100

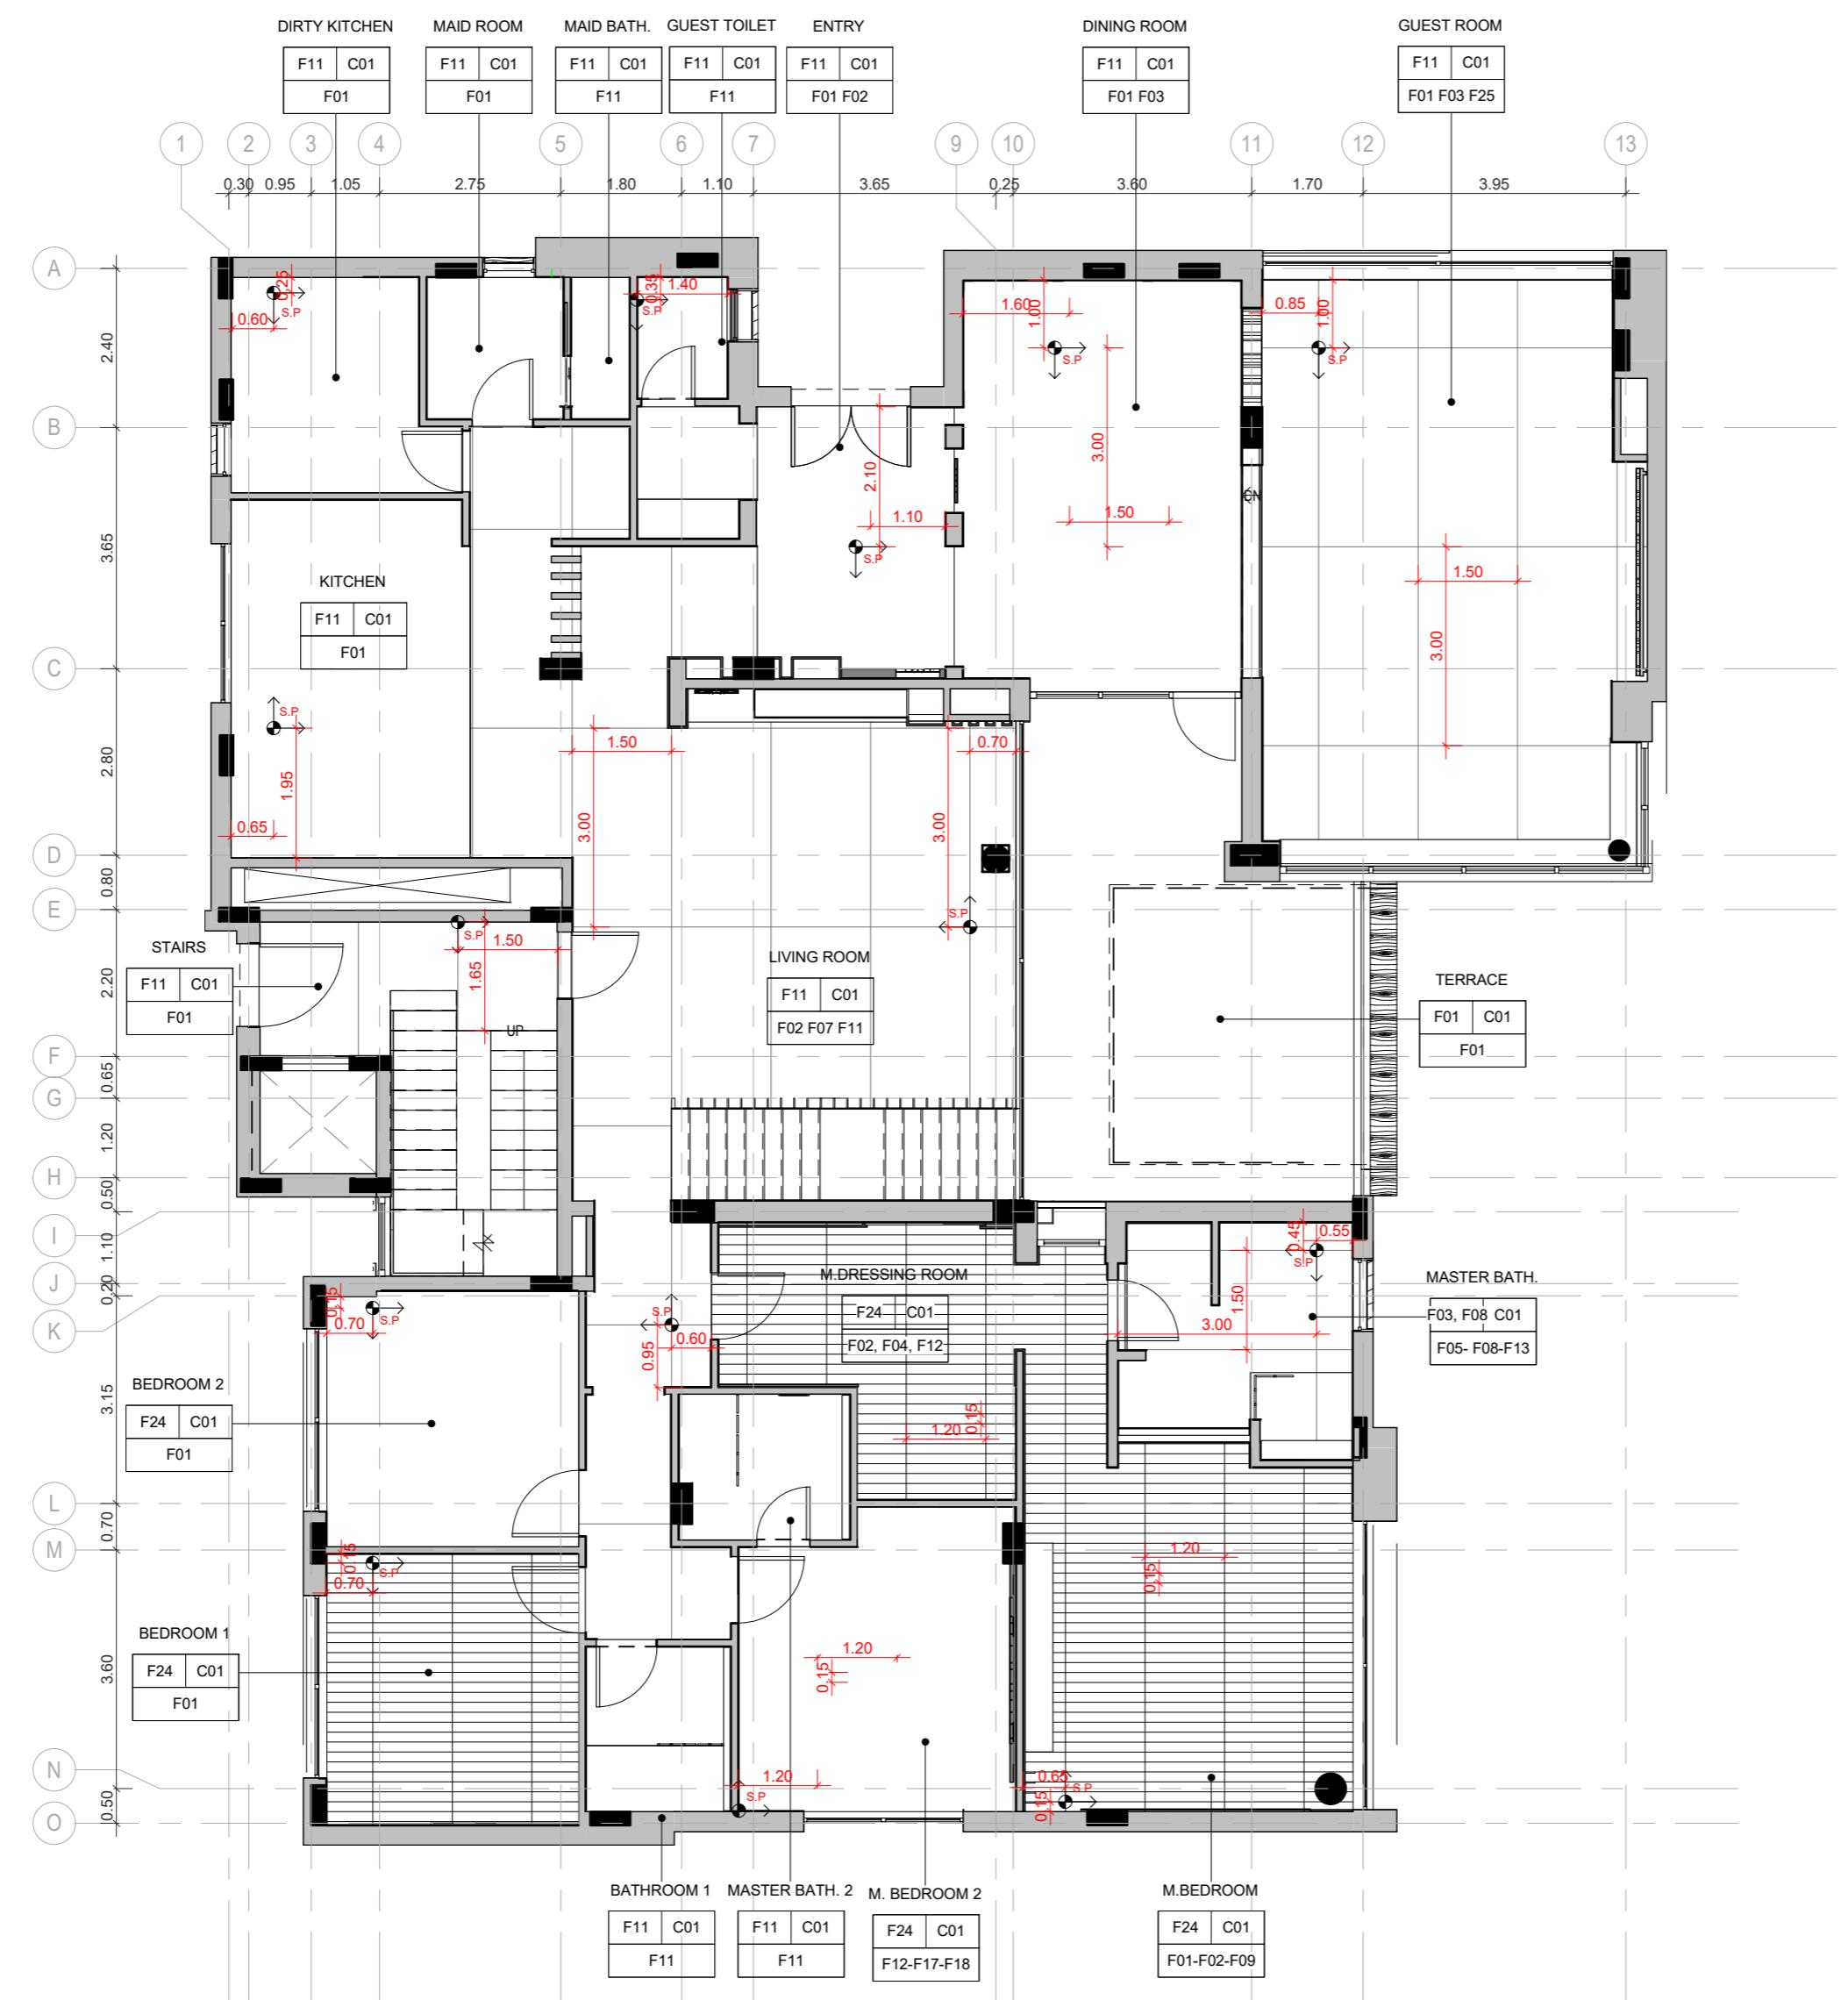

PROJECT NAME

APARTMENTS BUILDING

NOTES

FOR FINISHES REFER TO SHEETS:
ID-6000
ID-6001


Project Type	Residential
Owner	Khalid Khadir Hasan AL-Saeed
Location	Amman
Plot No.	1659
Basin No.	19
Designed by	A.Shaker Khulief 4809

SHEET NAME
FIRST FLOOR-OVERALL TILING PLAN

ID-1030

Date	05/20/19
Scale	1 : 100



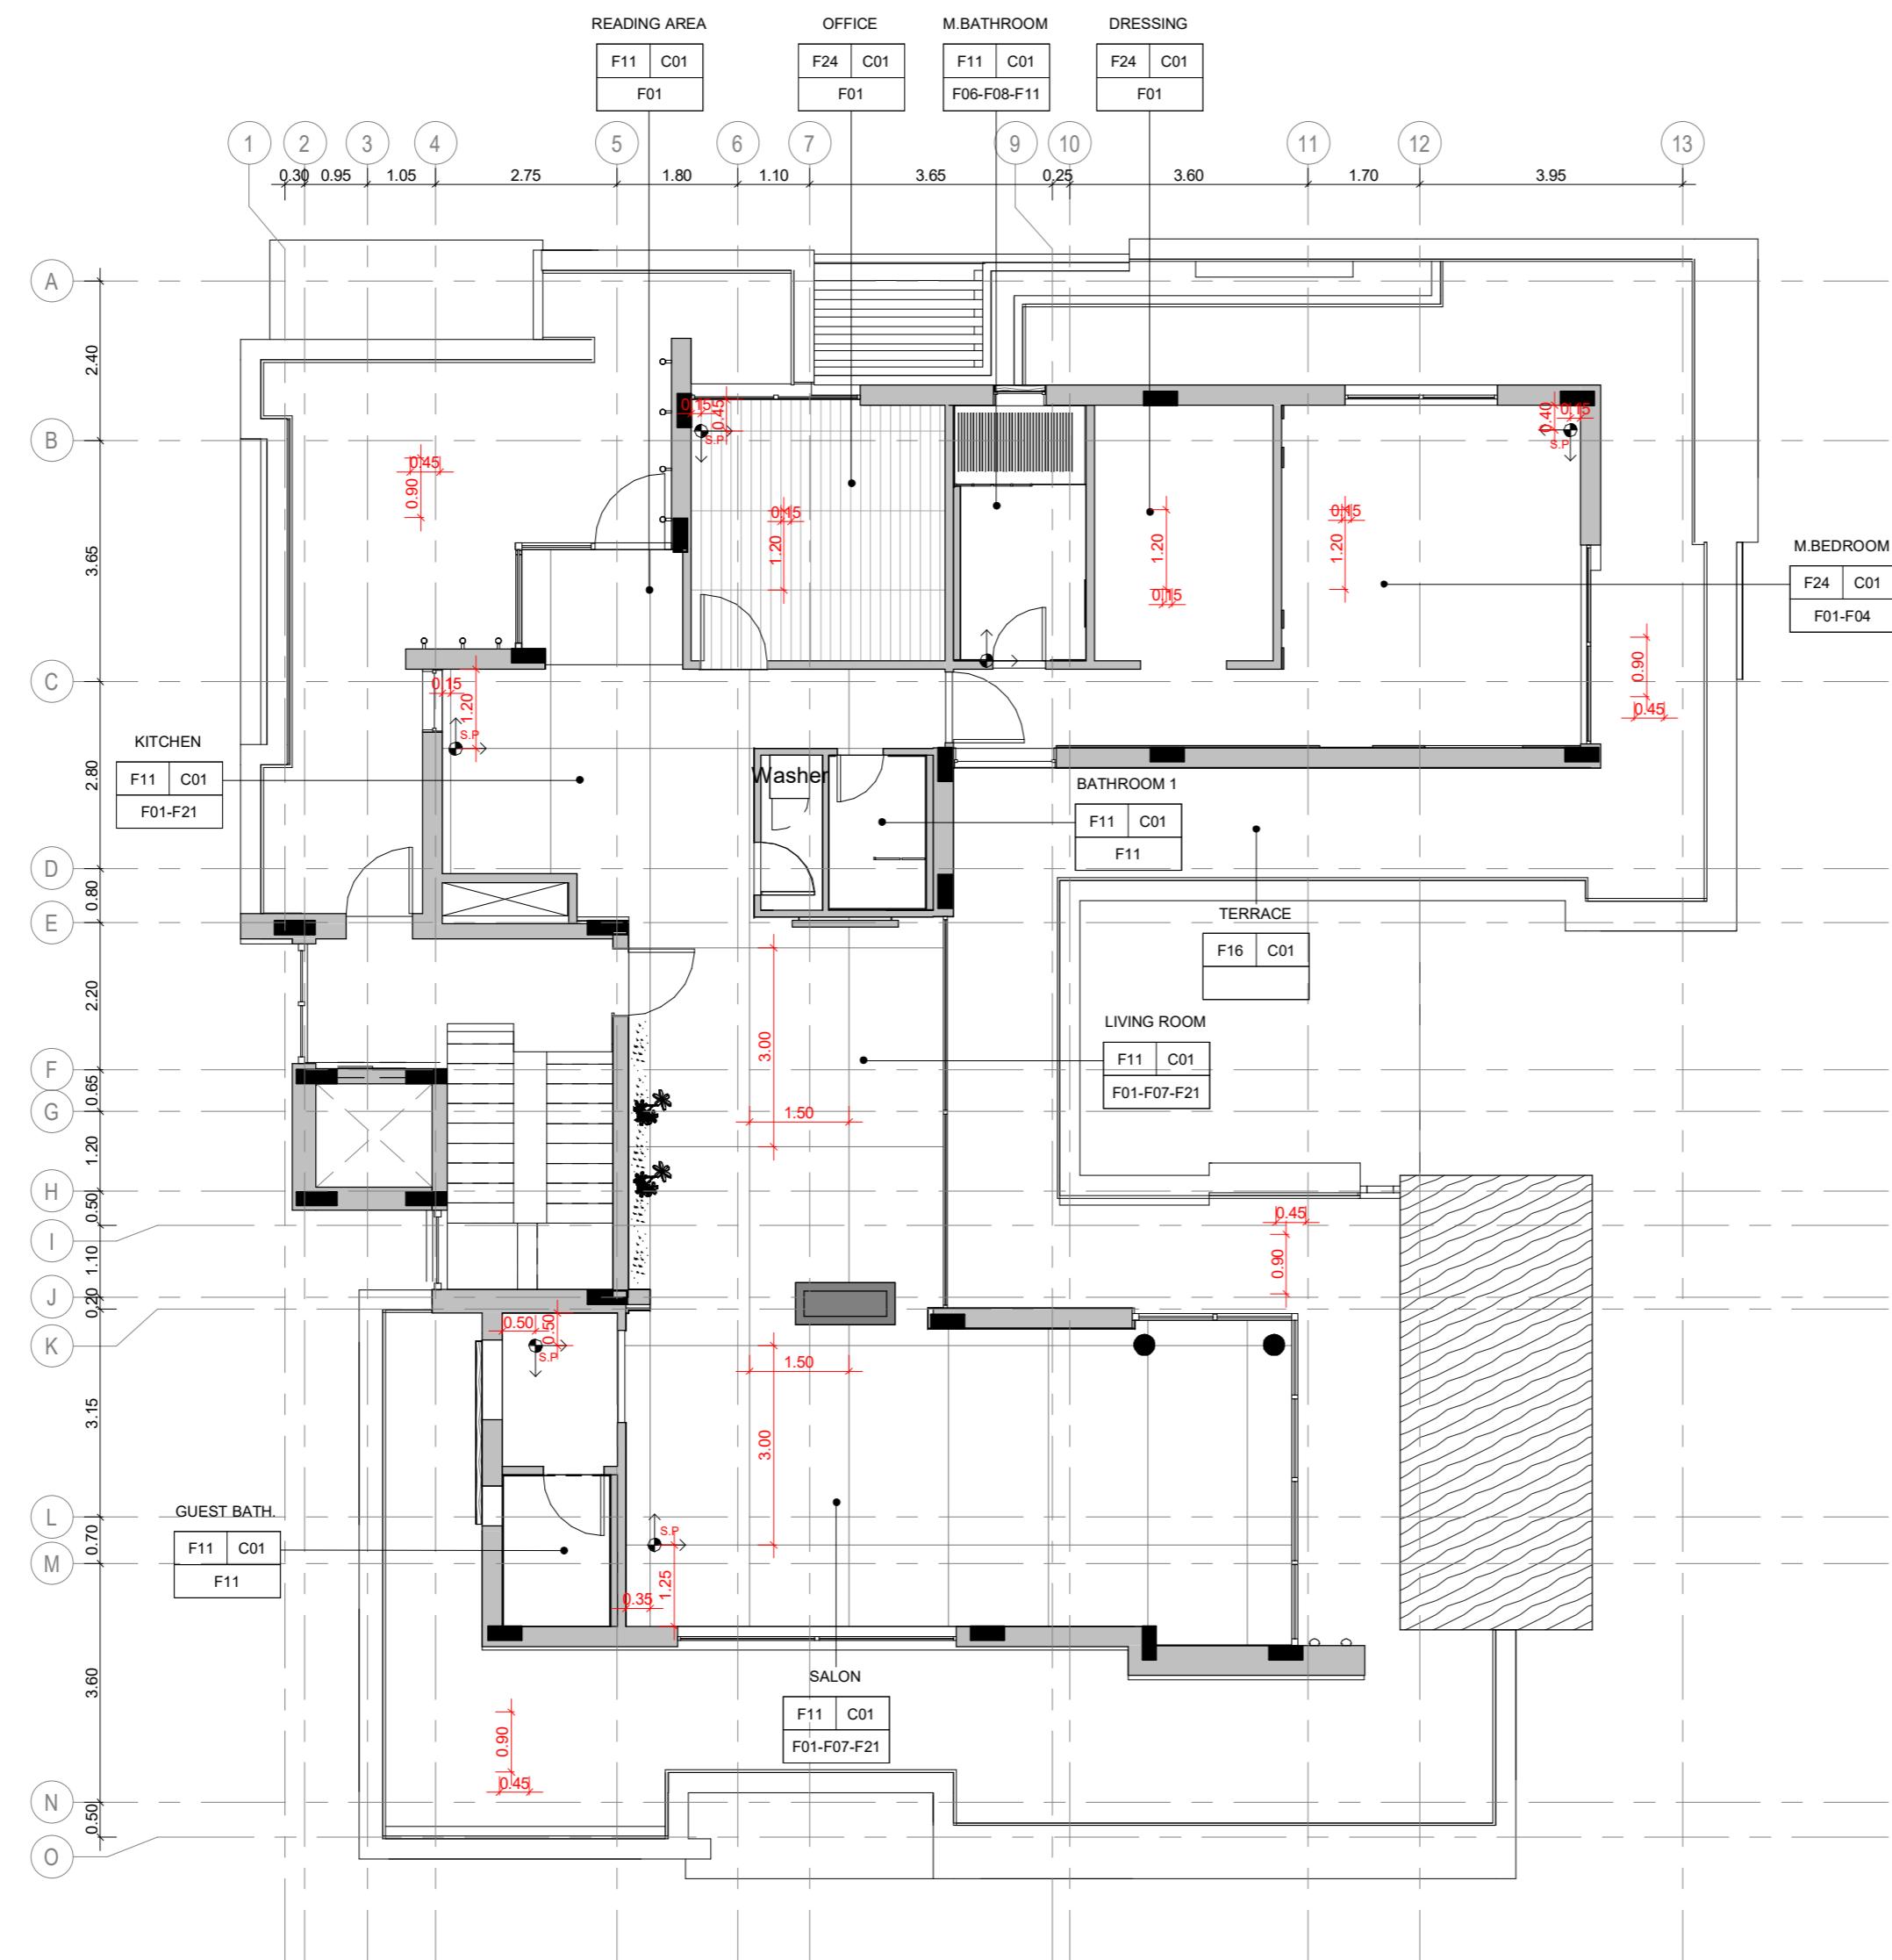

PROJECT NAME	APARTMENTS BUILDING
NOTES	FOR FINISHES REFER TO SHEETS: ID-6000 ID-6001
Project Type	Residential
Owner	Khalid Khadir Hasan AL-Saeed
Location	Amman
Plot No.	1659
Basin No.	19
Designed by	A.Shaker Khulief 4809
SHEET NAME	ROOF FLOOR-OVERALL TILING PLAN
ID-1040	
Date	05/20/19
Scale	1 : 100

PROJECT NAME

APARTMENTS BUILDING

NOTES


FOR FINISHES REFER TO SHEETS:
ID-6000
ID-6001

Project Type	Residential
Owner	Khalid Khadir Hasan AL-Saeed
Location	Amman
Plot No.	1659
Basin No.	19
Designed by	A.Shaker Khulief 4809

SHEET NAME
**BASEMENT FLOOR
-OVERALL FURNISHED PLAN**

ID-1110

Date	05/20/19
Scale	1 : 100

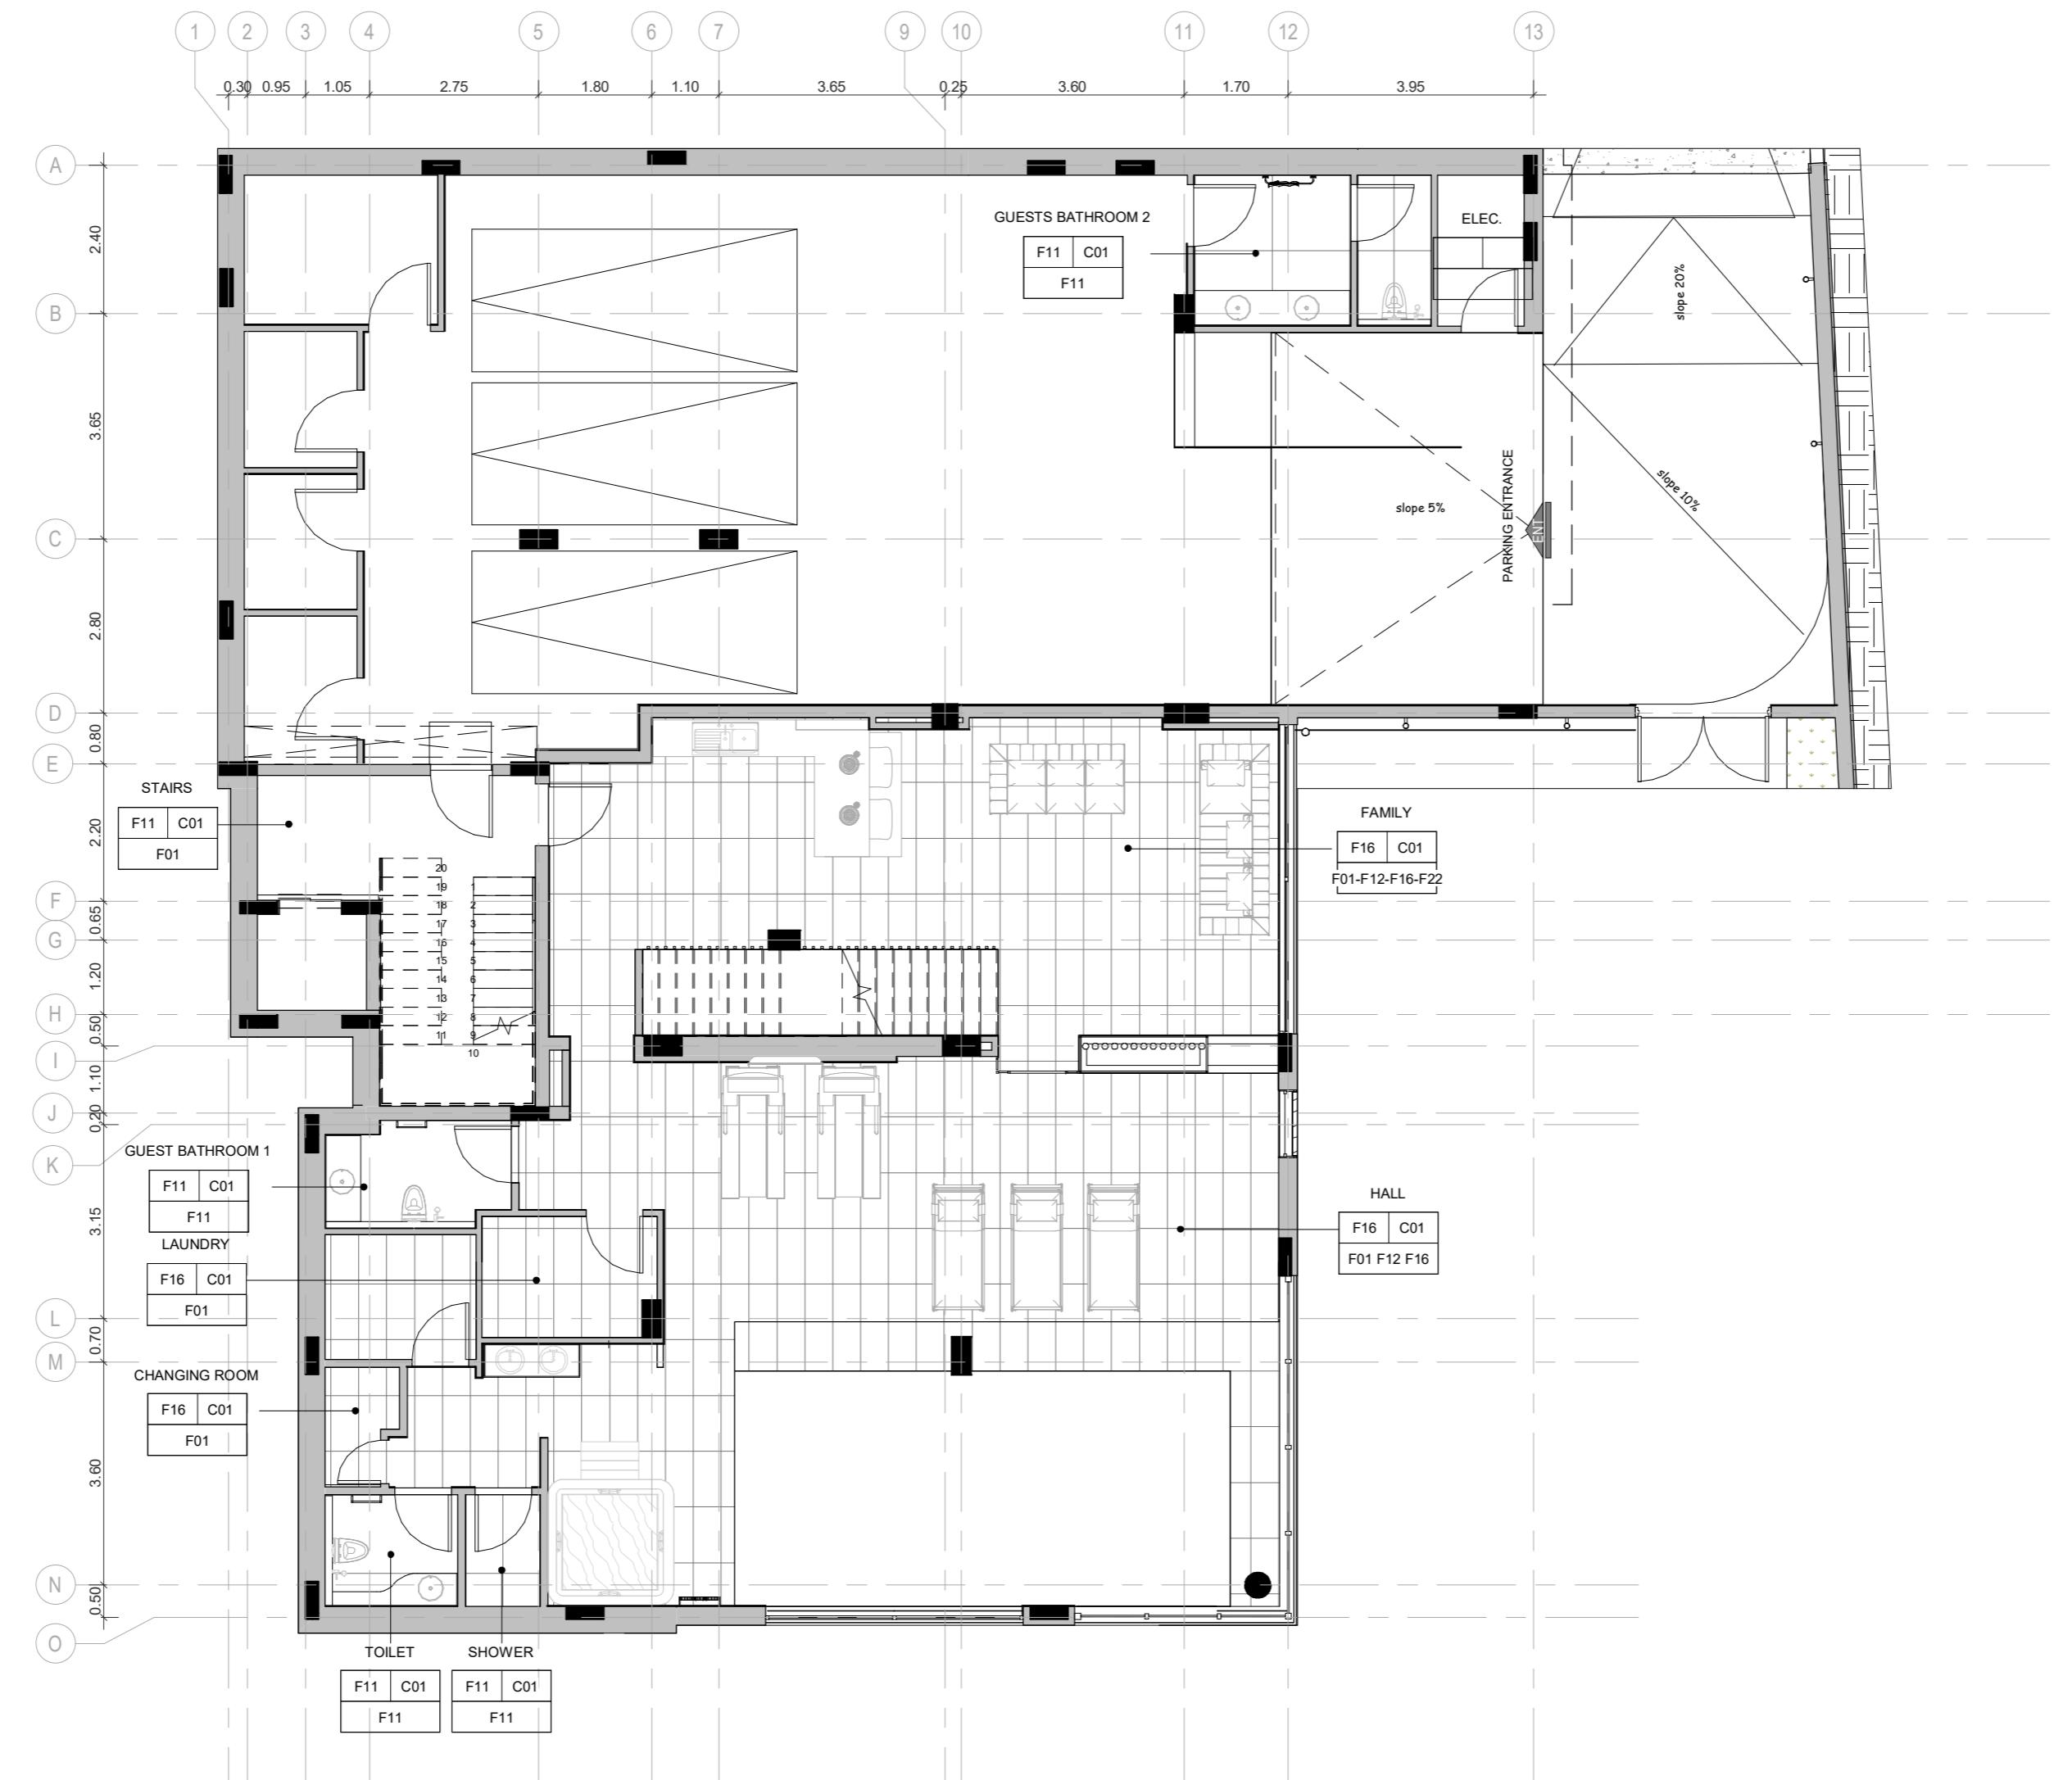

PROJECT NAME

APARTMENTS BUILDING

NOTES


FOR FINISHES REFER TO SHEETS:
ID-6000
ID-6001

Project Type	Residential
Owner	Khalid Khadir Hasan AL-Saeed
Location	Amman
Plot No.	1659
Basin No.	19
Designed by	A.Shaker Khulief 4809

SHEET NAME
GROUND FLOOR -OVERALL FURNISHED PLAN

ID-1120

Date	05/20/19
Scale	1 : 100

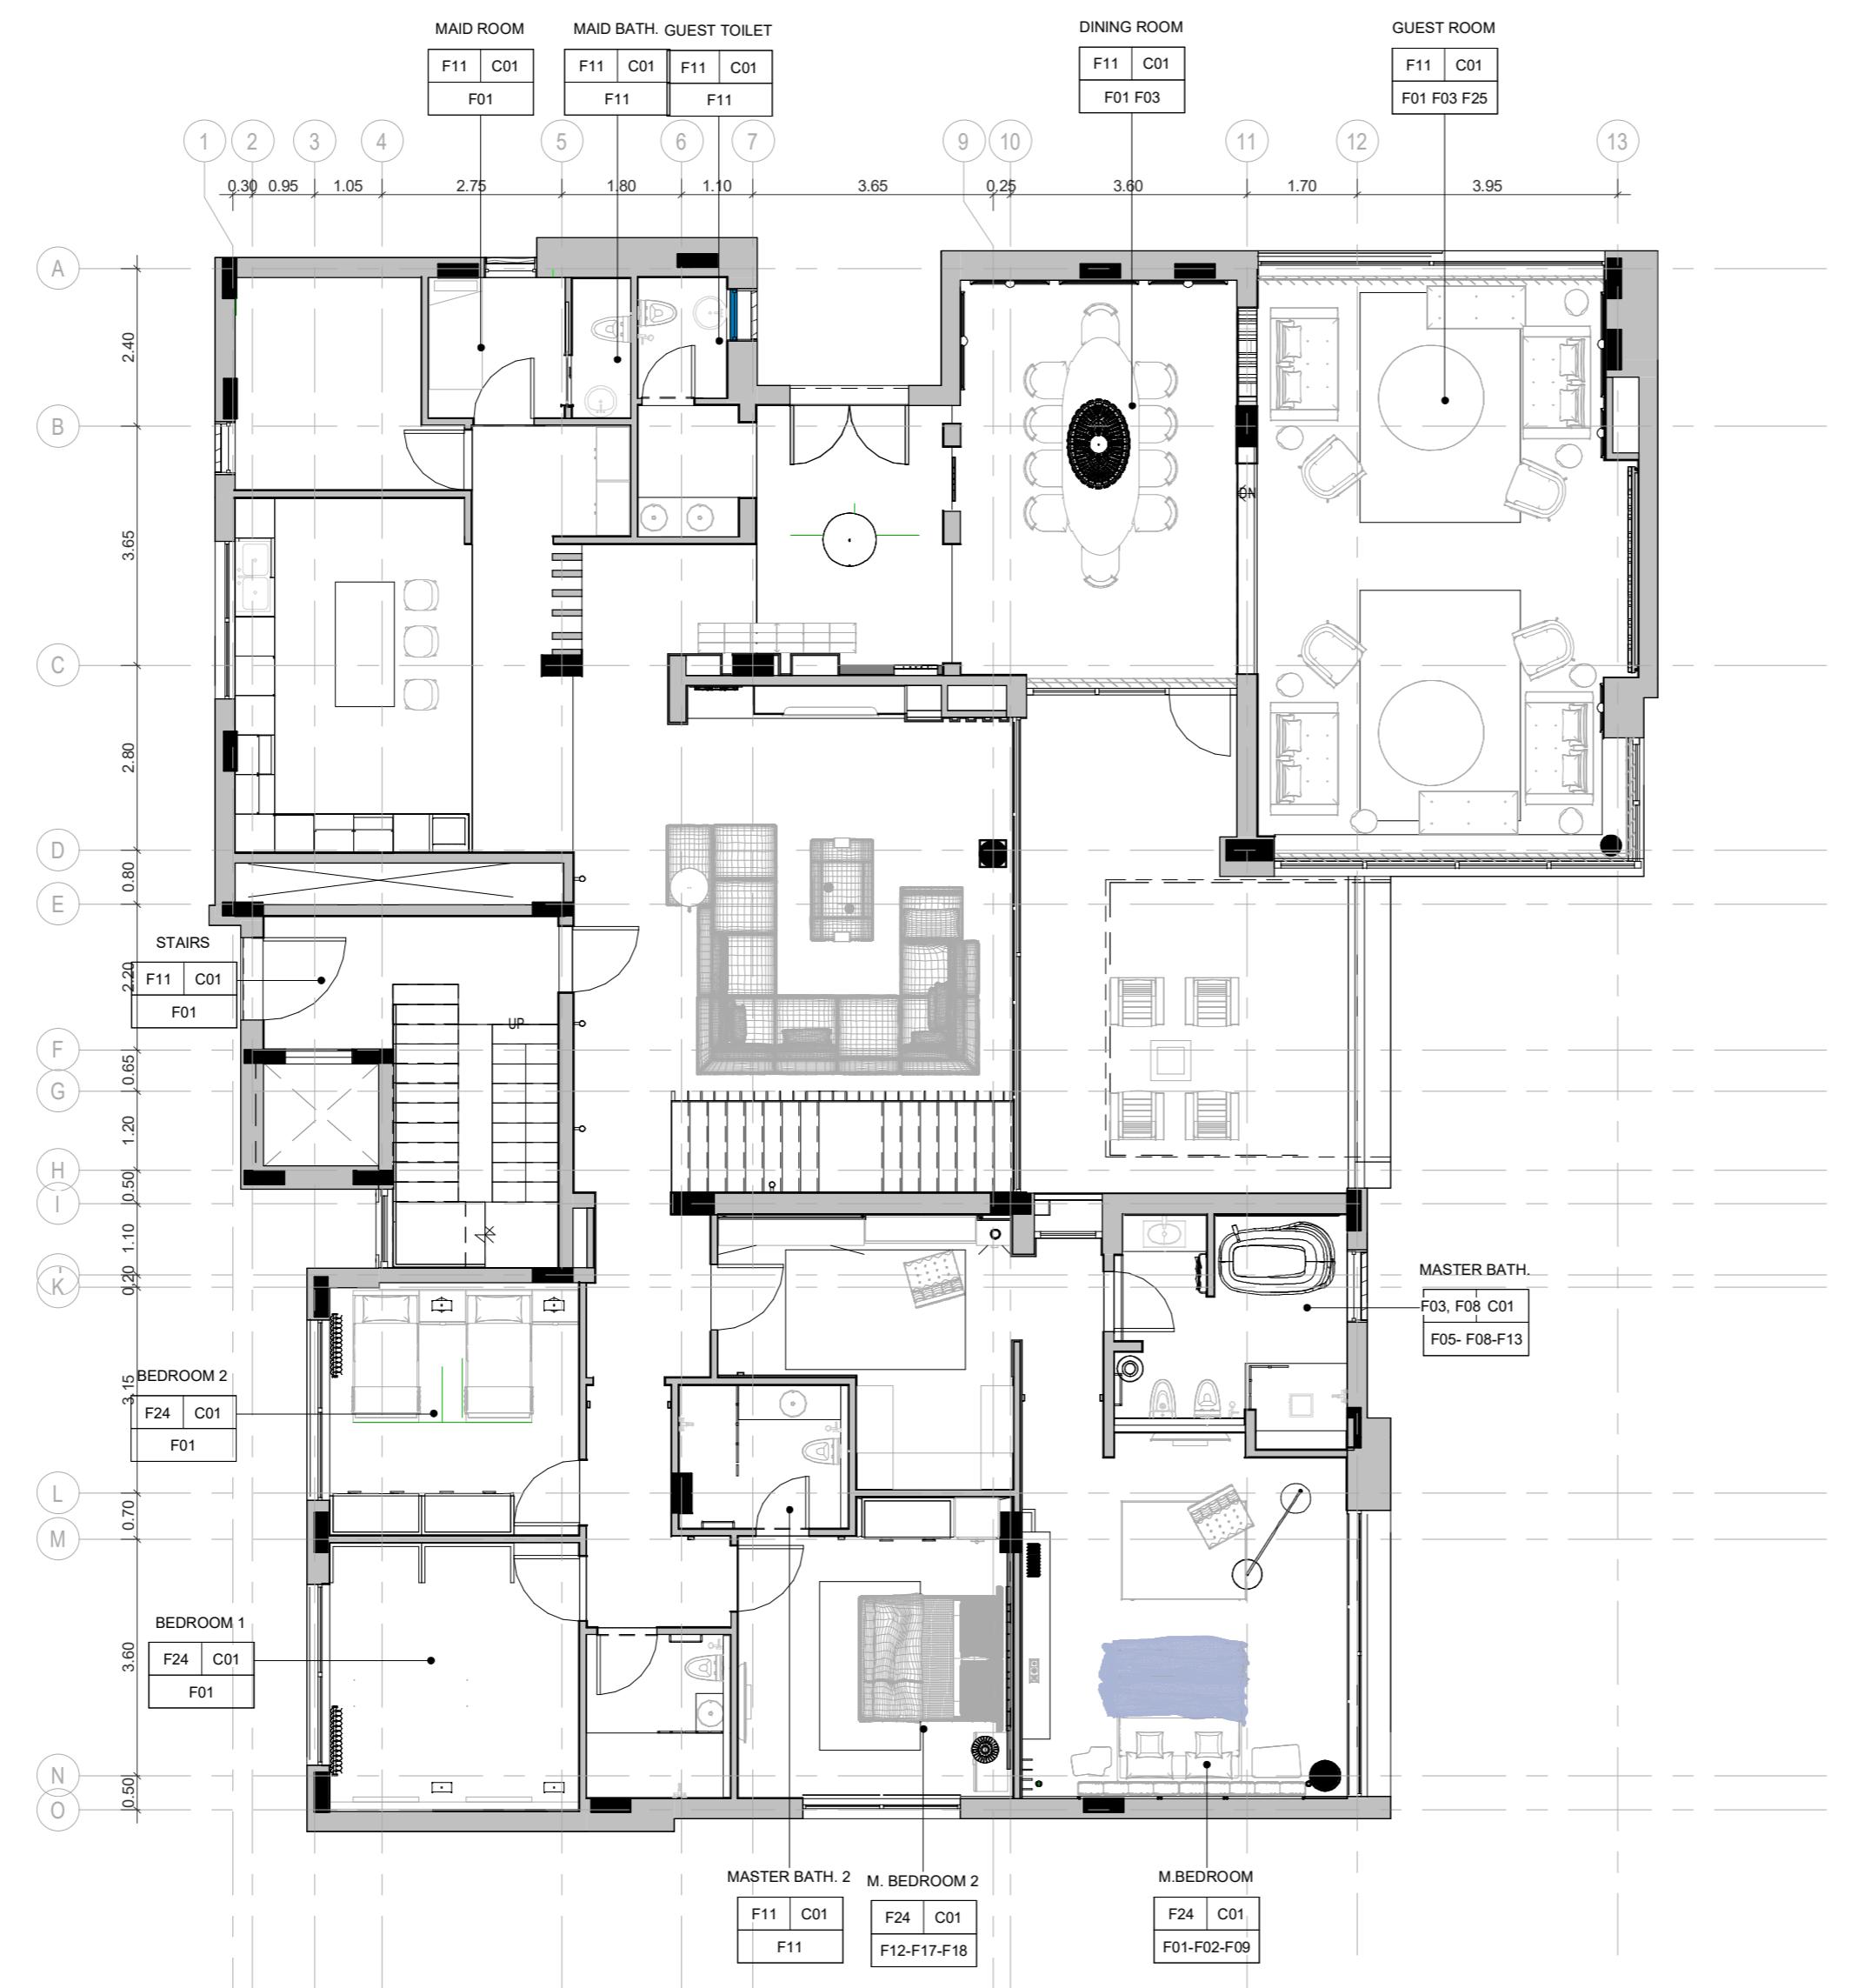

PROJECT NAME

APARTMENTS BUILDING

NOTES


FOR FINISHES REFER TO SHEETS:
ID-6000
ID-6001

Project Type	Residential
Owner	Khalid Khadir Hasan AL-Saeed
Location	Amman
Plot No.	1659
Basin No.	19
Designed by	A.Shaker Khulief 4809

SHEET NAME
FIRST FLOOR -OVERALL FURNISHED PLAN

ID-1130

Date	05/20/19
Scale	1 : 100

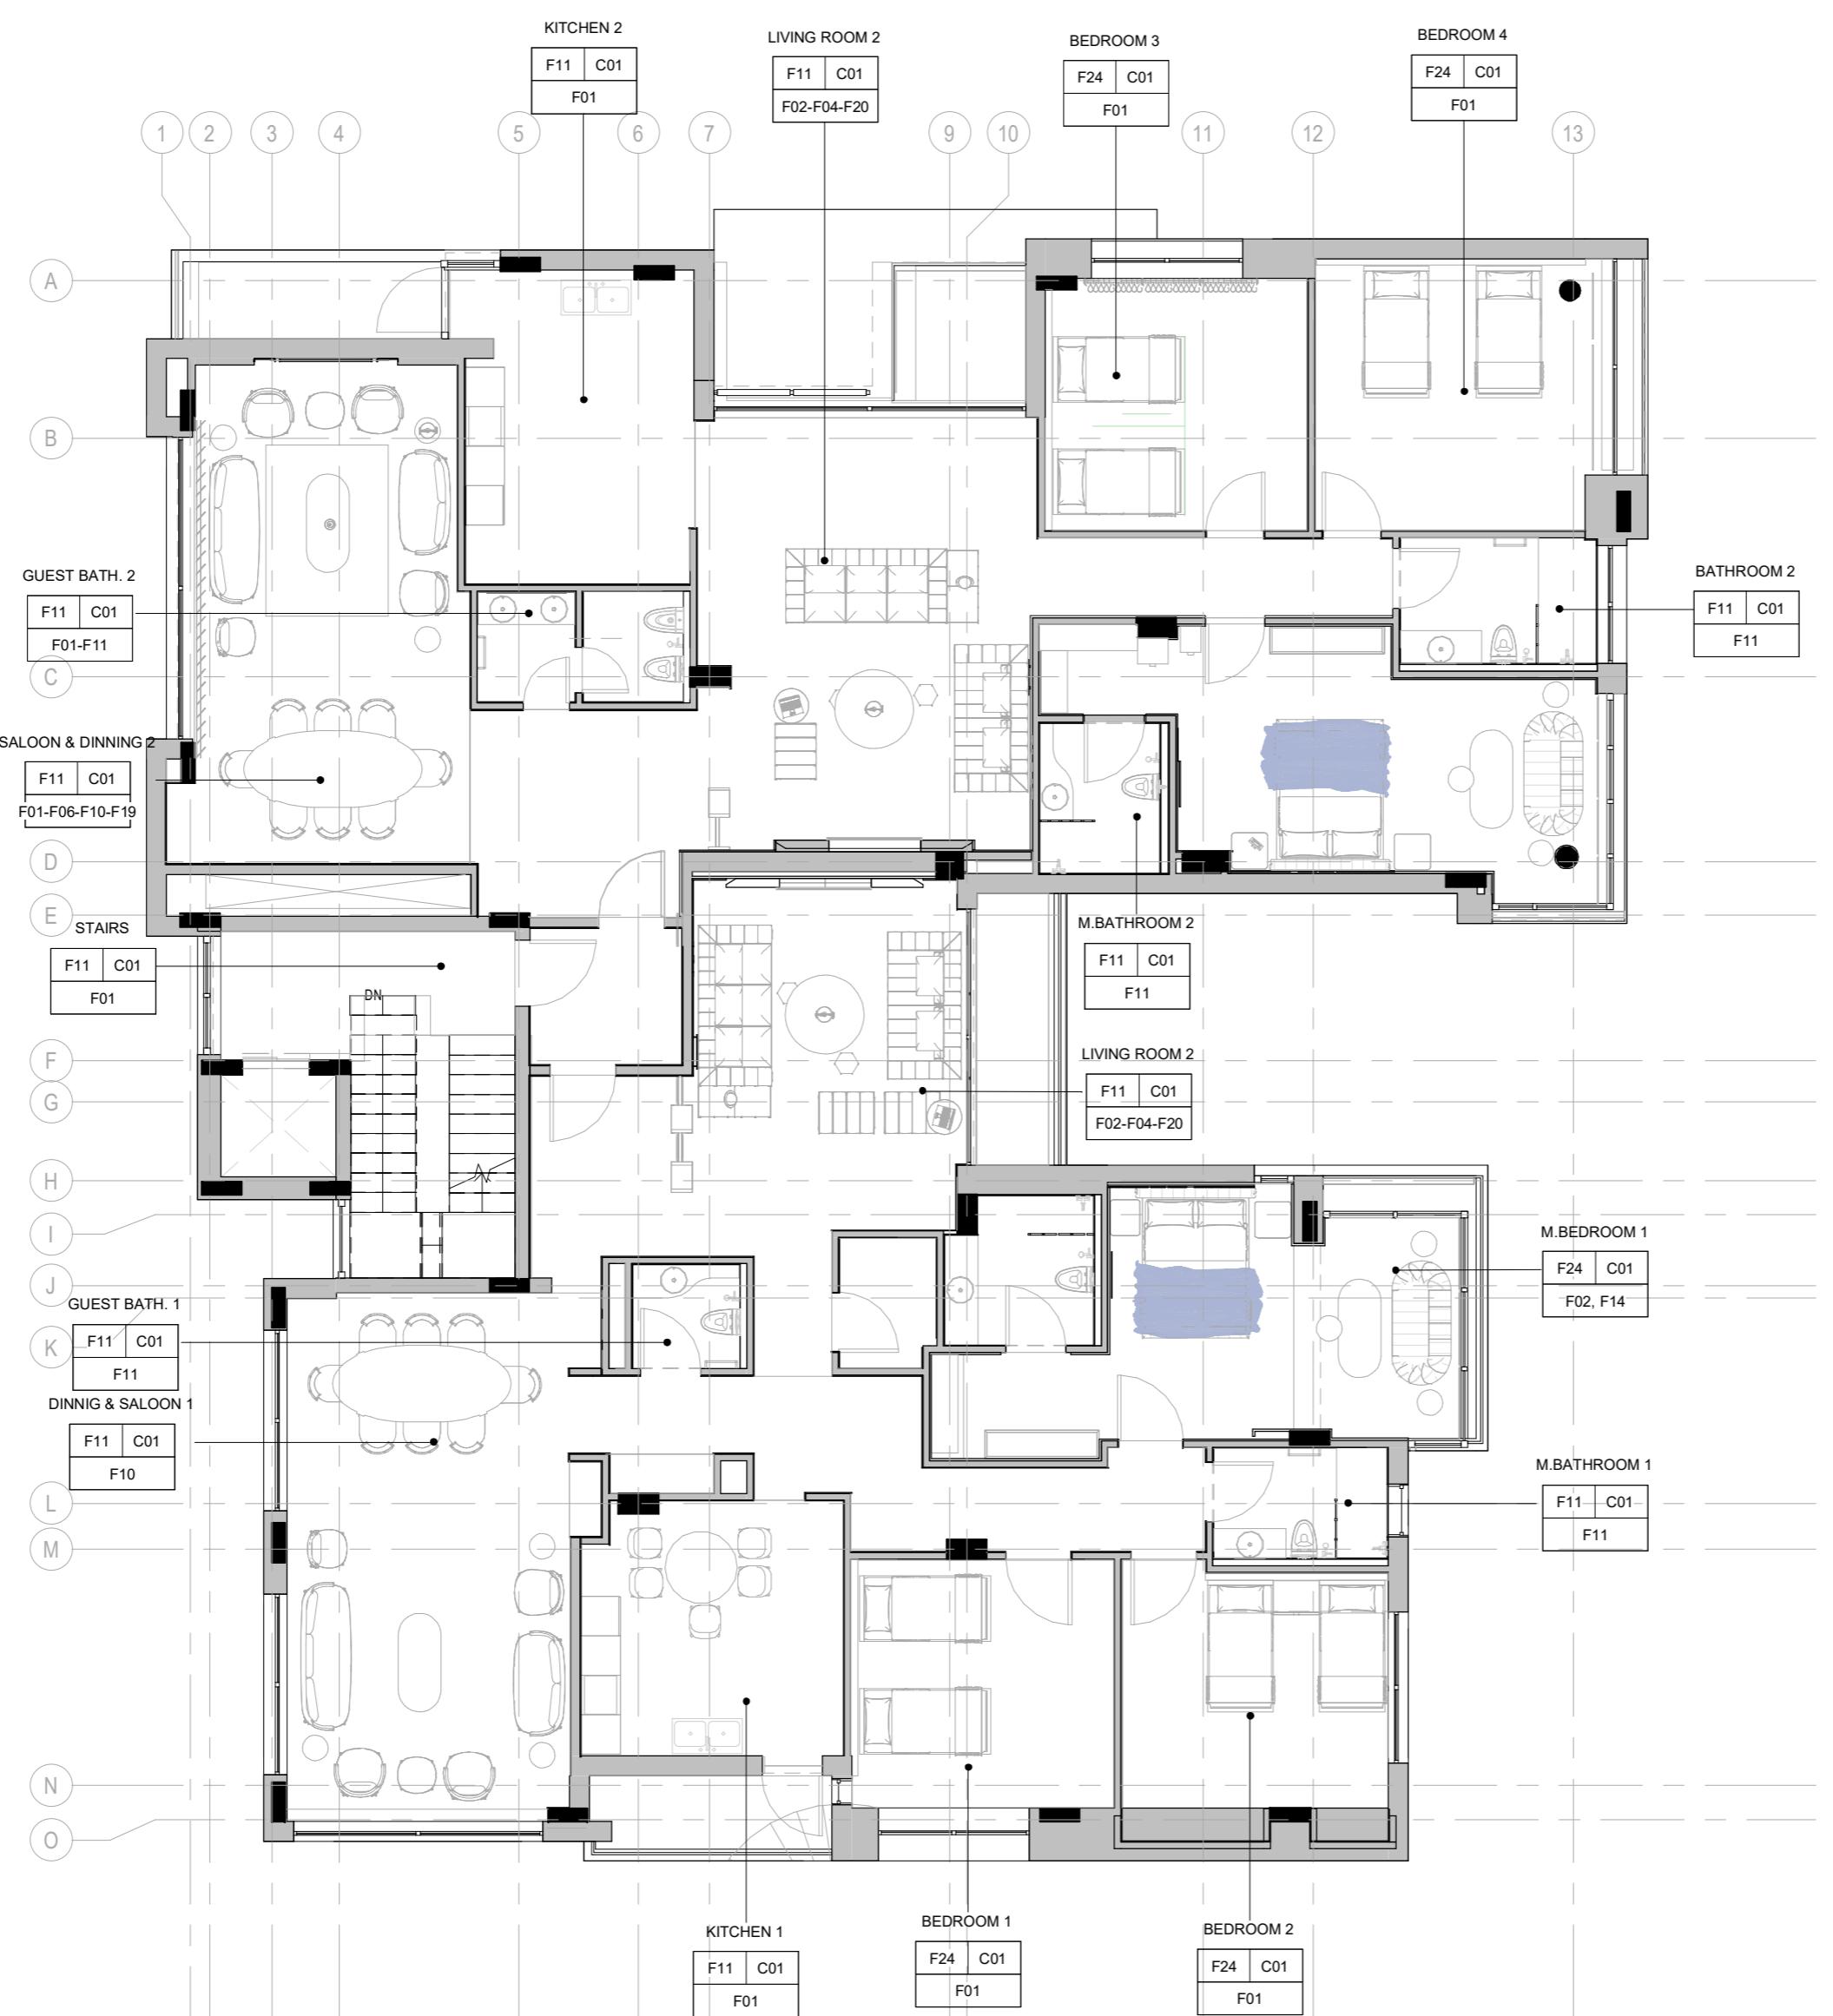

PROJECT NAME

APARTMENTS BUILDING

NOTES


FOR FINISHES REFER TO SHEETS:
ID-6000
ID-6001

Project Type	Residential
Owner	Khalid Khadir Hasan AL-Saeed
Location	Amman
Plot No.	1659
Basin No.	19
Designed by	A.Shaker Khulief 4809

SHEET NAME
ROOF FLOOR -OVERALL FURNISHED PLAN

ID-1140

Date	05/20/19
Scale	1 : 100

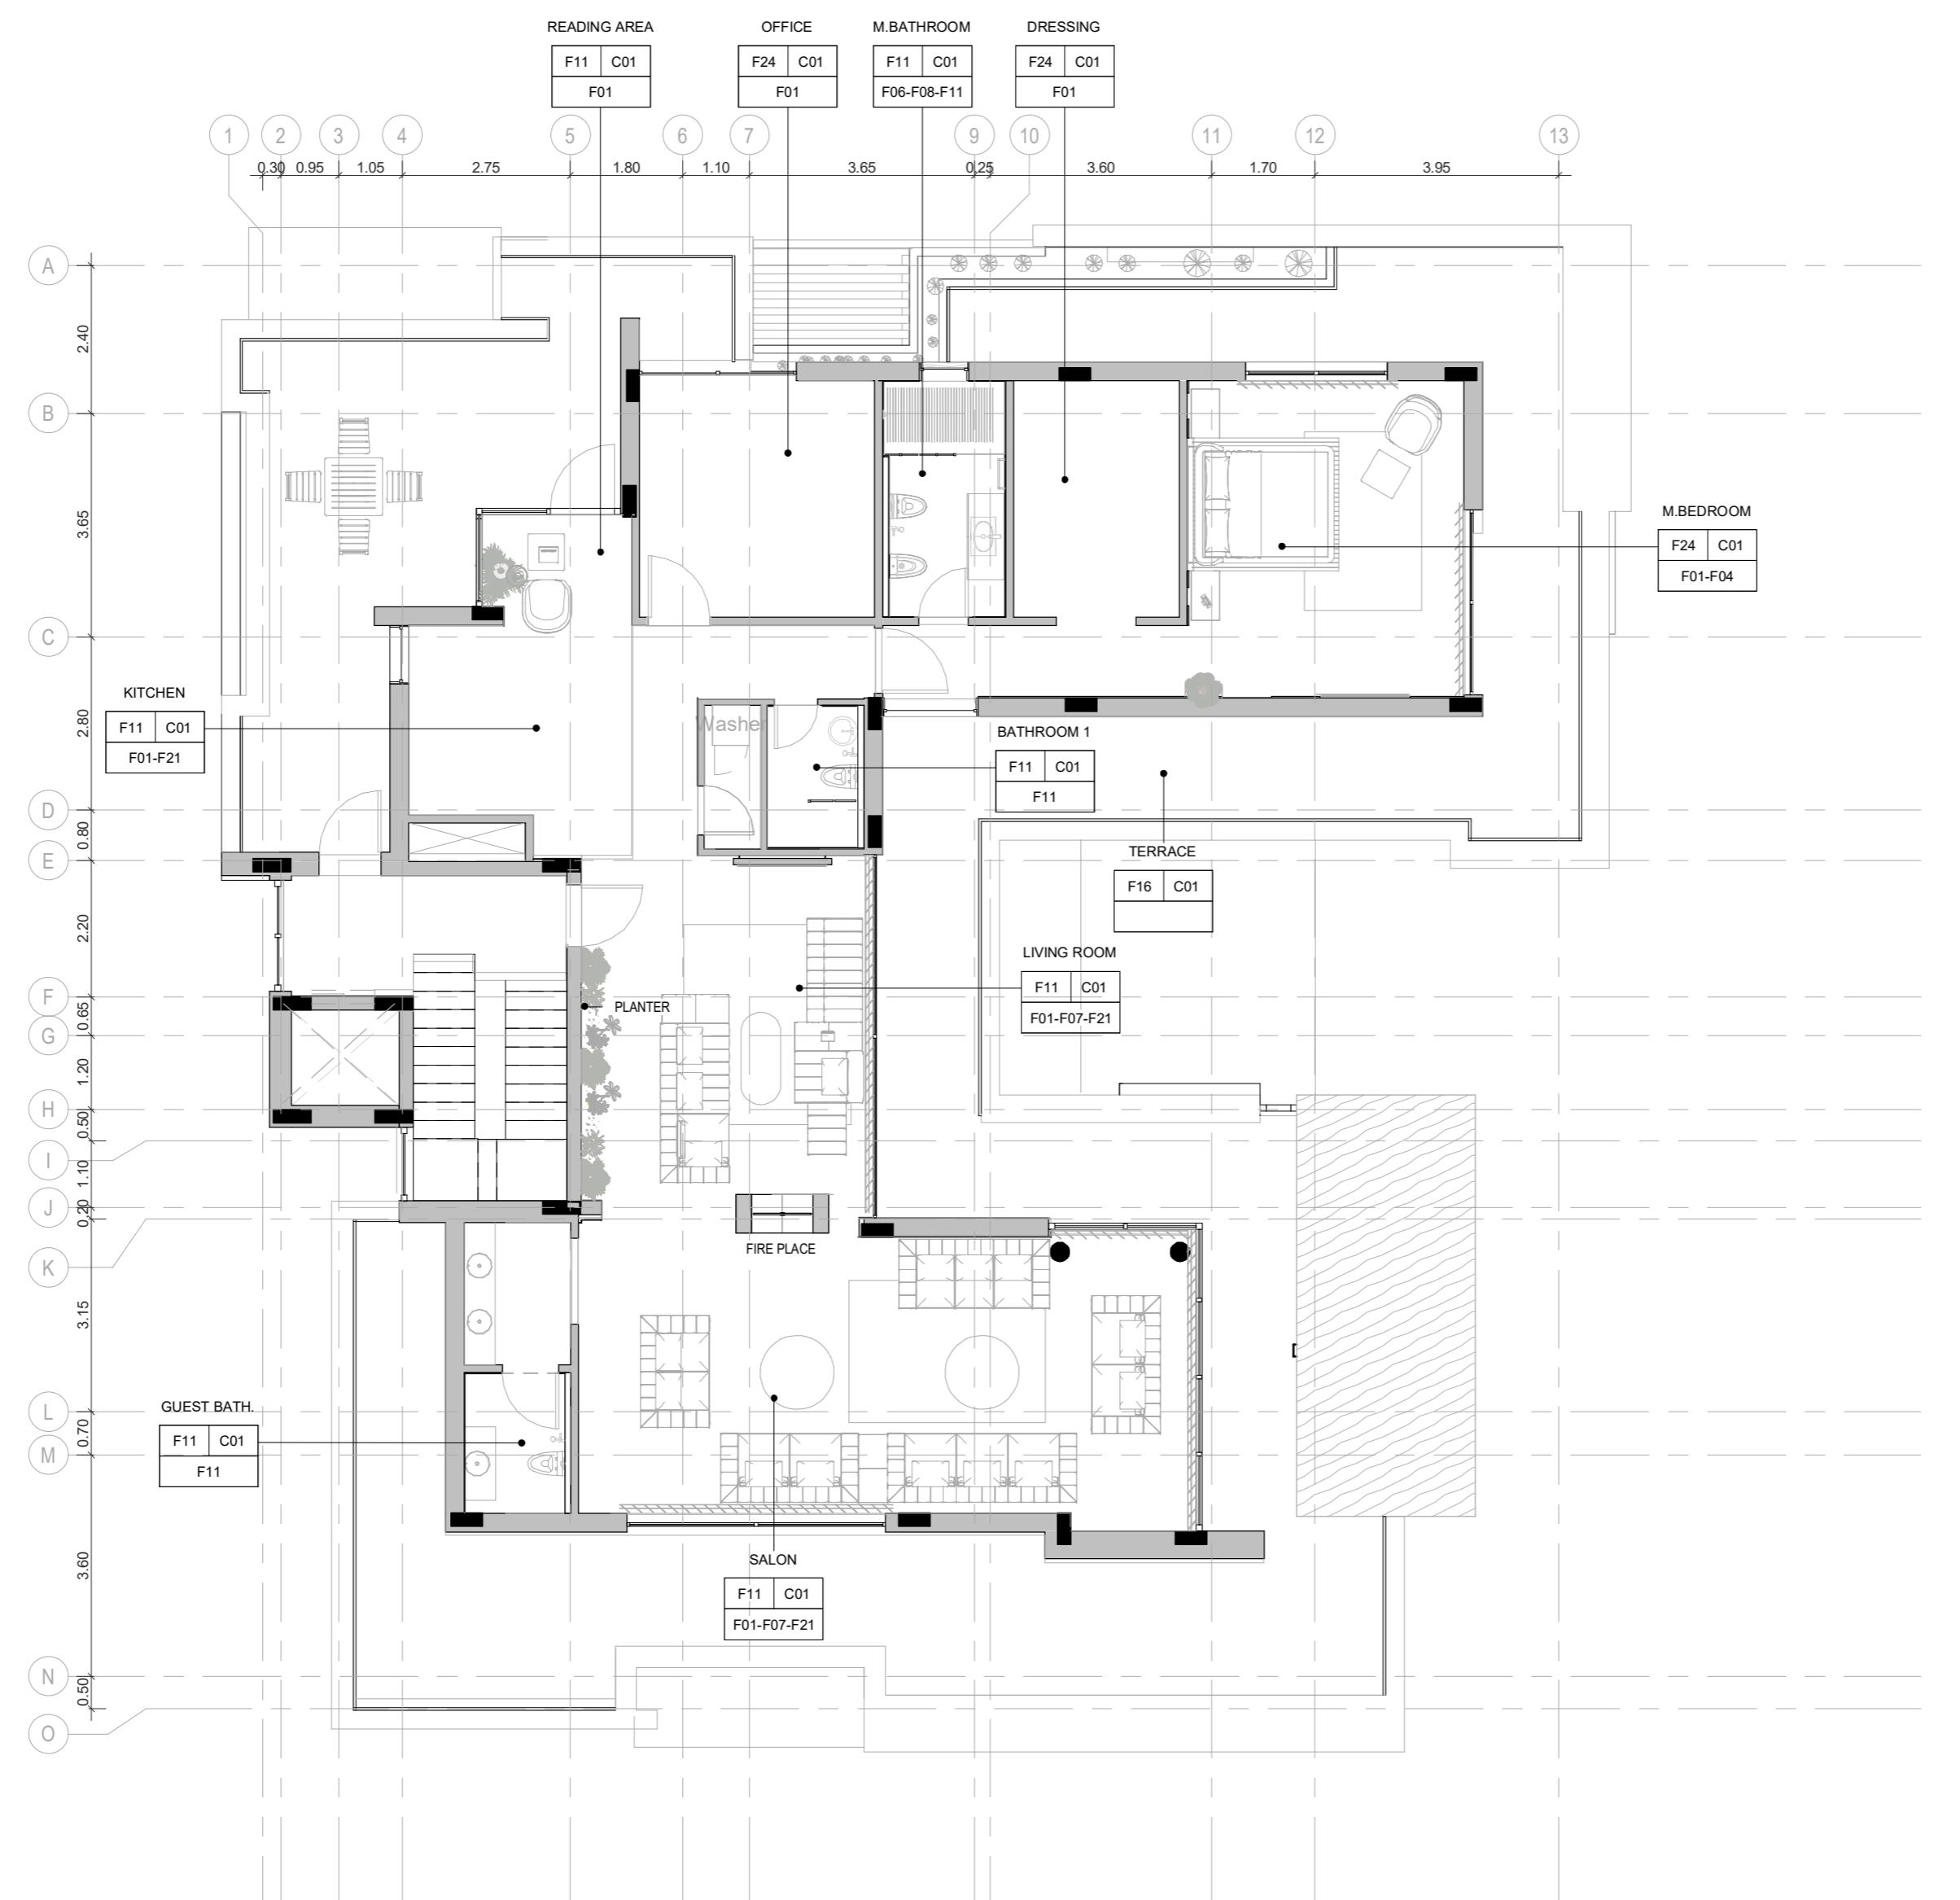

PROJECT NAME

APARTMENTS BUILDING

NOTES

FOR FINISHES REFER TO SHEETS:
ID-6000
ID-6001

ROOM NAME


FLOOR FINISH	CEILING FINISH
--------------	----------------

WALL FINISH

FINISHES SCHEDULE		FINISHES SCHEDULE	
Material:	Mark	Material:	Mark
F01	WHITE PAINT	F15	BEIGE PAINT
F02	GOLD WOOD	F16	TRAVERTINO MARBLE
F03	GOLD STONE	F04	DARK WOOD
F05	DECORATIVE STONE	F06	WOOD
F06	PAINT GOLD METAL EFFECT	F07	BLACK MARBLE
F07	DECORATIVE WOOD	F08	BEIGE MARBLE
F08	GREY STONE	F09	GYRE STONE
F10	WALL PAPER	F11	CALCAGNA
F12	SWIMMING POOL MARBLE	F13	BLACK PAINT
F13	PARQUET	F14	CALCAGNA
F14	WHITE FINISH GRC	F15	

Project Type	Residential
Owner	Khalid Khadir Hasan AL-Saeed
Location	Amman
Plot No.	1659
Basin No.	19
Designed by	A.Shaker Khulief 4809

SHEET NAME			
BASEMENT FLOOR-OVERALL FINISHES PLAN			
Date	06/17/19	Scale	1 : 100

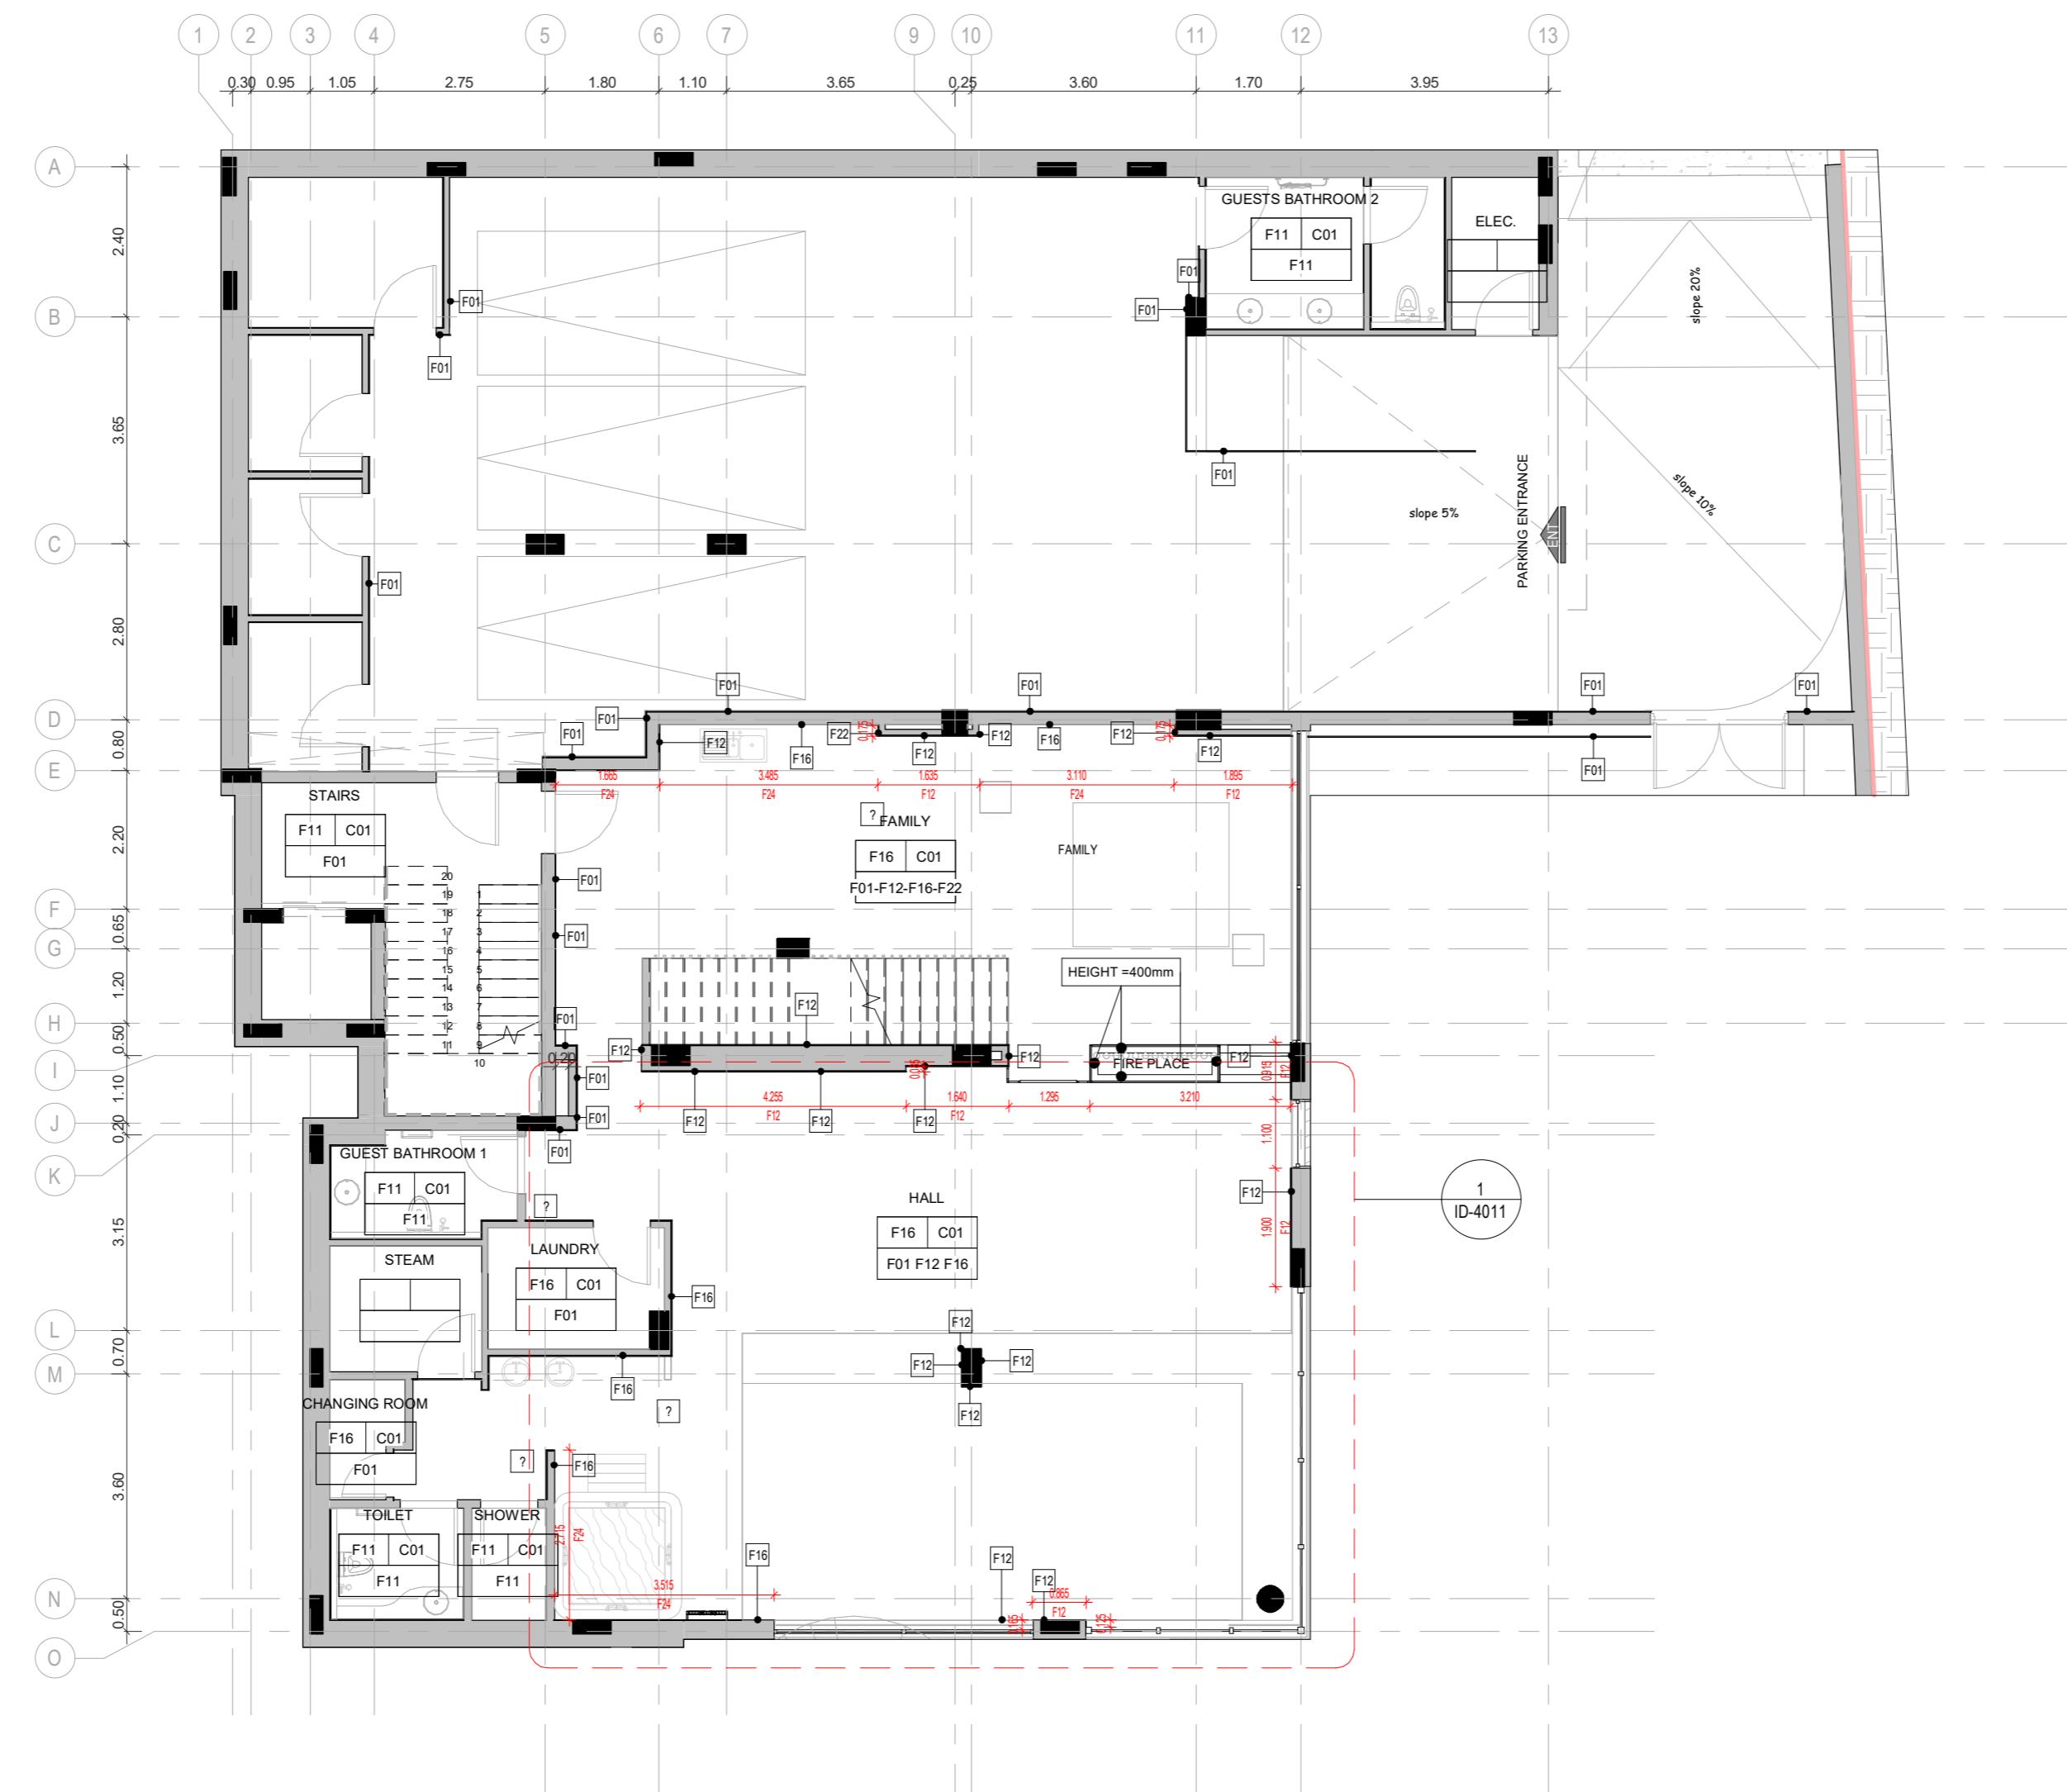

TILING SCHEDULE BASEMENT			
NAME	FLOOR FINISHES	WALL FINISHES	CEILING FINISHES

BASEMENT FLOOR

CHANGING ROOM	F16	F01	C01
LAUNDRY	F16	F01	C01
STAIRS	F11	F01	C01
HALL	F16	F01 F12 F16	C01
FAMILY	F16	F01-F12-F16-F22	C01
TOILET	F11	F11	C01
SHOWER	F11	F11	C01
GUEST BATHROOM 1	F11	F11	C01
GUESTS BATHROOM 2	F11	F11	C01

ID-1210

PROJECT NAME

APARTMENTS BUILDING

NOTES

FOR FINISHES REFER TO SHEETS:
ID-6000
ID-6001

ROOM NAME

FLOOR FINISH	CEILING FINISH
--------------	----------------

WALL FINISH

FINISHES SCHEDULE		FINISHES SCHEDULE	
Material: Mark	DESCRIPTION	Material: Mark	DESCRIPTION
F01	WHITE PAINT	F15	BEIGE PAINT
F02	GOLD WOOD	F16	TRAVERTINO MARBLE
F03	GOLD STONE	F17	LEATHER
F04	DARK WOOD	F18	PAINT GOLD METAL EFFECT
F05	DECORATIVE STONE	F06	WOOD
F06	WOOD	F07	BLACK MARBLE
F07	BLACK MARBLE	F08	BEIGE MARBLE
F08	BEIGE MARBLE	F09	GREY STONE
F09	GREY STONE	F10	WALL PAPER
F10	WALL PAPER	F11	KITCHENNE WOOD
F11	KITCHENNE WOOD	F12	SWIMMING POOL MARBLE
F12	SWIMMING POOL MARBLE	F13	BLACK PAINT
F13	BLACK PAINT	F24	PARQUET
F14	CALCATTA	F25	WHITE FINISH GRC

Project Type Residential

Owner Khalid Khadir Hasan AL-Saeed

Location Amman

Plot No. 1659

Basin No. 19


Designed by A.Shaker Khulief 4809

SHEET NAME

GROUND FLOOR-OVERALL FINISHES PLAN

① GROUND FLOOR-OVERALL FINISHES PLAN

1 : 100

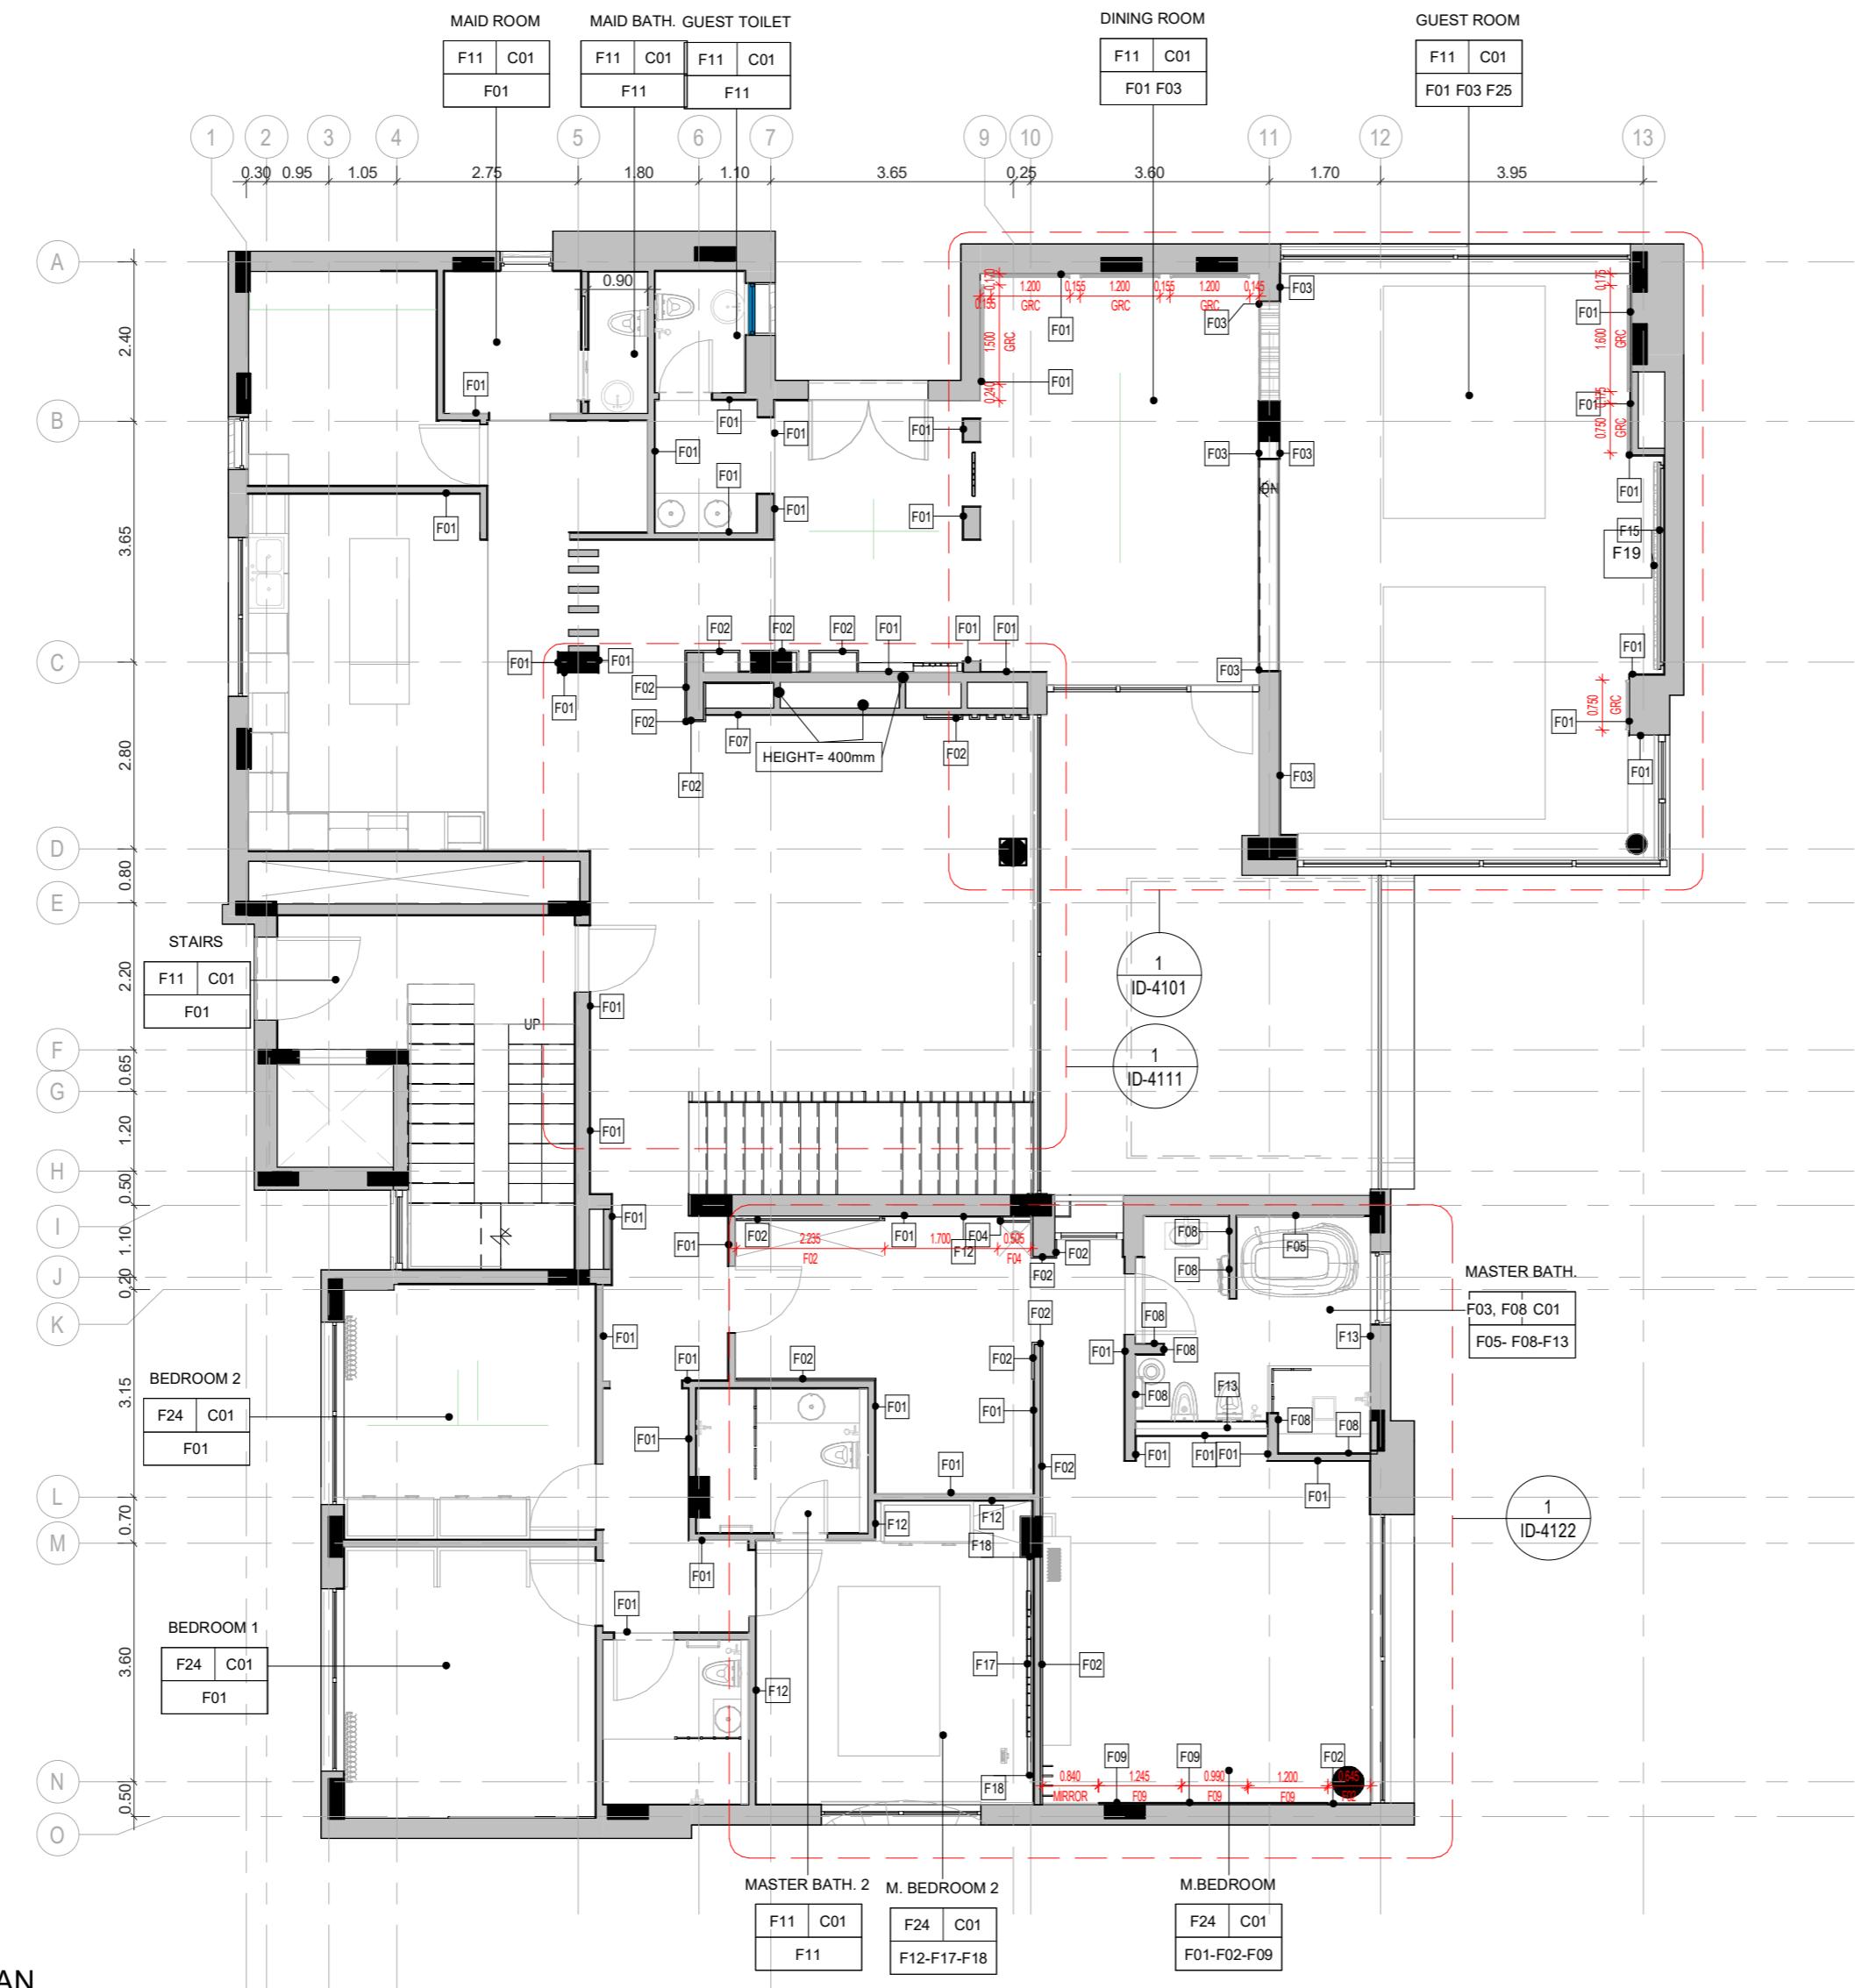

FINISHING SCHEDULE GROUND FLOOR			
NAME	FLOOR FINISHES	WALL FINISHES	CEILING FINISHES
MAID ROOM	F11	F01	C01
DIRTY KITCHEN	F11	F01	C01
BEDROOM 2	F24	F01	C01
BEDROOM 1	F24	F01	C01

FINISHING SCHEDULE GROUND FLOOR			
NAME	FLOOR FINISHES	WALL FINISHES	CEILING FINISHES
TERRACE	F01	F01	C01
KITCHEN	F11	F01	C01
STAIRS	F11	F01	C01
ENTRY	F11	F01 F02	C01
DINING ROOM	F11	F01 F03	C01

FINISHING SCHEDULE GROUND FLOOR			
NAME	FLOOR FINISHES	WALL FINISHES	CEILING FINISHES
GUEST ROOM	F11	F01 F03 F25	C01
M.BEDROOM	F24	F01-F02-F09	C01
LIVING ROOM	F11	F02 F07 F11	C01
M.DRESSING ROOM	F24	F02, F04, F12	C01
MASTER BATH.	F03, F08	F05- F08-F13	C01

FINISHING SCHEDULE GROUND FLOOR			
NAME	FLOOR FINISHES	WALL FINISHES	CEILING FINISHES
MAID BATH.	F11	F11	C01
GUEST TOILET	F11	F11	C01
BATHROOM 1	F11	F11	C01
MASTER BATH. 2	F11	F11	C01
M. BEDROOM 2	F24	F12-F17-F18	C01

ID-1220

Date 06/17/19

Scale 1 : 100

PROJECT NAME	
APARTMENTS BUILDING	
NOTES	
FOR FINISHES REFER TO SHEETS: ID-6000 ID-6001	
ROOM NAME	
FLOOR FINISH	CEILING FINISH
WALL FINISH	
FINISHES SCHEDULE	
Material: Mark	DESCRIPTION
F01	WHITE PAINT
F02	GOLD WOOD
F03	GOLD STONE
F04	DARK WOOD
F05	DECORATIVE STONE
F06	WOOD
F07	BLACK MARBLE
F08	BEIGE MARBLE
F09	GREY STONE
F10	WALL PAPER
F11	KITCHENETTE WOOD
F12	SWIMMING POOL MARBLE
F13	BLACK PAINT
F14	CALCAGNA
FINISHES SCHEDULE	
Material: Mark	DESCRIPTION
F15	BEIGE PAINT
F16	TRAVERTINO MARBLE
F17	LEATHER
F18	PAINT GOLD METAL EFFECT
F19	DECORATIVE WOOD
F20	GREY STONE
F21	CONCRETE FINISH
F22	KITCHENETTE WOOD
F23	SWIMMING POOL WALL FINISH
F24	PARQUET
F25	WHITE FINISH GRC



TILING SCHEDULE - FIRST FLOOR				TILING SCHEDULE - FIRST FLOOR				TILING SCHEDULE - FIRST FLOOR				TILING SCHEDULE - FIRST FLOOR			
NAMES	FLOOR FINISHES	WALL FINISHES	CEILING FINISHES	NAMES	FLOOR FINISHES	WALL FINISHES	CEILING FINISHES	NAMES	FLOOR FINISHES	WALL FINISHES	CEILING FINISHES	NAMES	FLOOR FINISHES	WALL FINISHES	CEILING FINISHES
WIP FIRST FLOOR															
KITCHEN 2	F11	F01	C01	ENTRY	F11	F01	C01	GUEST BATH. 2	F11	F01-F11	C01	DINNIG & SALOON 1	F11	F10	C01
KITCHEN 1	F11	F01	C01	KITCHEN 1	F11	F01	C01	M.DRESSING 2	F24	F02	C01	M.BATHROOM 1	F11	F11	C01
CORRIDOR	F11	F01	C01	CORRIDOR	F11	F01	C01	M.DRESSING 1	F24	F02	C01	BATHROOM 2	F11	F11	C01
BEDROOM 2	F24	F01	C01	BEDROOM 1	F24	F01	C01	M.BEDROOM 1	F24	F02, F14	C01	M.BATHROOM 2	F11	F11	C01
BEDROOM 3	F24	F01	C01	ENTRY 1	F11	F01	C01	BEDROOM 2	F24	F02, F14	C01	BATHROOM 1	F11	F11	C01
BEDROOM 4	F24	F01	C01	SALOON & DINNING 2	F11	F01-F06-F10-F19	C01	LIVING ROOM 2	F11	F02-F04-F20	C01	GUEST BATH. 1	F11	F11	C01
STAIRS	F11	F01	C01					LIVING ROOM 1	F11	F02-F04-F20	C01				

FIRST FLOOR-OVERALL FINISHES PLAN
ID-1230
Date 06/17/19
Scale 1 : 100

PROJECT NAME

APARTMENTS BUILDING

NOTES

FOR FINISHES REFER TO SHEETS:
ID-6000
ID-6001

ROOM NAME

FLOOR FINISH	CEILING FINISH
--------------	----------------


WALL FINISH

FINISHES SCHEDULE		FINISHES SCHEDULE	
Material:	Mark	Material:	Mark
F01		WHITE PAINT	F15
F02		BEIGE PAINT	F16
F03		TRAVERTINO	MARBLE
F04		GOLD STONE	
F05		DARK WOOD	
F06		DECORATIVE STONE	
F07		WOOD	
F08		PAINT GOLD METAL EFFECT	
F09		BLACK MARBLE	
F10		DECORATIVE WOOD	
F11		BEIGE MARBLE	
F12		GREY STONE	
F13		CONCRETE FINISH	
F14		WALL PAPER	
F15		KITCHENNETE	WOOD
F16		SWIMMING POOL	MARBLE
F17		BLACK PAINT	
F18		PARQUET	
F19		CALCAGNA	
F20		WHITE FINISH GRC	

Project Type	Residential
Owner	Khalid Khadir Hasan AL-Saeed
Location	Amman
Plot No.	1659
Basin No.	19
Designed by	A.Shaker Khulief 4809

SHEET NAME
ROOF FLOOR-OVERALL FINISHES PLAN

ID-1240
Date 06/17/19
Scale 1 : 100

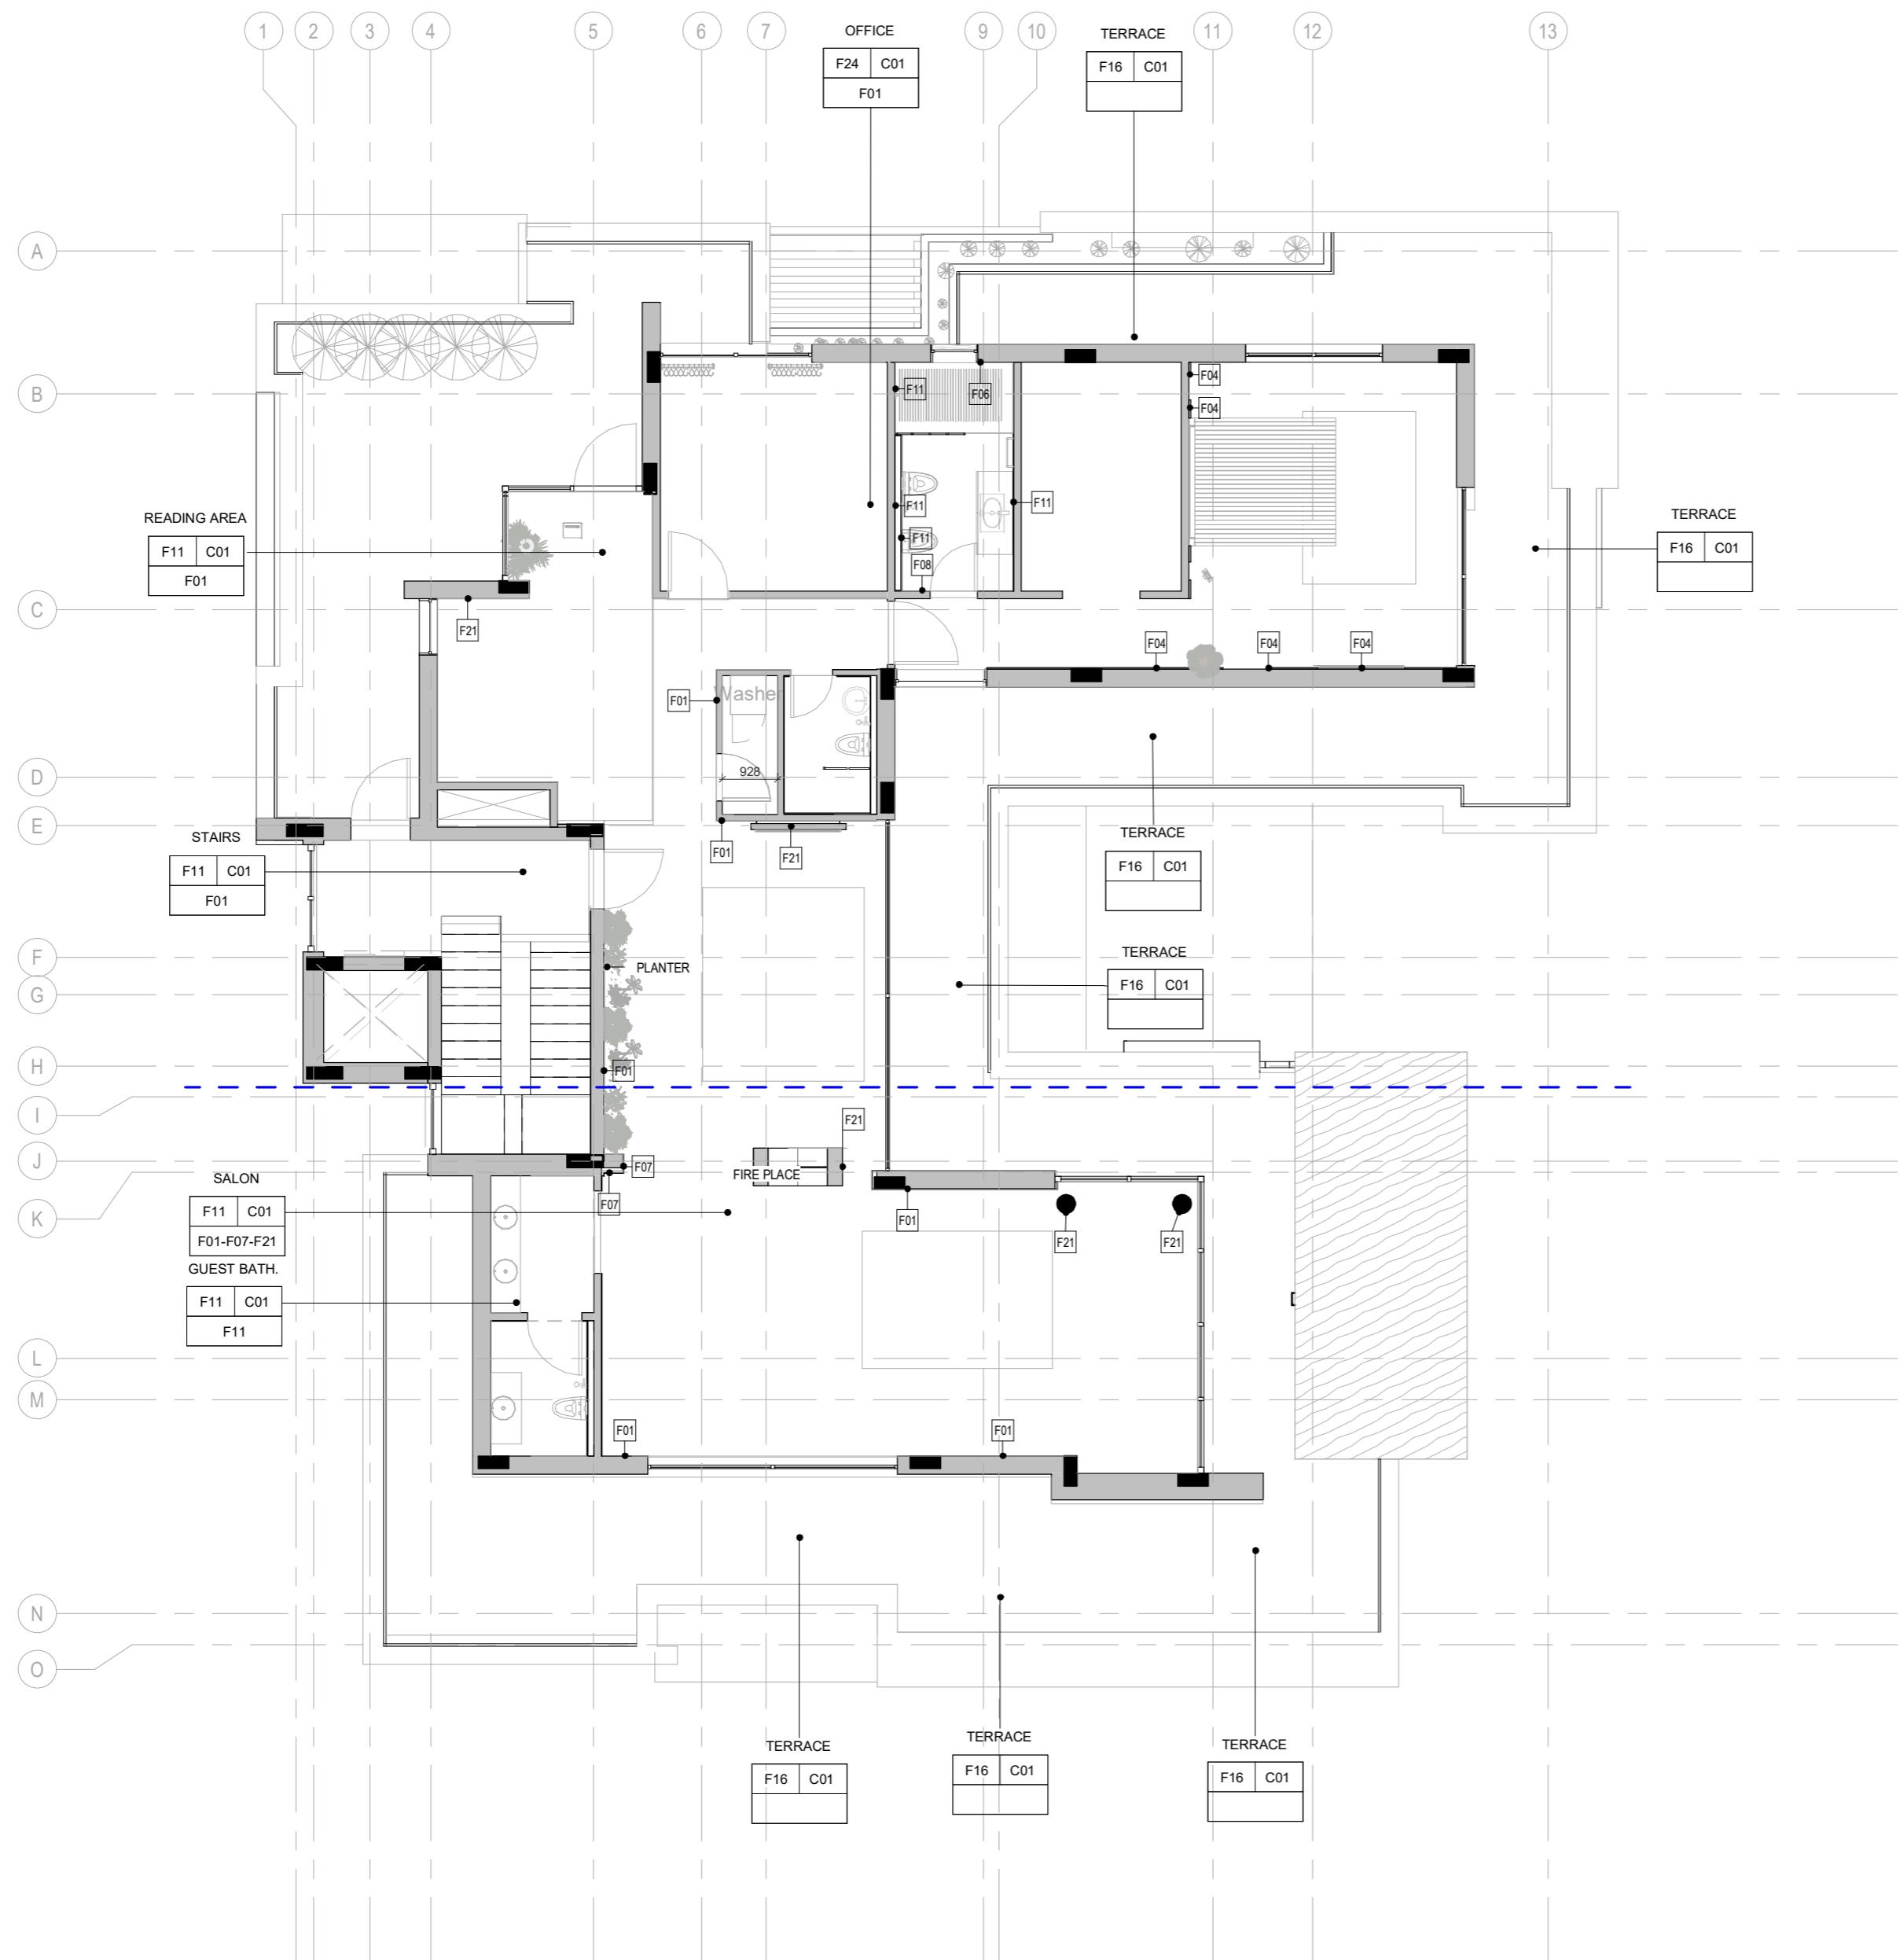


① ROOF FLOOR -OVERALL FINISHES PLAN
1 : 100


TILING SCHEDULE - ROOF FLOOR			
Name	Floor Tiles	Wall Tiling Types	Ceiling Finish

WIP ROOF FLOOR-MASTER BATHROOM			
TERRACE	F16	F01-F04	C01
OFFICE	F24	F01	C01
STAIRS	F11	F01	C01
READING AREA	F11	F01	C01
LAUNDRY	F11	F01	C01
DRESSING	F24	F01	C01

TILING SCHEDULE - ROOF FLOOR			
Name	Floor Tiles	Wall Tiling Types	Ceiling Finish

M.BEDROOM	F24	F01-F04	C01
SALON	F11	F01-F07-F21	C01
LIVING ROOM	F11	F01-F07-F21	C01
KITCHEN	F11	F01-F21	C01
M.BATHROOM	F11	F06-F08-F11	C01
GUEST BATH.	F11	F11	C01
BATHROOM 1	F11	F11	C01

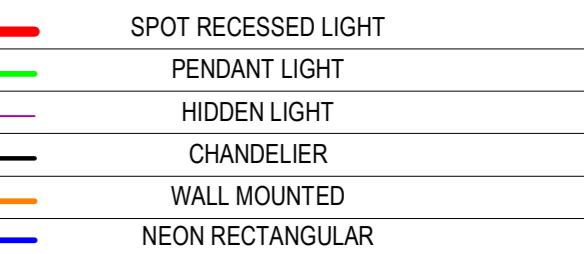PROJECT NAME	APARTMENTS BUILDING
NOTES	FOR FINISHES REFER TO SHEETS: ID-6000 ID-6001
	
Project Type	Residential
Owner	Khalid Khadir Hasan AL-Saeed
Location	Amman
Plot No.	1659
Basin No.	19
Designed by	A.Shaker Khulief 4809
SHEET NAME	BASEMENT FLOOR-OVERALL CEILING PLAN
ID-1310	
Date	05/20/19
Scale	As indicated

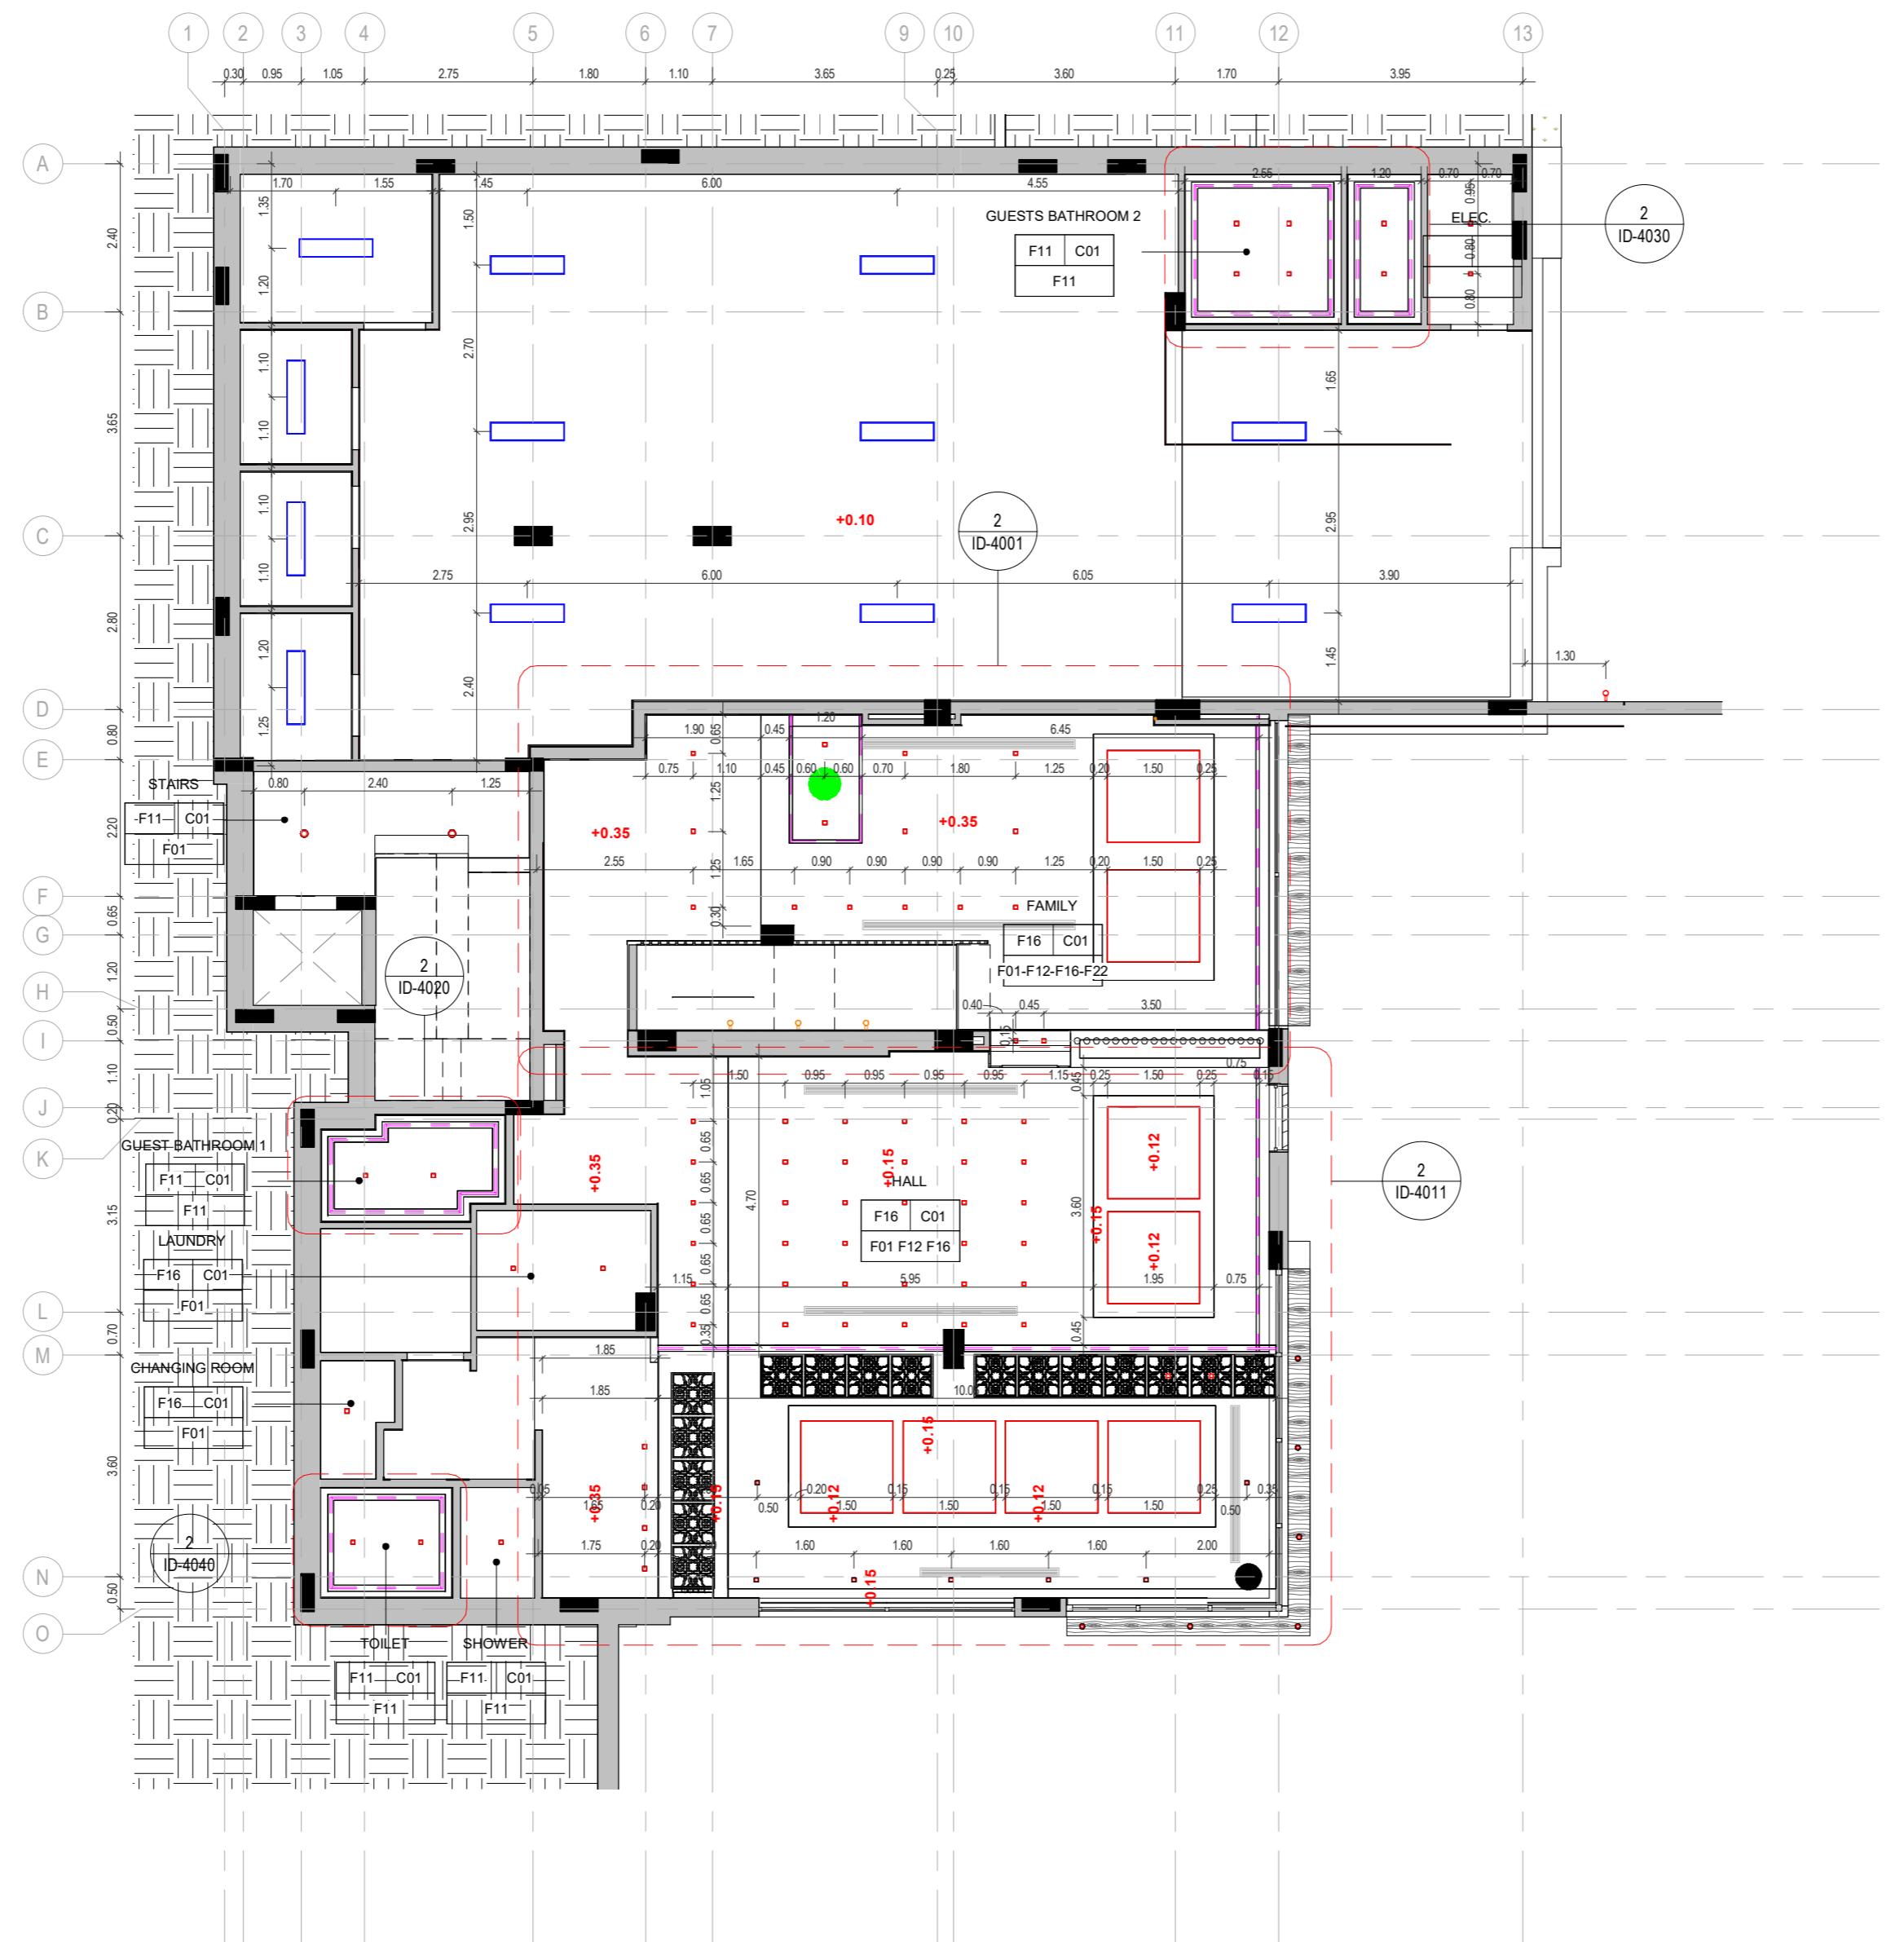


PROJECT NAME

APARTMENTS BUILDING

NOTES

FOR FINISHES REFER TO SHEETS:
ID-6000
ID-6001

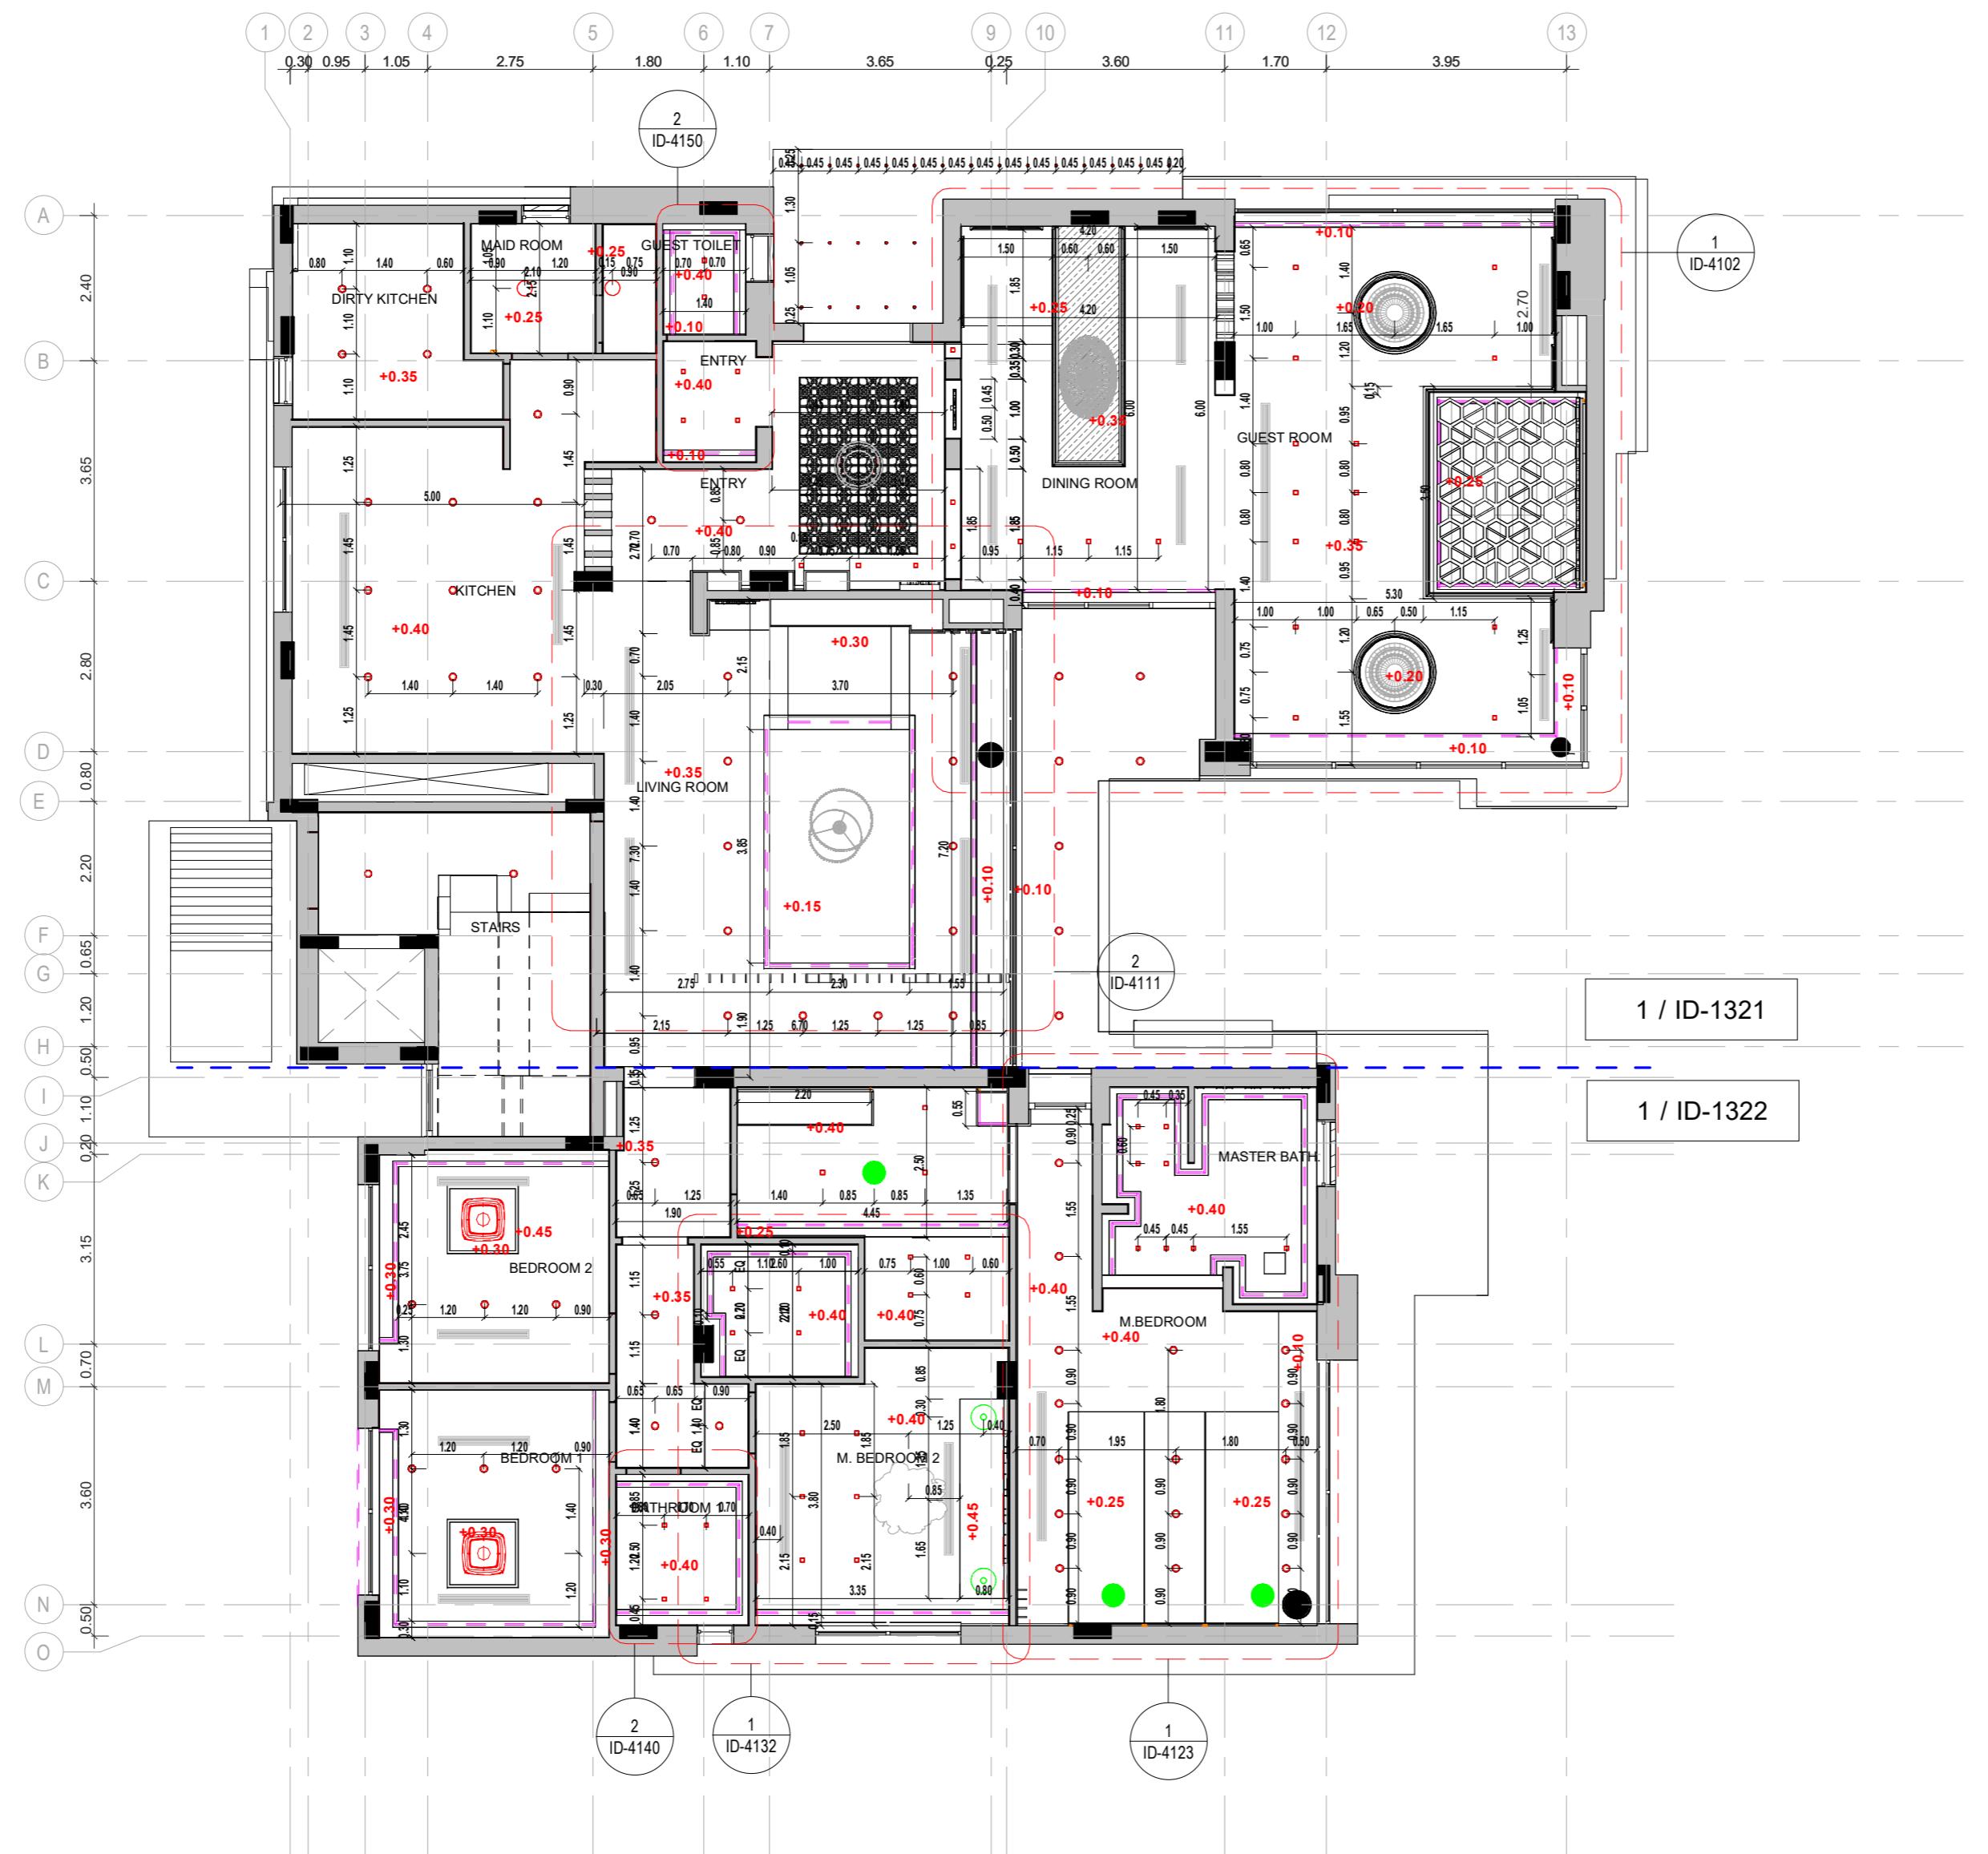

- SPOT RECESSED LIGHT
- PENDANT LIGHT
- HIDDEN LIGHT
- CHANDELIER
- WALL MOUNTED
- NEON RECTANGULAR

Project Type	Residential
Owner	Khalid Khadir Hasan AL-Saeed
Location	Amman
Plot No.	1659
Basin No.	19
Designed by	A.Shaker Khulief 4809

SHEET NAME
GROUND FLOOR-OVERALL CEILING PLAN

ID-1320

Date	05/20/19
Scale	As indicated

PROJECT NAME

APARTMENTS BUILDING

NOTES

FOR FINISHES REFER TO SHEETS:
ID-6000
ID-6001


- SPOT RECESSED LIGHT
- PENDANT LIGHT
- HIDDEN LIGHT
- CHANDELIER
- WALL MOUNTED
- NEON RECTANGULAR

Project Type	Residential
Owner	Khalid Khadir Hasan AL-Saeed
Location	Amman
Plot No.	1659
Basin No.	19
Designed by	A.Shaker Khulief 4809

SHEET NAME
GROUND FLOOR-OVRALL CEILING PLAN-PART01

ID-1321

Date 07/08/19
Scale 1 : 50

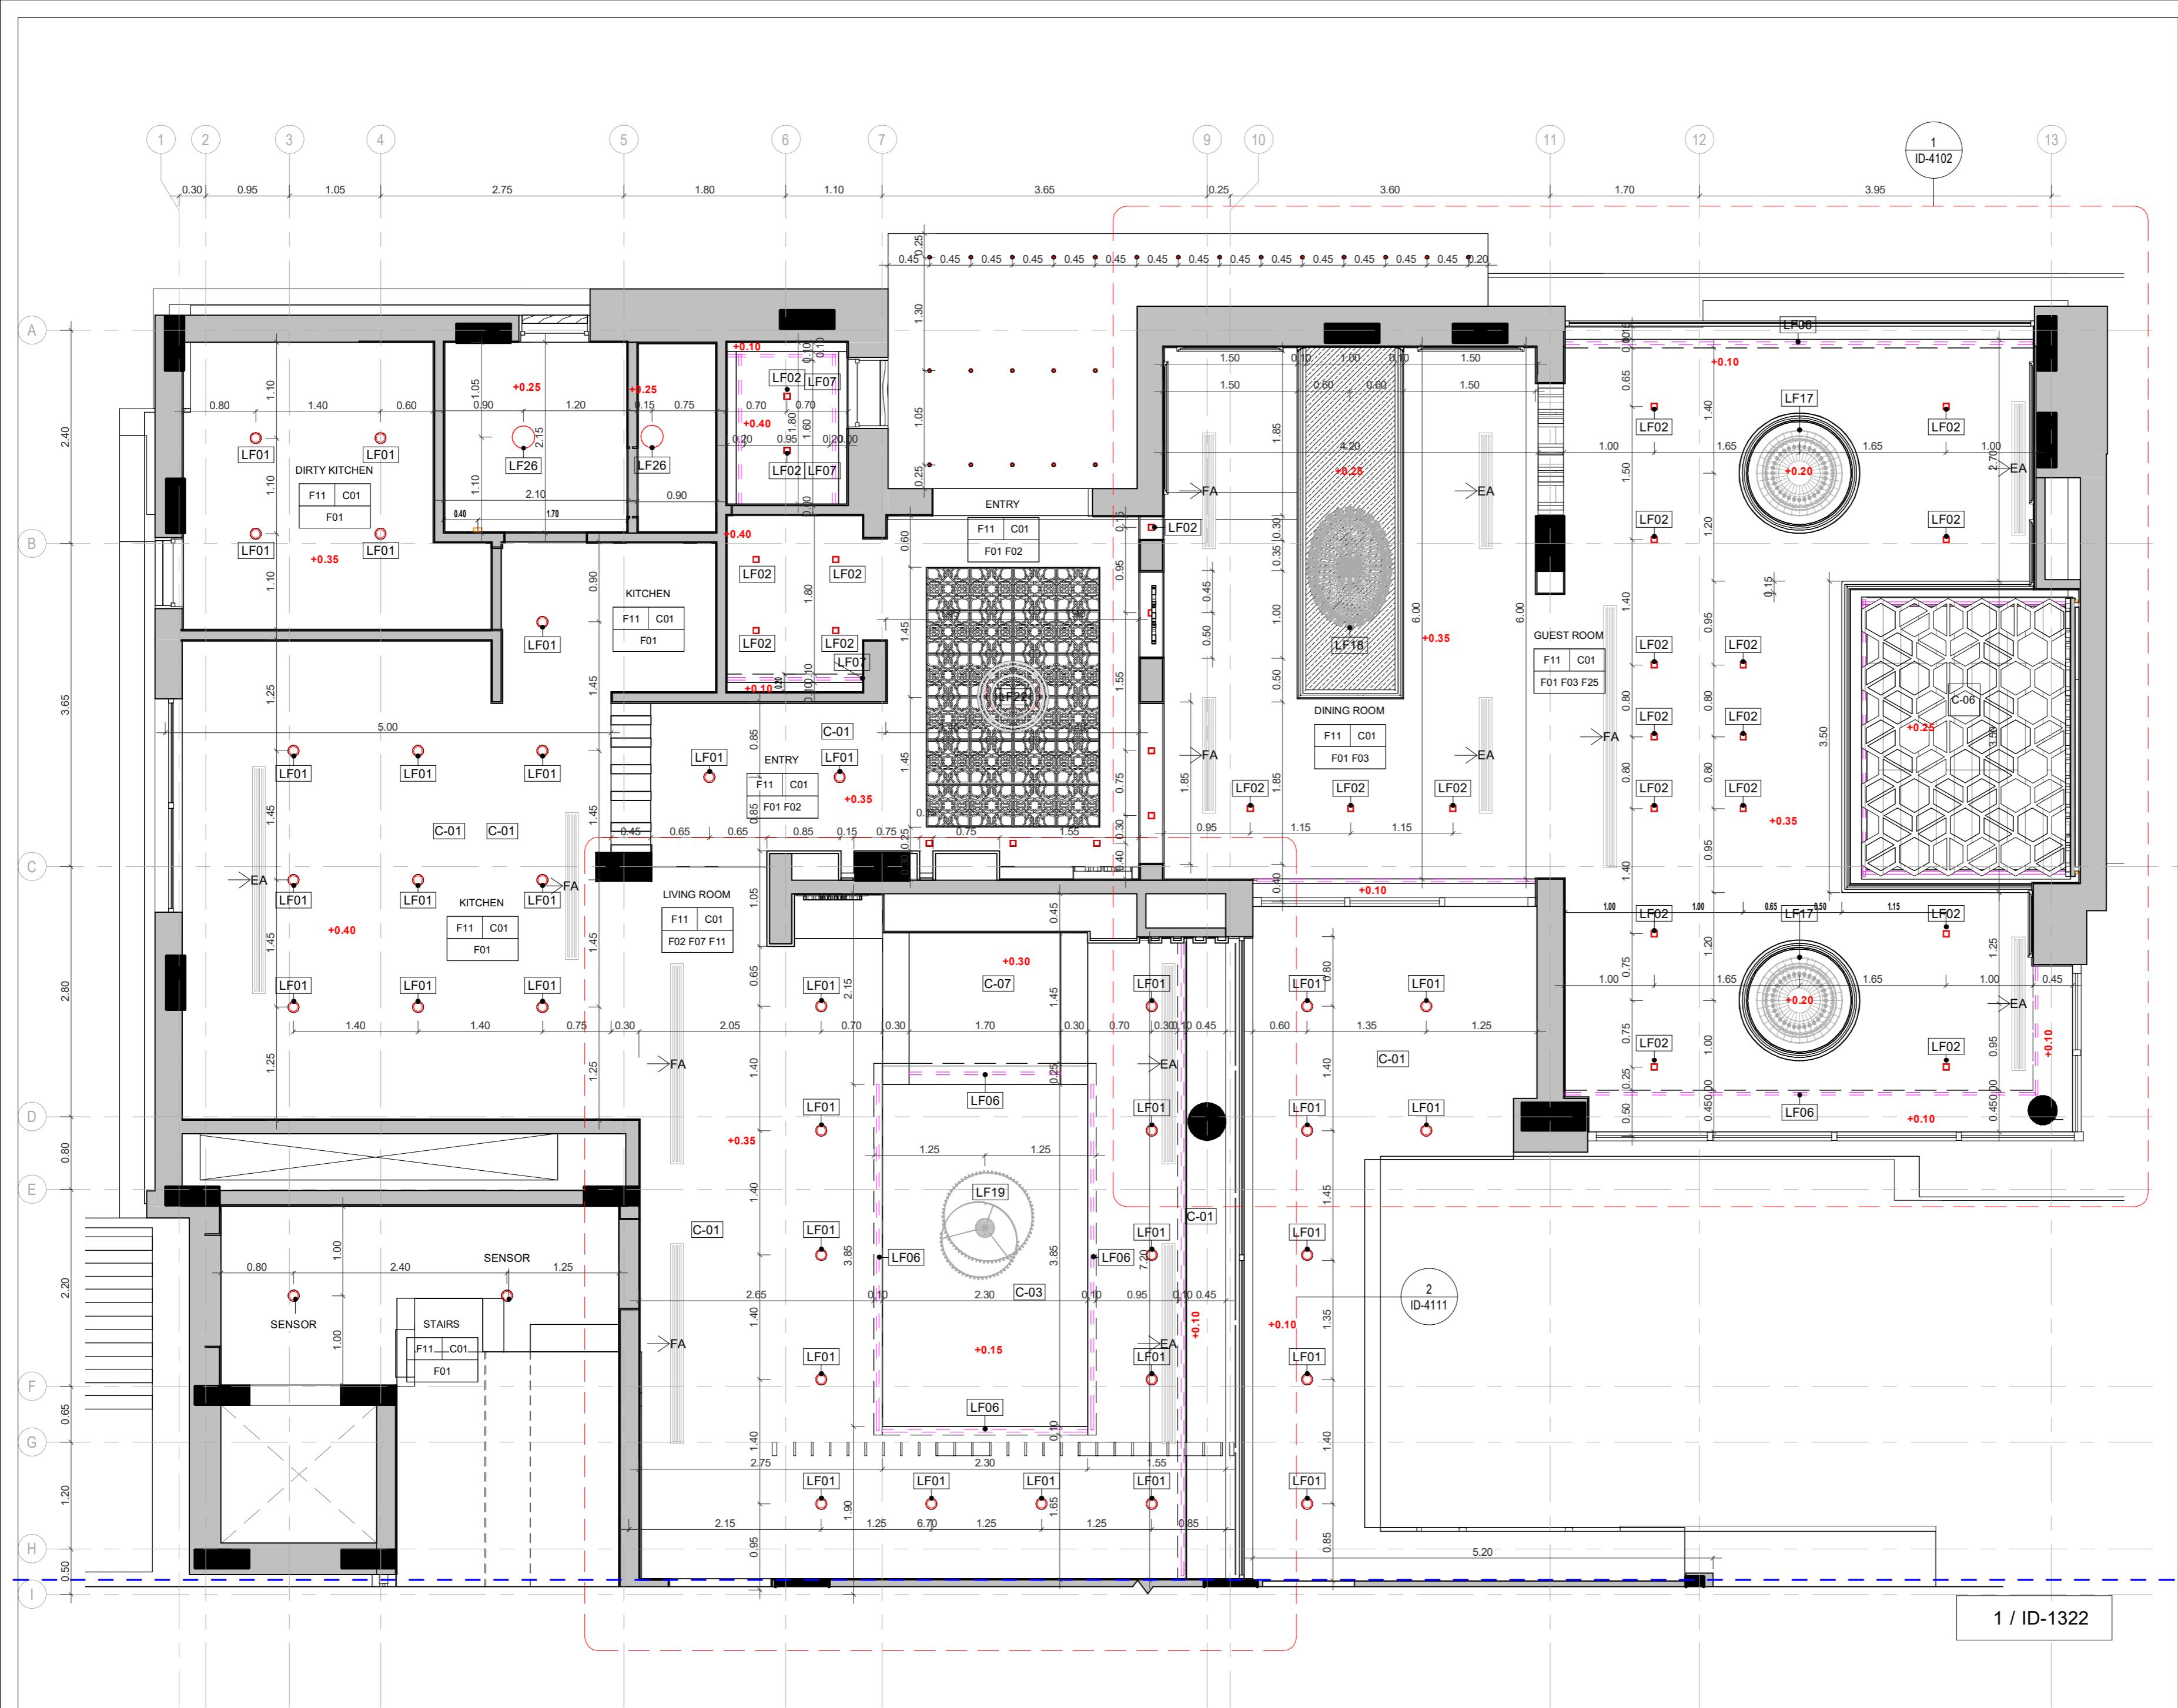

PROJECT NAME

APARTMENTS BUILDING

NOTES

FOR FINISHES REFER TO SHEETS:
ID-6000
ID-6001

- SPOT RECESSED LIGHT
- PENDANT LIGHT
- HIDDEN LIGHT
- CHANDELIER
- WALL MOUNTED
- NEON RECTANGULAR

Project Type	Residential
Owner	Khalid Khadir Hasan AL-Saeed
Location	Amman
Plot No.	1659
Basin No.	19
Designed by	A.Shaker Khulief 4809

SHEET NAME
GROUND FLOOR-OVRALL CEILING PLAN-PART 02

ID-1322

Date	07/08/19
Scale	1 : 50



PROJECT NAME

APARTMENTS BUILDING

NOTES

FOR FINISHES REFER TO SHEETS:
ID-6000
ID-6001


- SPOT RECESSED LIGHT
- PENDANT LIGHT
- HIDDEN LIGHT
- CHANDELIER
- WALL MOUNTED
- NEON RECTANGULAR

Project Type	Residential
Owner	Khalid Khadir Hasan AL-Saeed
Location	Amman
Plot No.	1659
Basin No.	19
Designed by	A.Shaker Khulief 4809

SHEET NAME
FIRST FLOOR-OVERALL CEILING PLAN

ID-1330

Date	05/20/19
Scale	As indicated

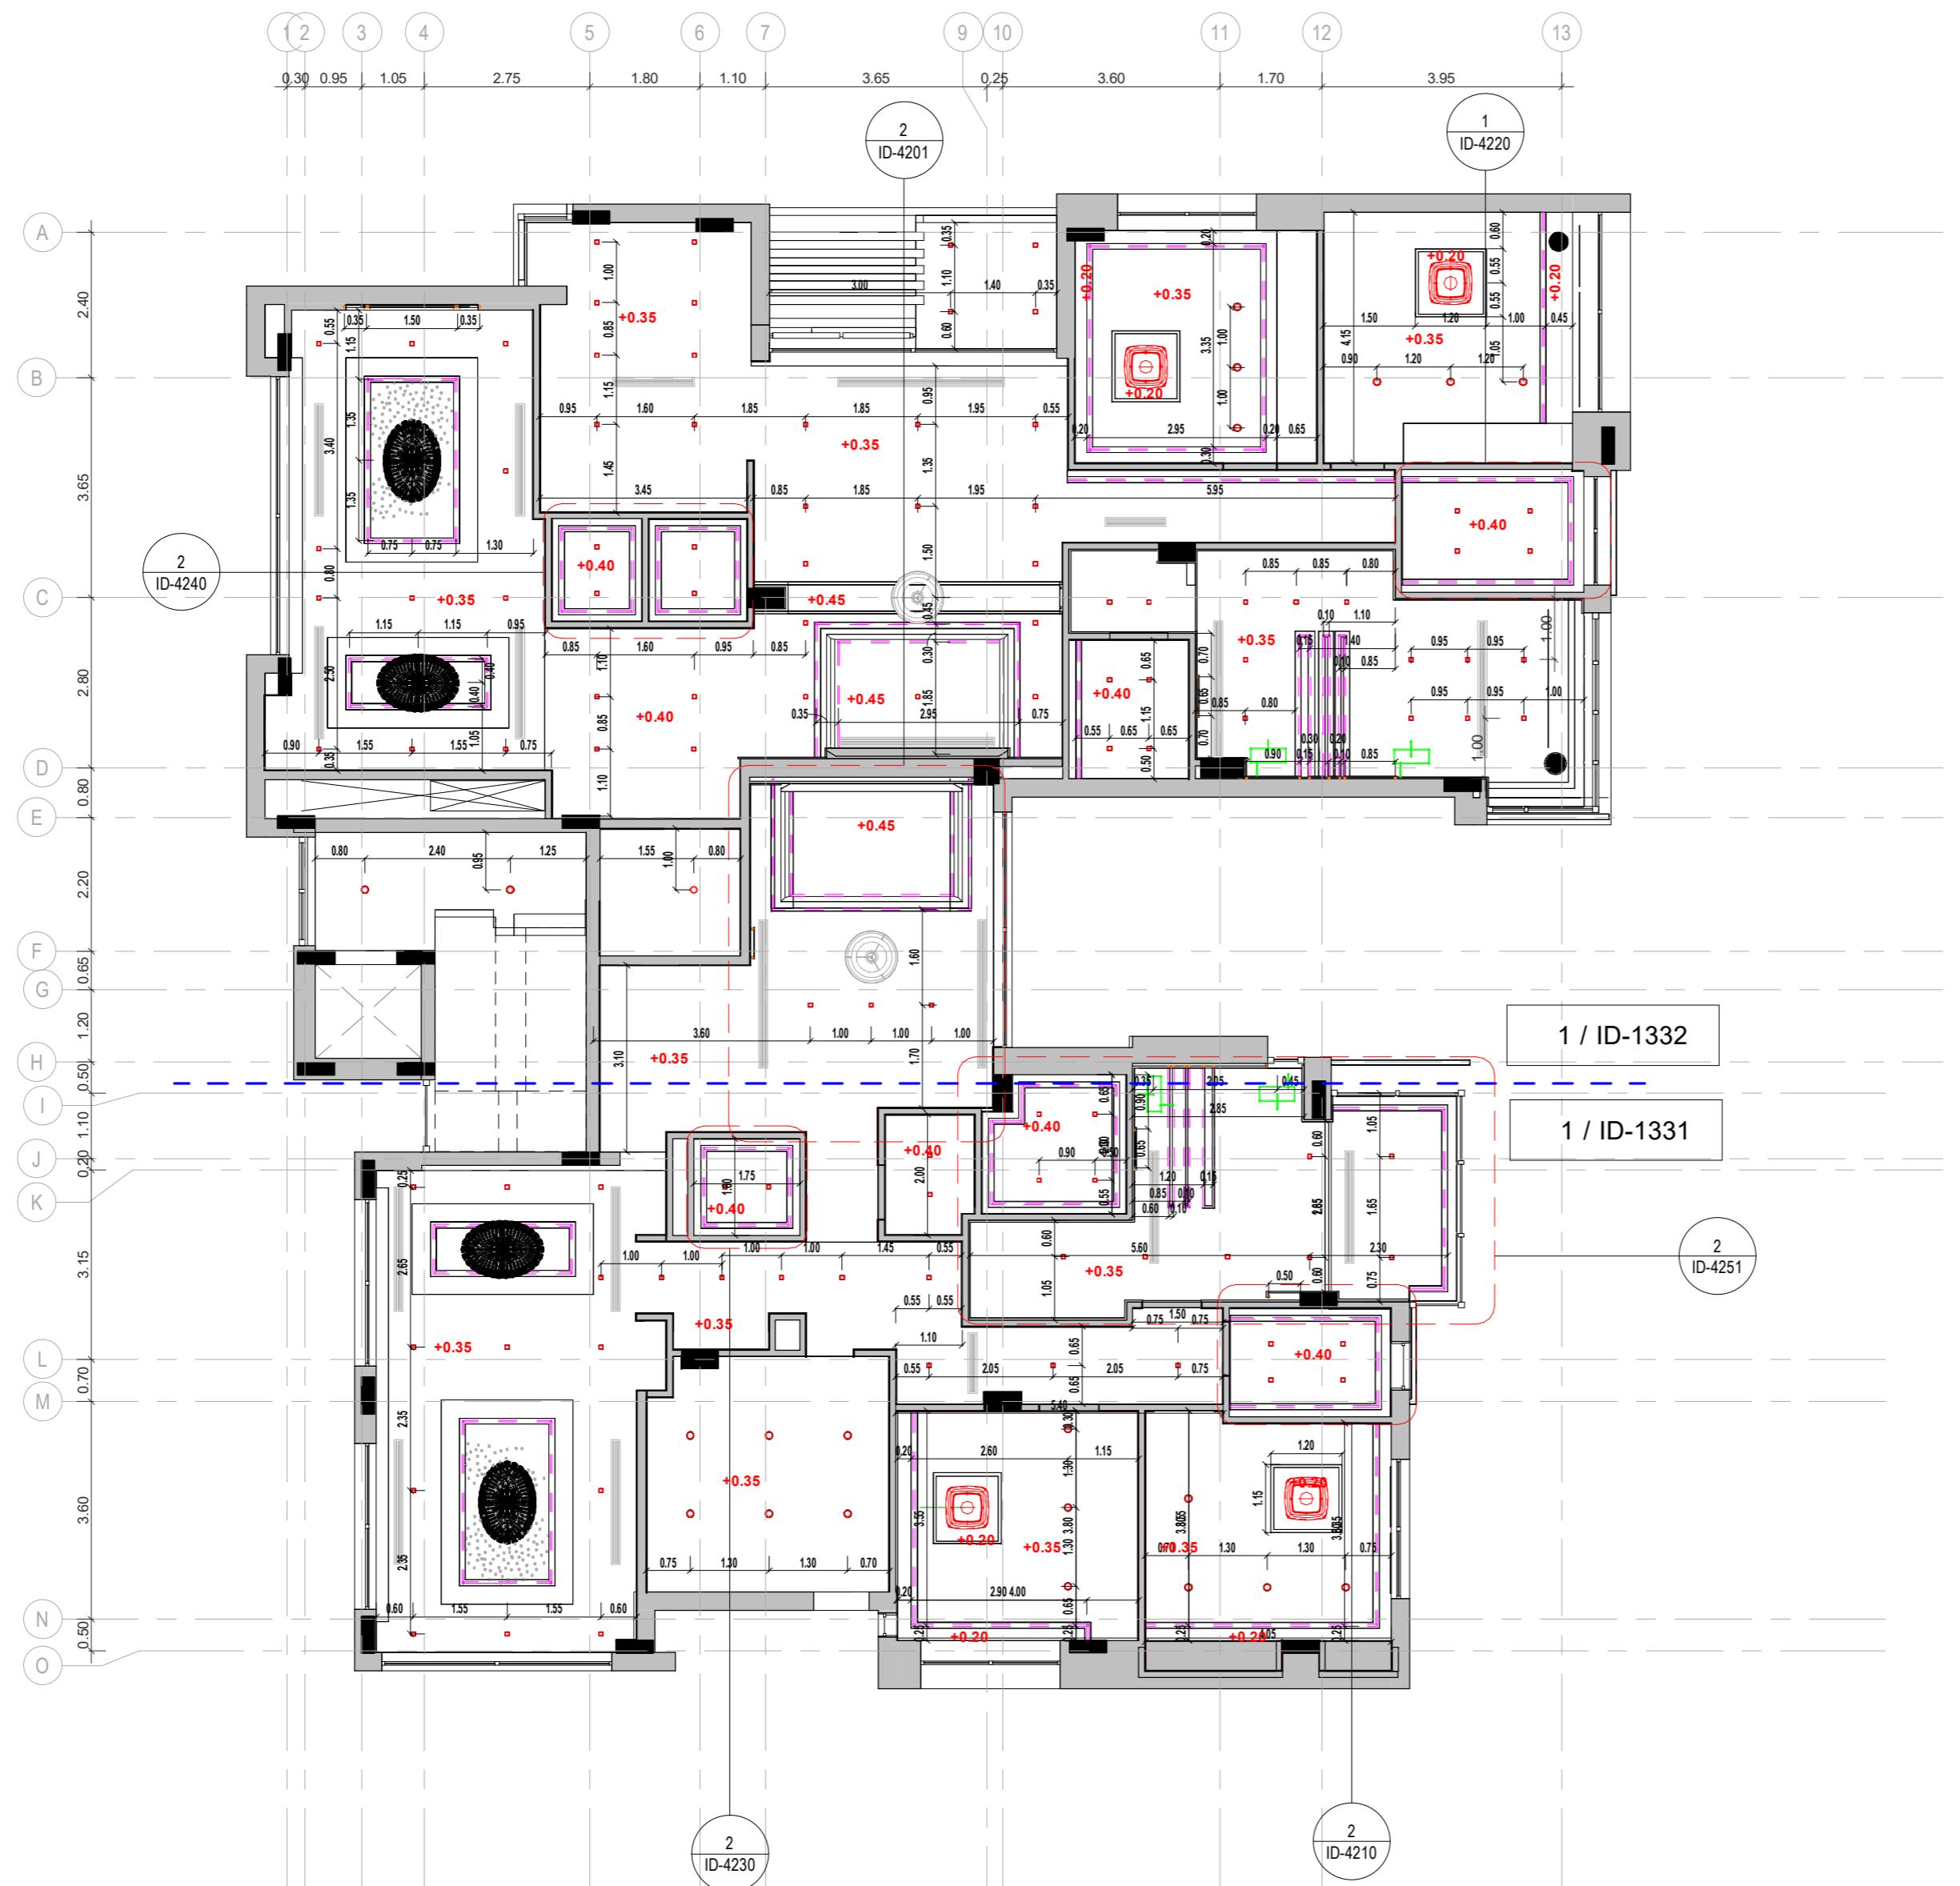

PROJECT NAME

APARTMENTS BUILDING

NOTES

FOR FINISHES REFER TO SHEETS:
ID-6000
ID-6001




Project Type	Residential
Owner	Khalid Khadir Hasan AL-Saeed
Location	Amman
Plot No.	1659
Basin No.	19
Designed by	A.Shaker Khulief 4809

SHEET NAME

**FIRST FLOOR-OVERALL
CEILING PLAN-PART01**

ID-1331

Date	07/13/19
Scale	1 : 50

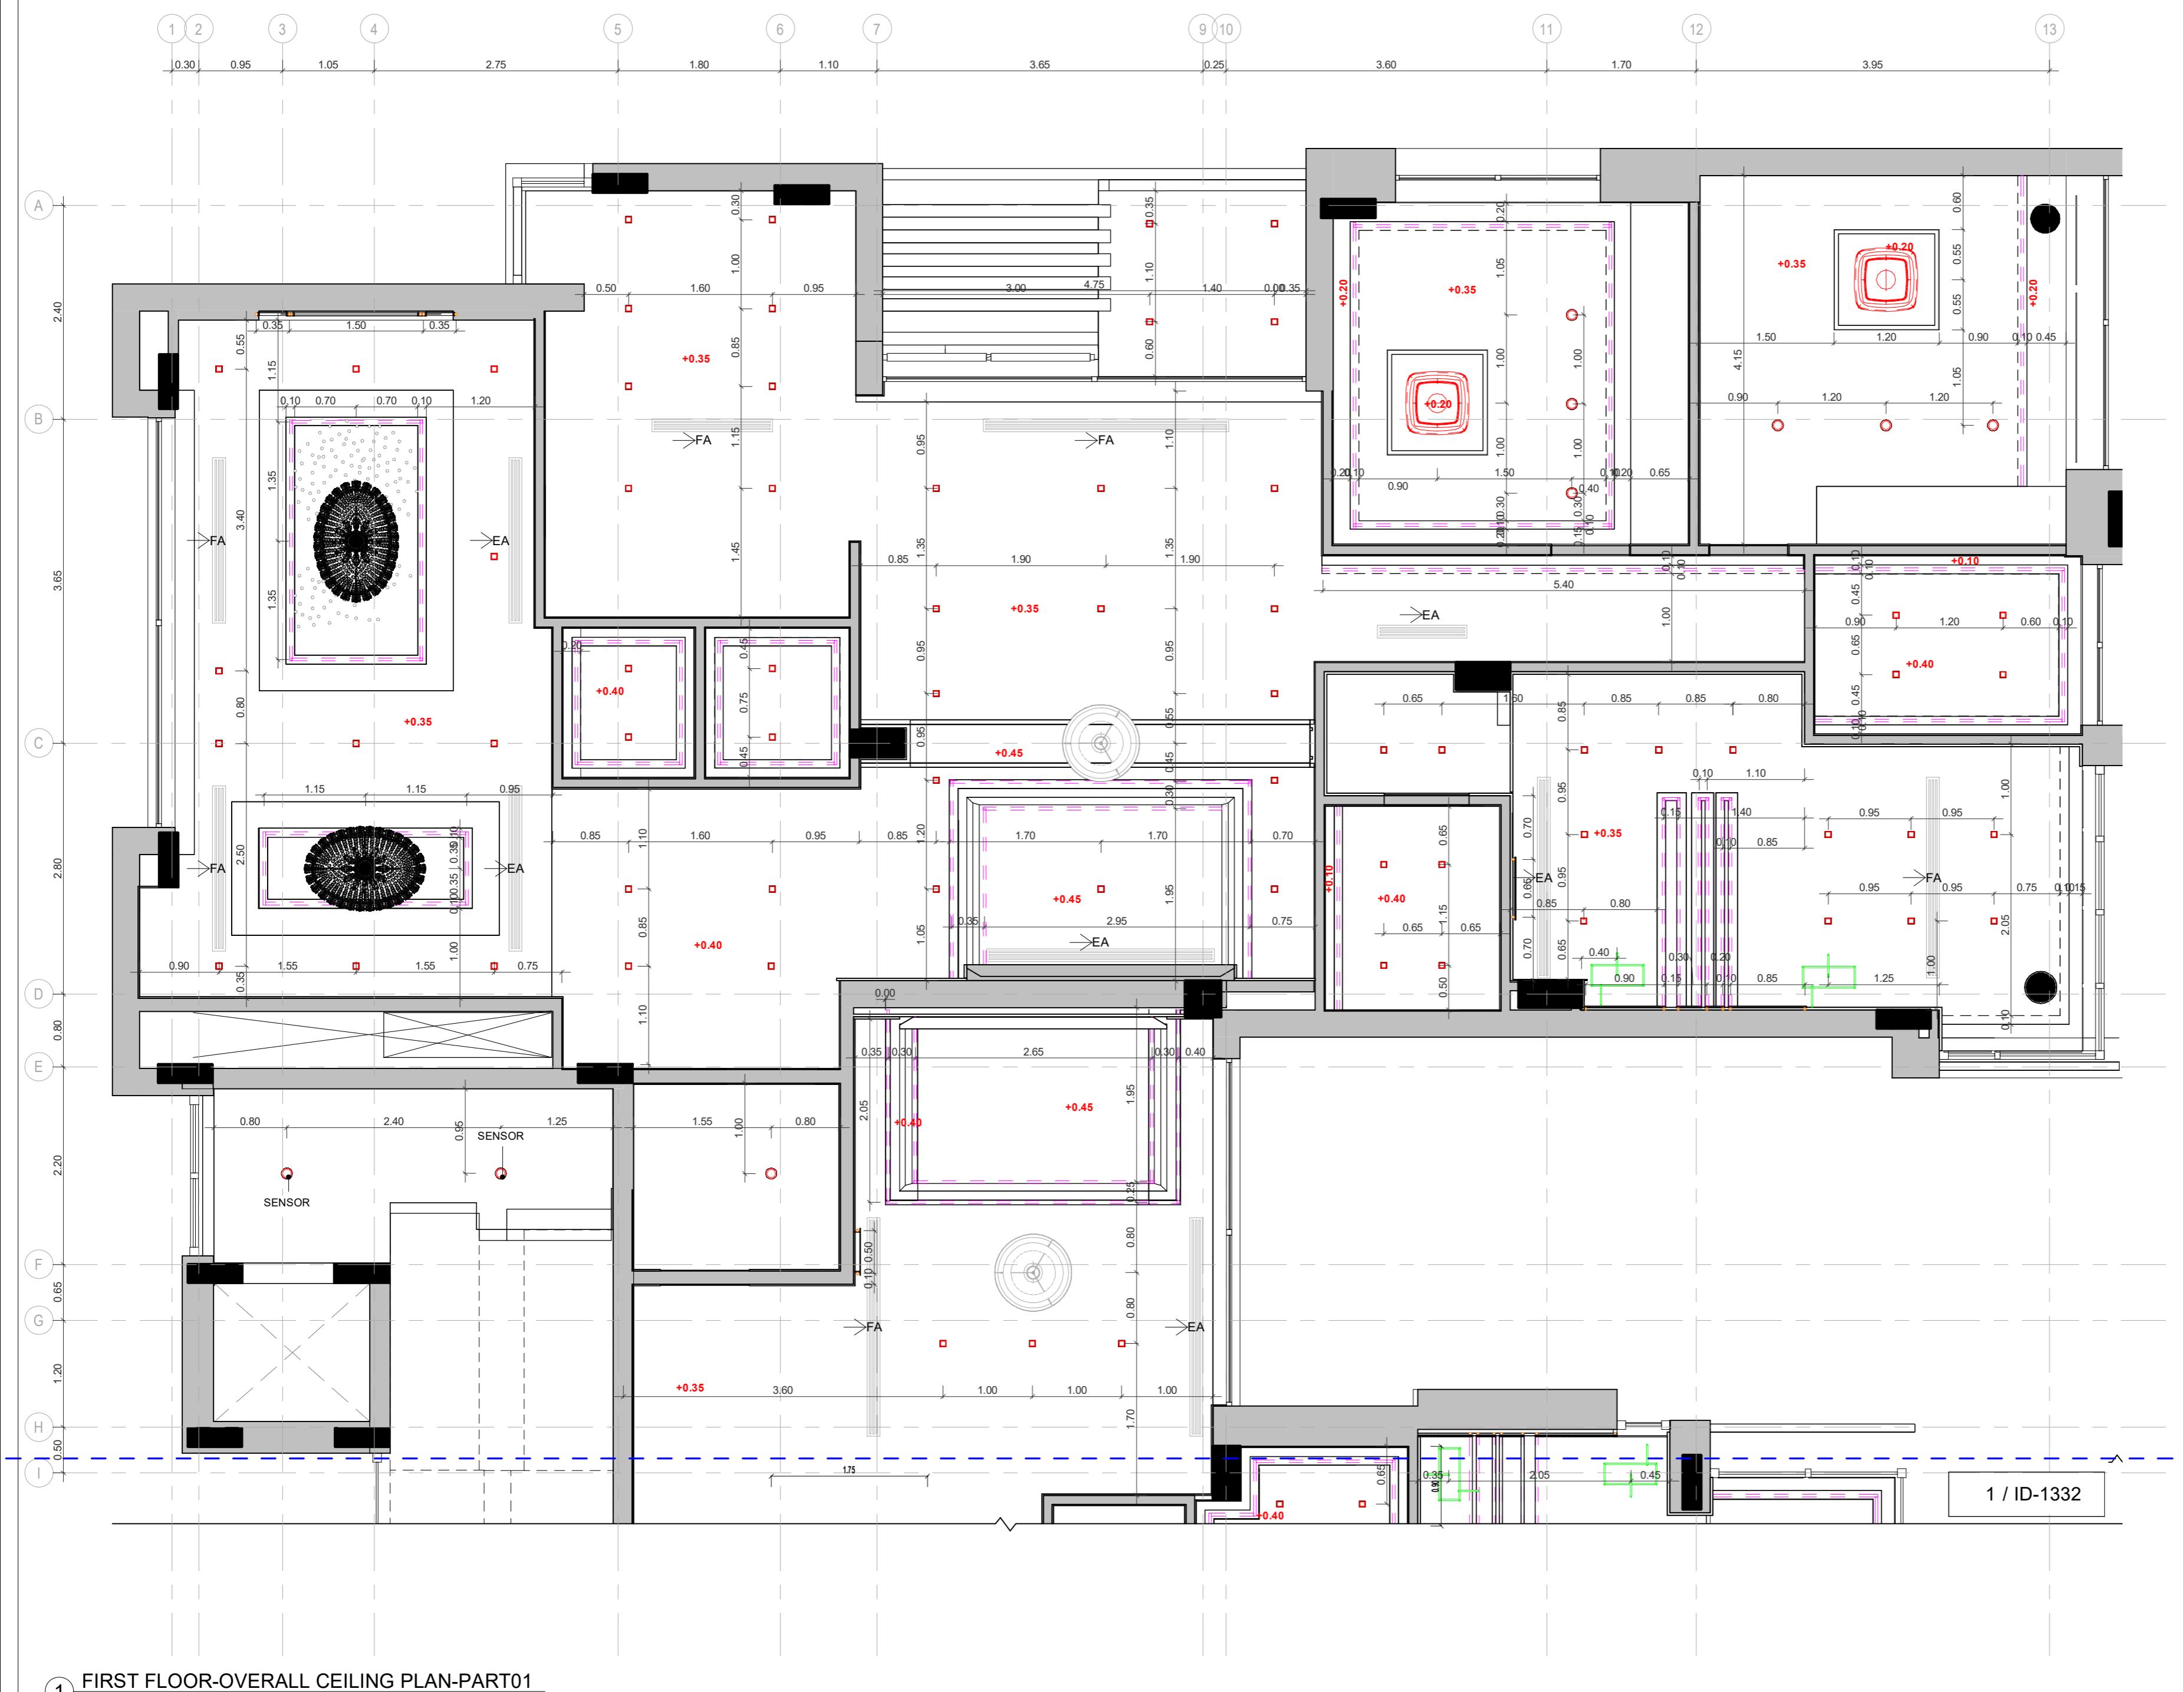

PROJECT NAME

APARTMENTS BUILDING

NOTES

FOR FINISHES REFER TO SHEETS:
ID-6000
ID-6001

- SPOT RECESSED LIGHT
- PENDANT LIGHT
- HIDDEN LIGHT
- CHANDELIER
- WALL MOUNTED
- NEON RECTANGULAR


Project Type	Residential
Owner	Khalid Khadir Hasan AL-Saeed
Location	Amman
Plot No.	1659
Basin No.	19
Designed by	A.Shaker Khulief 4809

SHEET NAME
FIRST FLOOR-OVERALL CEILING PLAN-PART02

ID-1332

Date 07/13/19

Scale 1 : 50

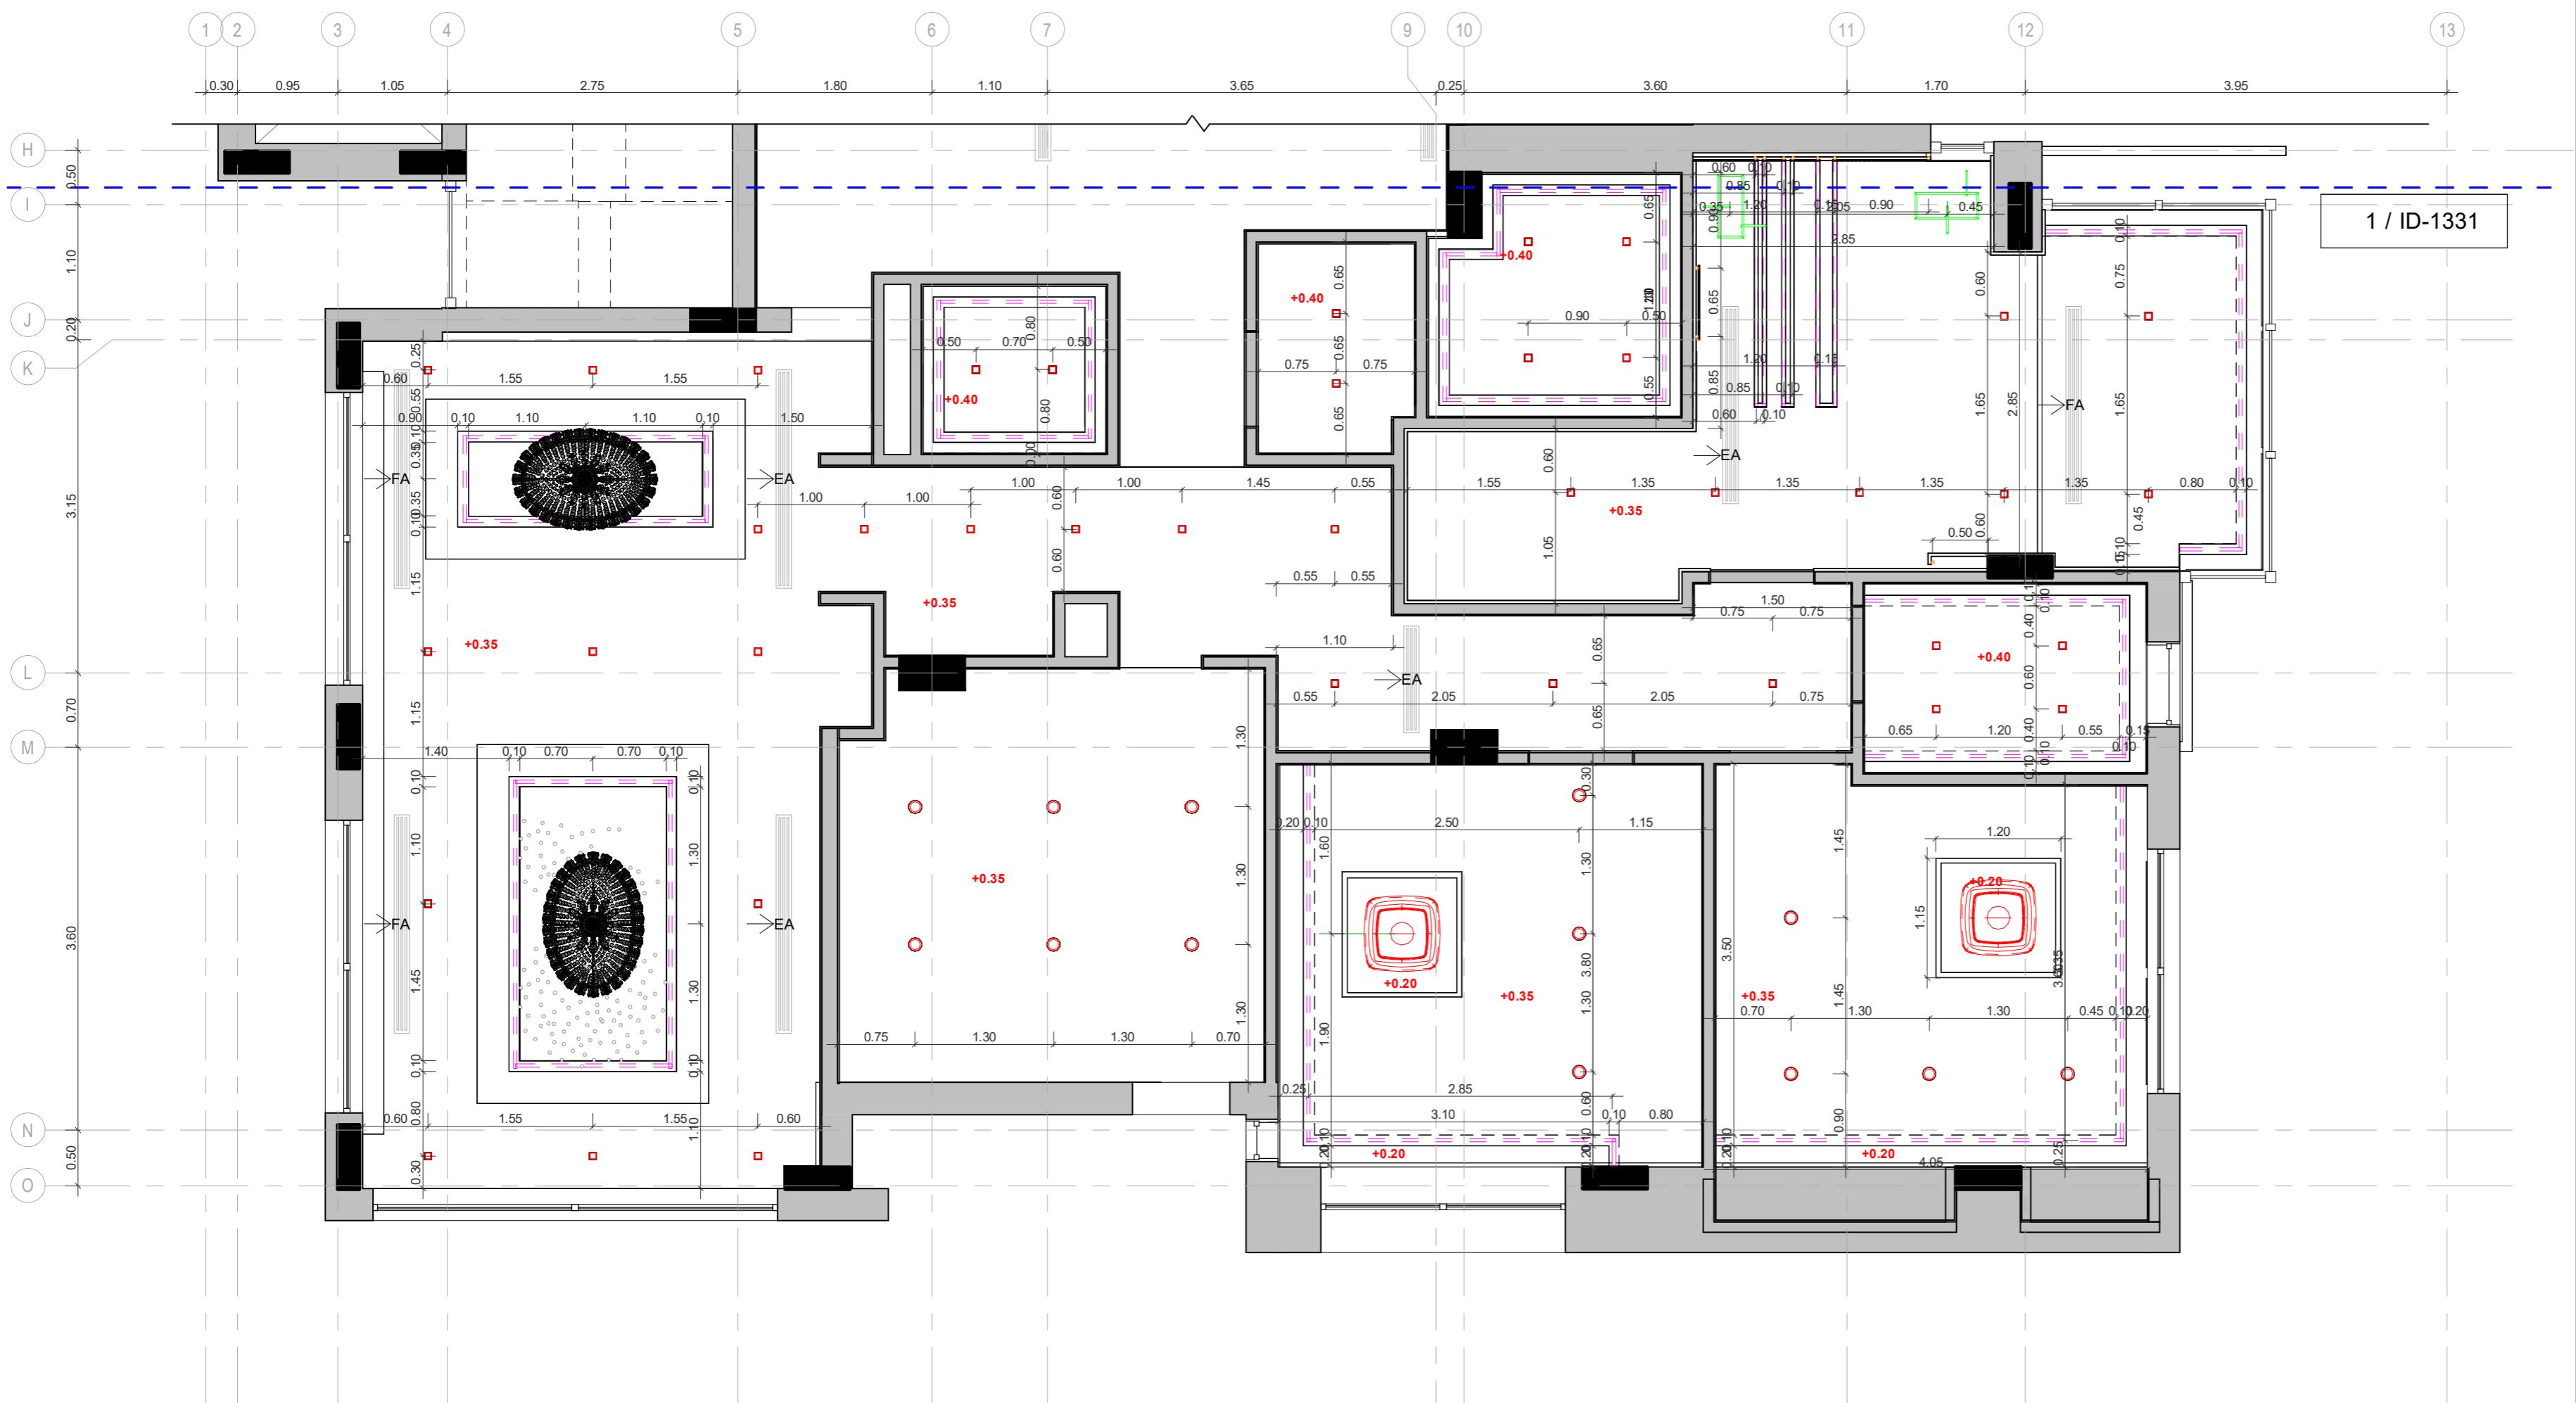

PROJECT NAME

APARTMENTS BUILDING

NOTES

FOR FINISHES REFER TO SHEETS:
ID-6000
ID-6001


- SPOT RECESSED LIGHT
- PENDANT LIGHT
- HIDDEN LIGHT
- CHANDELIER
- WALL MOUNTED
- NEON RECTANGULAR

Project Type	Residential
Owner	Khalid Khadir Hasan AL-Saeed
Location	Amman
Plot No.	1659
Basin No.	19
Designed by	A.Shaker Khulief 4809

SHEET NAME
ROOF FLOOR-OVERALL CEILING PLAN

ID-1340

Date 05/20/19
Scale 1 : 50

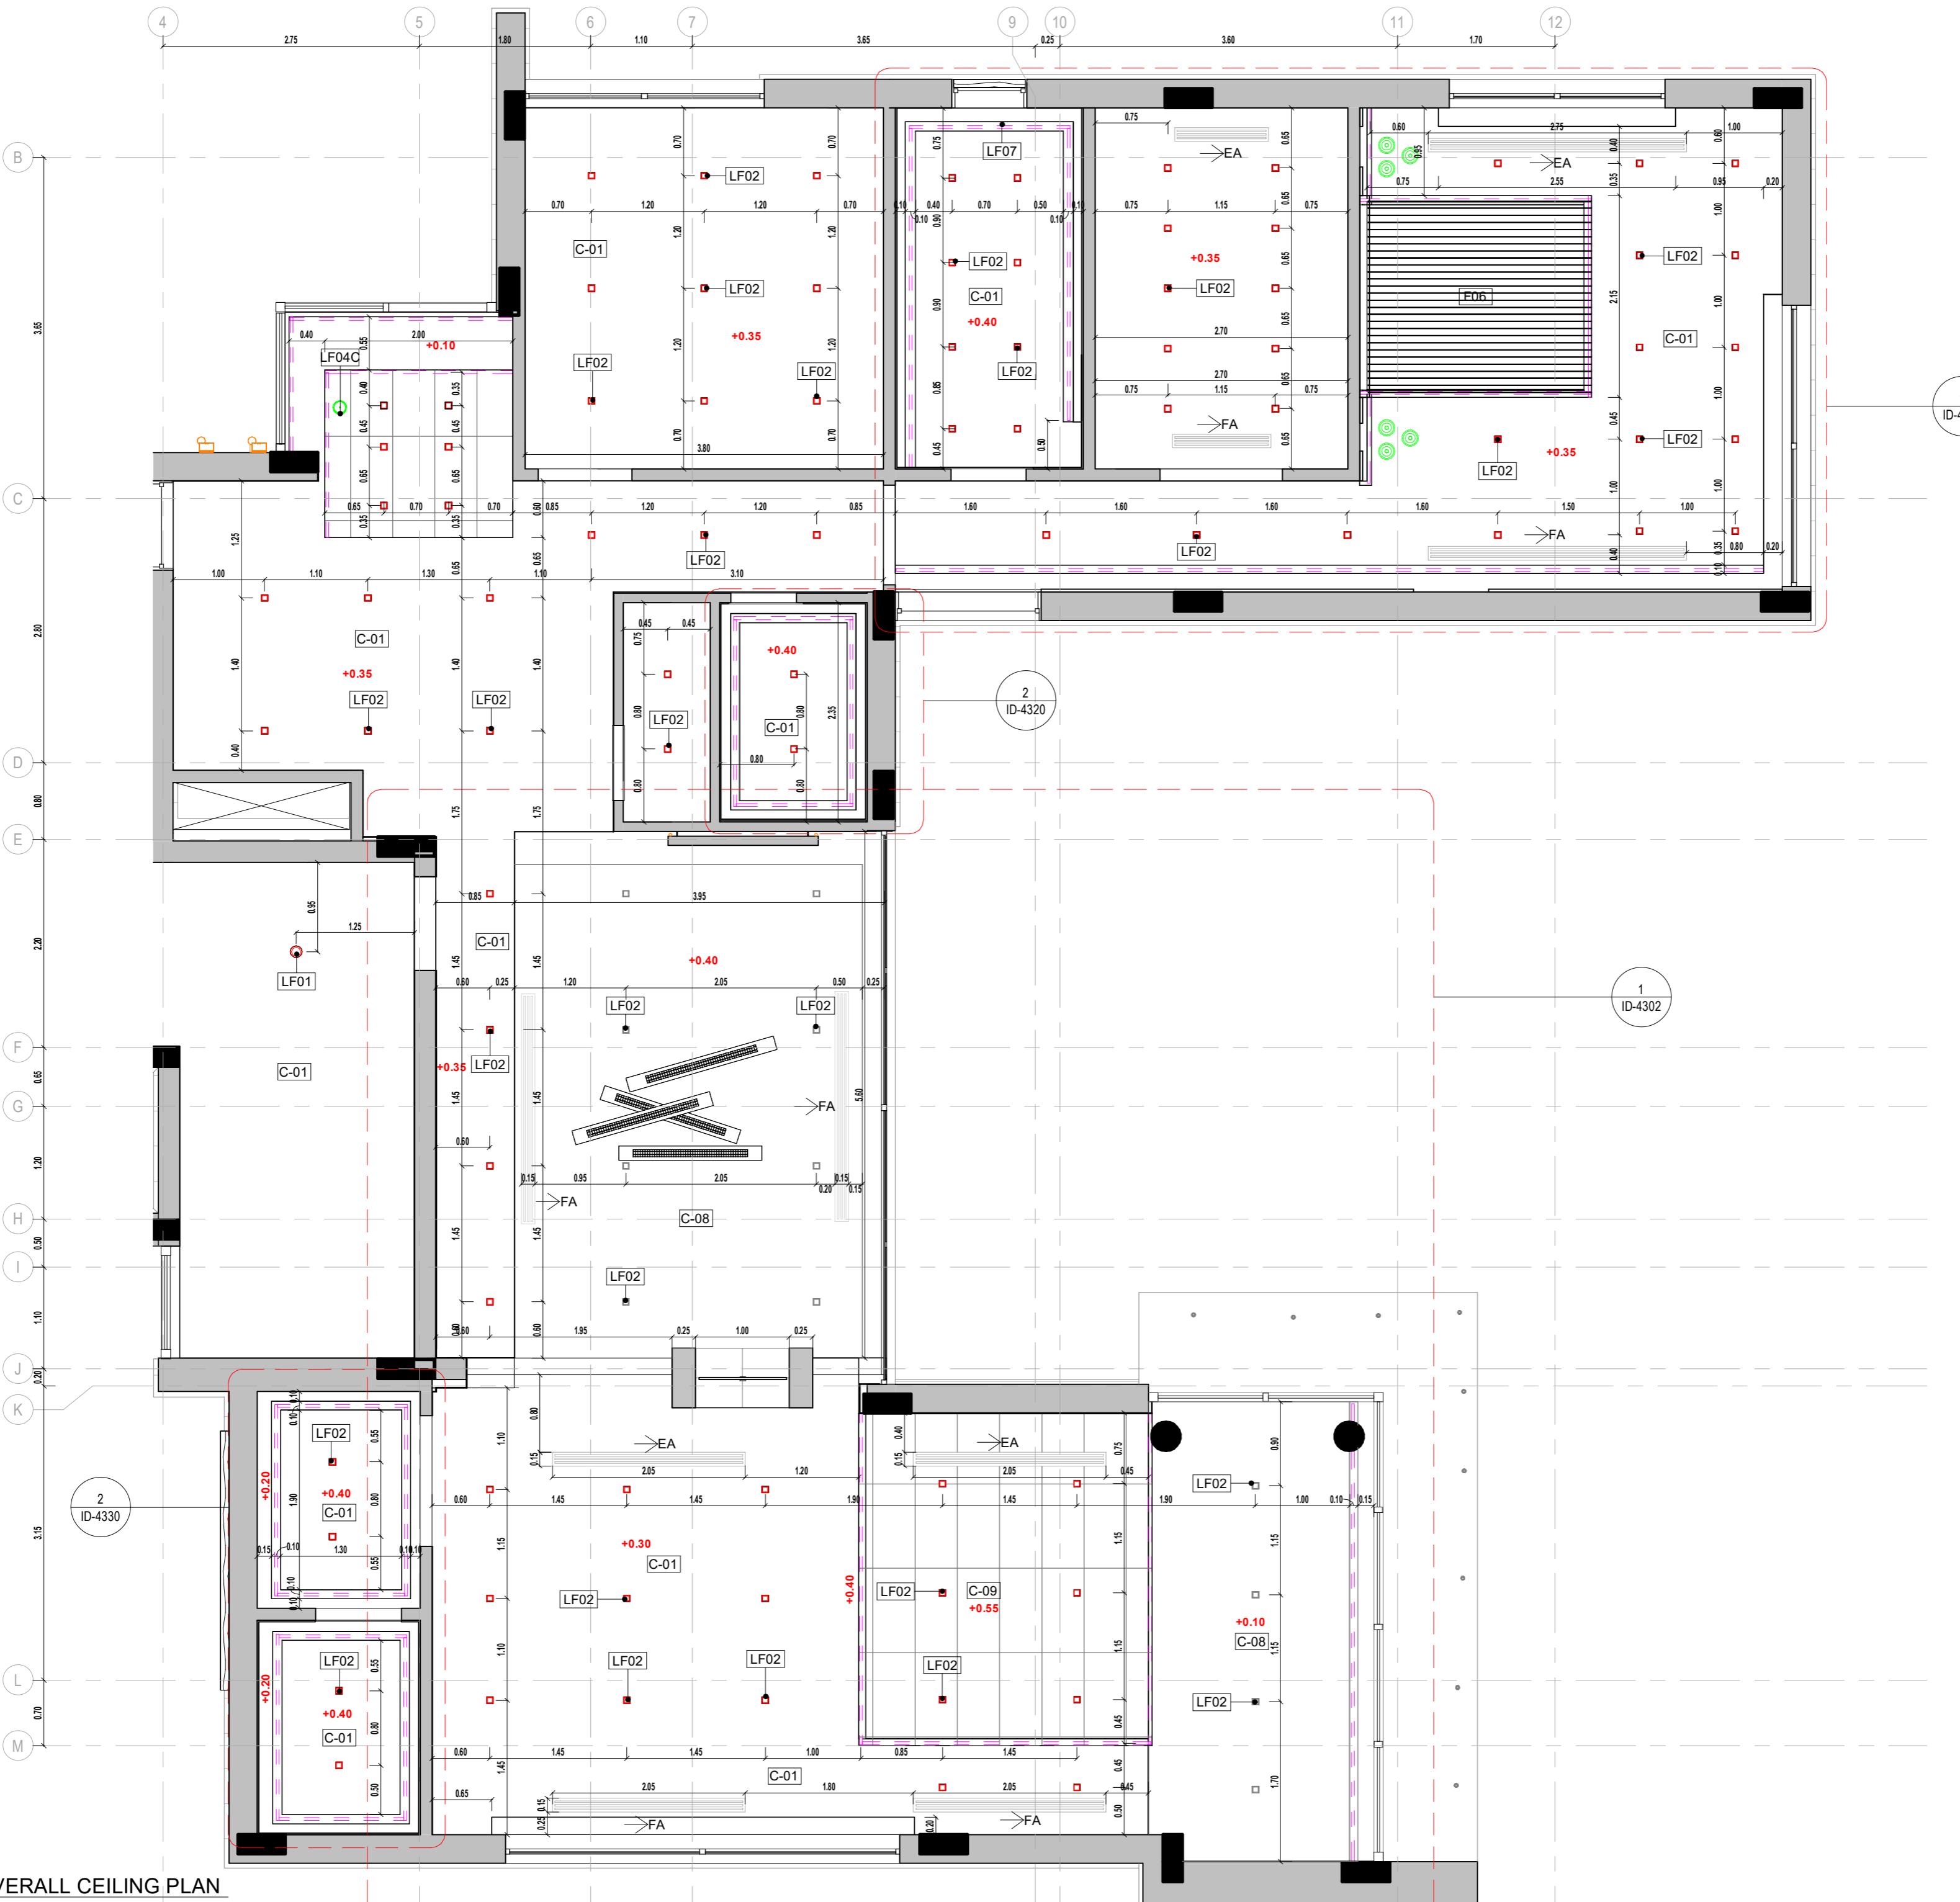



PROJECT NAME

APARTMENTS BUILDING

NOTES

FOR FINISHES REFER TO SHEETS:
ID-6000
ID-6001

Project Type	Residential
Owner	Khalid Khadir Hasan AL-Saeed
Location	Amman
Plot No.	1659
Basin No.	19
Designed by	A.Shaker Khulief 4809

SHEET NAME
LIVING ROOM- SHOTS

ID-4000

Date	10/08/19
Scale	

PROJECT NAME

APARTMENTS BUILDING

NOTES

FOR FINISHES REFER TO SHEETS:
ID-6000
ID-6001



FINISHES SCHEDULE	
Material: Mark	DESCRIPTION
F01	WHITE PAINT
F02	GOLD WOOD
F03	TRAVERTINO MARBLE
F04	GOLD STONE
F05	DARK WOOD
F06	DECORATIVE STONE
F07	PAINT GOLD METAL EFFECT
F08	WOOD
F09	BLACK MARBLE
F10	BEIGE MARBLE
F11	GREY STONE
F12	CONCRETE FINISH
F13	KITCHENNE WOOD
F14	WALL PAPER CALCATTA
F15	SWIMMING POOL MARBLE
F16	PARQUET
F17	CALCATTA
F18	WHITE FINISH GRC

SPOT RECESSED LIGHT
PENDANT LIGHT
HIDDEN LIGHT
CHANDELIER
WALL MOUNTED
NEON RECTANGULAR

Project Type	Residential
Owner	Khalid Khadir Hasan AL-Saeed
Location	Amman
Plot No.	1659
Basin No.	19
Designed by	A.Shaker Khulief 4809

SHEET NAME
BASEMENT FLOOR-LIVING ROOM

ID-4001
Date 08/10/2019
Scale 1 : 50

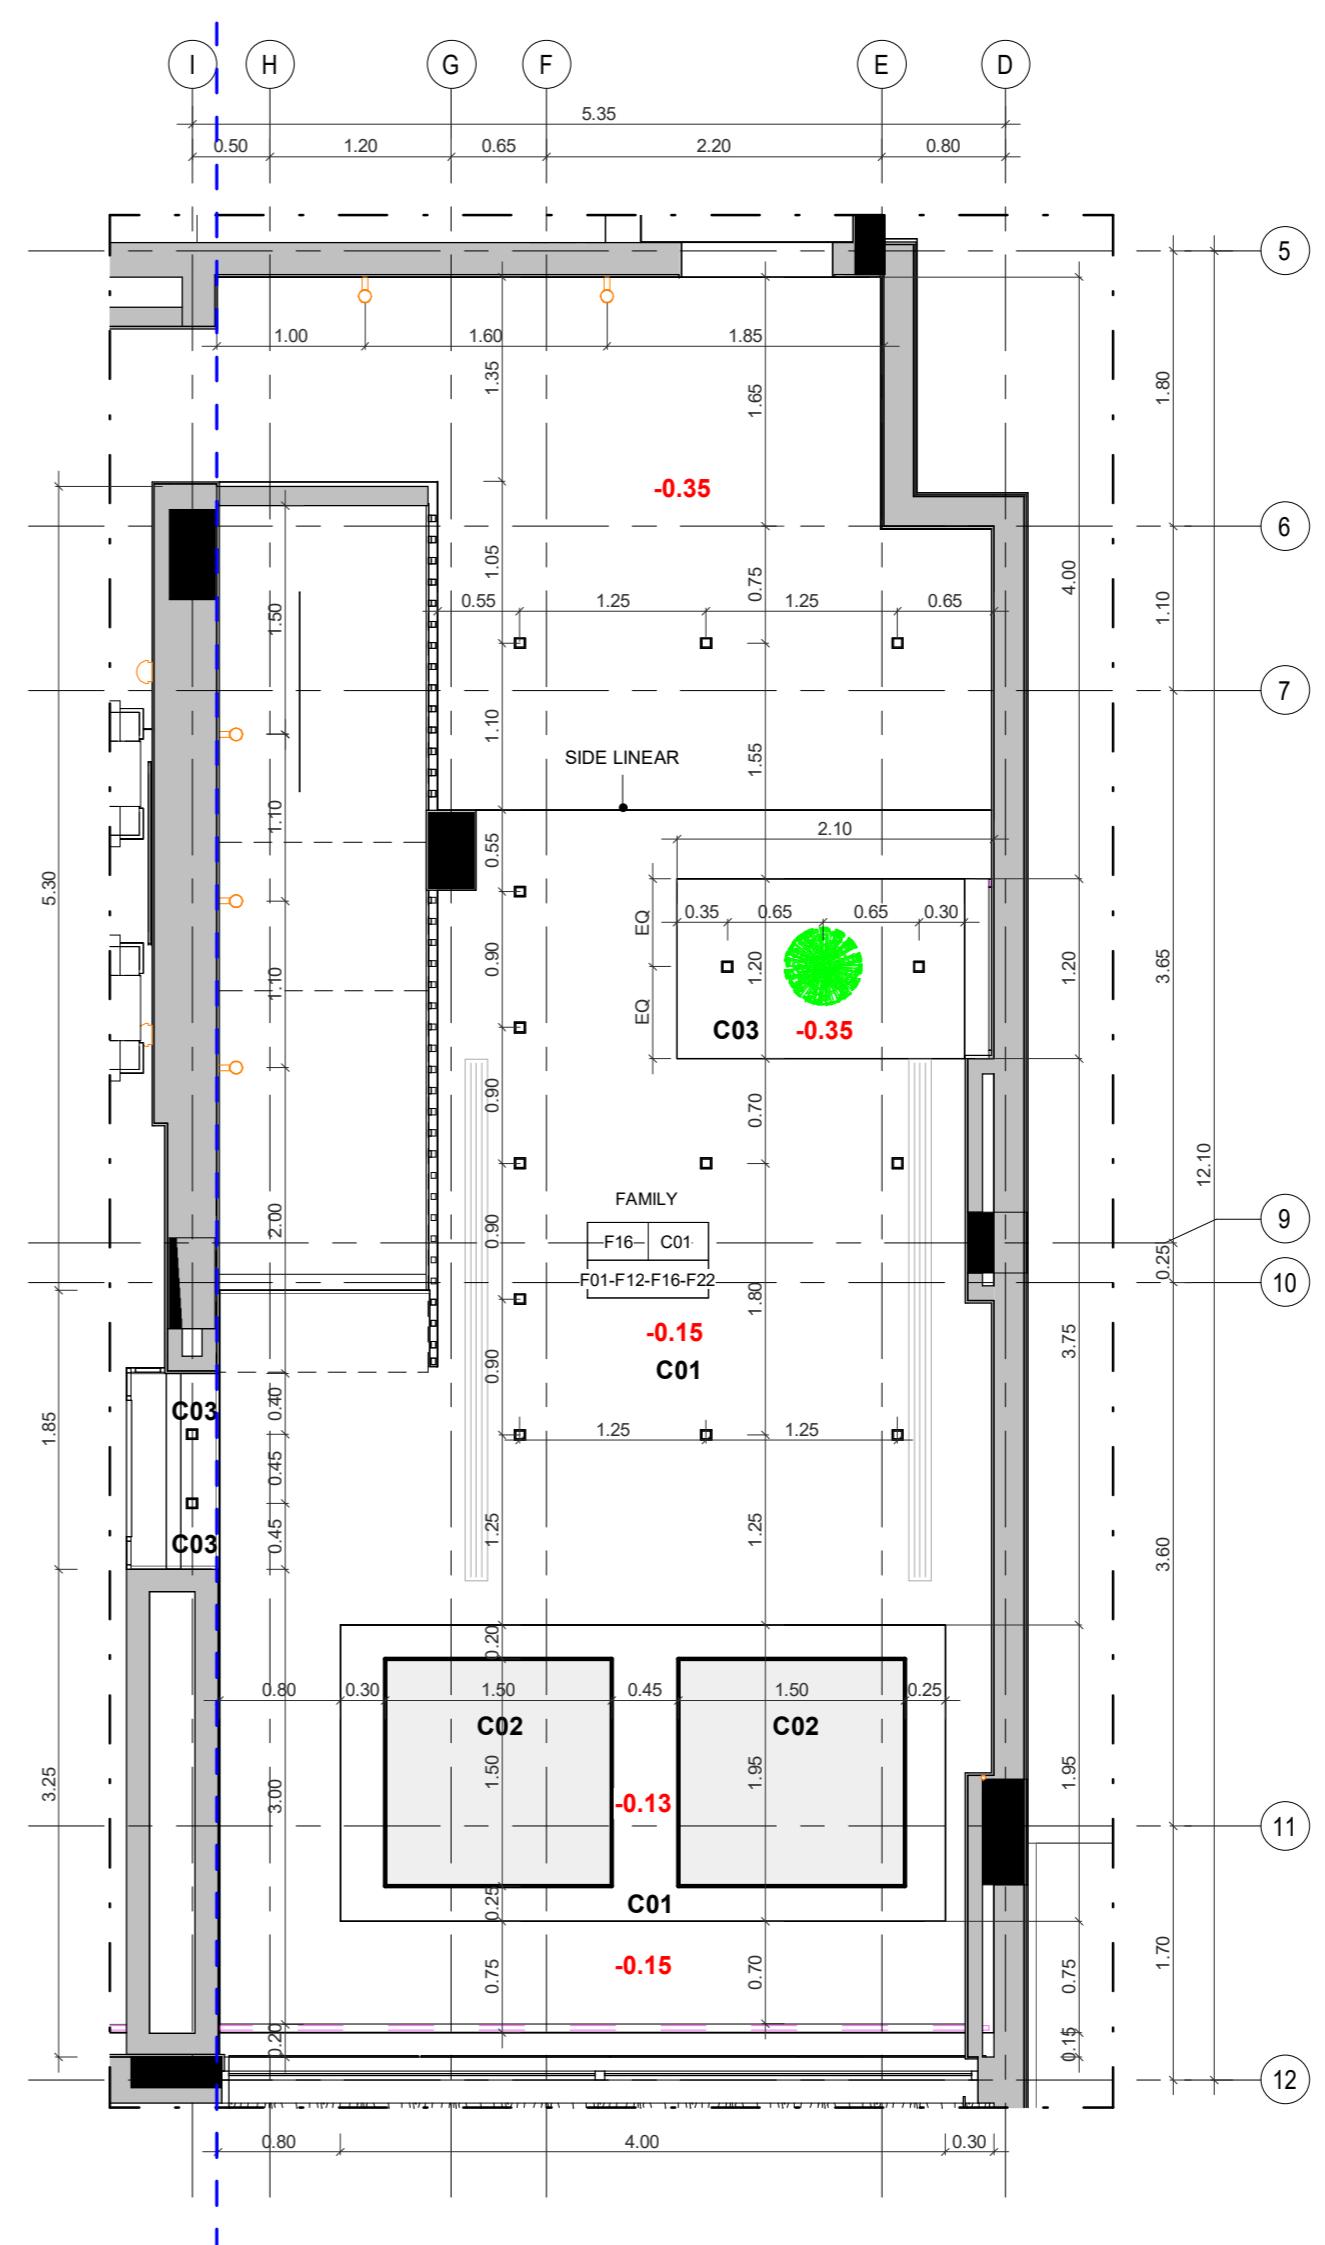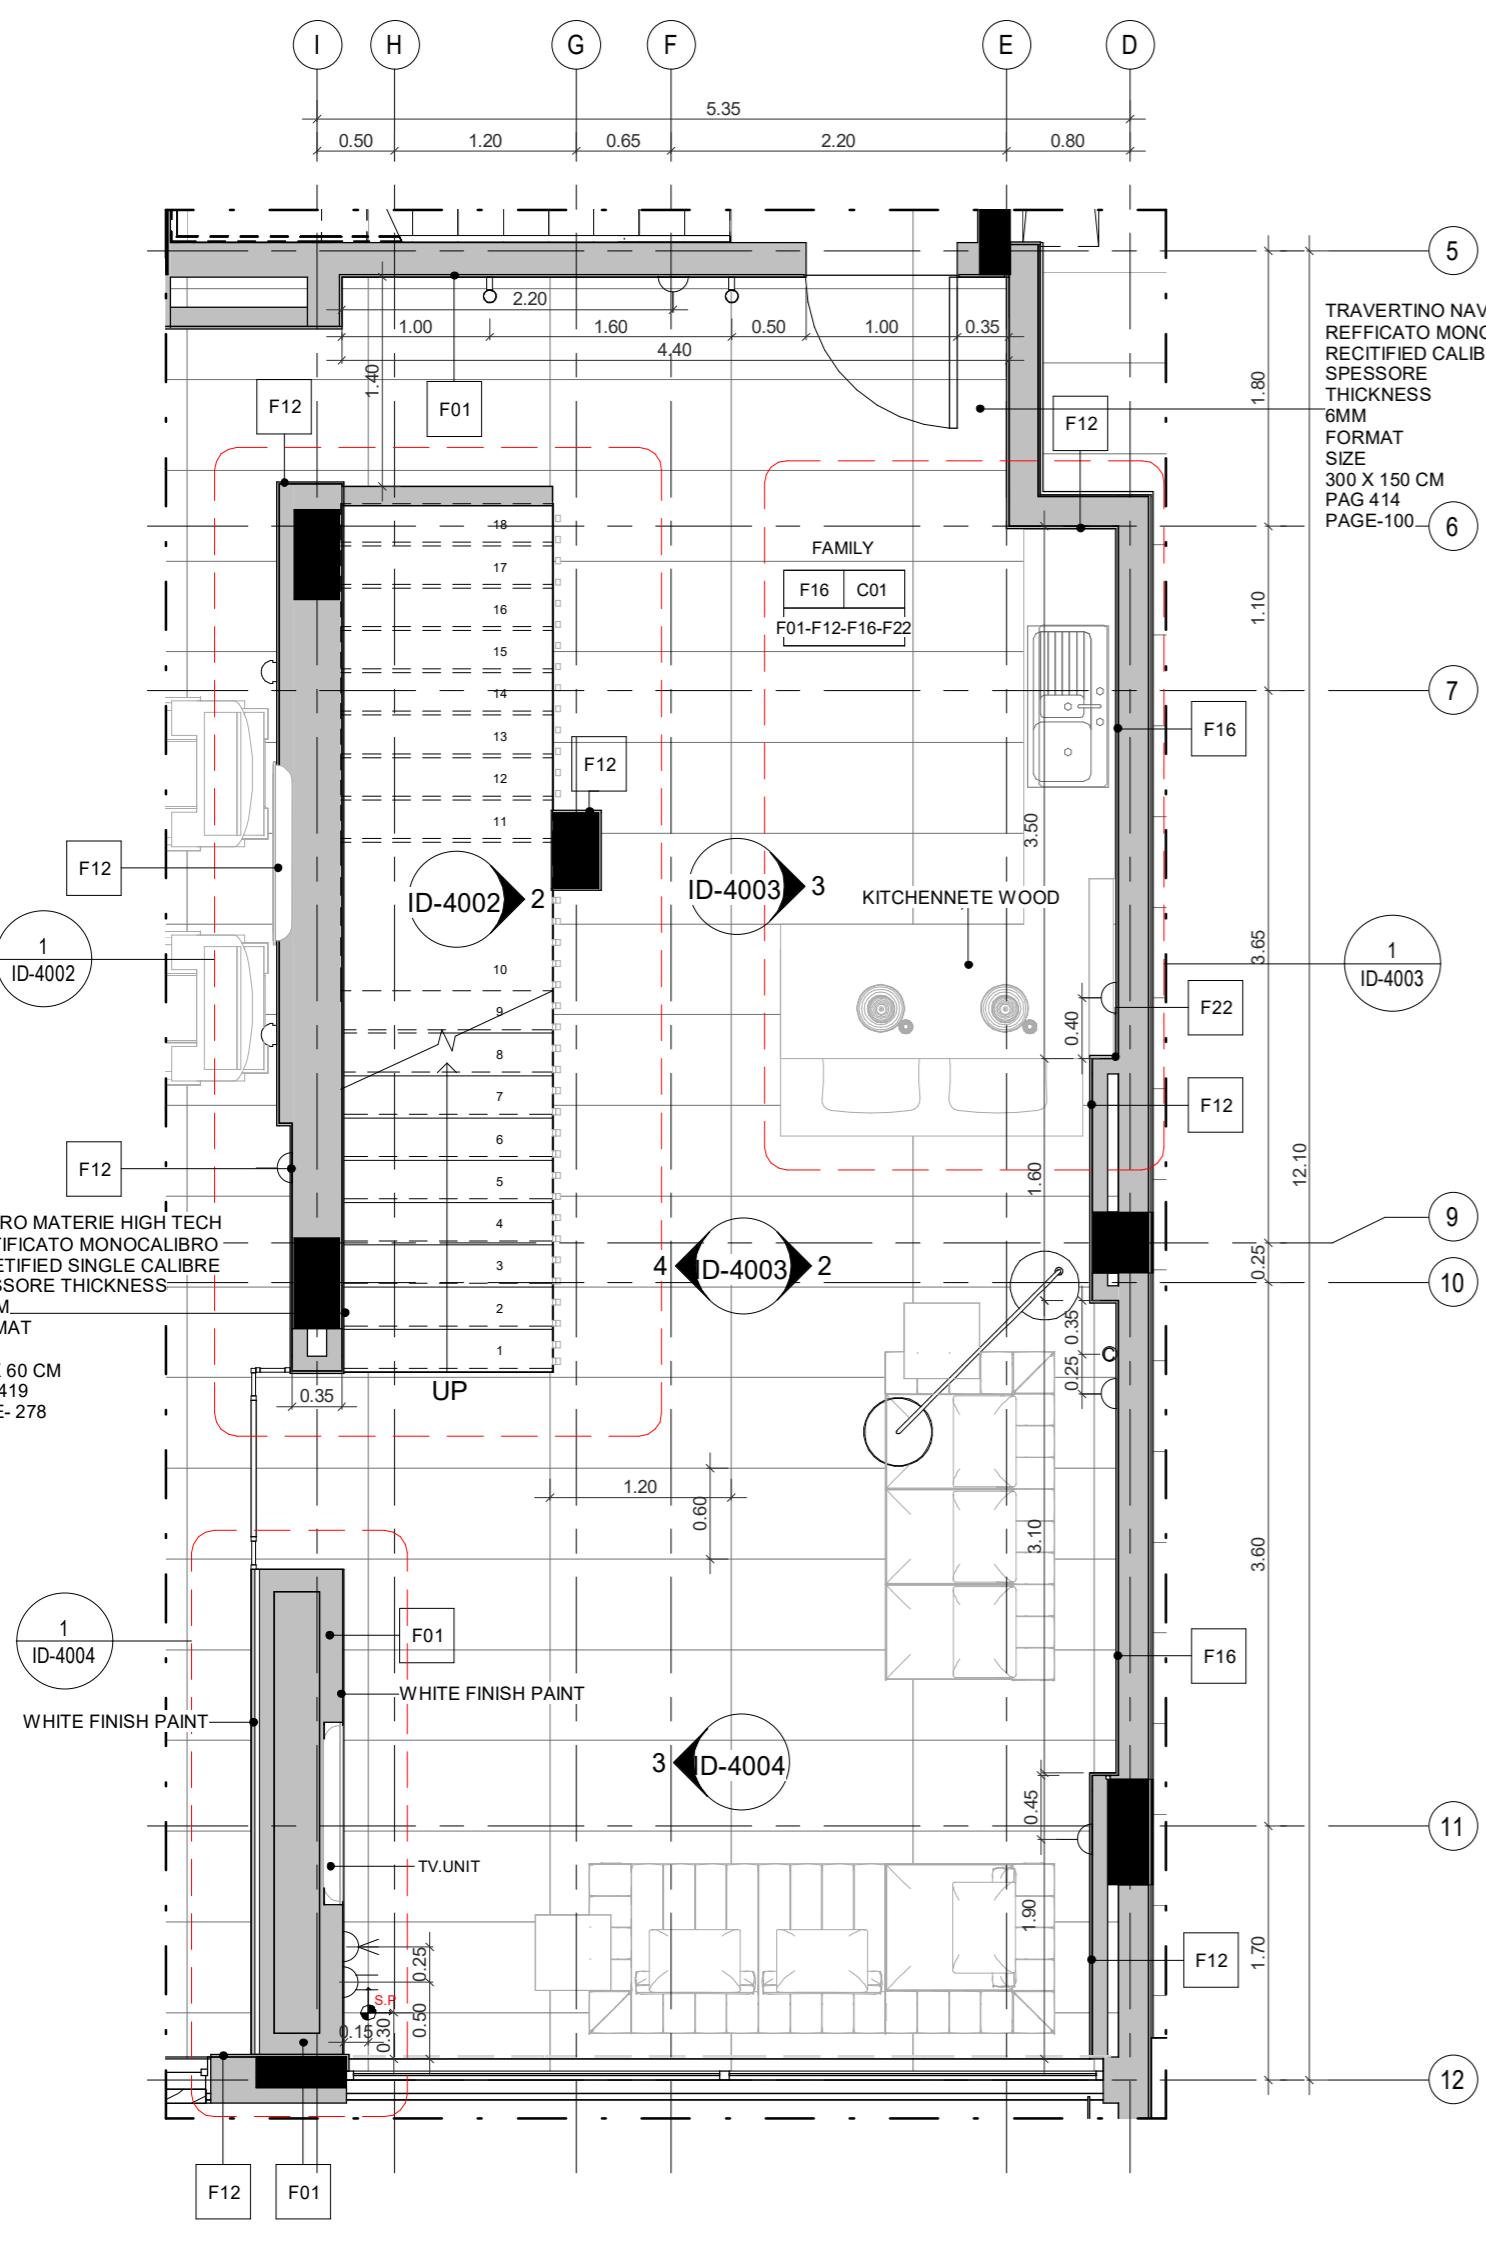

PROJECT NAME

APARTMENTS BUILDING

NOTES

FOR FINISHES REFER TO SHEETS:
ID-6000
ID-6001


FINISHES SCHEDULE		FINISHES SCHEDULE			
Material:	Mark	DESCRIPTION	Material:	Mark	DESCRIPTION
F01		WHITE PAINT	F15		BEIGE PAINT
F02		GOLD WOOD	F16		TRAVERTINO MARBLE
F03		GOLD STONE	F04		DARK WOOD
F05		DECORATIVE STONE	F17		LEATHER
F06		WOOD	F18		PAINT GOLD METAL EFFECT
F07		BLACK MARBLE	F19		DECORATIVE WOOD
F08		BEIGE MARBLE	F20		GREY STONE
F09		GREY STONE	F21		CONCRETE FINISH
F10		WALL PAPER	F22		KITCHENNETE WOOD
F11		CALCAGNA	F23		SWIMMING POOL WALL FINISH
F12		SWIMMING POOL MARBLE	F13		BLACK PAINT
F14		CALCAGNA	F24		PARQUET
F15		WHITE FINISH GRC	F25		WHITE FINISH GRC


Project Type	Residential
Owner	Khalid Khadir Hasan AL-Saeed
Location	Amman
Plot No.	1659
Basin No.	19
Designed by	A.Shaker Khulief 4809

SHEET NAME	
	BASEMENT FLOOR-LIVING ROOM

ID-4002


Date 08/10/2019
Scale As indicated

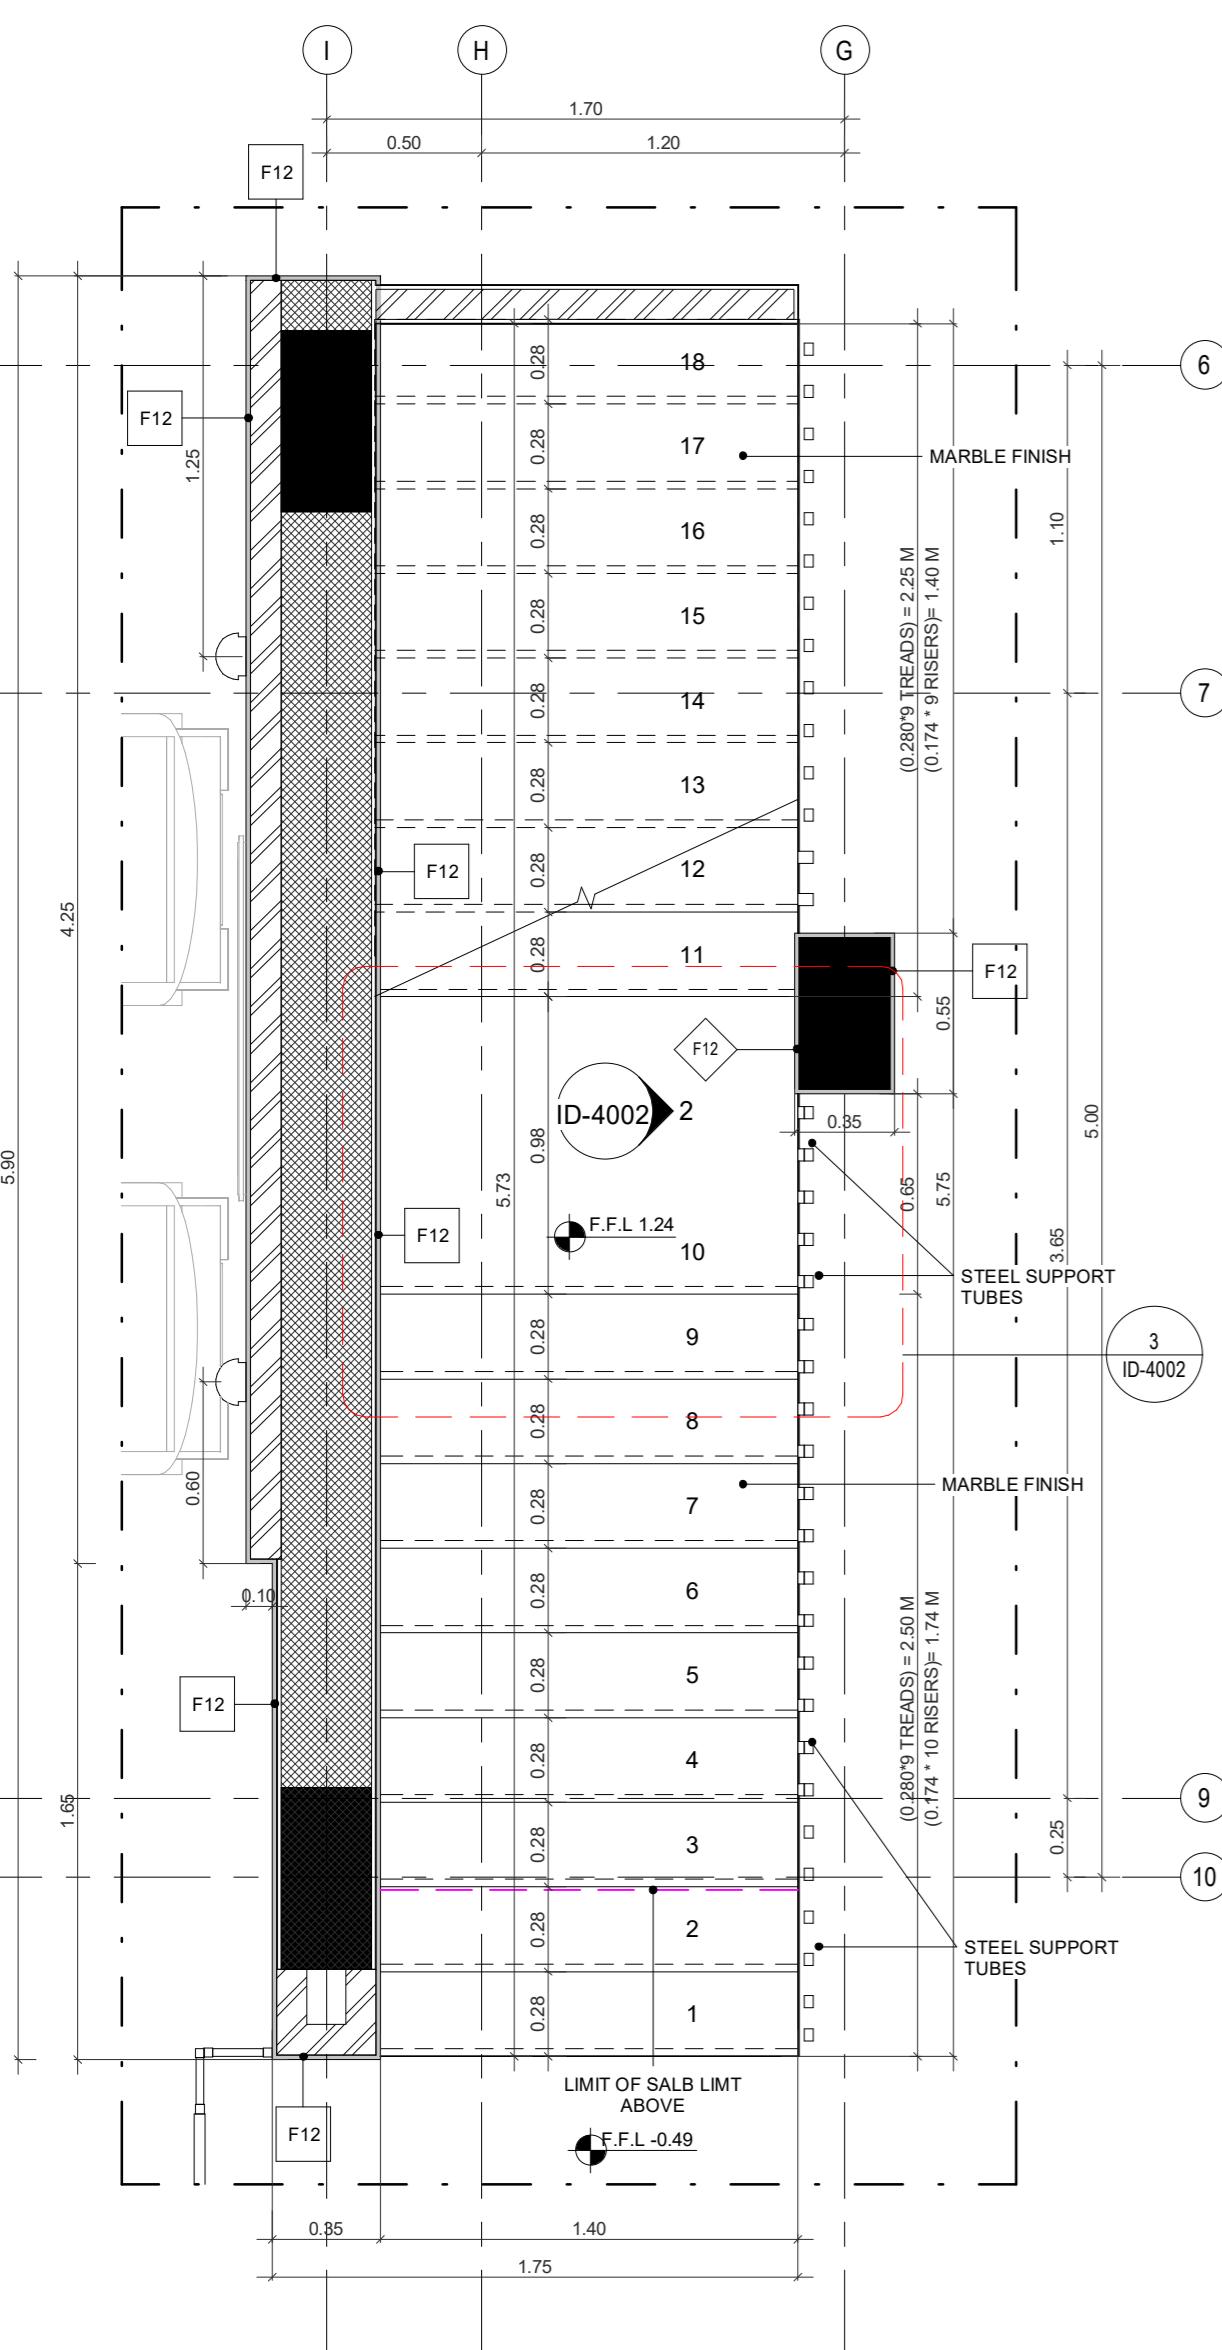

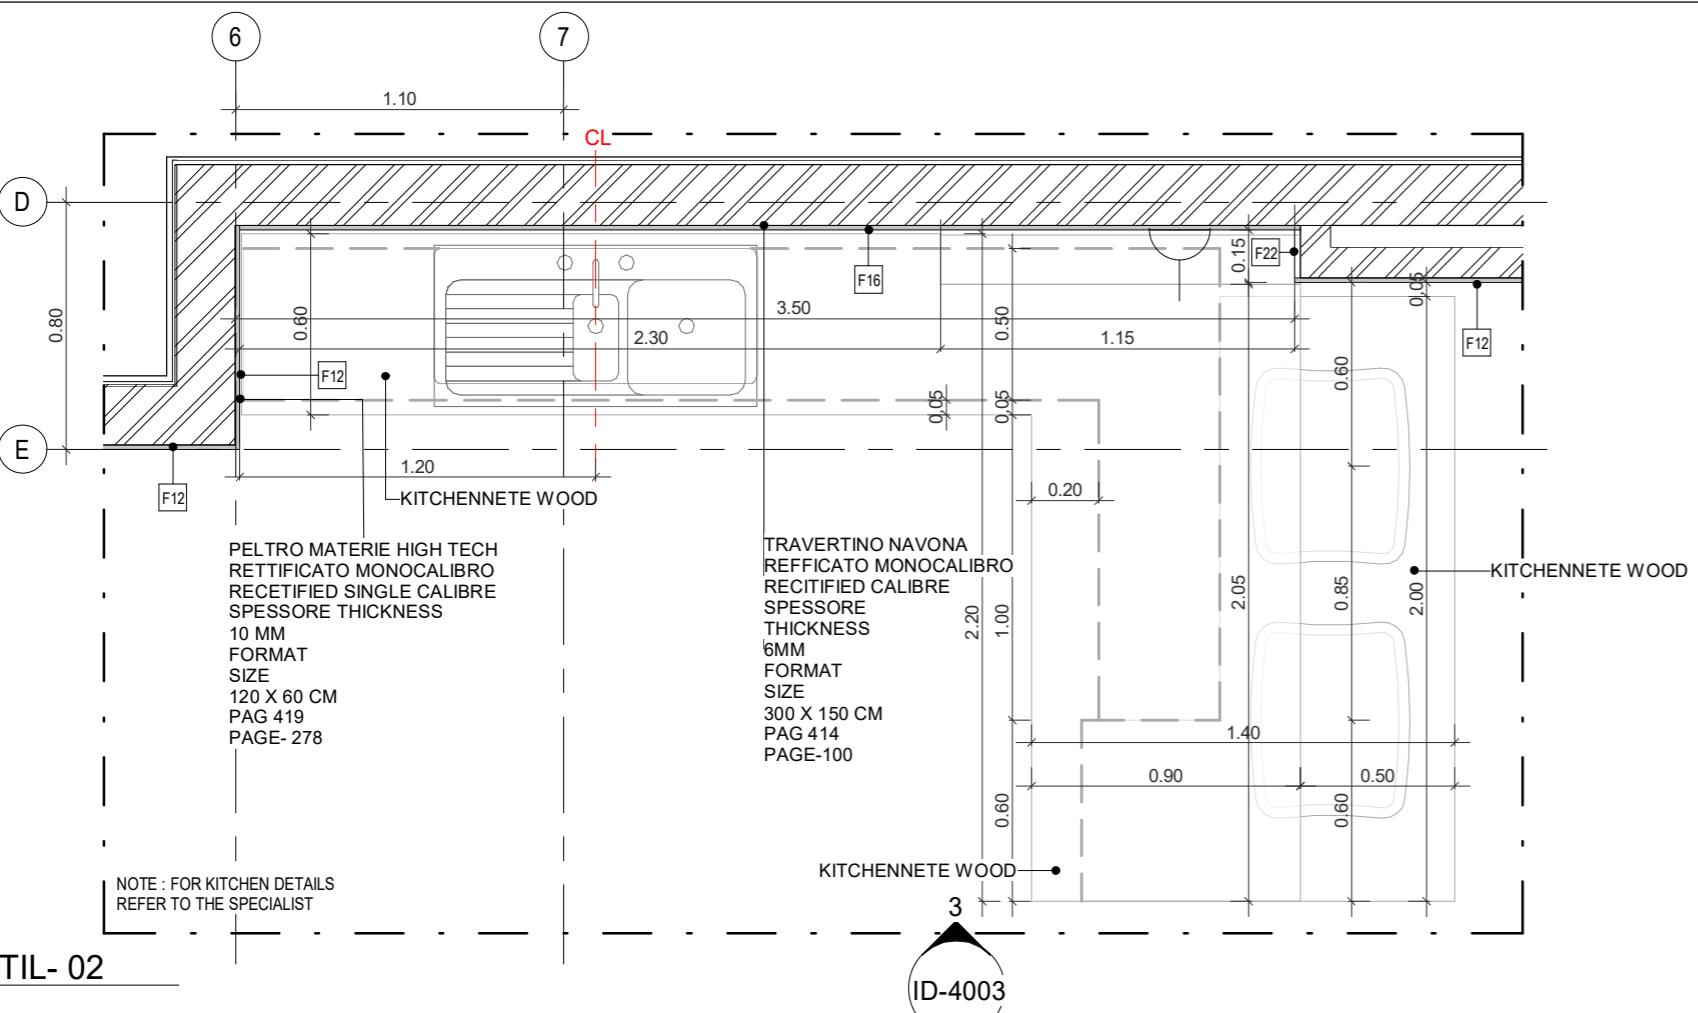


1 PLAN DEATIL- 02
1 : 25

1 : 25

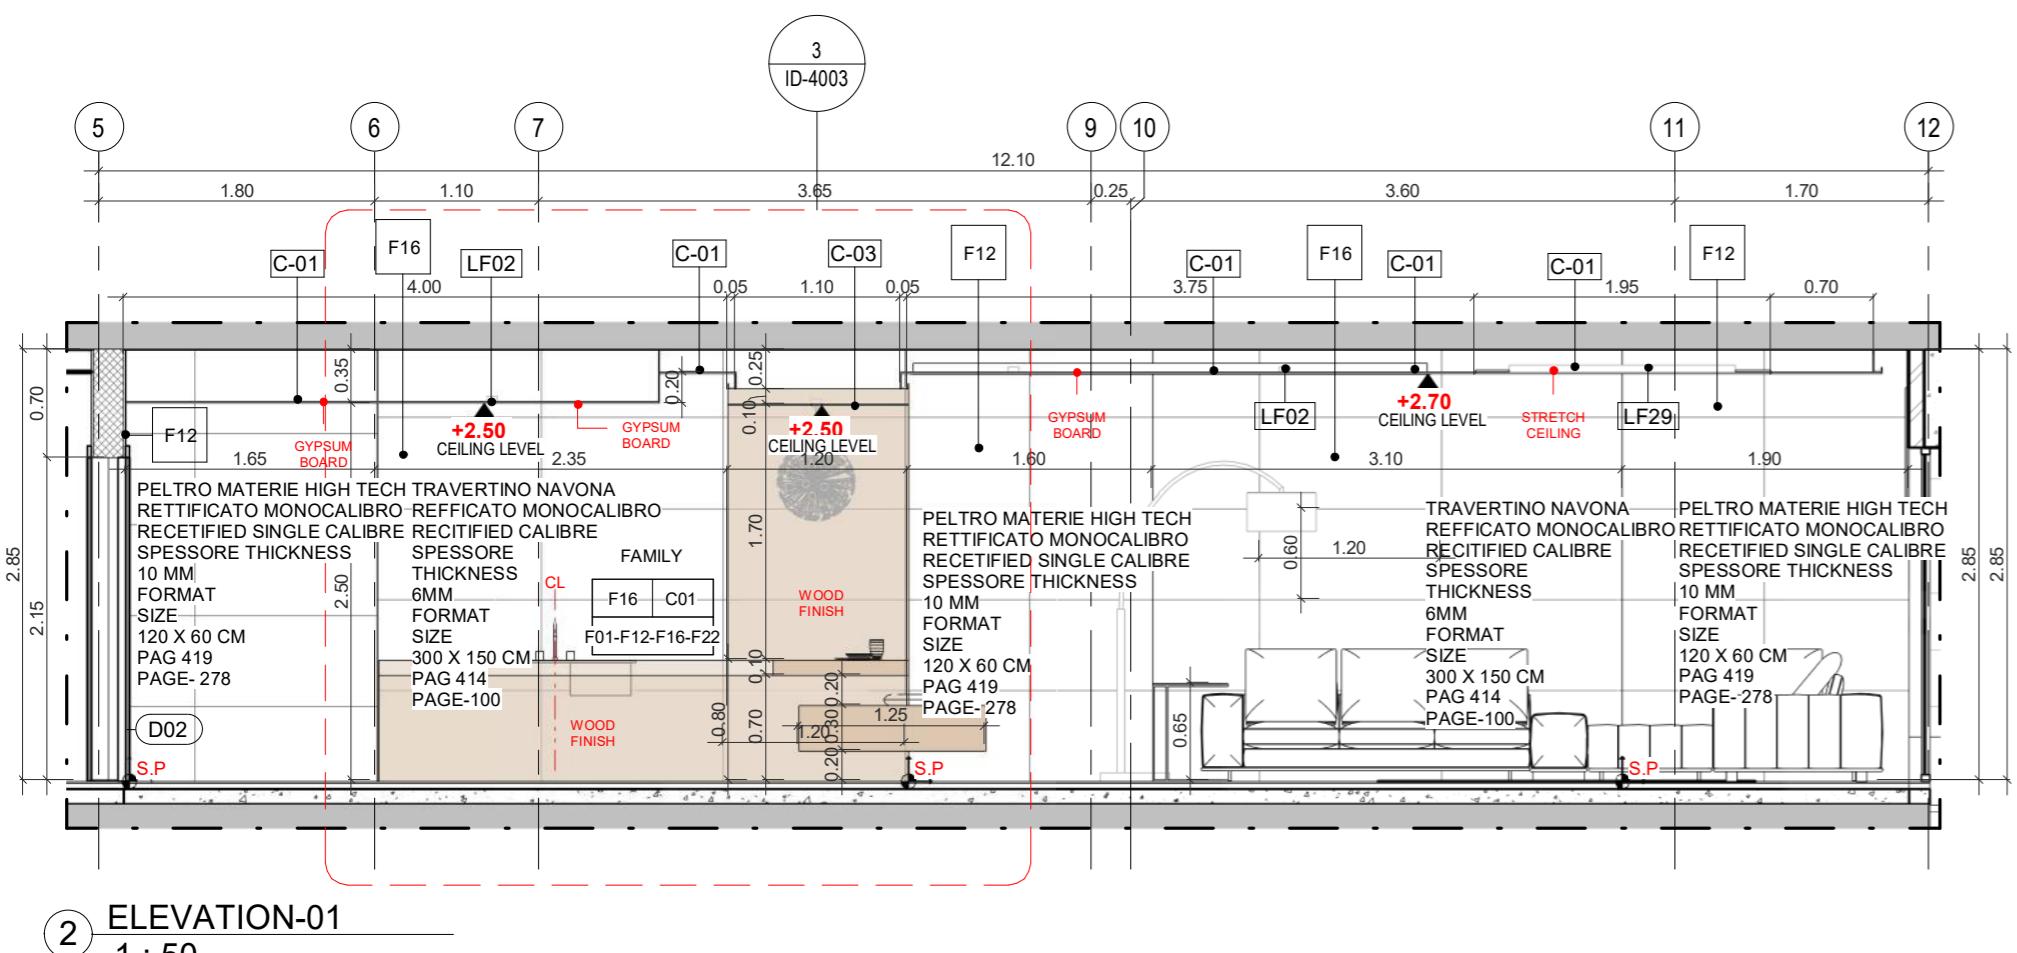


2 ELEVAT
1 : 50

1 : 5

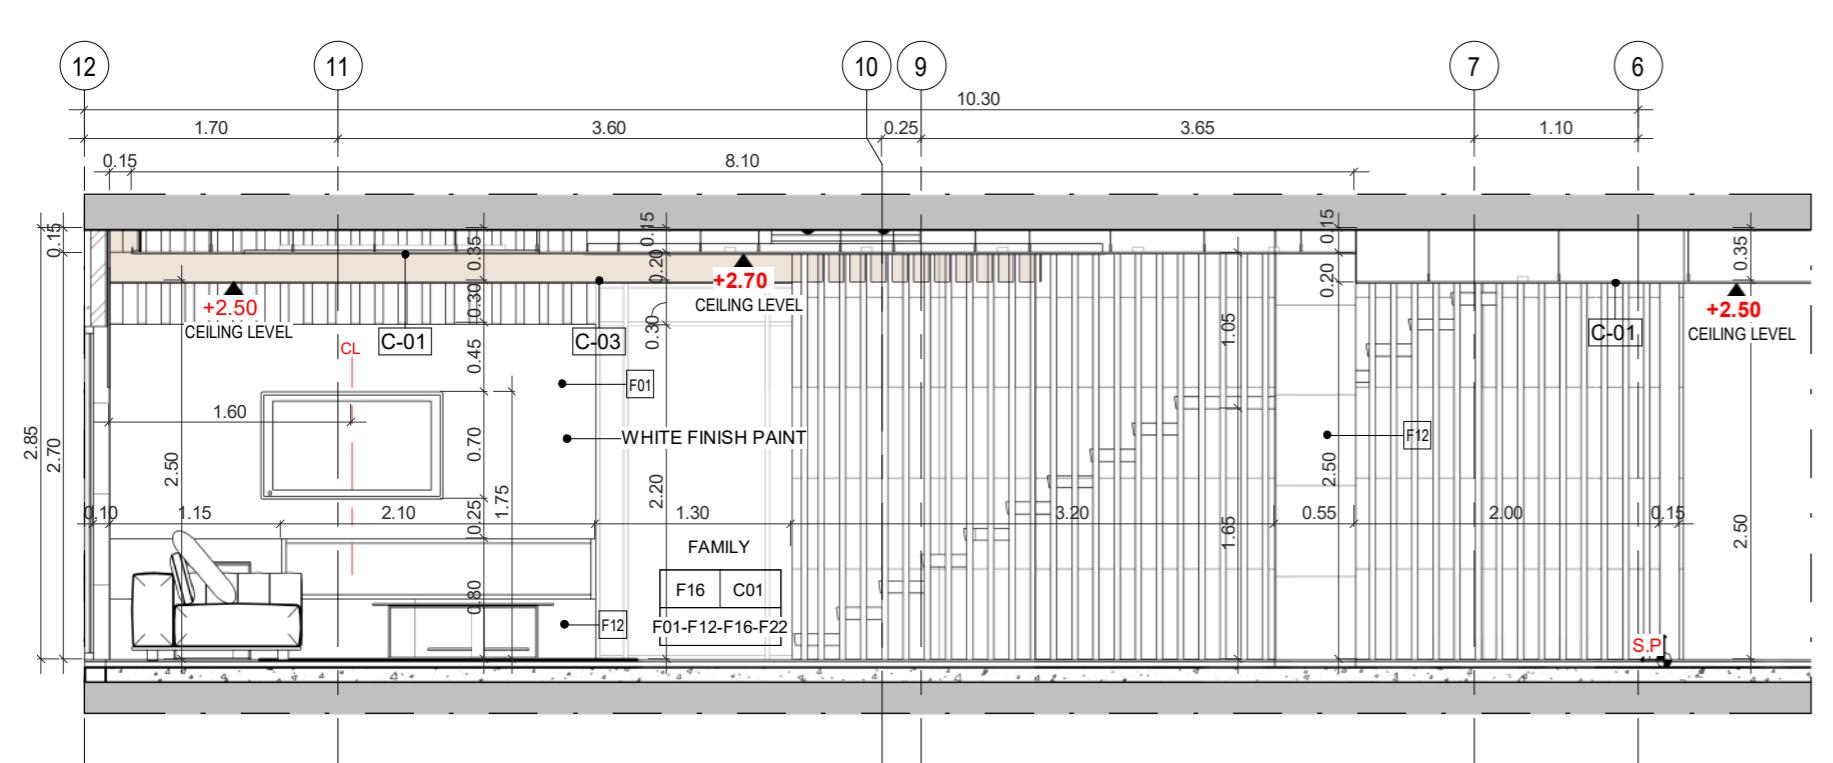


4 ELEVATION-03
1 : 50

4 1 : 50

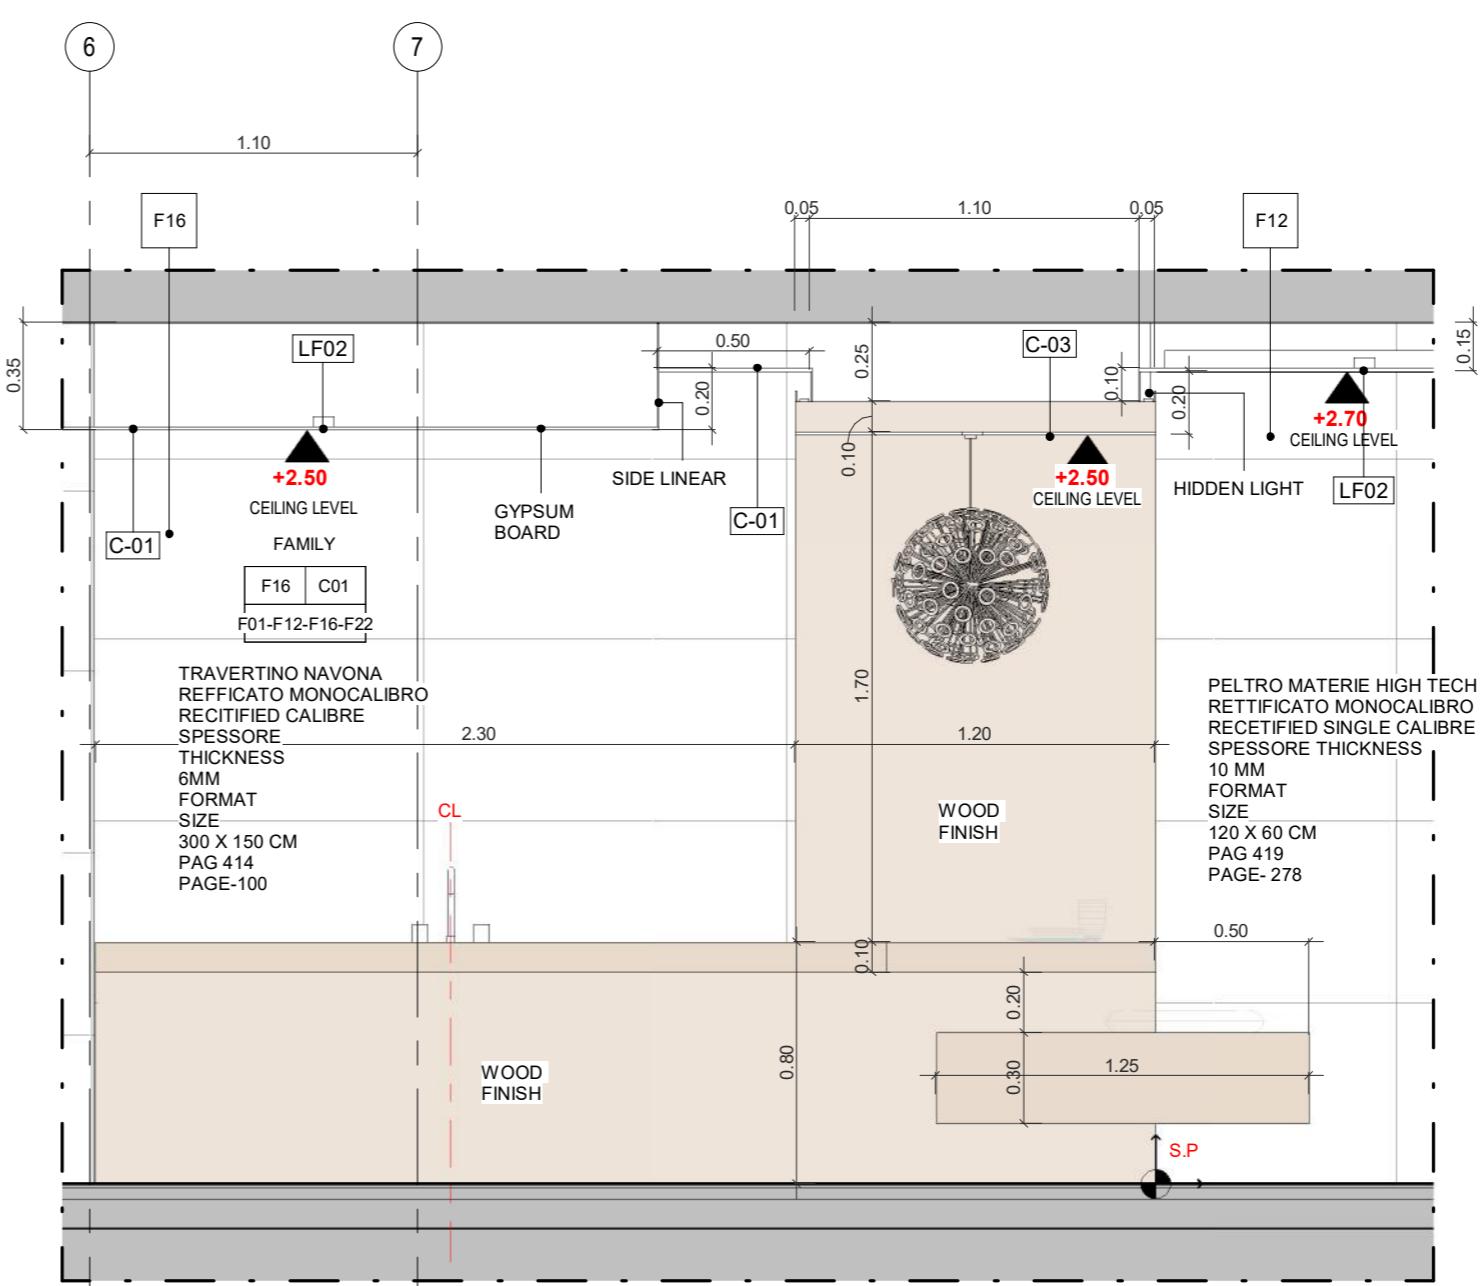

3 ELEVATION DETAIL-01
1 : 25

3 1 : 25

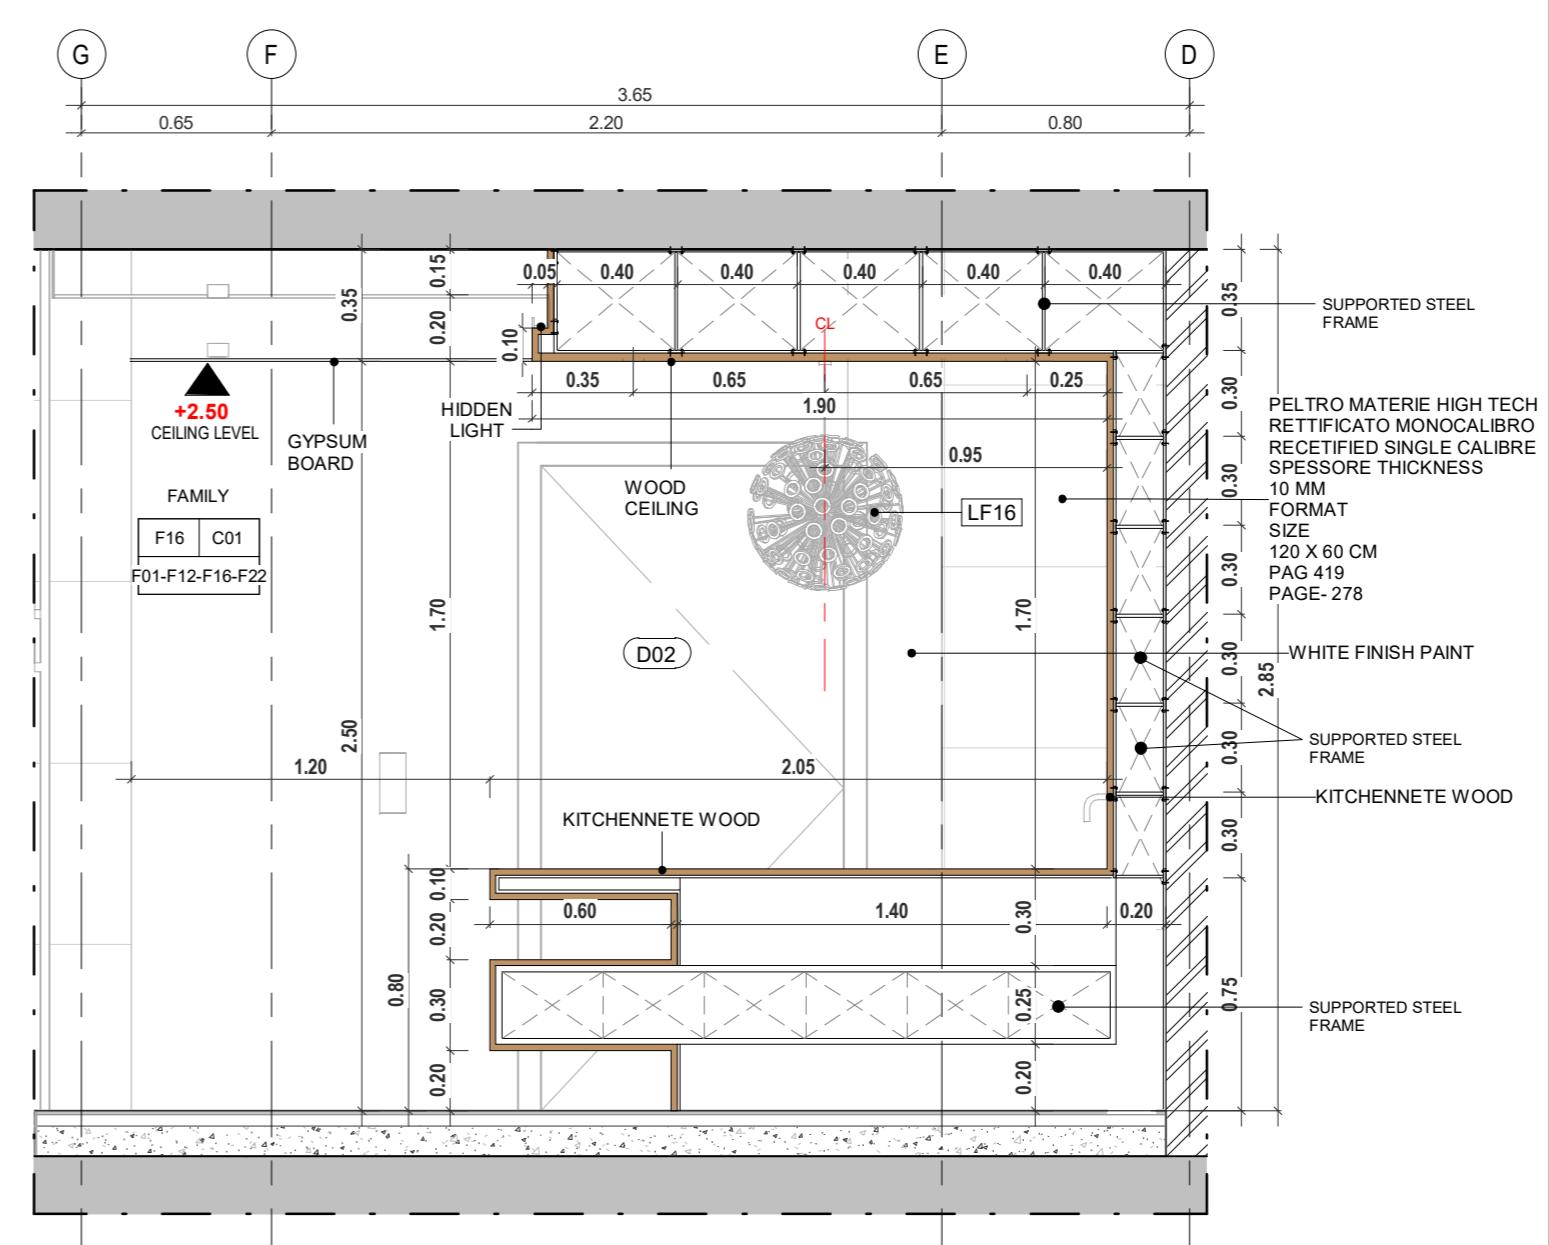

5 SECTION DETAIL
1 : 25

1 : 25



PROJECT NAME

APARTMENTS BUILDING

NOTES

FOR FINISHES REFER TO SHEETS:
ID-6000
ID-6001

FINISHES SCHEDULE		FINISHES SCHEDULE	
Material: Mark	DESCRIPTION	Material: Mark	DESCRIPTION
F01	WHITE PAINT	F15	BEIGE PAINT
F02	GOLD WOOD	F16	TRAVERTINO MARBLE
F03	GOLD STONE	F17	LEATHER
F04	DARK WOOD	F18	PAINT GOLD METAL EFFECT
F05	DECORATIVE STONE	F19	DECORATIVE WOOD
F06	WOOD	F20	GREY STONE
F07	BLACK MARBLE	F21	CONCRETE FINISH
F08	BEIGE MARBLE	F22	KITCHENNETE WOOD
F09	GREY STONE	F23	SWIMMING POOL WALL FINISH
F10	WALL PAPER	F24	PARQUET
F11	CALCATTÀ	F25	WHITE FINISH GRC
F12	SWIMMING POOL MARBLE		
F13	BLACK PAINT		
F14	CALCATTÀ		

Project Type	Residential
Owner	Khalid Khadir Hasan AL-Saeed
Location	Amman
Plot No.	1659
Basin No.	19
Designed by	A.Shaker Khulief 4809

SHEET NAME

BASEMENT FLOOR-LIVING ROOM

ID-4003

Date

08/10/2019

Scale

As indicated



AL-BOUCA'ID
ENGINEERING CONSULTING BUREAU

مکتب البقاعی
للاستشارات الهندسية

The logo for BIM Lab Engineering Services. It features the word "BIM" in large, bold, orange-red letters with a geometric, faceted texture. To the right of "BIM" is a vertical grey line. To the right of the line is the word "Lab" in a smaller, black, sans-serif font. Below "BIM" and "Lab" is the phrase "Engineering Services" in a smaller, black, sans-serif font.

PROJECT NAME

APARTMENTS BUILDING

NOTES



**FOR FINISHES REFER TO SHEETS:
ID-6000
ID-6001**

1 PLAN DETAIL-03

:25

2 PLAN DETAIL-TOP

1 : 25

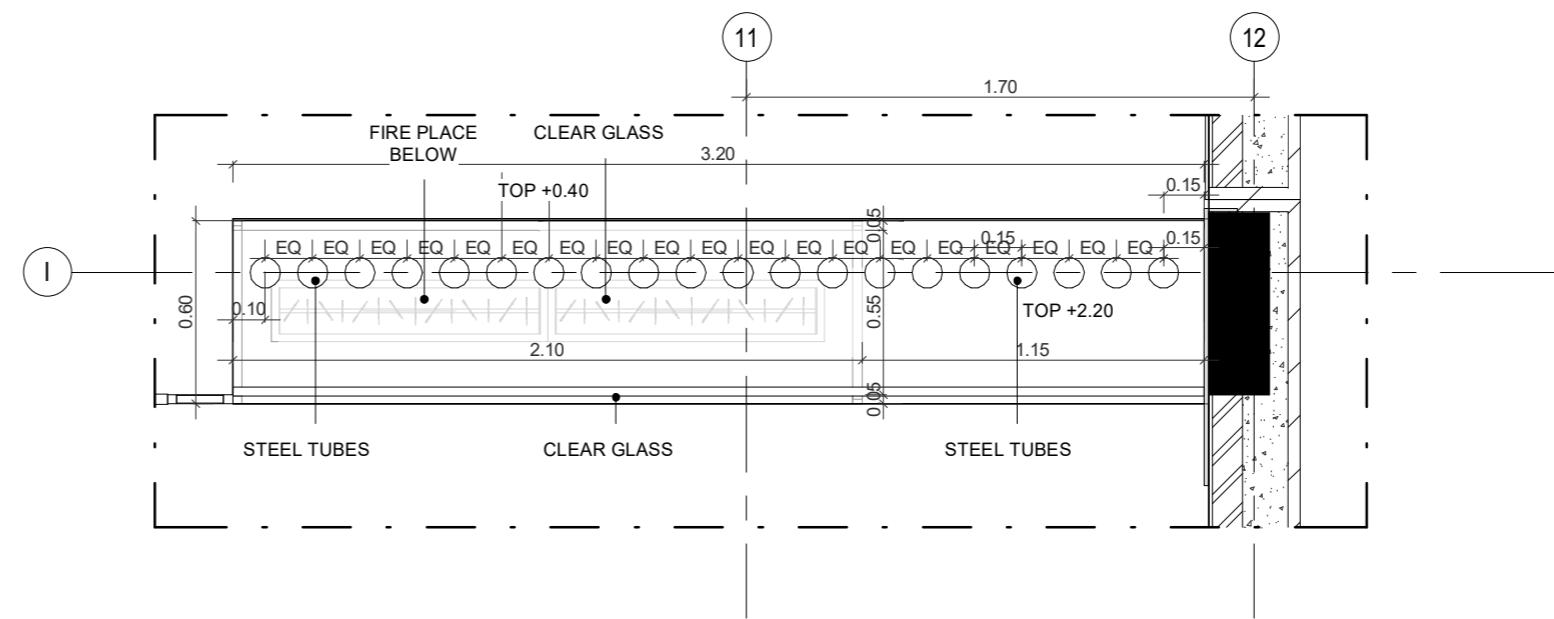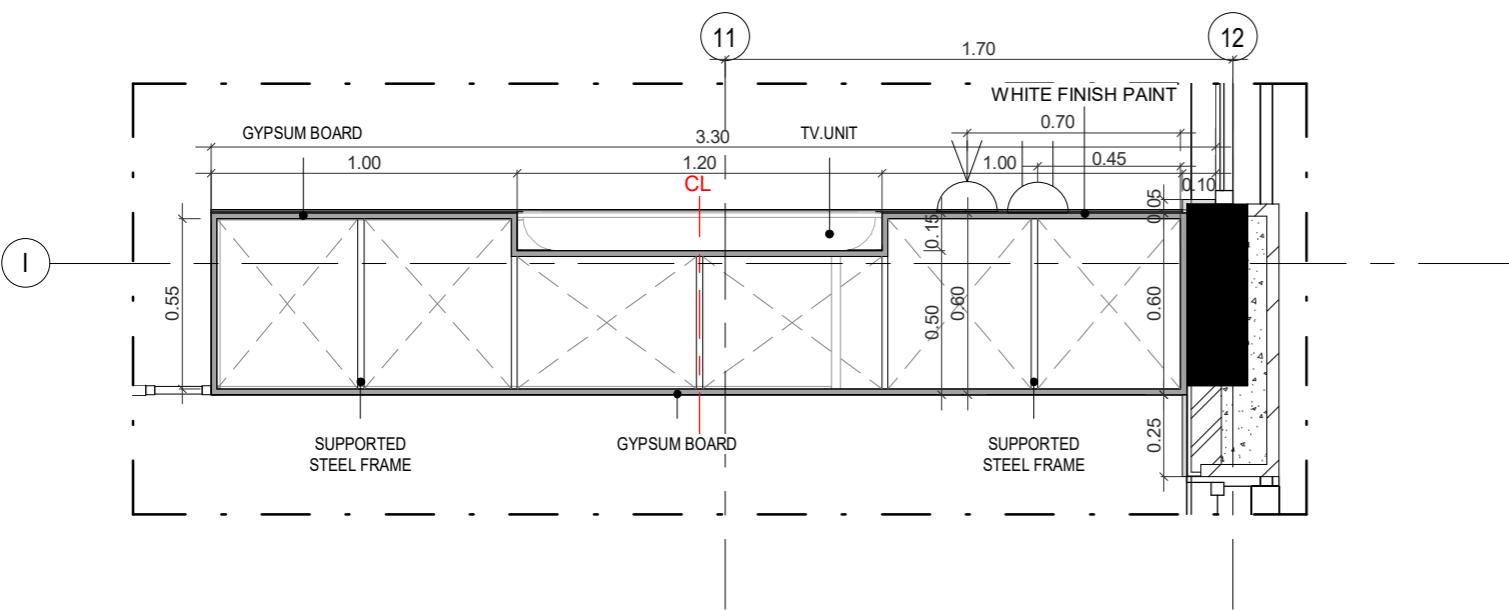


1 PLAN DETAIL-03

:25

2 PLAN DETAIL-TOP

1 : 25

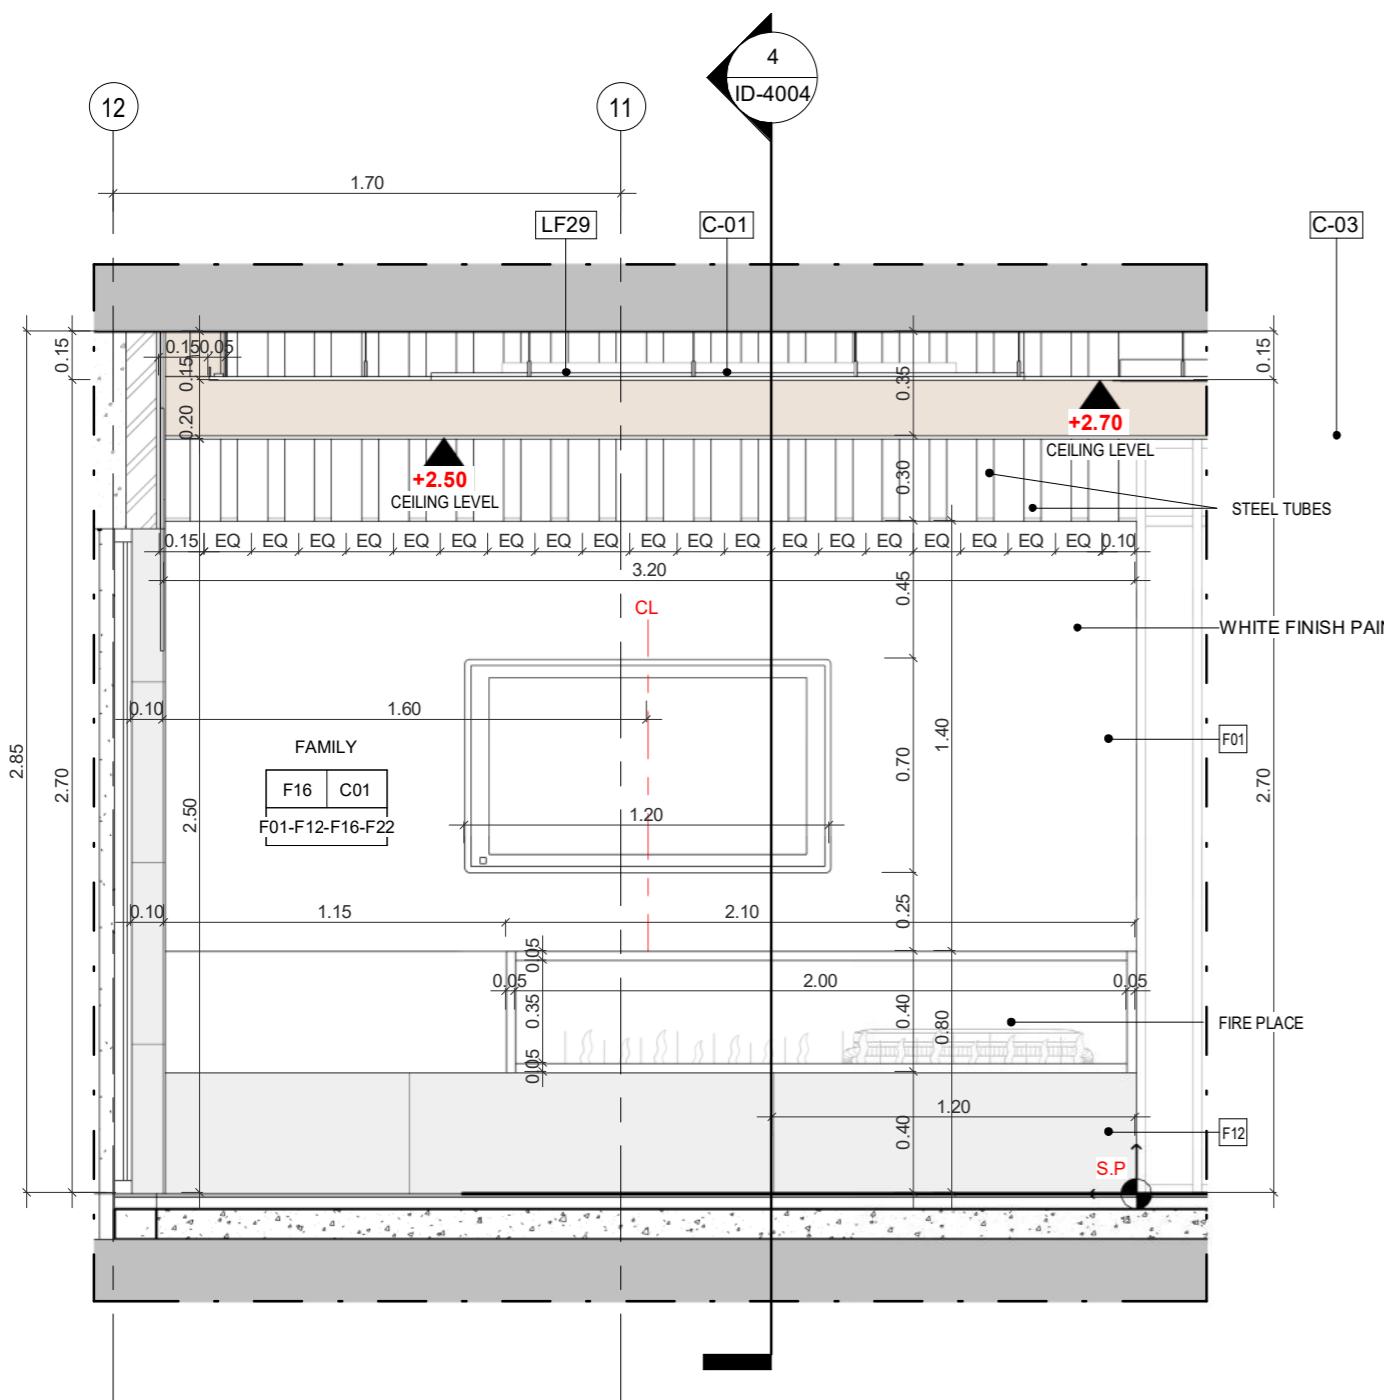


3 ELEVATION DETAIL 02

:25

4 SECTION DETAIL-0

4 1:25

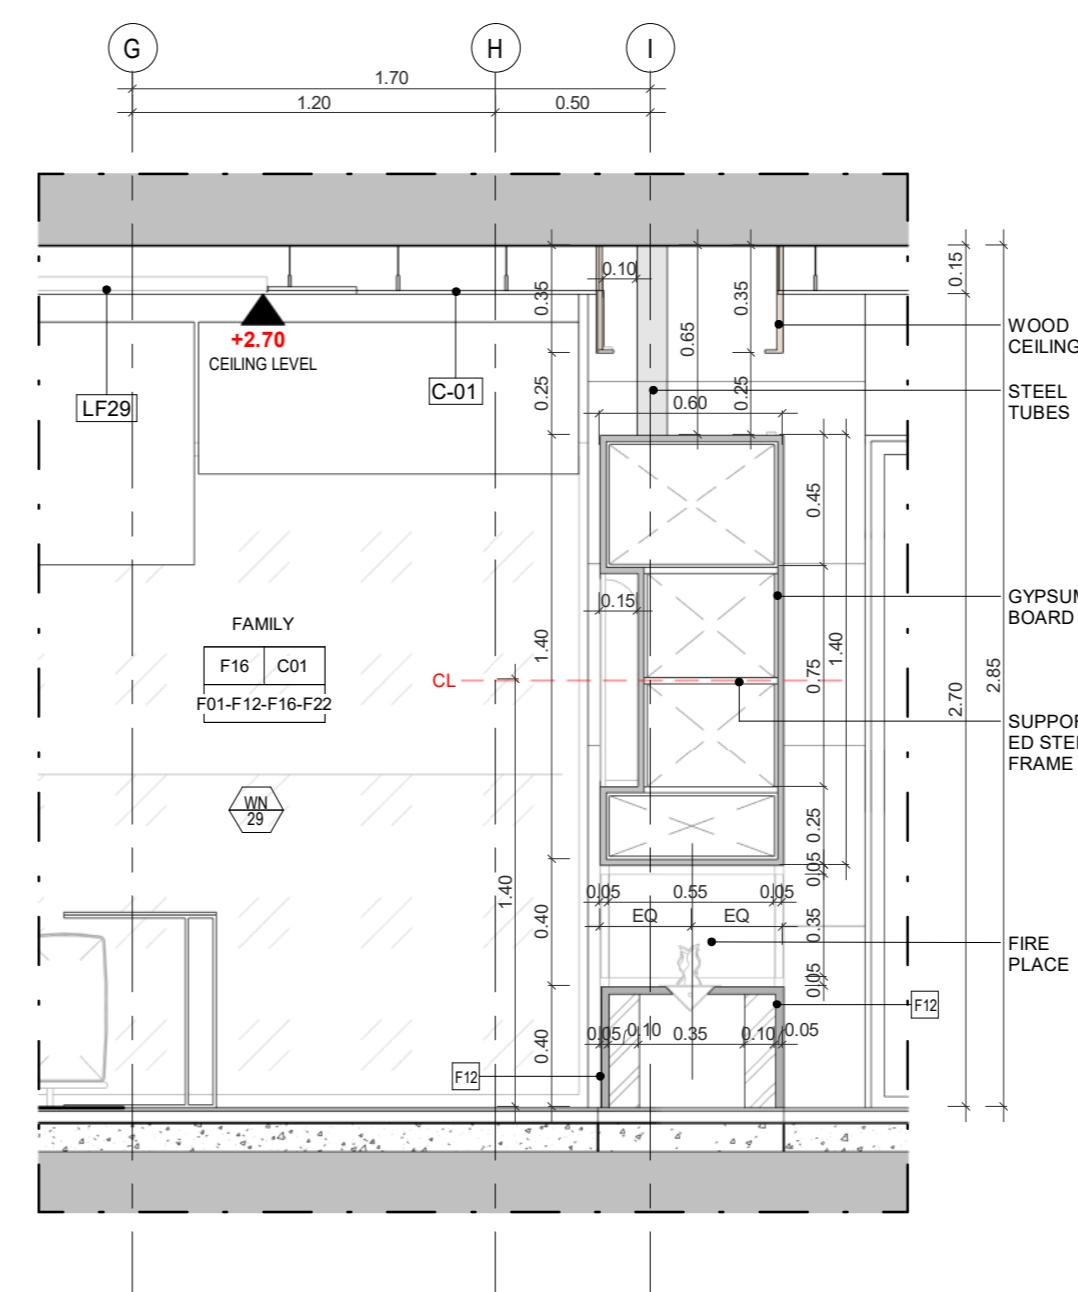

Project Type	Residential
Owner	Khalid Khadir Hasan AL-Saeed
Location	Amman
Plot No.	1659
Basin No.	19
Designed by	A.Shaker Khulief 4809

SHEET NAME

**BASEMENT FLOOR-LIVING
ROOM**

ID-4004

Date 08/10/2019

Scale 1 : 25

PROJECT NAME

APARTMENTS BUILDING

NOTES



Project Type	Residential
Owner	Khalid Khadir Hasan AL-Saeed
Location	Amman
Plot No.	1659
Basin No.	19
Designed by	A.Shaker Khulief 4809

SHEET NAME

SWIMMING POOL -SHOT

ID-4010

Date 08/10/2019

Scale


PROJECT NAME

APARTMENTS BUILDING

NOTES

FOR FINISHES REFER TO SHEETS:
ID-6000
ID-6001

FINISHES SCHEDULE	
Material: Mark	DESCRIPTION
F01	WHITE PAINT
F15	BEIGE PAINT
F02	GOLD WOOD
F03	TRAVERTINO MARBLE
F04	DARK WOOD
F05	DECORATIVE STONE
F06	WOOD
F07	BLACK MARBLE
F08	BEIGE MARBLE
F09	GREY STONE
F10	WALL PAPER
F11	CALCAGNA
F12	SWIMMING POOL MARBLE
F13	BLACK PAINT
F14	PARQUET
F25	WHITE FINISH GRC

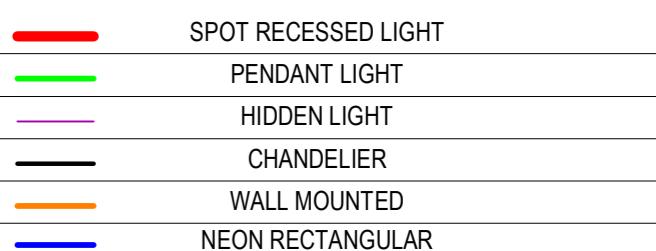


Project Type	Residential
Owner	Khalid Khadir Hasan AL-Saeed
Location	Amman
Plot No.	1659
Basin No.	19
Designed by	A.Shaker Khulief 4809


SHEET NAME	BASEMENT FLOOR-SWIMMING POOL
------------	------------------------------

ID-4011

Date 08/10/2019
Scale 1 : 50

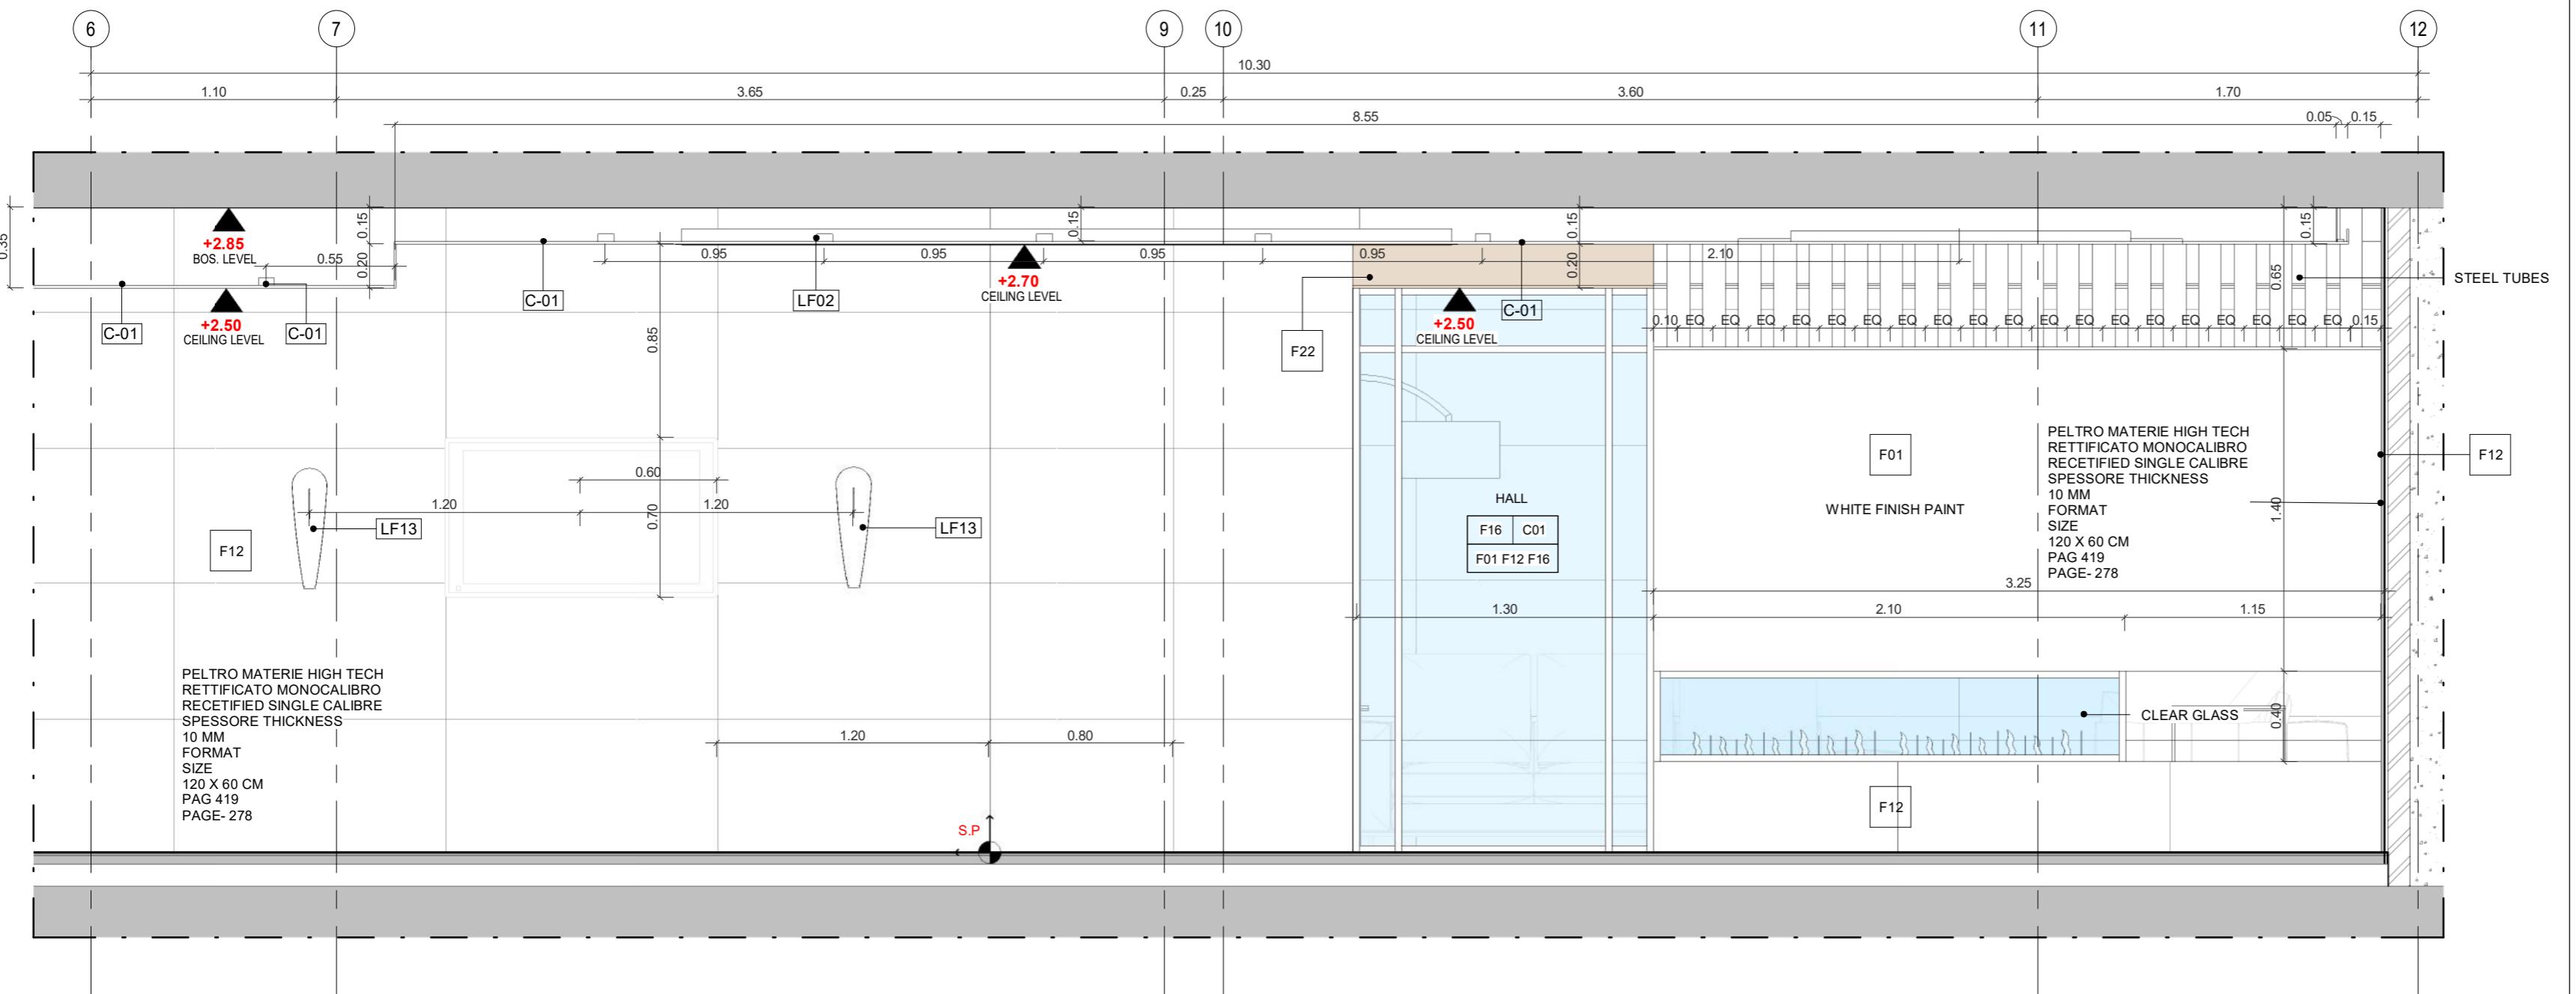

1 SWIMMING POOL HALL-ELEVATION 01
1 : 25

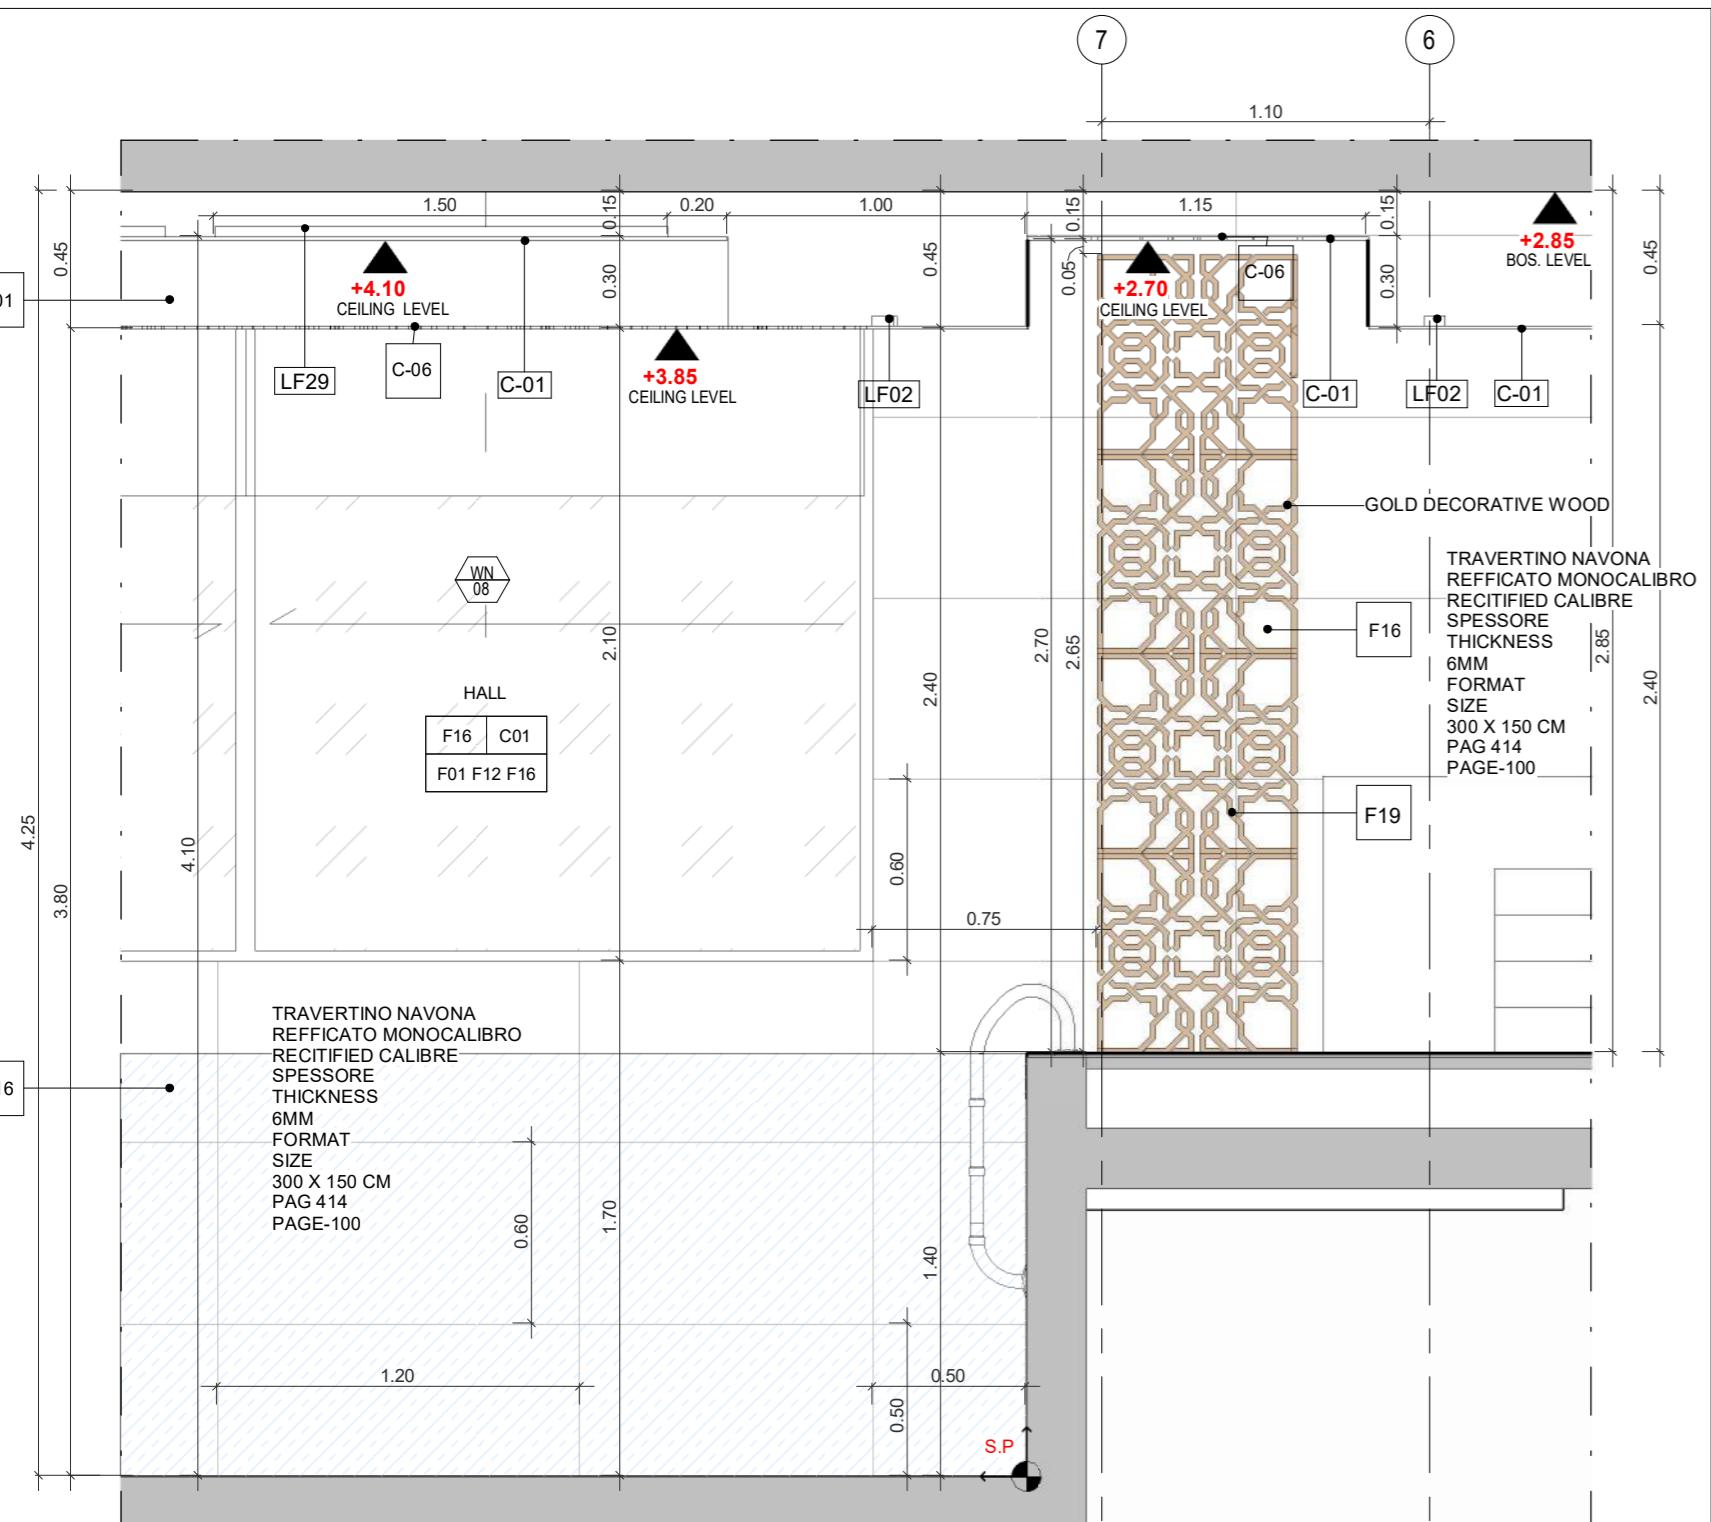

2 SWIMMING POOL HALL-ELEVATION 02
1 : 25

3 SWIMMING POOL-CEILING SECTION
1 : 10

AL-BOUCA'I
ENGINEERING CONSULTING BUREAU
مكتب الباعي
للاستشارات الهندسية

BIM lab
Engineering Services

PROJECT NAME

APARTMENTS BUILDING

NOTES

FINISHES SCHEDULE	
Material: Mark	DESCRIPTION
F01	WHITE PAINT
F15	BEIGE PAINT
F02	GOLD WOOD
F03	GOLD STONE
F04	DARK WOOD
F05	DECORATIVE STONE
F17	LEATHER
F18	PAINT GOLD METAL EFFECT
F06	WOOD
F07	BLACK MARBLE
F08	BEIGE MARBLE
F09	GREY STONE
F10	CONCRETE FINISH
F21	KITCHENNE WOOD
F12	SWIMMING POOL MARBLE
F23	WALL PAPER
F24	PARQUET
F13	CALCATTA
F25	WHITE FINISH GRC







Project Type	Residential
Owner	Khalid Khadir Hasan AL-Saeed
Location	Amman
Plot No.	1659
Basin No.	19
Designed by	A.Shaker Khulief 4809

SHEET NAME
BASEMENT FLOOR-SWIMMING POOL



ID-4012

Date 08/10/2019
Scale As indicated

PROJECT NAME	APARTMENTS BUILDING	
NOTES	FOR FINISHES REFER TO SHEETS: ID-6000 ID-6001	
ROOM NAME	
FLOOR FINISH CEILING FINISH	
WALL FINISH	
<table border="1"> <thead> <tr> <th>FINISHES</th><th>FINISH TAG</th><th>COMMENTS</th></tr> </thead> <tbody> <tr><td>F01</td><td></td><td></td></tr> <tr><td>F02</td><td></td><td></td></tr> <tr><td>F03</td><td></td><td>GOLD STONE</td></tr> <tr><td>F04</td><td></td><td>DARK WOOD</td></tr> <tr><td>F05</td><td></td><td>DARK WOOD</td></tr> <tr><td>F06</td><td></td><td>WOOD</td></tr> <tr><td>F07</td><td></td><td>BLACK MARBLE</td></tr> <tr><td>F08</td><td></td><td>BEIGE MARBLE</td></tr> <tr><td>F09</td><td></td><td>GREY STONE</td></tr> <tr><td>F10</td><td></td><td>WALL PAPER</td></tr> <tr><td>F11</td><td></td><td></td></tr> <tr><td>F12</td><td></td><td></td></tr> <tr><td>F13</td><td></td><td>BLACK PAINT</td></tr> <tr><td>F14</td><td></td><td>CALACATTA</td></tr> <tr><td>F15</td><td></td><td>BEIGE PAINT</td></tr> </tbody> </table>			FINISHES	FINISH TAG	COMMENTS	F01			F02			F03		GOLD STONE	F04		DARK WOOD	F05		DARK WOOD	F06		WOOD	F07		BLACK MARBLE	F08		BEIGE MARBLE	F09		GREY STONE	F10		WALL PAPER	F11			F12			F13		BLACK PAINT	F14		CALACATTA	F15		BEIGE PAINT
FINISHES	FINISH TAG	COMMENTS	
F01	
F02	
F03		GOLD STONE	
F04		DARK WOOD	
F05		DARK WOOD	
F06		WOOD	
F07		BLACK MARBLE	
F08		BEIGE MARBLE	
F09		GREY STONE	
F10		WALL PAPER	
F11	
F12	
F13		BLACK PAINT	
F14		CALACATTA	
F15		BEIGE PAINT	
<table border="1"> <thead> <tr> <th>FINISHES</th><th>FINISH TAG</th><th>COMMENTS</th></tr> </thead> <tbody> <tr><td>F16</td><td></td><td></td></tr> <tr><td>F17</td><td></td><td>LEATHER</td></tr> <tr><td>F18</td><td></td><td>PAINT-GOLD METAL EFFECT</td></tr> <tr><td>F19</td><td></td><td></td></tr> <tr><td>F20</td><td></td><td>GREY STONE</td></tr> <tr><td>F21</td><td></td><td>CONCRETE FINISH</td></tr> <tr><td>F22</td><td></td><td></td></tr> <tr><td>F23</td><td></td><td>SWIMMING POOL WALL FINISHES</td></tr> </tbody> </table>			FINISHES	FINISH TAG	COMMENTS	F16			F17		LEATHER	F18		PAINT-GOLD METAL EFFECT	F19			F20		GREY STONE	F21		CONCRETE FINISH	F22			F23		SWIMMING POOL WALL FINISHES																					
FINISHES	FINISH TAG	COMMENTS	
F16	
F17		LEATHER	
F18		PAINT-GOLD METAL EFFECT	
F19	
F20		GREY STONE	
F21		CONCRETE FINISH	
F22	
F23		SWIMMING POOL WALL FINISHES	
Project Type	Residential	
Owner	Khalid Khadir Hasan AL-Saeed	
Location	Amman	
Plot No.	1659	
Basin No.	19	
Designed by	A.Shaker Khulief 4809	
SHEET NAME	BASEMENT FLOOR- GUEST BATHROOM 1	
ID-4020	
Date	08/10/2019	
Scale	As indicated	

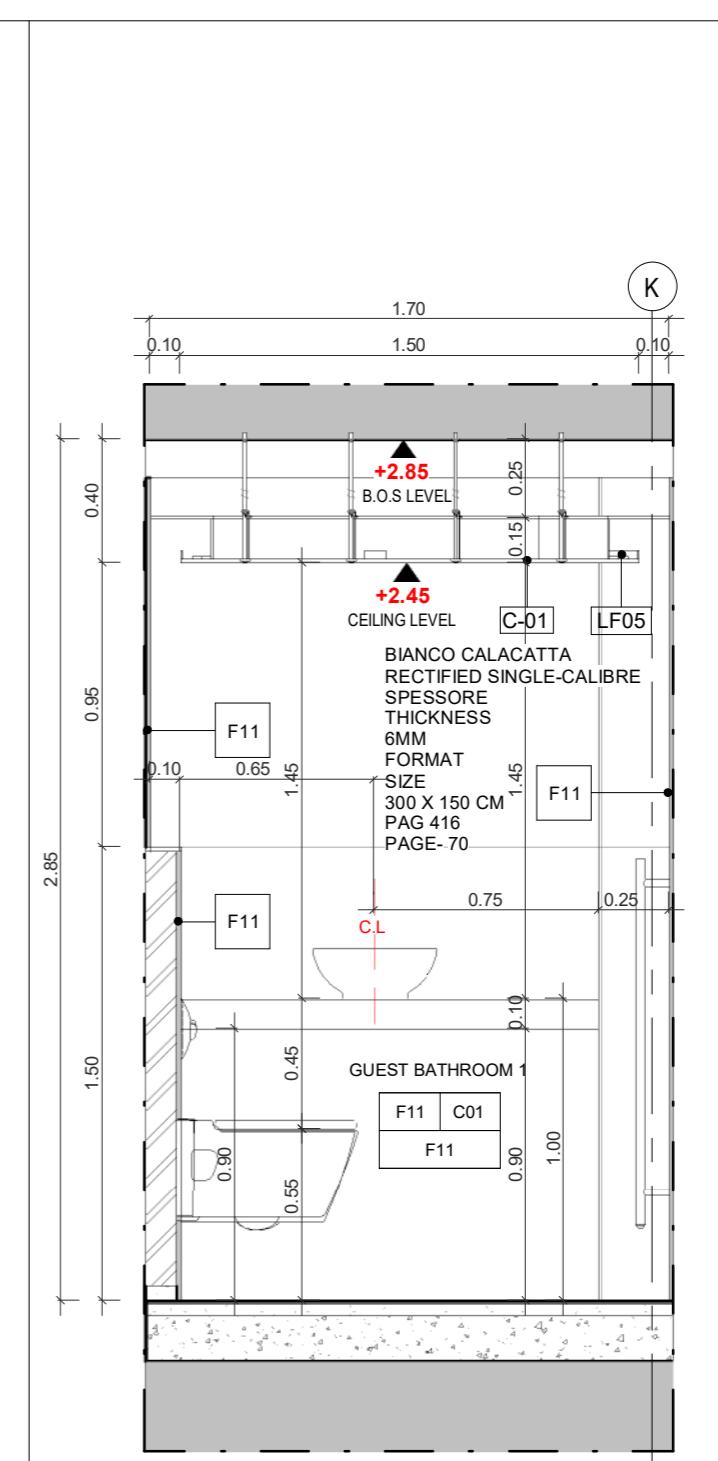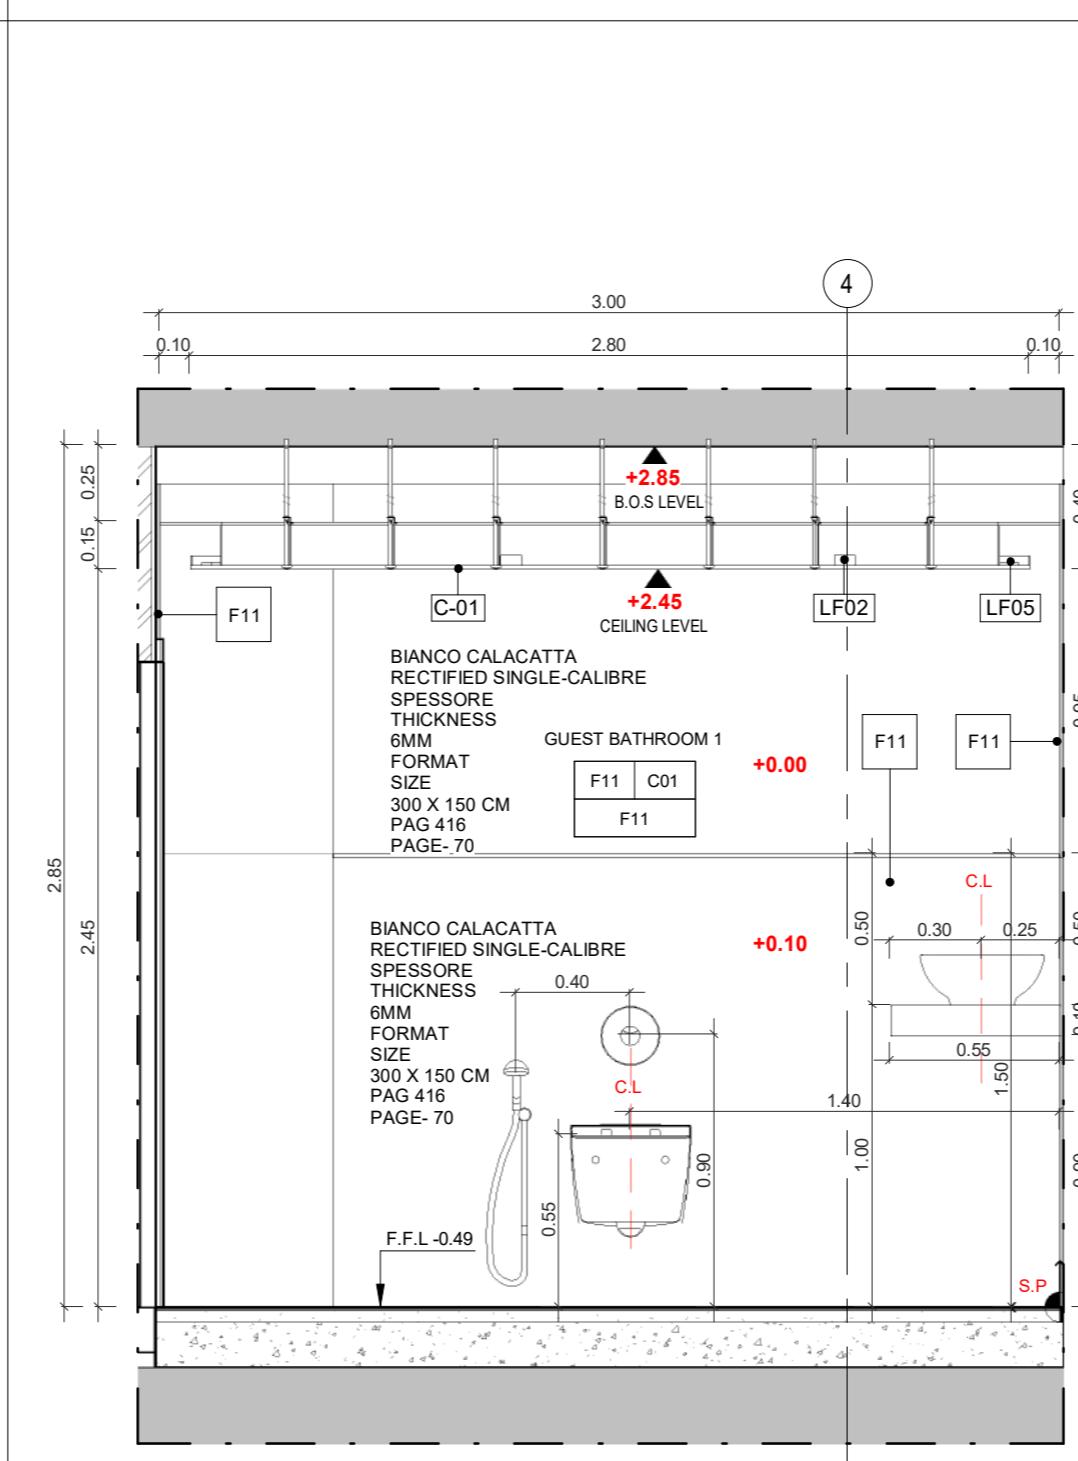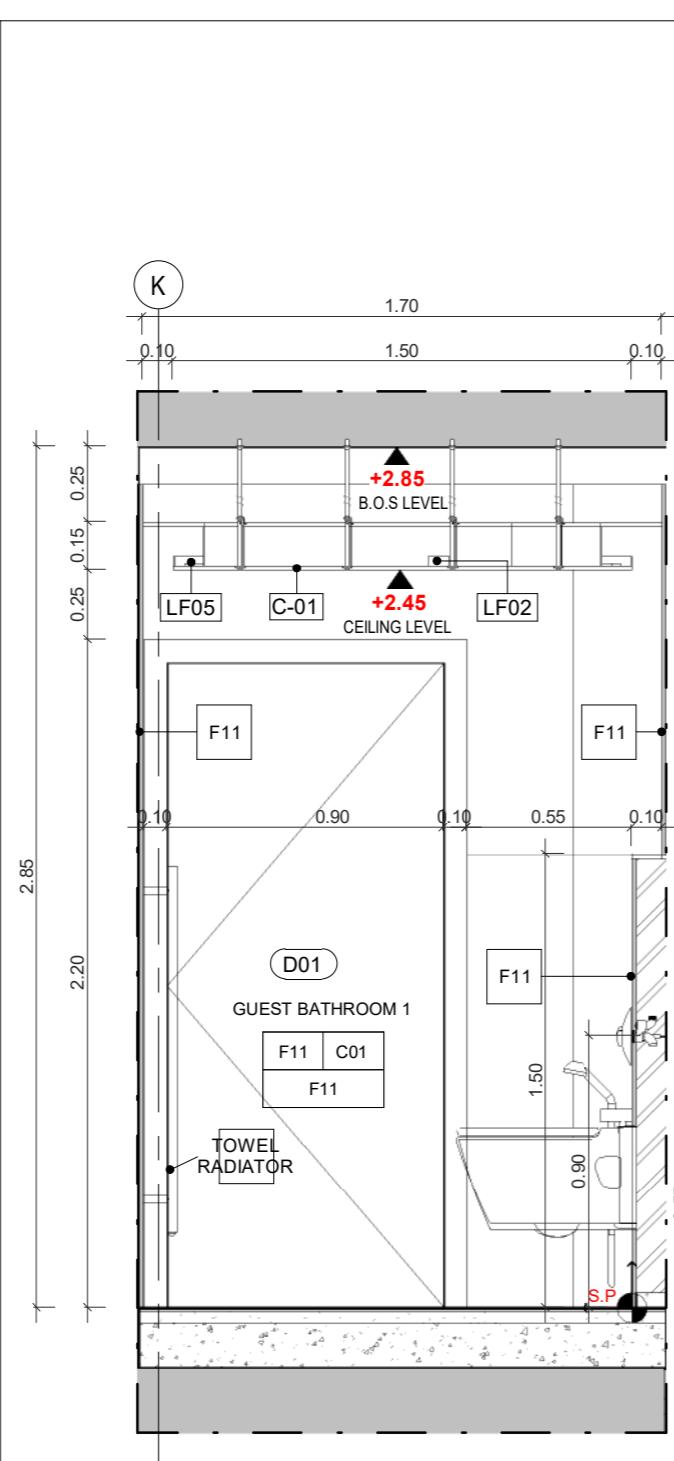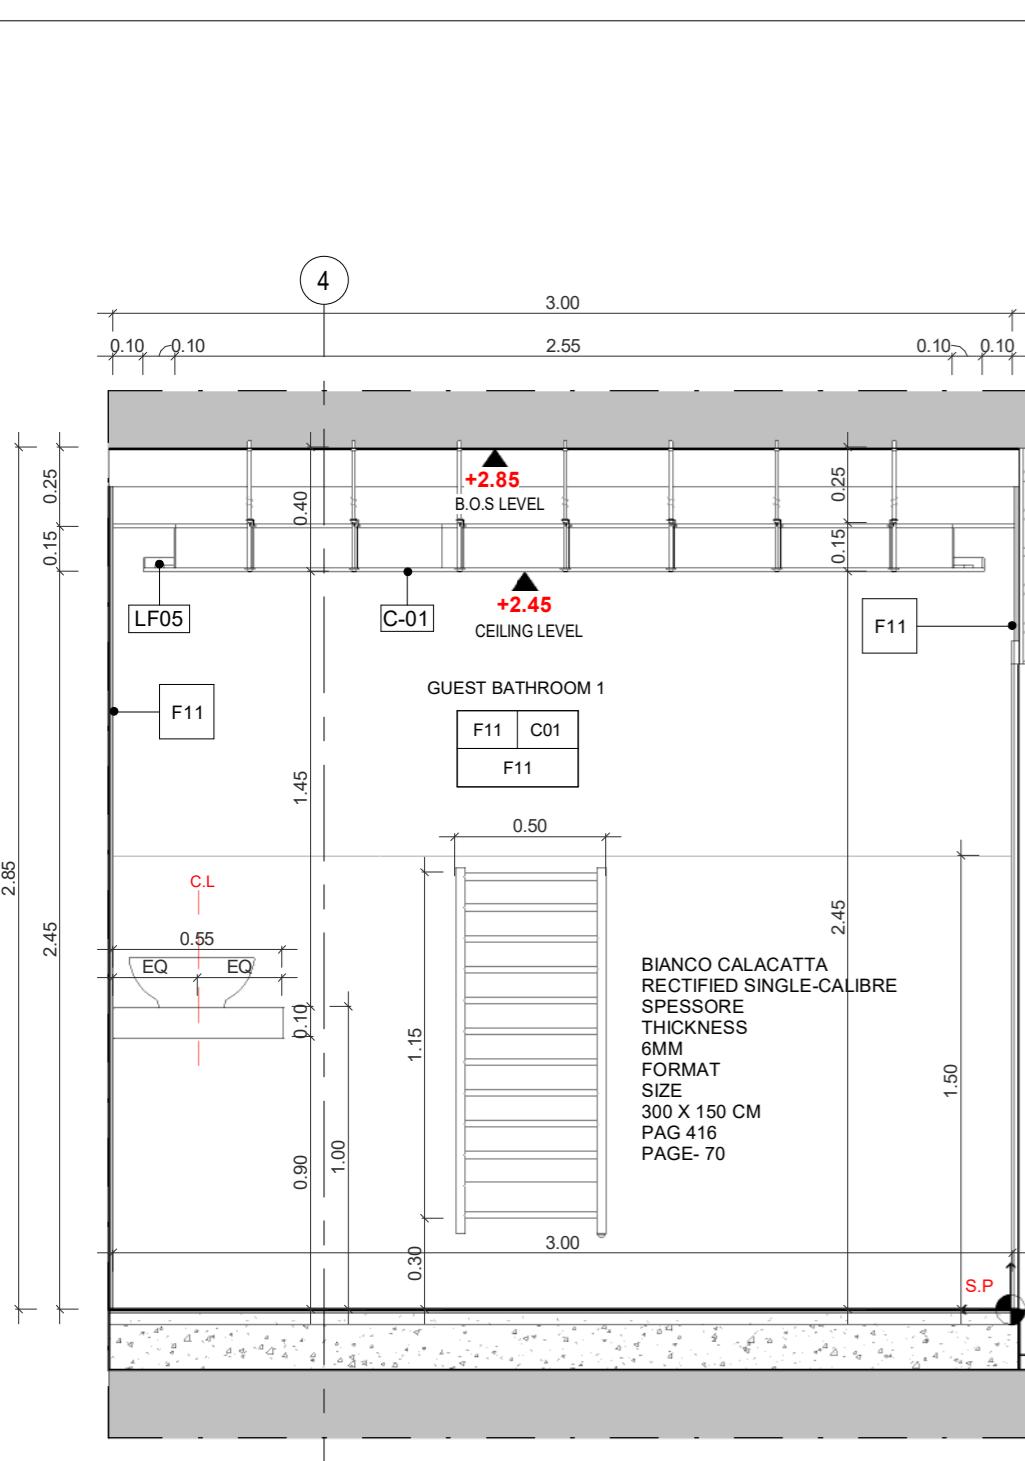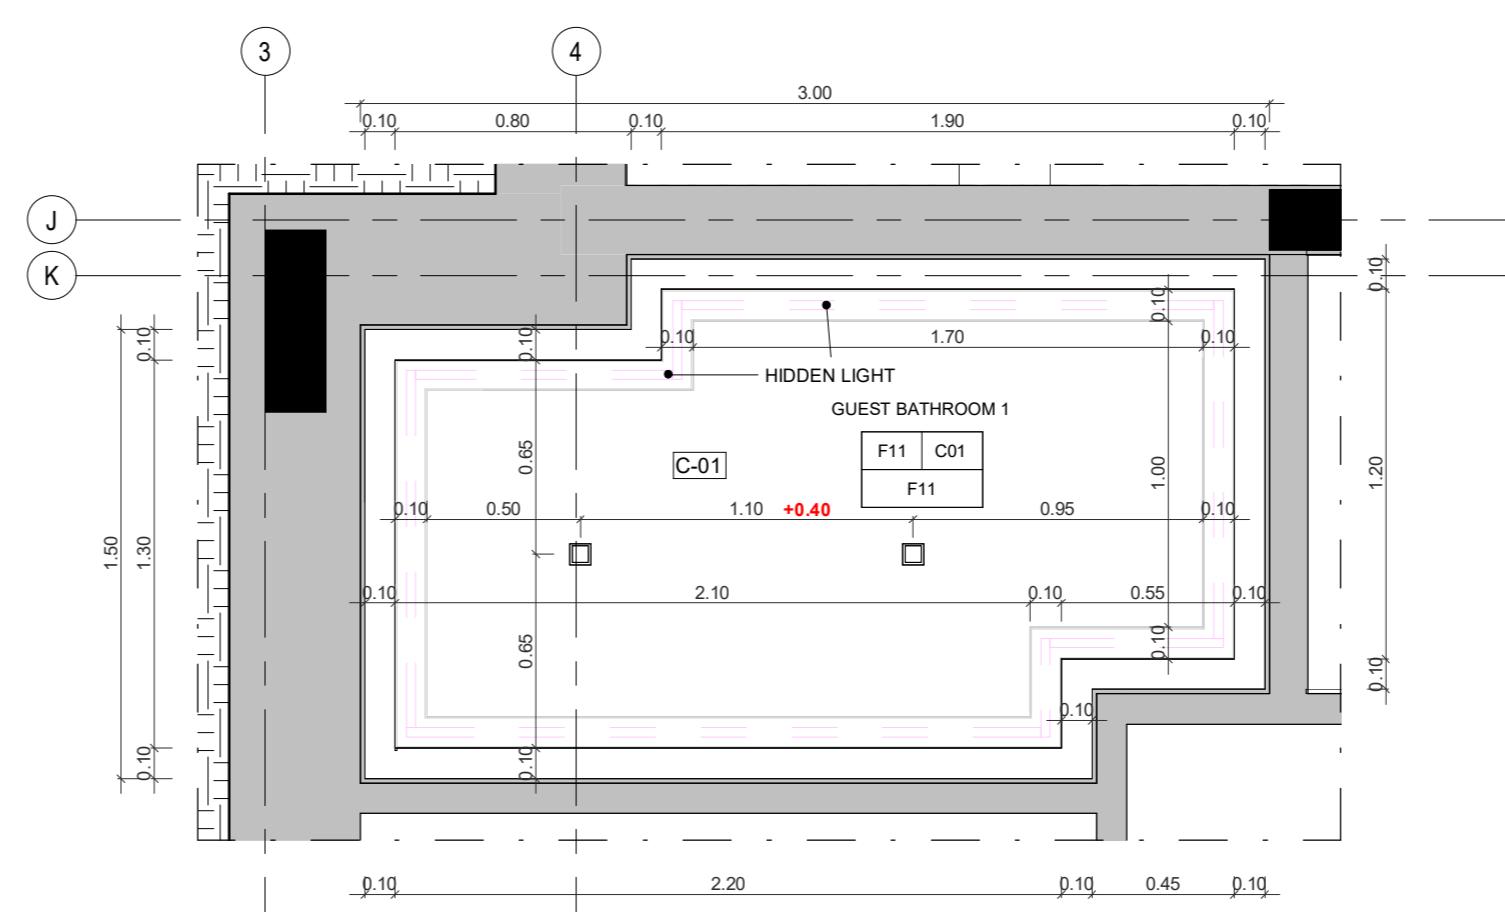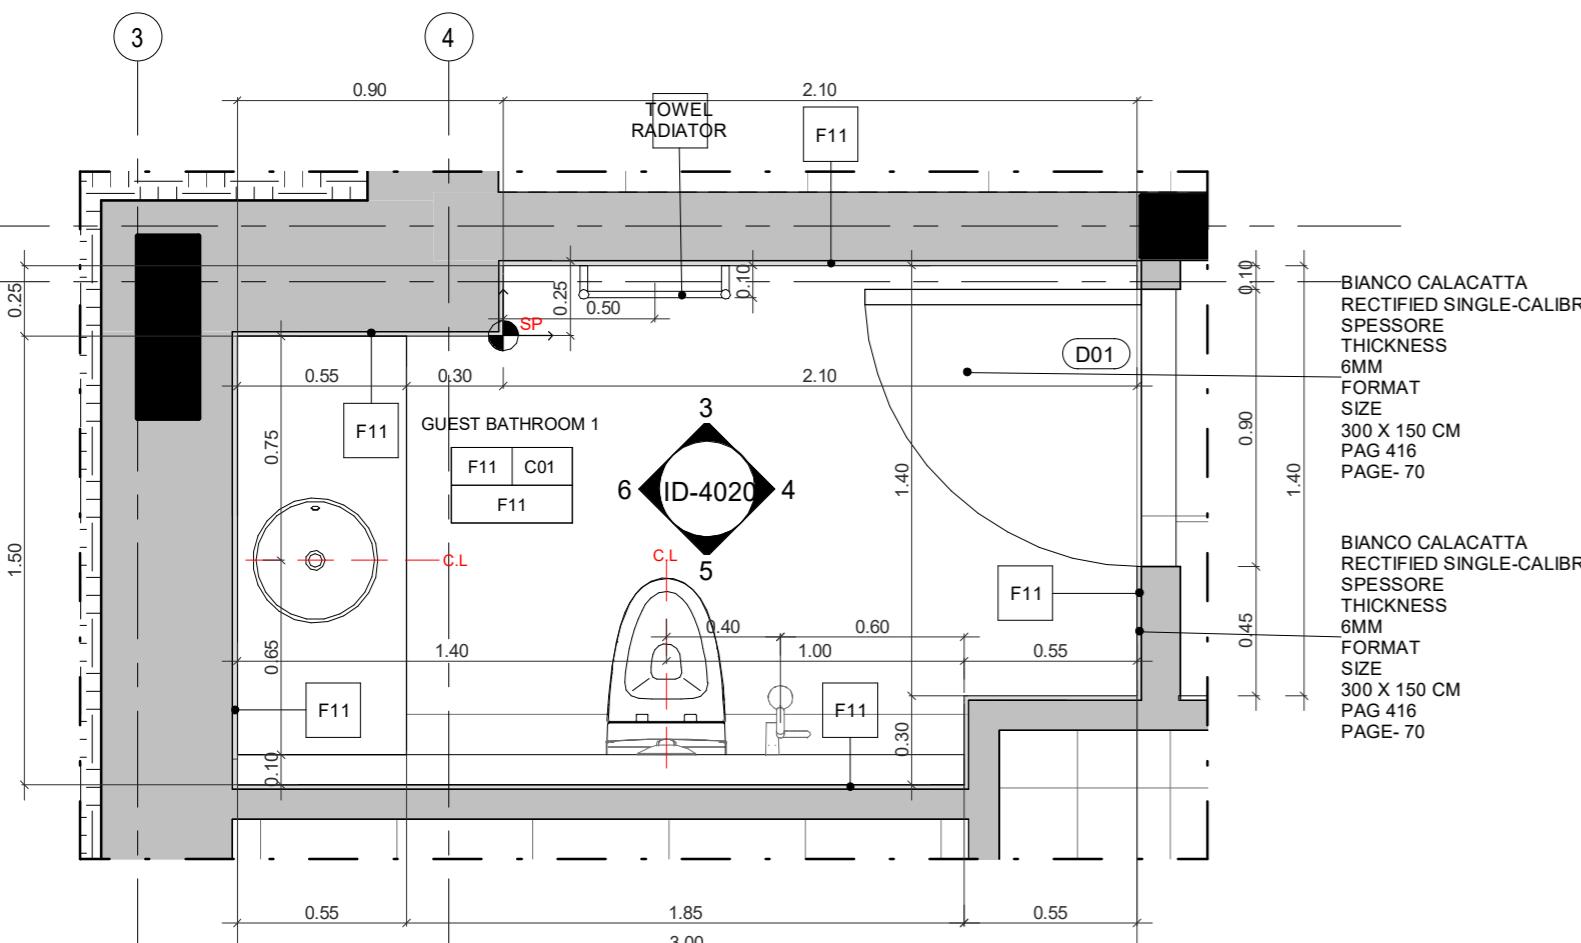

PROJECT NAME	APARTMENTS BUILDING																																			
NOTES	FOR FINISHES REFER TO SHEETS: ID-6000 ID-6001																																			
ROOM NAME																																				
FLOOR FINISH CEILING FINISH																																				
WALL FINISH																																				
<table border="1"> <thead> <tr> <th>FINISHES</th> <th>FINISHES</th> </tr> <tr> <th>FINISH TAG</th> <th>COMMENTS</th> </tr> </thead> <tbody> <tr> <td>F01</td> <td></td> </tr> <tr> <td>F02</td> <td></td> </tr> <tr> <td>F03</td> <td>GOLD STONE</td> </tr> <tr> <td>F04</td> <td>DARK WOOD</td> </tr> <tr> <td>F05</td> <td>DARK WOOD</td> </tr> <tr> <td>F06</td> <td>WOOD</td> </tr> <tr> <td>F07</td> <td>BLACK MARBLE</td> </tr> <tr> <td>F08</td> <td>BEIGE MARBLE</td> </tr> <tr> <td>F09</td> <td>GREY STONE</td> </tr> <tr> <td>F10</td> <td>WALL PAPER</td> </tr> <tr> <td>F11</td> <td></td> </tr> <tr> <td>F12</td> <td></td> </tr> <tr> <td>F13</td> <td>BLACK PAINT</td> </tr> <tr> <td>F14</td> <td>CALACATTA</td> </tr> <tr> <td>F15</td> <td>BEIGE PAINT</td> </tr> </tbody> </table>			FINISHES	FINISHES	FINISH TAG	COMMENTS	F01		F02		F03	GOLD STONE	F04	DARK WOOD	F05	DARK WOOD	F06	WOOD	F07	BLACK MARBLE	F08	BEIGE MARBLE	F09	GREY STONE	F10	WALL PAPER	F11		F12		F13	BLACK PAINT	F14	CALACATTA	F15	BEIGE PAINT
FINISHES	FINISHES																																			
FINISH TAG	COMMENTS																																			
F01																																				
F02																																				
F03	GOLD STONE																																			
F04	DARK WOOD																																			
F05	DARK WOOD																																			
F06	WOOD																																			
F07	BLACK MARBLE																																			
F08	BEIGE MARBLE																																			
F09	GREY STONE																																			
F10	WALL PAPER																																			
F11																																				
F12																																				
F13	BLACK PAINT																																			
F14	CALACATTA																																			
F15	BEIGE PAINT																																			
<table border="1"> <thead> <tr> <th>FINISHES</th> <th>FINISHES</th> </tr> <tr> <th>FINISH TAG</th> <th>COMMENTS</th> </tr> </thead> <tbody> <tr> <td>F16</td> <td></td> </tr> <tr> <td>F17</td> <td>LEATHER</td> </tr> <tr> <td>F18</td> <td>PAINT-GOLD METAL EFFECT</td> </tr> <tr> <td>F19</td> <td></td> </tr> <tr> <td>F20</td> <td>GREY STONE</td> </tr> <tr> <td>F21</td> <td>CONCRETE FINISH</td> </tr> <tr> <td>F22</td> <td></td> </tr> <tr> <td>F23</td> <td>SWIMMING POOL WALL FINISHES</td> </tr> </tbody> </table>			FINISHES	FINISHES	FINISH TAG	COMMENTS	F16		F17	LEATHER	F18	PAINT-GOLD METAL EFFECT	F19		F20	GREY STONE	F21	CONCRETE FINISH	F22		F23	SWIMMING POOL WALL FINISHES														
FINISHES	FINISHES																																			
FINISH TAG	COMMENTS																																			
F16																																				
F17	LEATHER																																			
F18	PAINT-GOLD METAL EFFECT																																			
F19																																				
F20	GREY STONE																																			
F21	CONCRETE FINISH																																			
F22																																				
F23	SWIMMING POOL WALL FINISHES																																			
Project Type	Residential																																			
Owner	Khalid Khadir Hasan AL-Saeed																																			
Location	Amman																																			
Plot No.	1659																																			
Basin No.	19																																			
Designed by	A.Shaker Khulief 4809																																			
SHEET NAME	BASEMENT FLOOR- GUESTS BATHROOM 2																																			
ID-4030																																				
Date	08/10/2019																																			
Scale	As indicated																																			

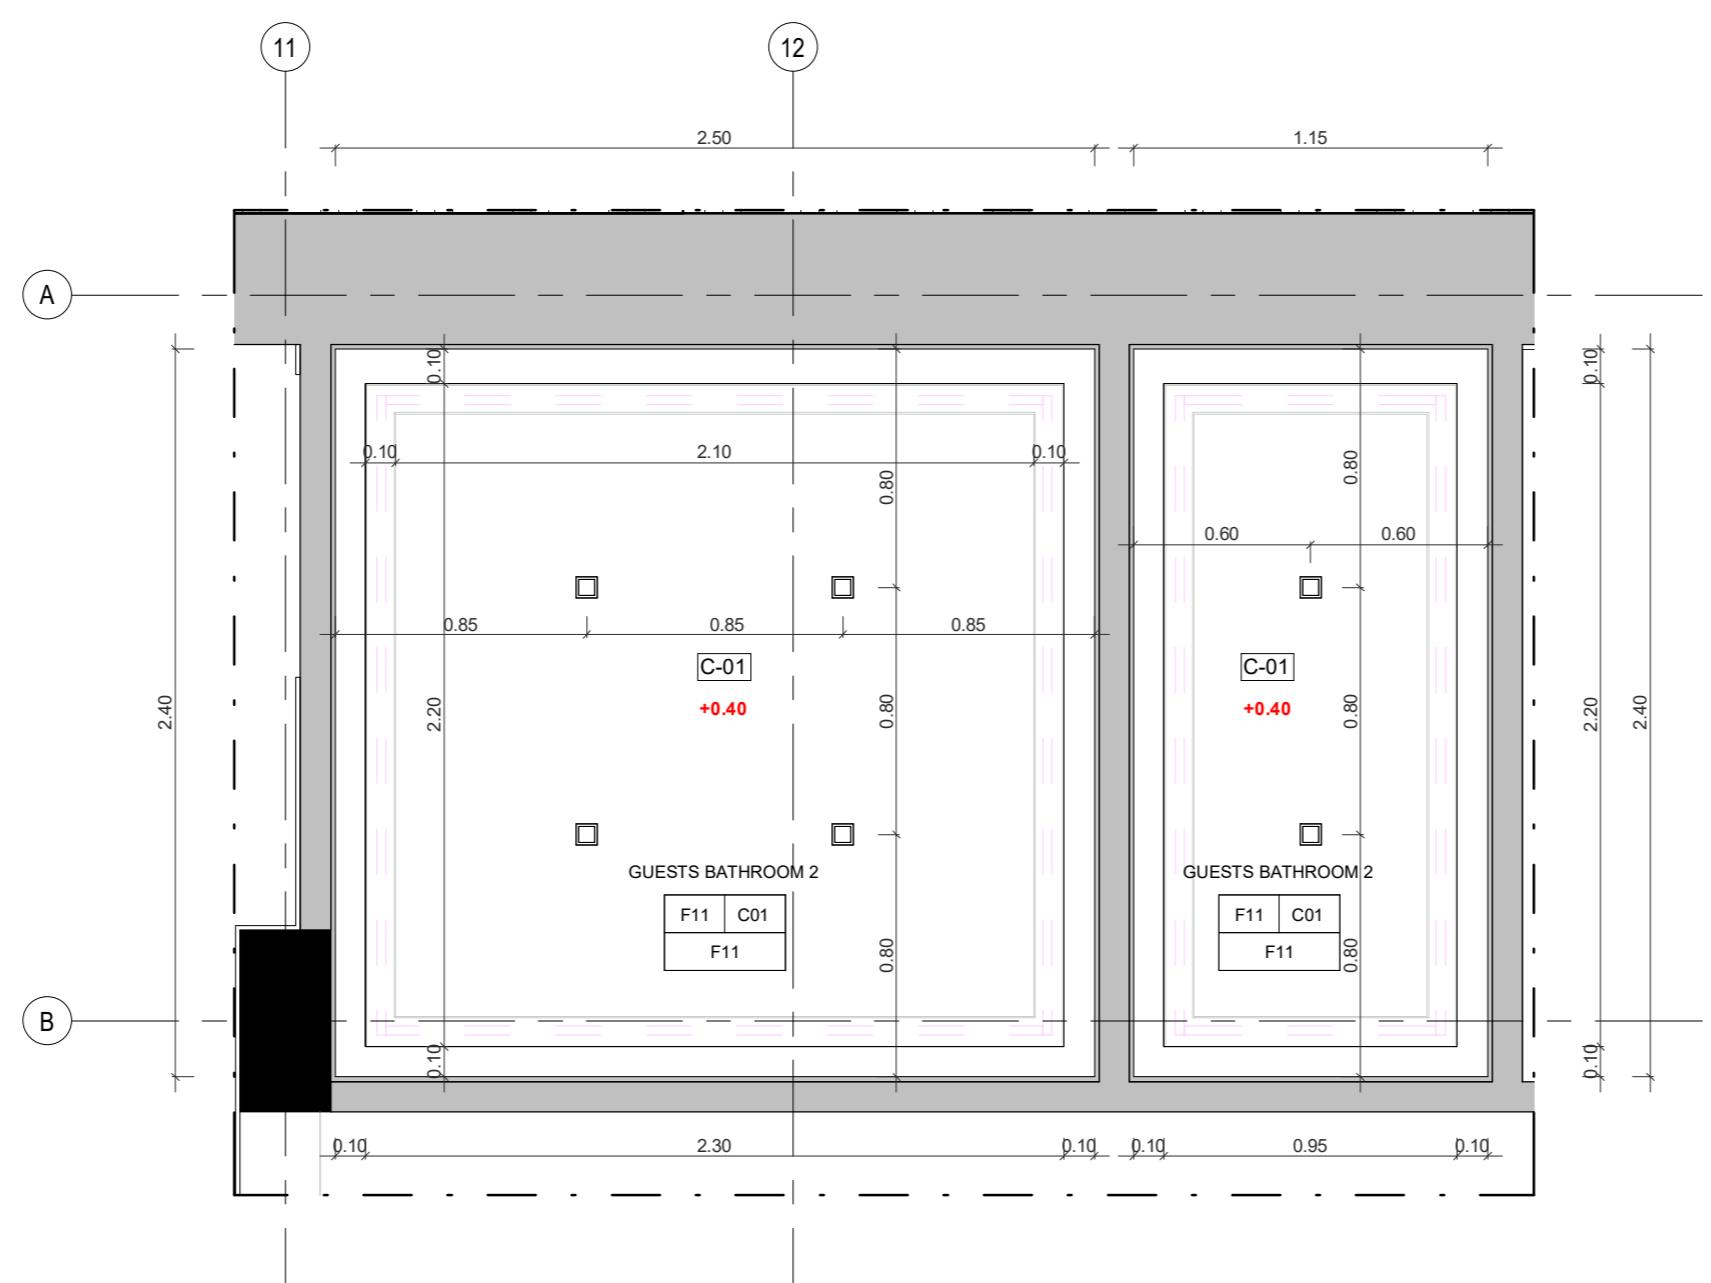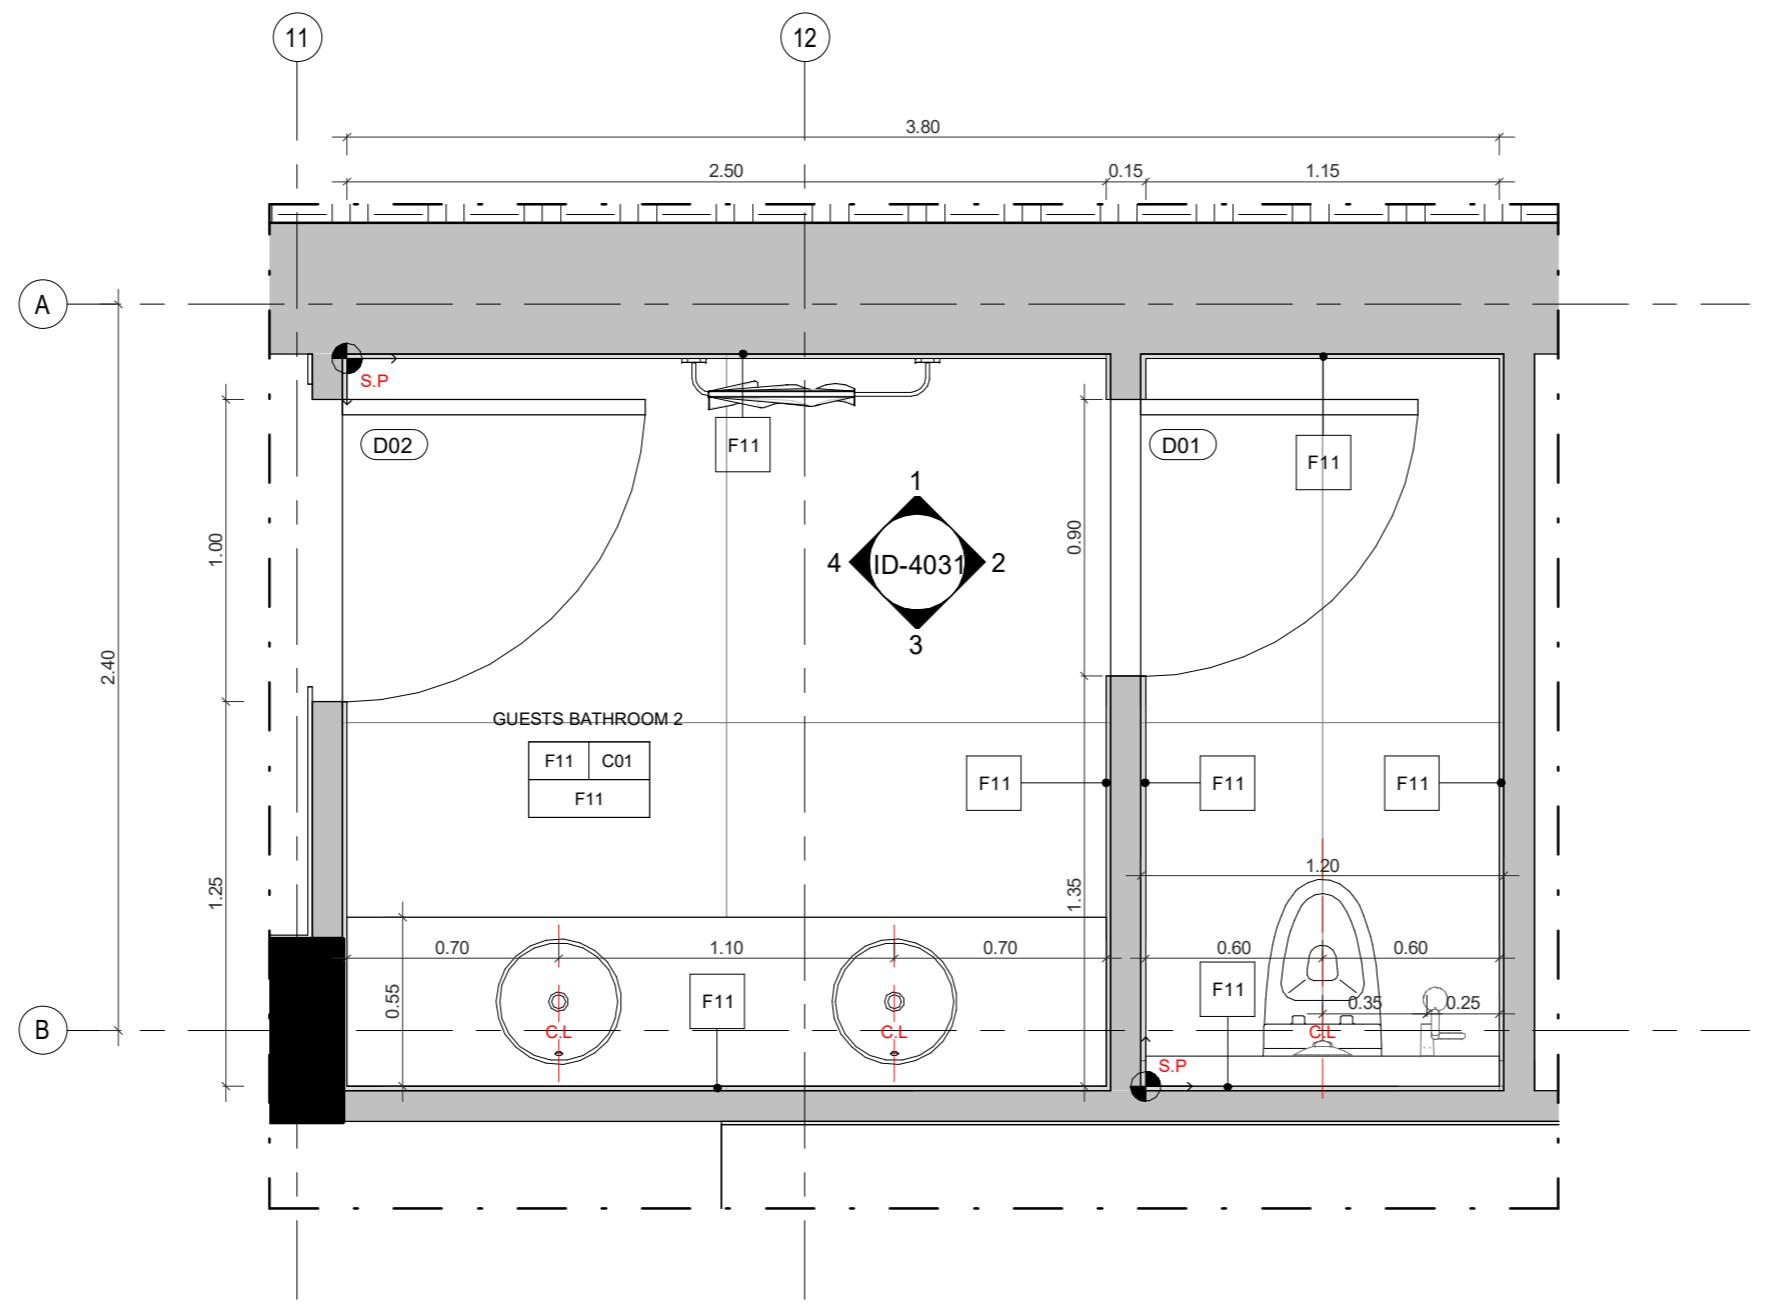

PROJECT NAME

APARTMENTS BUILDING

NOTES

FOR FINISHES REFER TO SHEETS:
ID-6000
ID-6001

ROOM NAME

FLOOR FINISH	CEILING FINISH
--------------	----------------

WALL FINISH

FINISHES		FINISHES	
FINISH TAG	COMMENTS	FINISH TAG	COMMENTS
F01		F16	
F02		F17	LEATHER
F03	GOLD STONE	F18	PAINT-GOLD METAL EFFECT
F04	DARK WOOD	F05	DARK WOOD
F06	WOOD	F19	
F07	BLACK MARBLE	F20	GREY STONE
F08	BEIGE MARBLE	F21	CONCRETE FINISH
F09	GREY STONE	F10	WALL PAPER
F11		F12	
F13	BLACK PAINT	F14	CALACATTA
F15	BEIGE PAINT	F15	BEIGE PAINT

SPOT RECESSED LIGHT

PENDANT LIGHT

HIDDEN LIGHT

CHANDELIER

WALL MOUNTED


NEON RECTANGULAR

Project Type	Residential
Owner	Khalid Khadir Hasan AL-Saeed
Location	Amman
Plot No.	1659
Basin No.	19
Designed by	A.Shaker Khulief 4809

SHEET NAME	BASEMENT FLOOR- GUESTS BATHROOM 2 ELEVATIONS
------------	--


ID-4031

Date	08/10/2019
Scale	As indicated

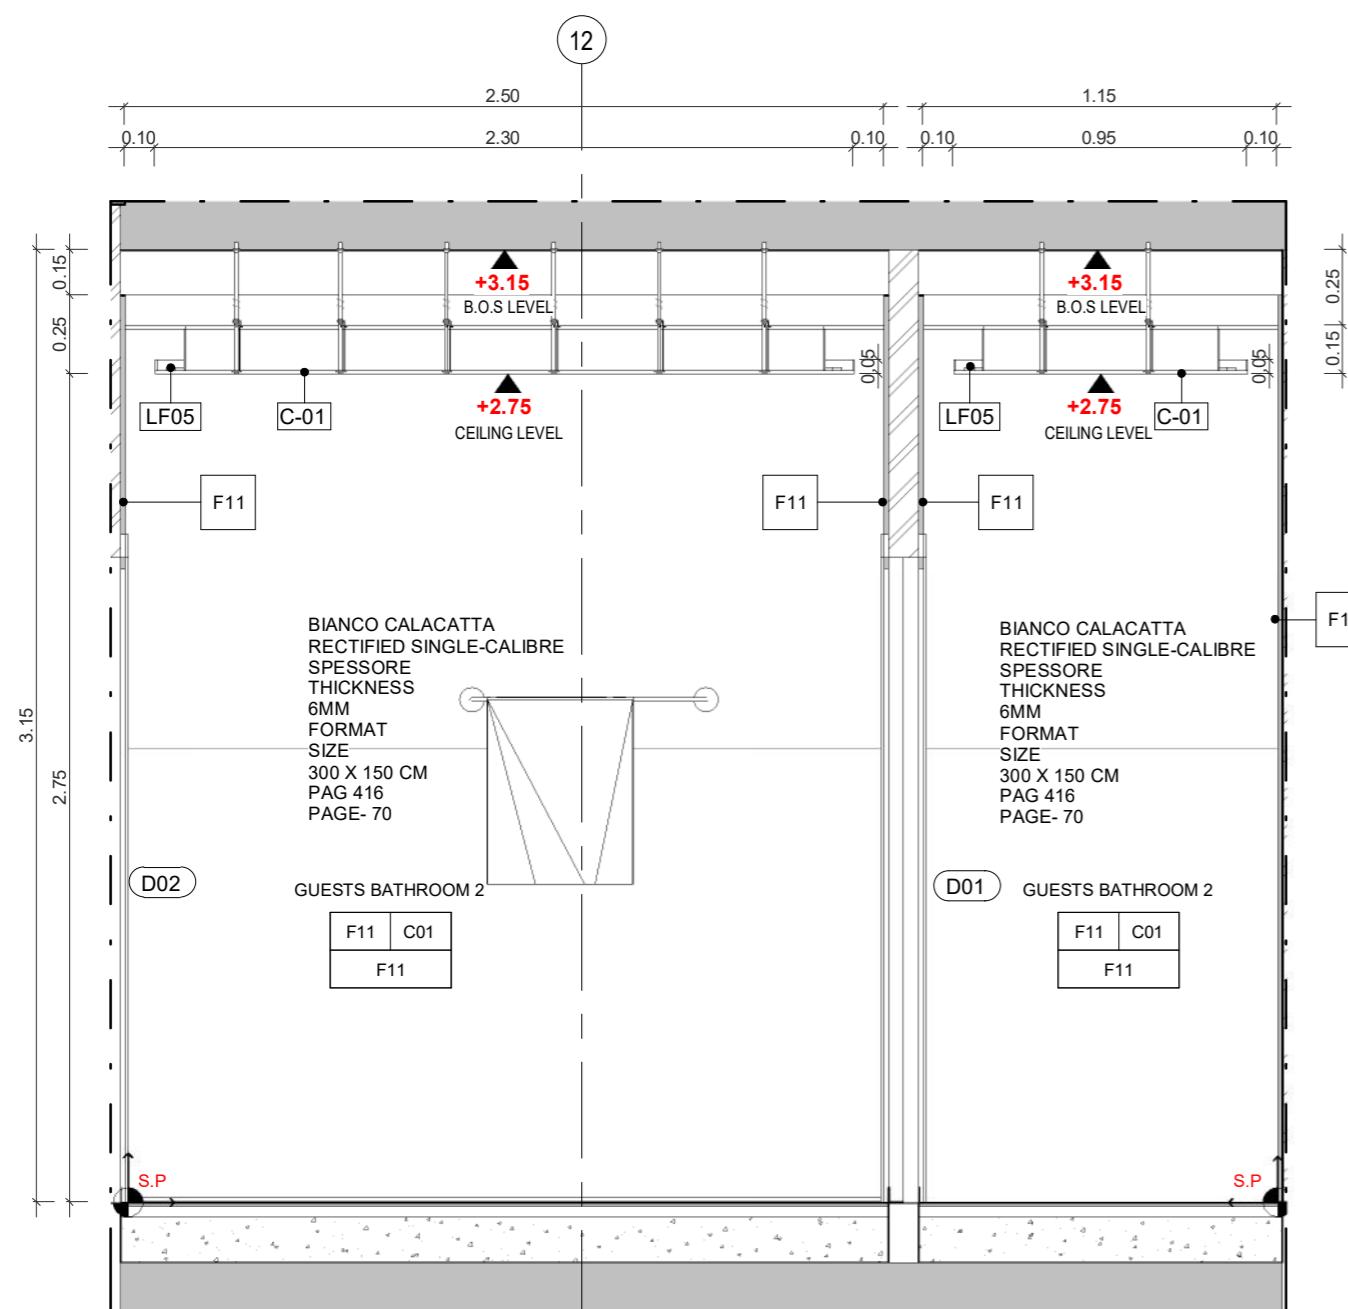


① GUEST BATHROOM 2-ELEVATION 01

1 : 25

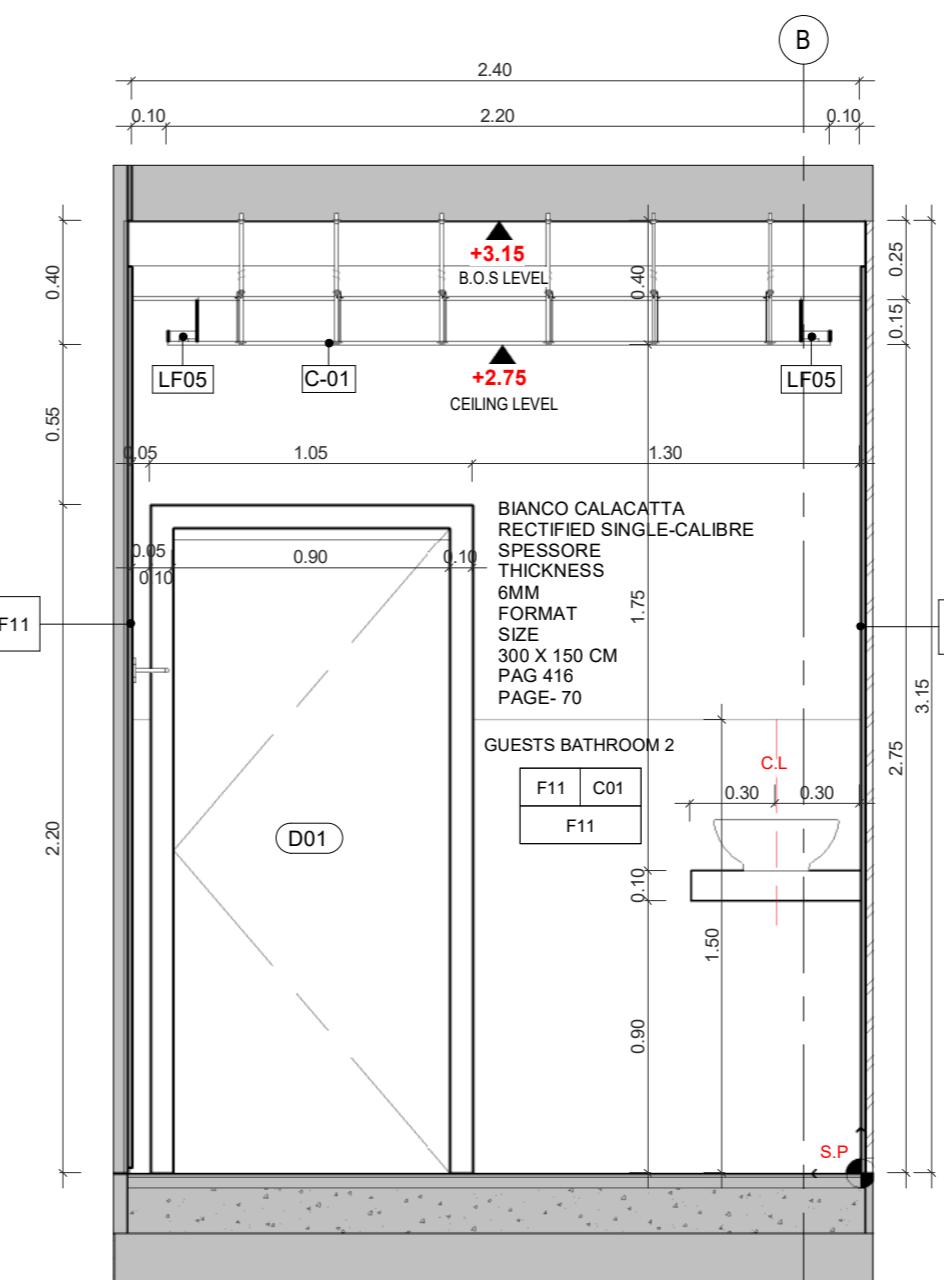


② GUEST BATHROOM 2-ELEVATION 02

1 : 25

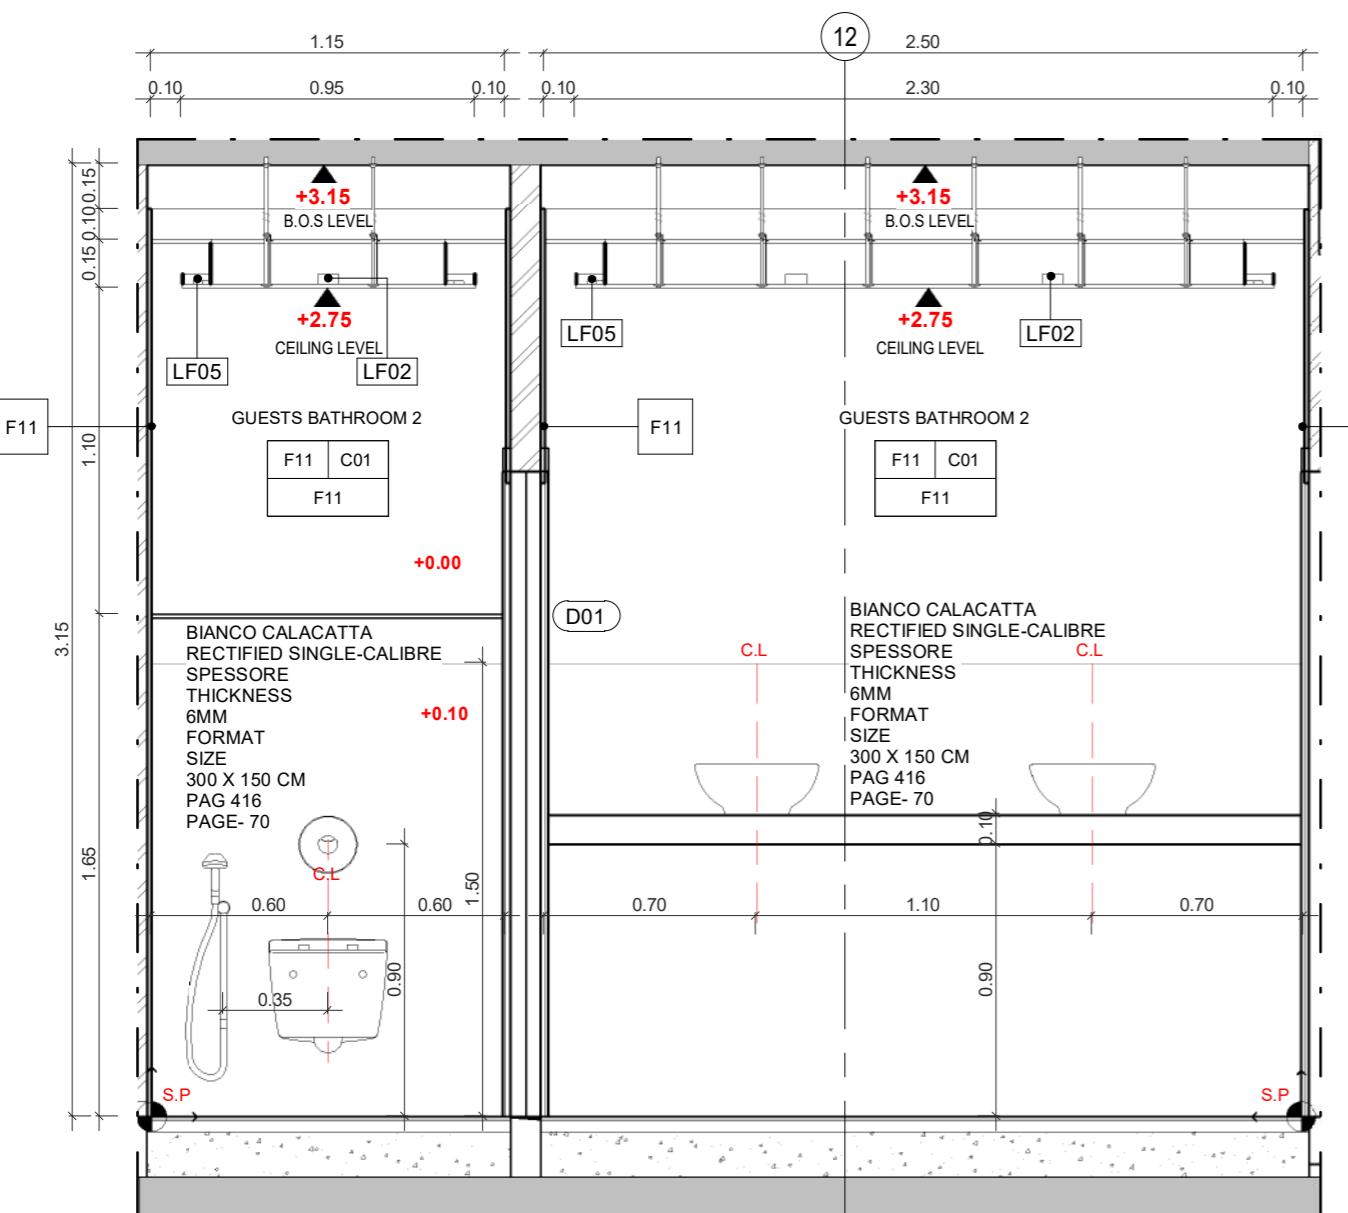

③ GUEST BATHROOM 2-ELEVATION 03

1 : 25

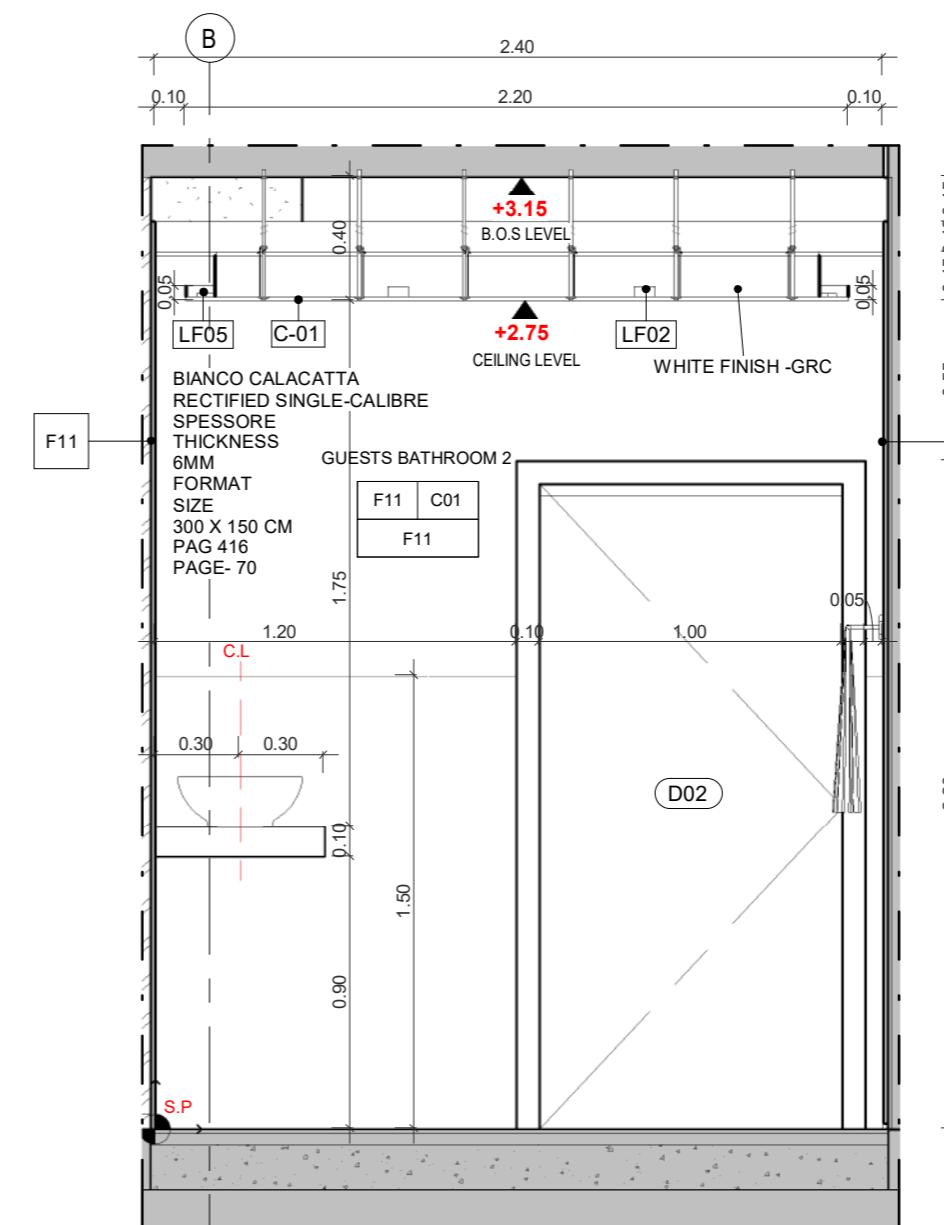

④ GUEST BATHROOM 2-ELEVATION 04

1 : 25

PROJECT NAME

APARTMENTS BUILDING

NOTES

FOR FINISHES REFER TO SHEETS:
ID-6000
ID-6001

FINISHES		FINISHES	
FINISH TAG	COMMENTS	FINISH TAG	COMMENTS
F01		F16	
F02		F17	LEATHER
F03	GOLD STONE	F18	PAINT-GOLD METAL EFFECT
F04	DARK WOOD	F19	
F05	DARK WOOD	F20	GREY STONE
F06	WOOD	F21	CONCRETE FINISH
F07	BLACK MARBLE	F09	GREY STONE
F08	BEIGE MARBLE	F10	WALL PAPER
F09		F11	
F10		F12	
F11		F13	BLACK PAINT
F12		F14	CALACATTA
F13		F15	BEIGE PAINT
F14		F16	
F15		F17	
F16		F18	
F17		F19	
F18		F20	
F19		F21	
F20		F22	
F21		F23	SWIMMING POOL WALL FINISHES

SPOT RECESSED LIGHT
PENDANT LIGHT
HIDDEN LIGHT
CHANDELIER
WALL MOUNTED
NEON RECTANGULAR

Project Type	Residential
Owner	Khalid Khadir Hasan AL-Saeed
Location	Amman
Plot No.	1659
Basin No.	19
Designed by	A.Shaker Khulief 4809





SHEET NAME

BASEMENT FLOOR- TOILET

ID-4040

Date 08/10/2019

Scale As indicated

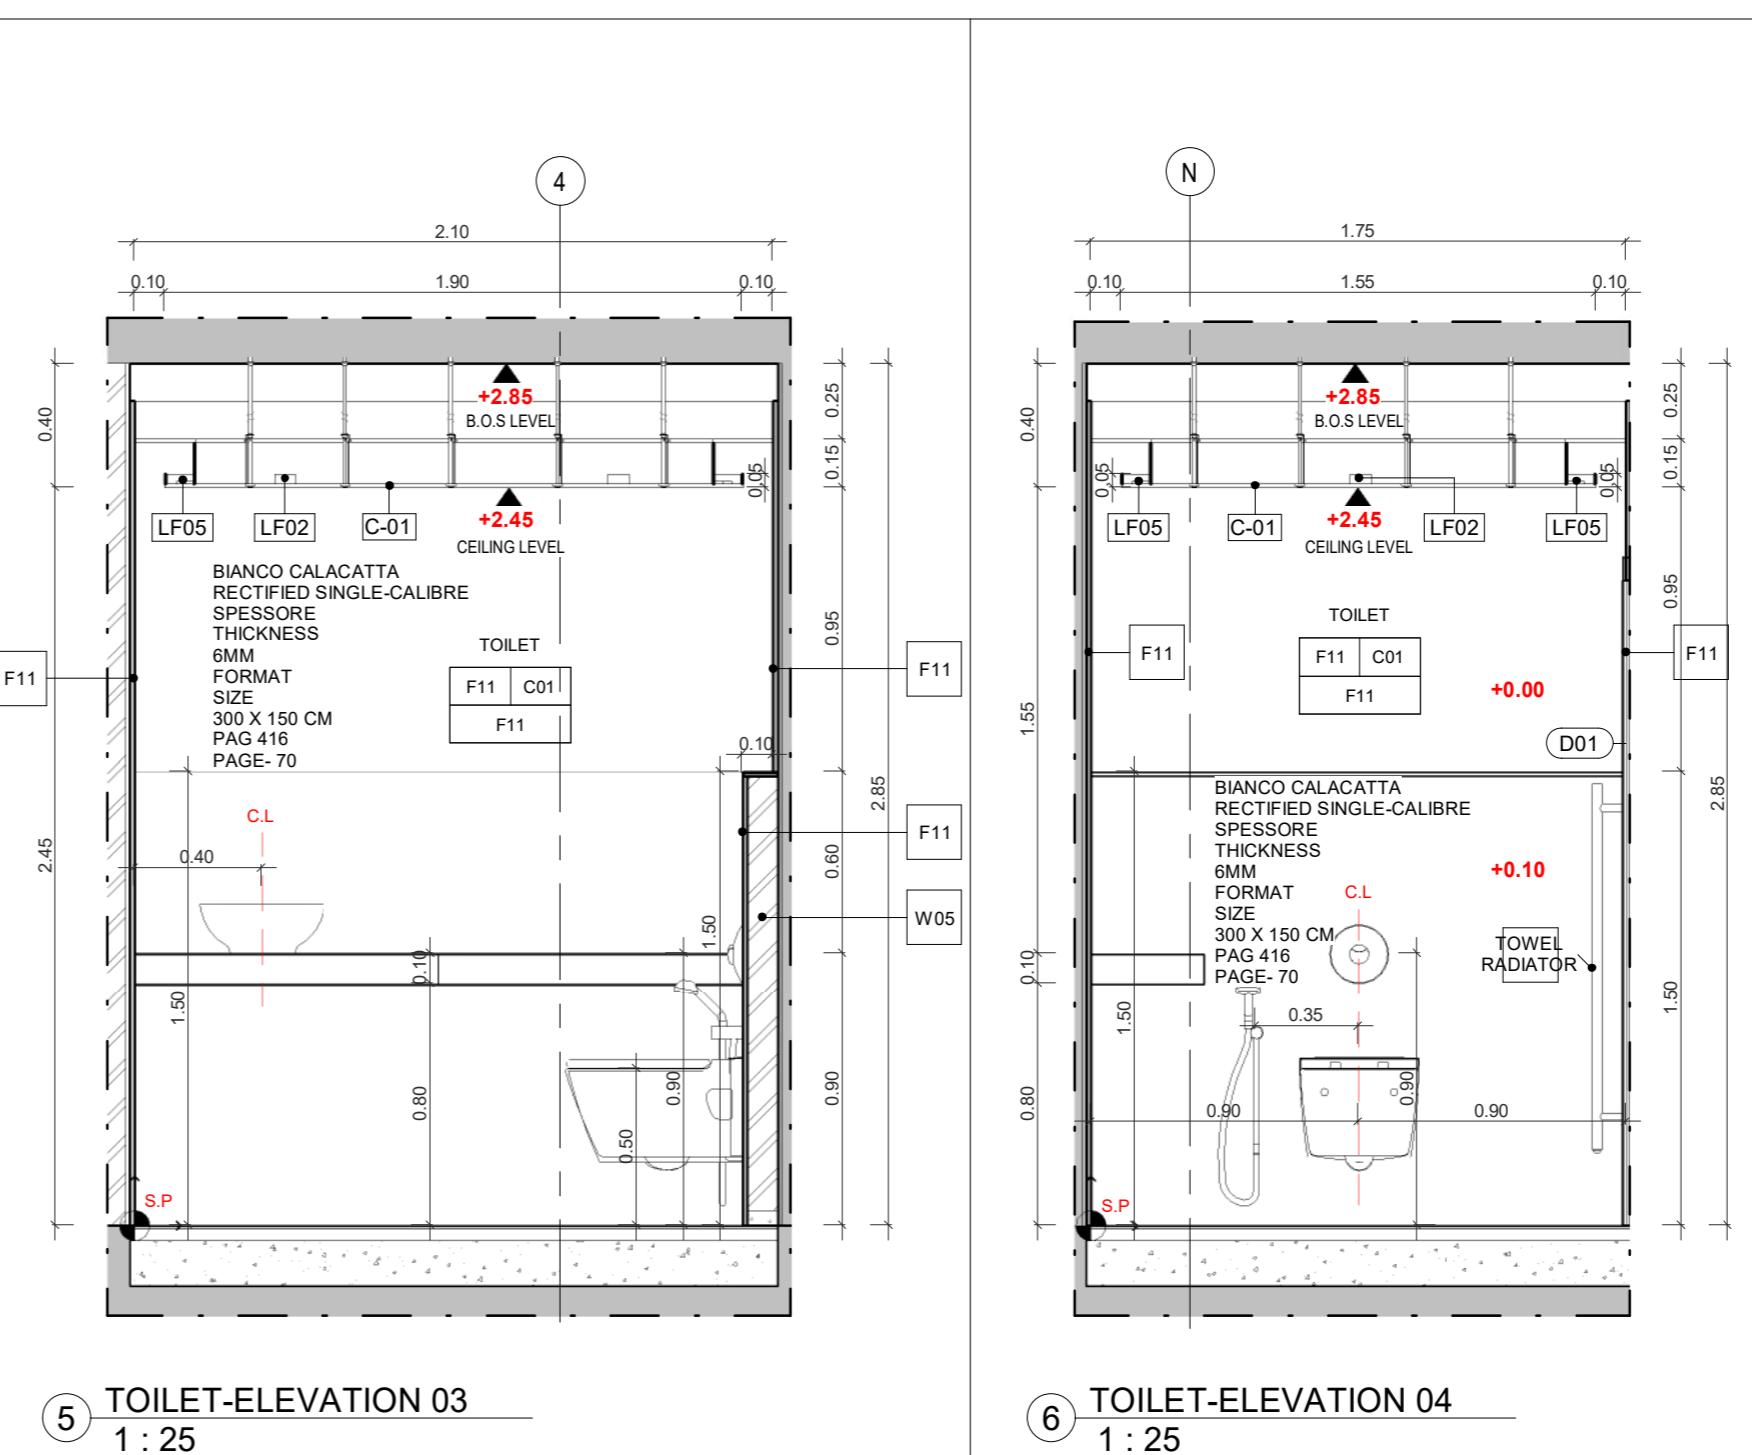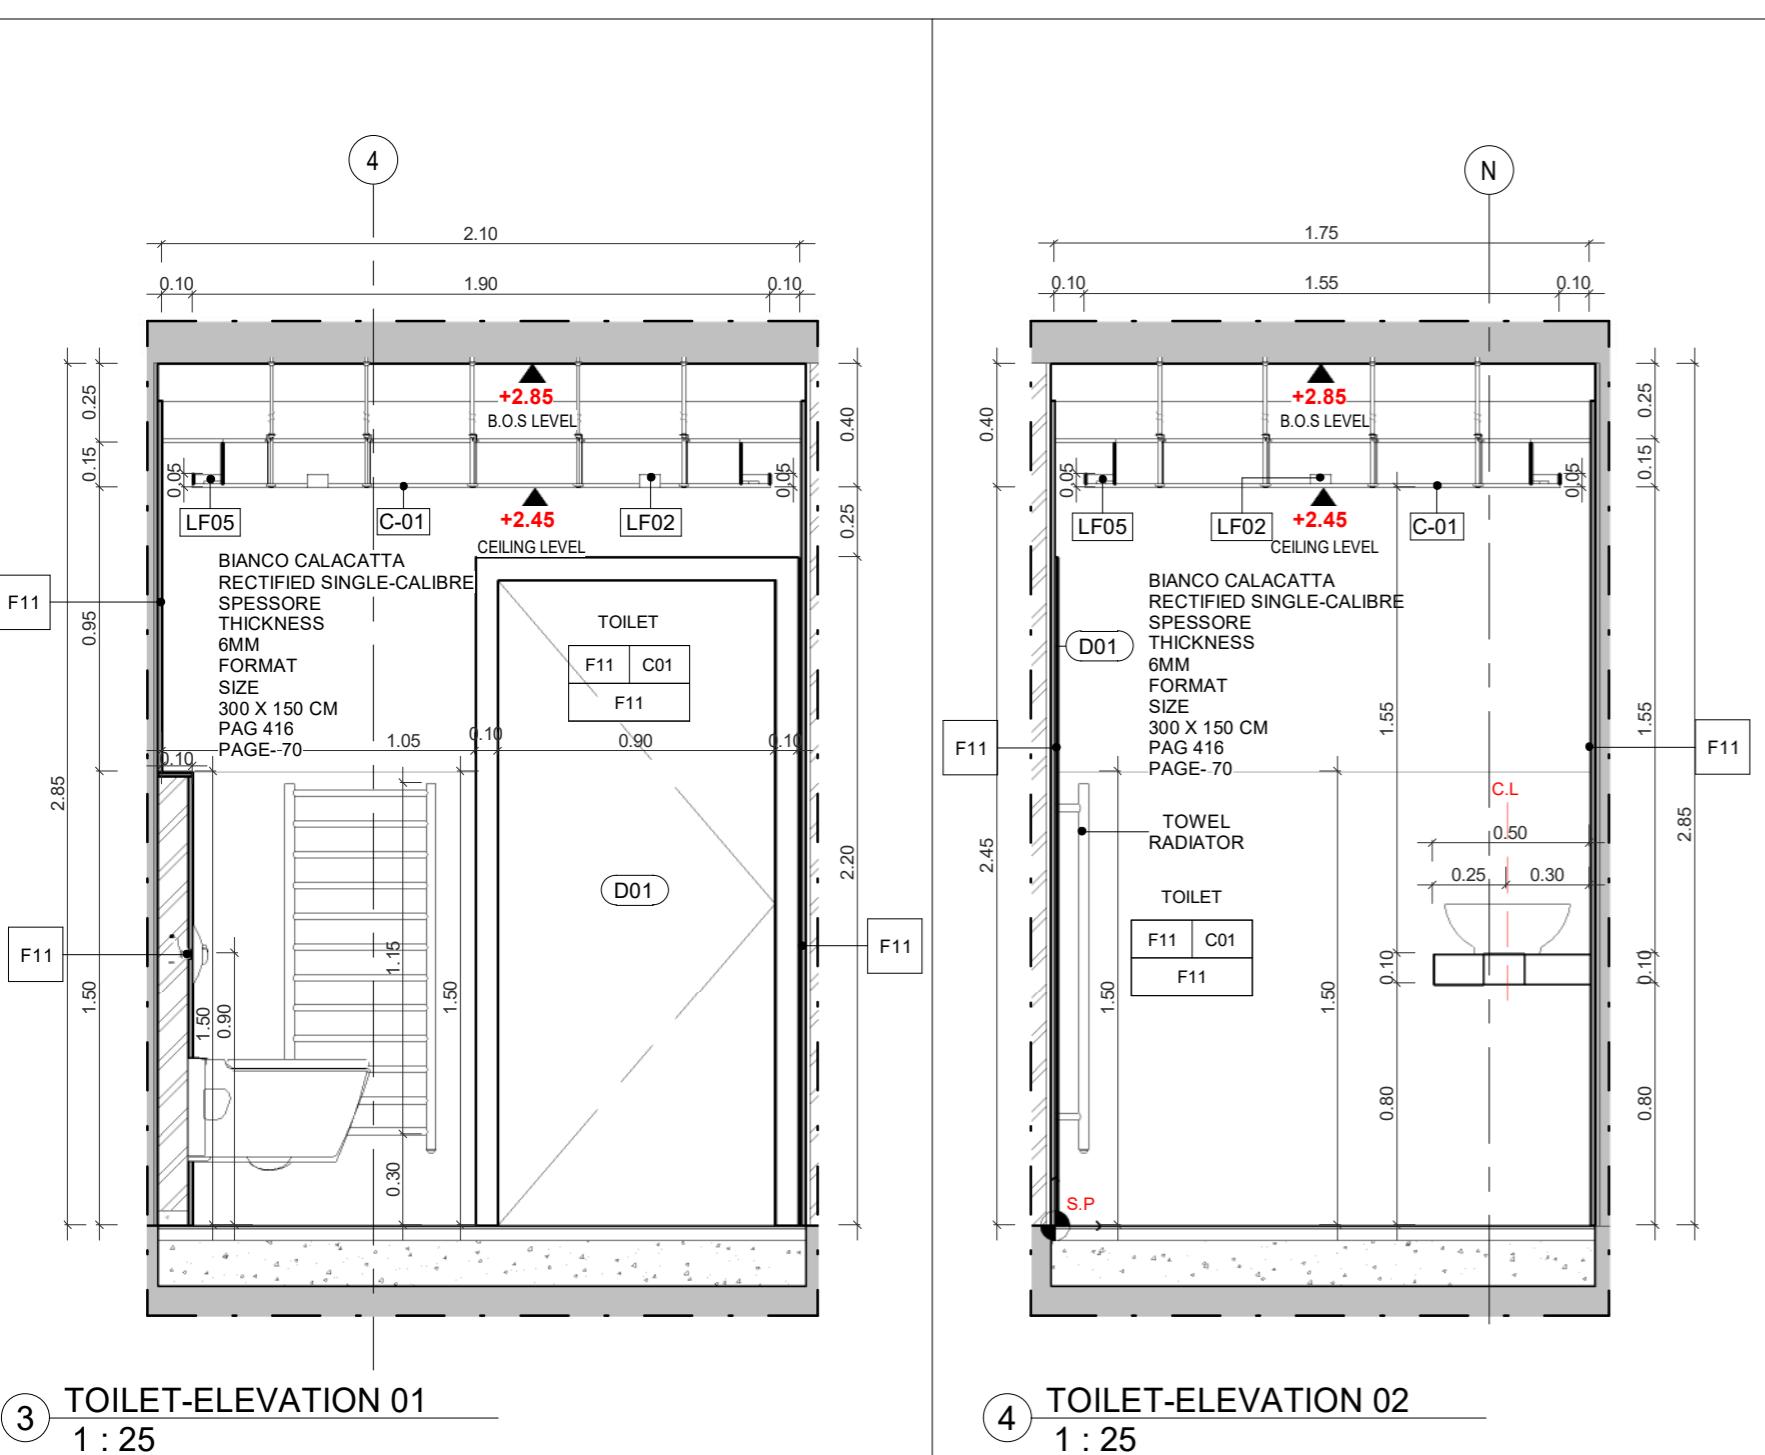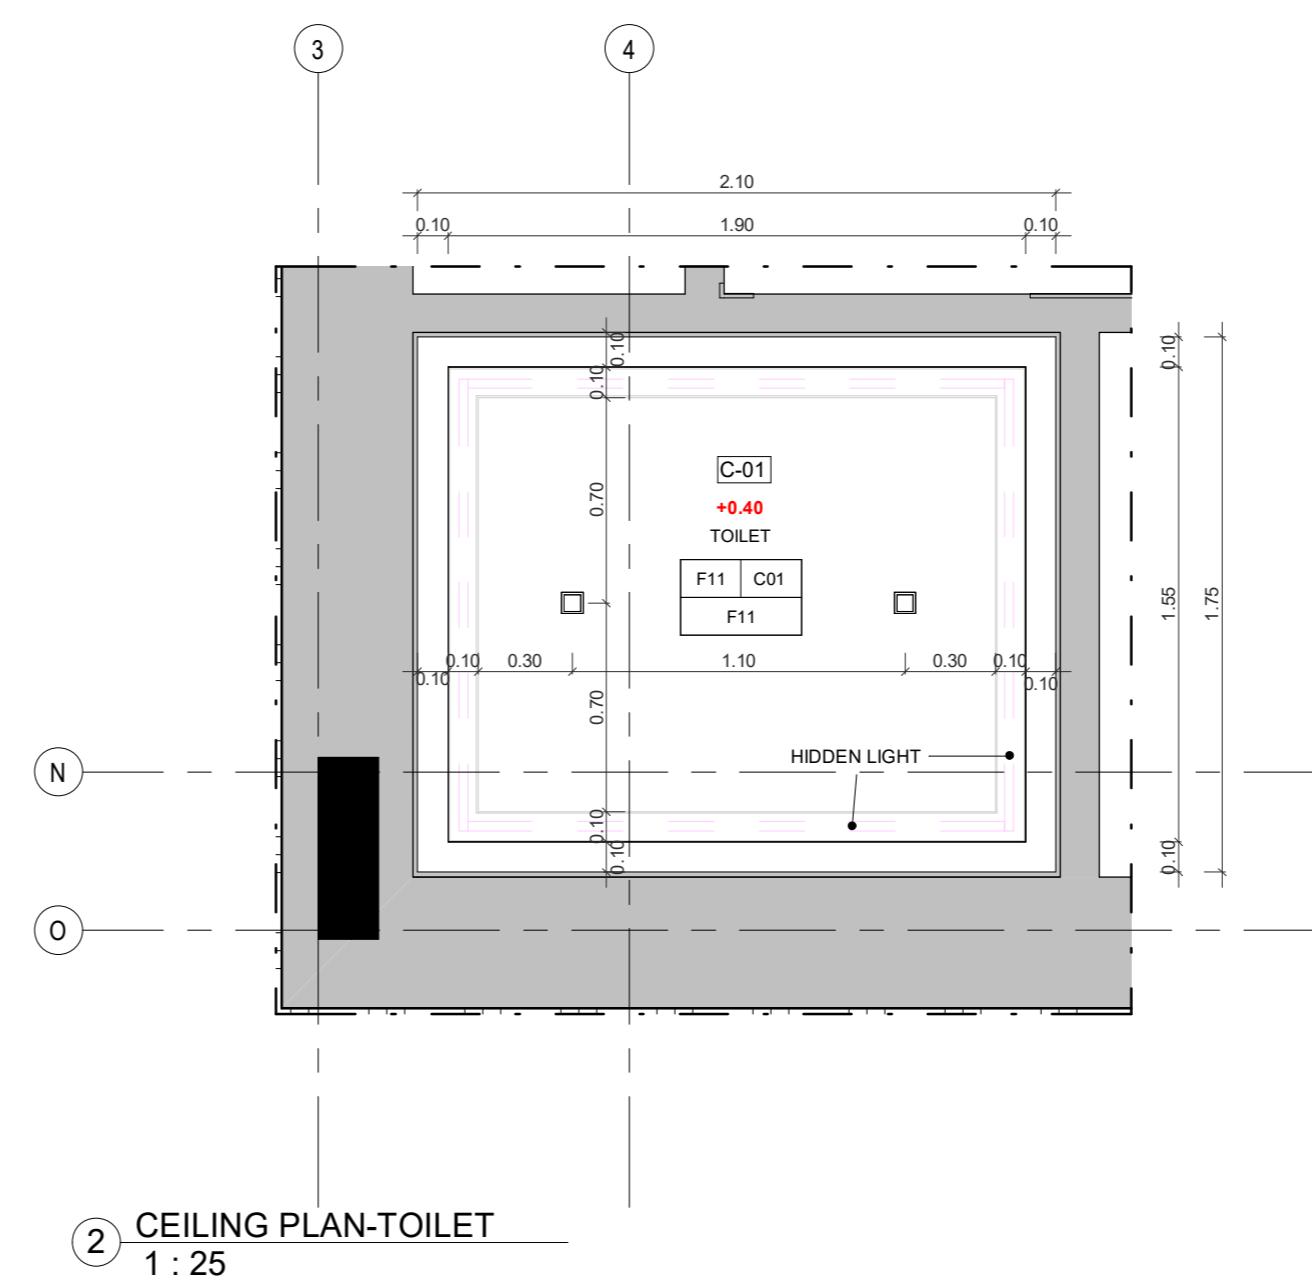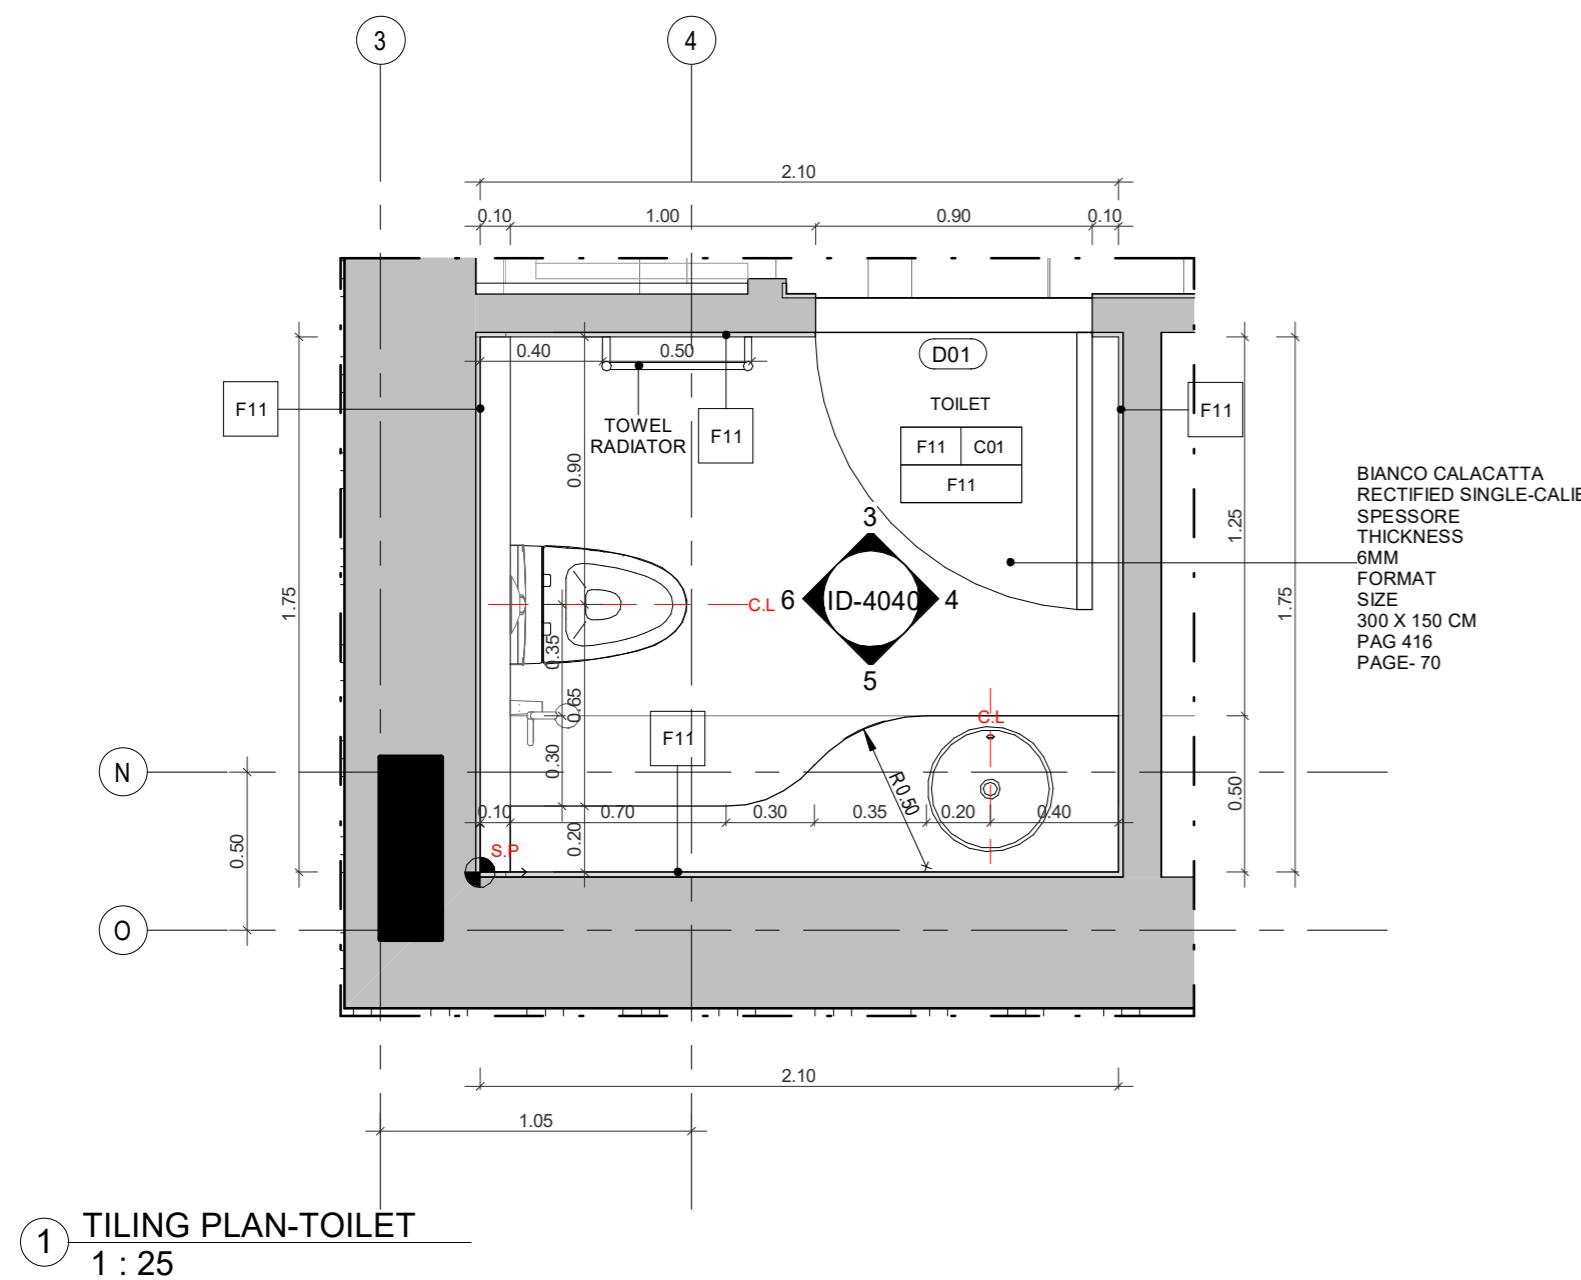

PROJECT NAME

APARTMENTS BUILDING

NOTES

SHOT 1



SHOT 2



Project Type	Residential
Owner	Khalid Khadir Hasan AL-Saeed
Location	Amman
Plot No.	1659
Basin No.	19
Designed by	A.Shaker Khulief 4809

SHEET NAME
SALON & DINING-SHOTS

ID-4100

Date 08/10/2019
Scale

PROJECT NAME

APARTMENTS BUILDING

NOTES

FOR FINISHES REFER TO SHEETS:
ID-6000
ID-6001

ROOM NAME

FLOOR FINISH CEILING FINISH

WALL FINISH

FINISHES SCHEDULE		FINISHES SCHEDULE			
Material:	Mark	DESCRIPTION	Material:	Mark	DESCRIPTION
F01		WHITE PAINT	F15		BEIGE PAINT
F02		GOLD WOOD	F16		TRAVERTINO MARBLE
F03		GOLD STONE	F17		DARK WOOD
F04			F18		DECORATIVE STONE WOOD
F05			F06		PAINT GOLD METAL EFFECT
F06			F07		BLACK MARBLE
F07			F08		DECO WOOD
F08			F09		BEIGE MARBLE
F09			F10		GREY STONE
F10			F11		CONCRETE FINISH
F11			F12		KITCHENETTE WOOD
F12			F13		SWIMMING POOL MARBLE
F13			F14		BLACK PAINT
F14			F15		CALCAGNA
F15			F16		PARQUET
F16			F17		WHITE FINISH GRC

Project Type Residential

Owner Khalid Khadir Hasan AL-Saeed

Location Amman

Plot No. 1659

Basin No. 19

Designed by A.Shaker Khulief 4809






SHEET NAME

GROUND FLOOR- SALON & DINING ROOM

ID-4101

Date 08/10/2019

Scale As indicated

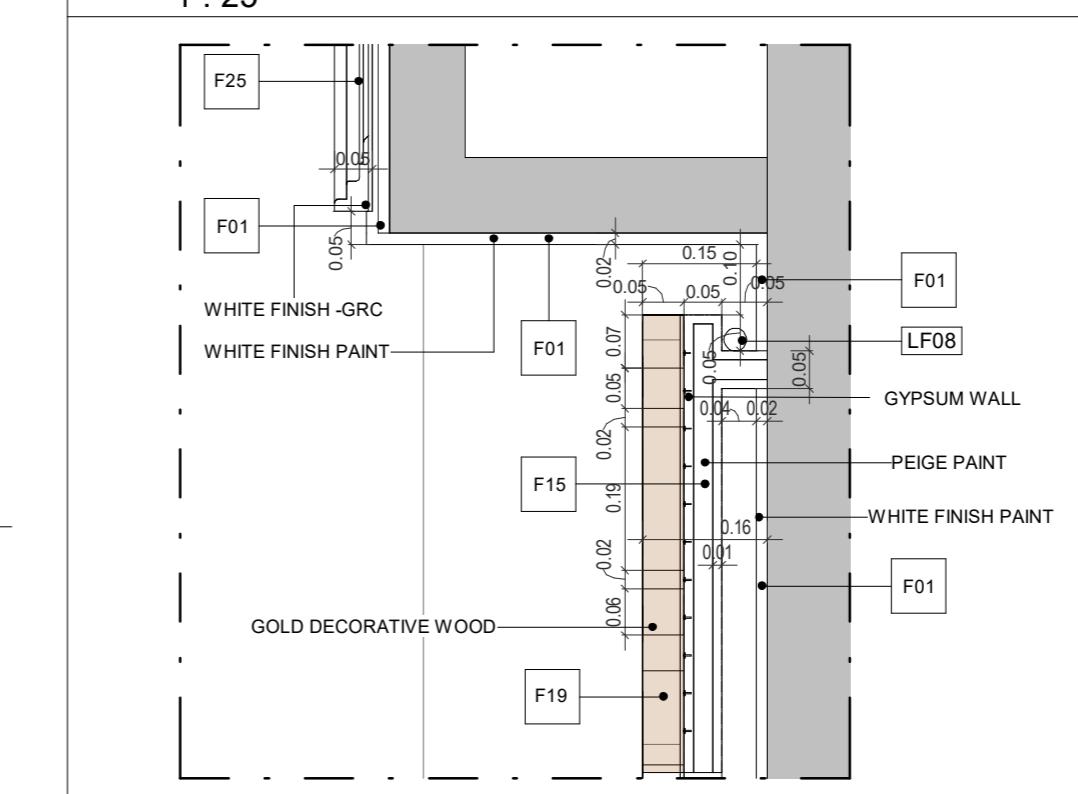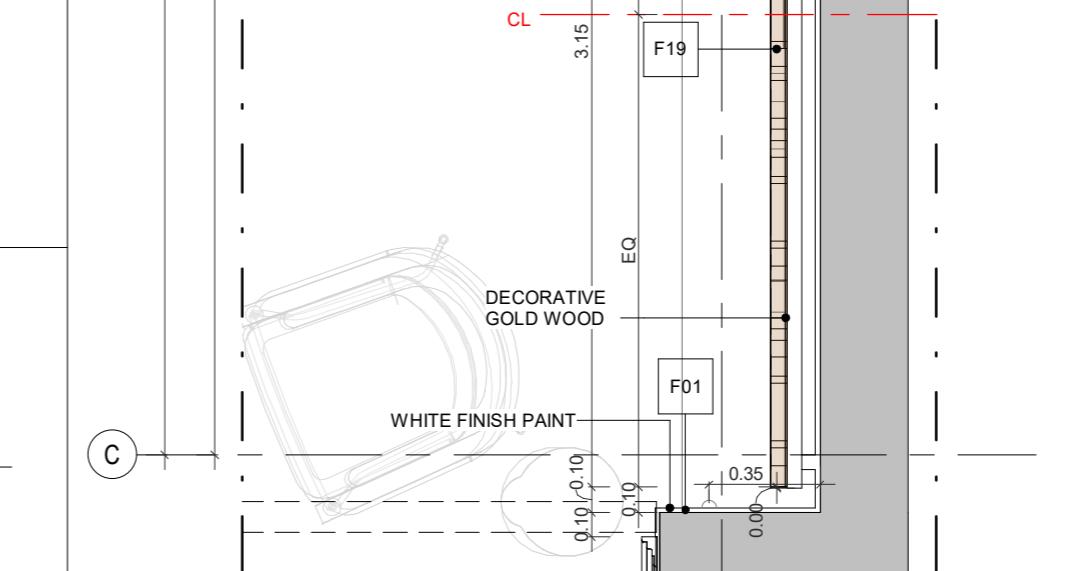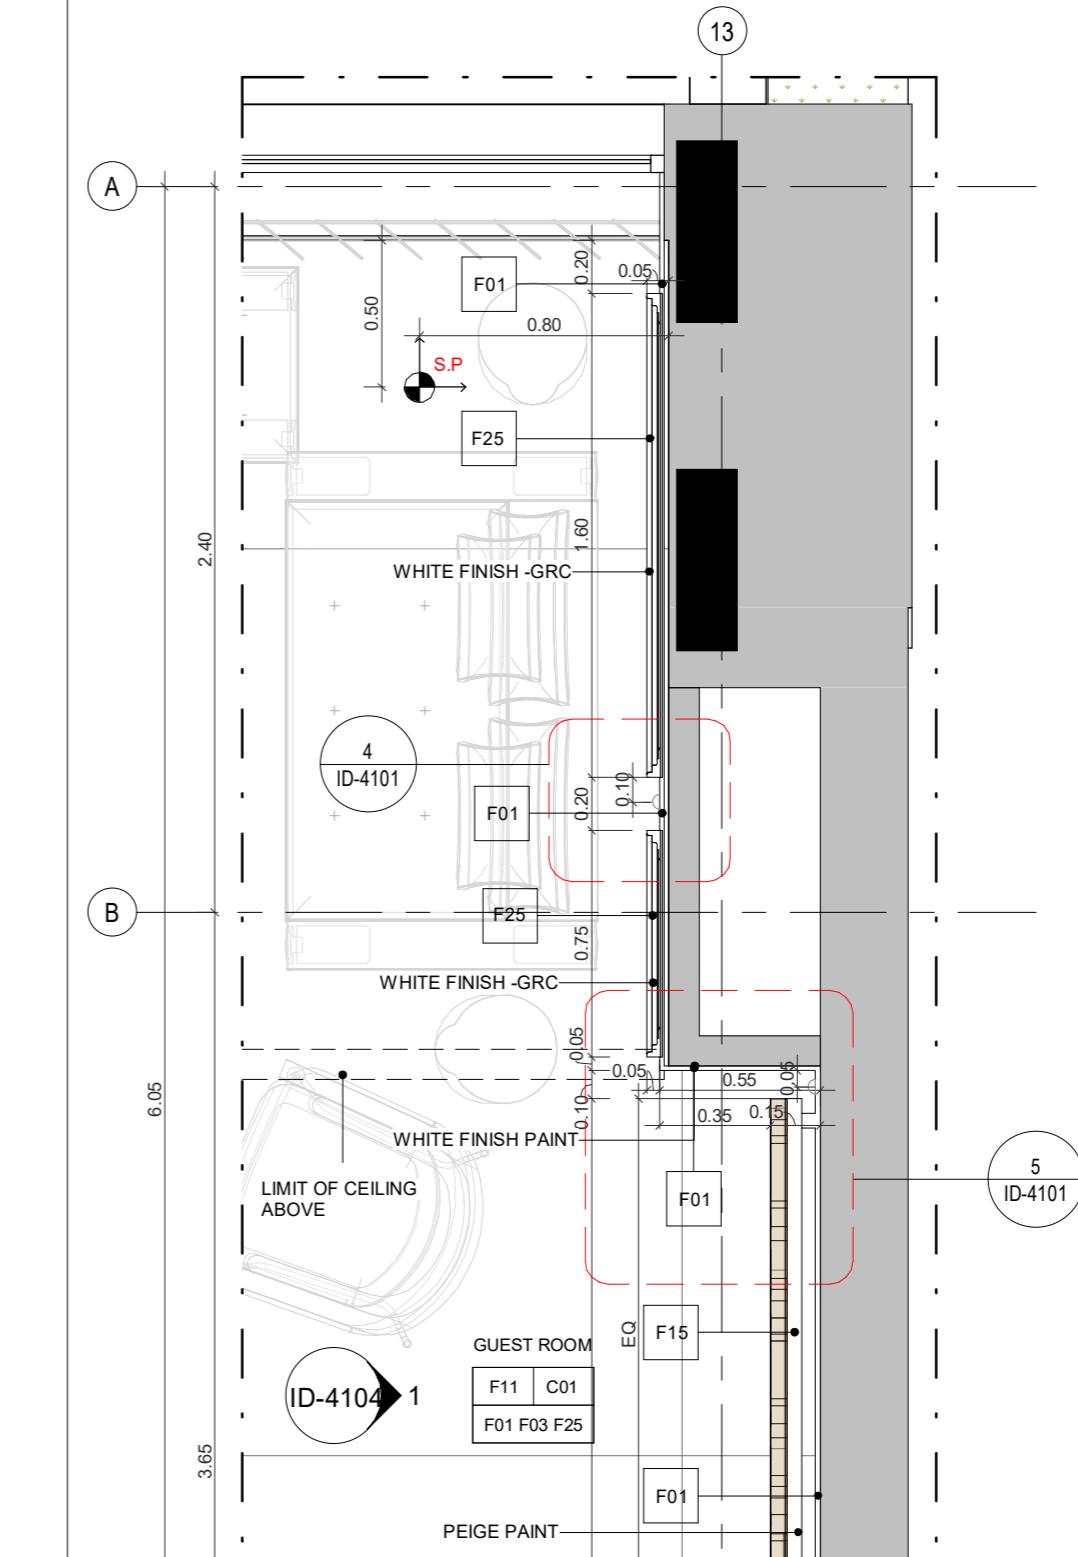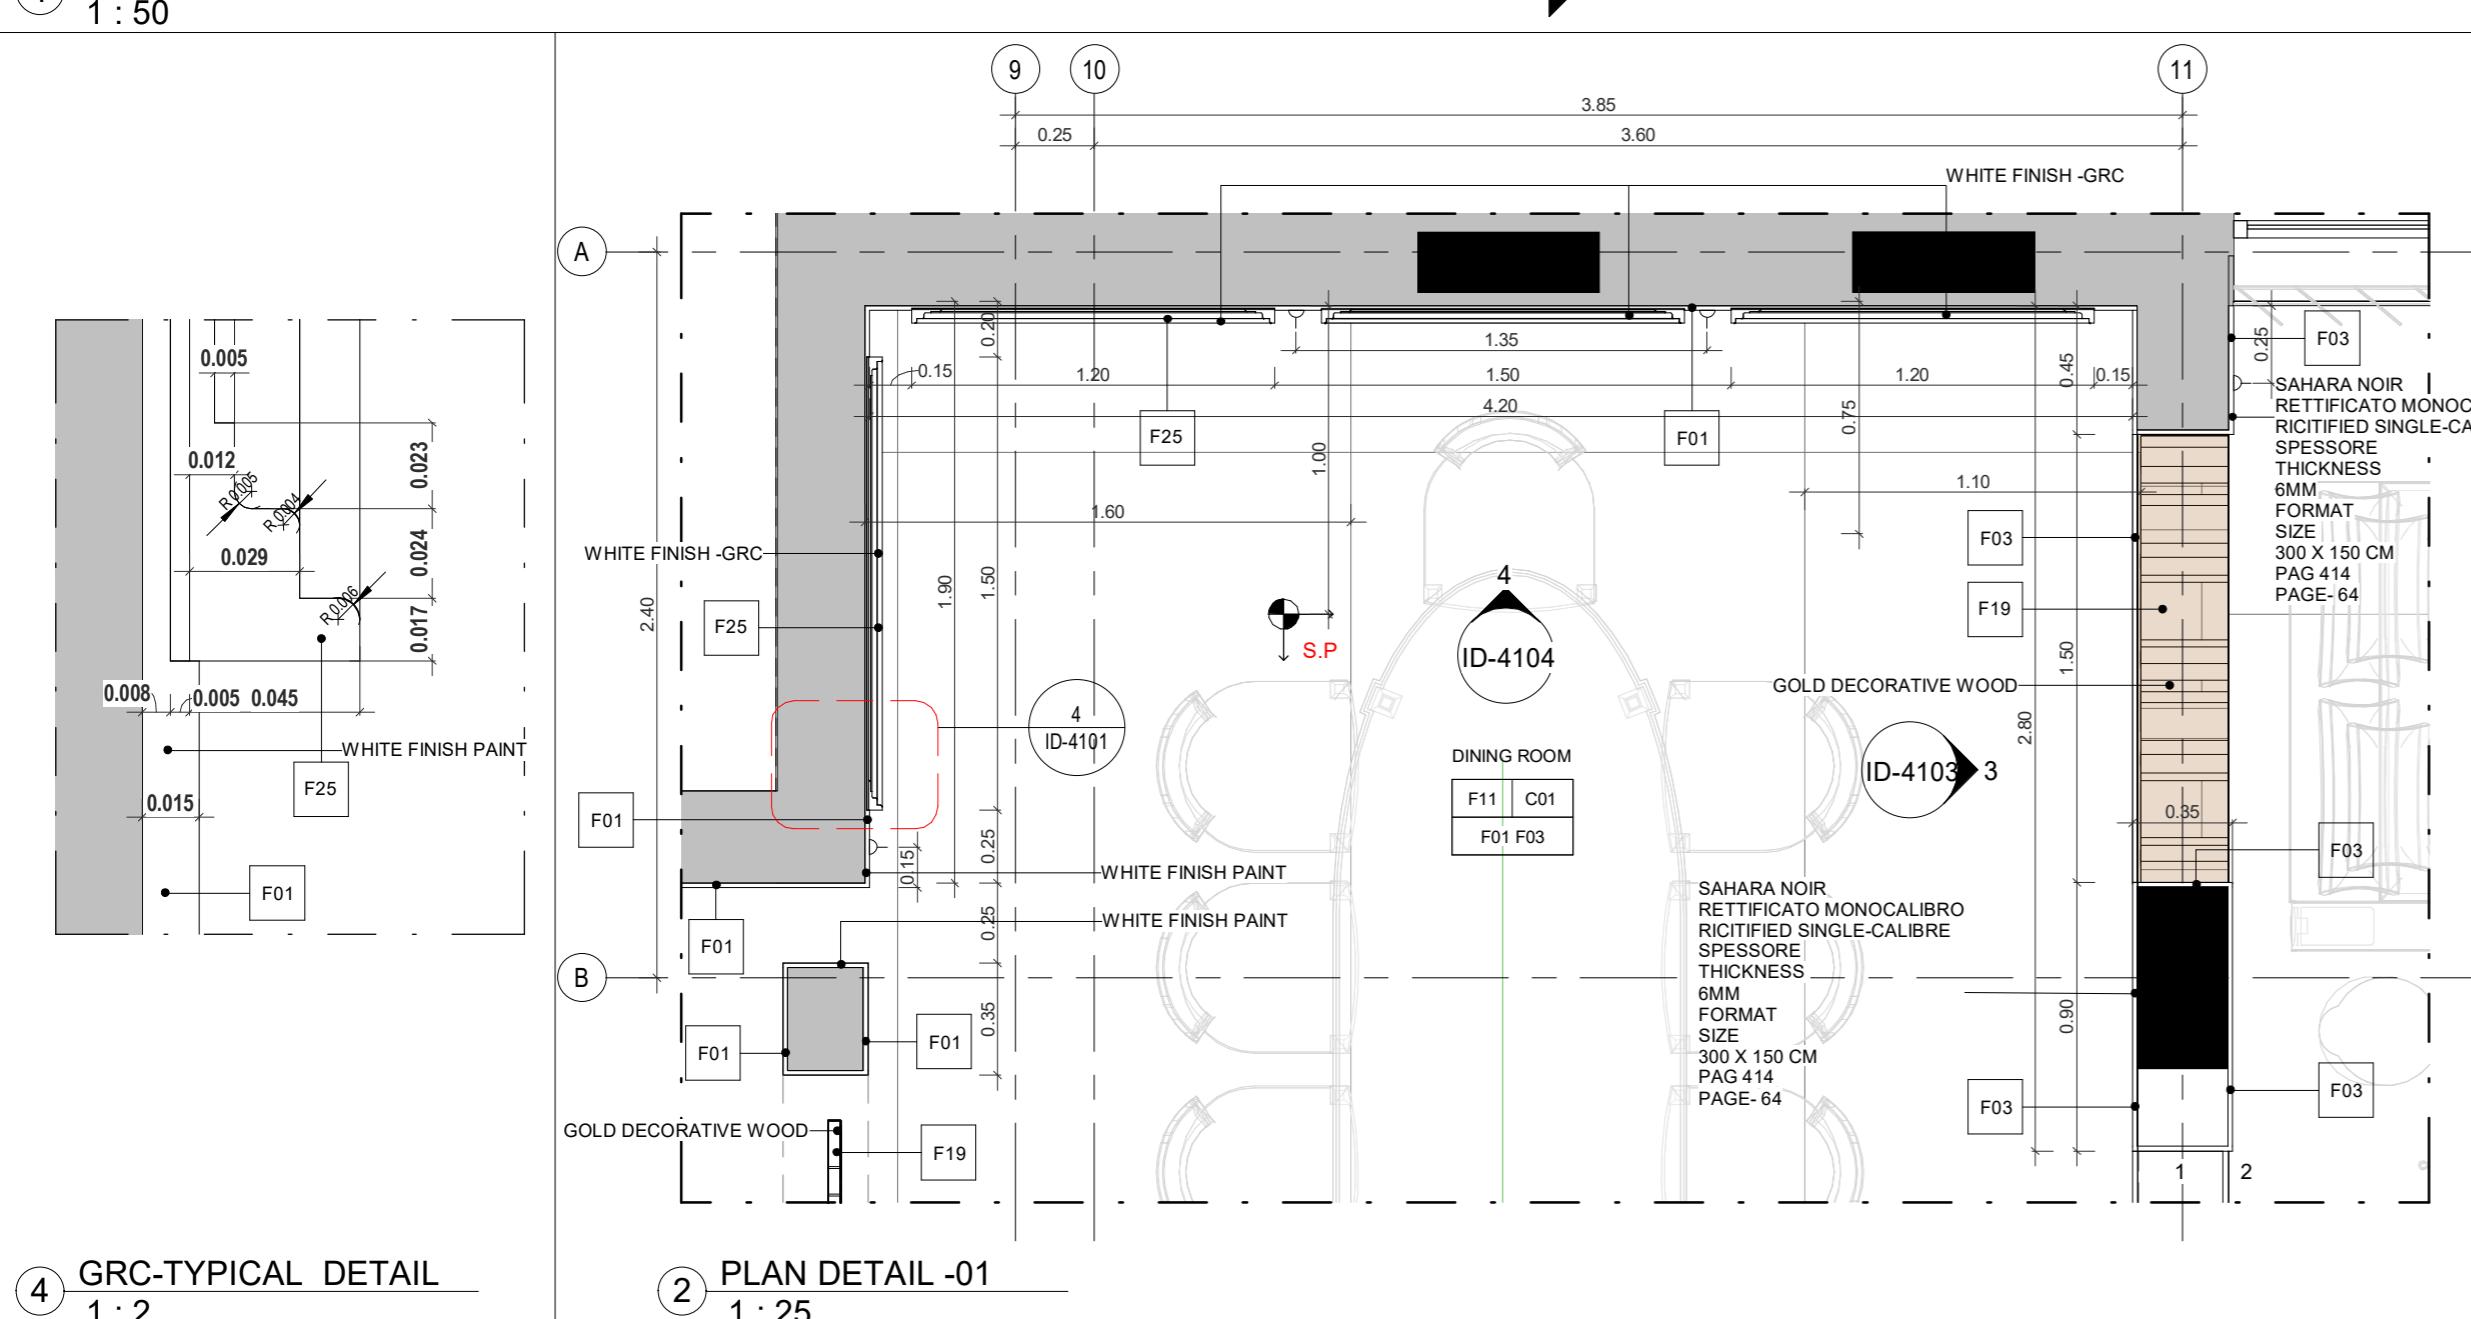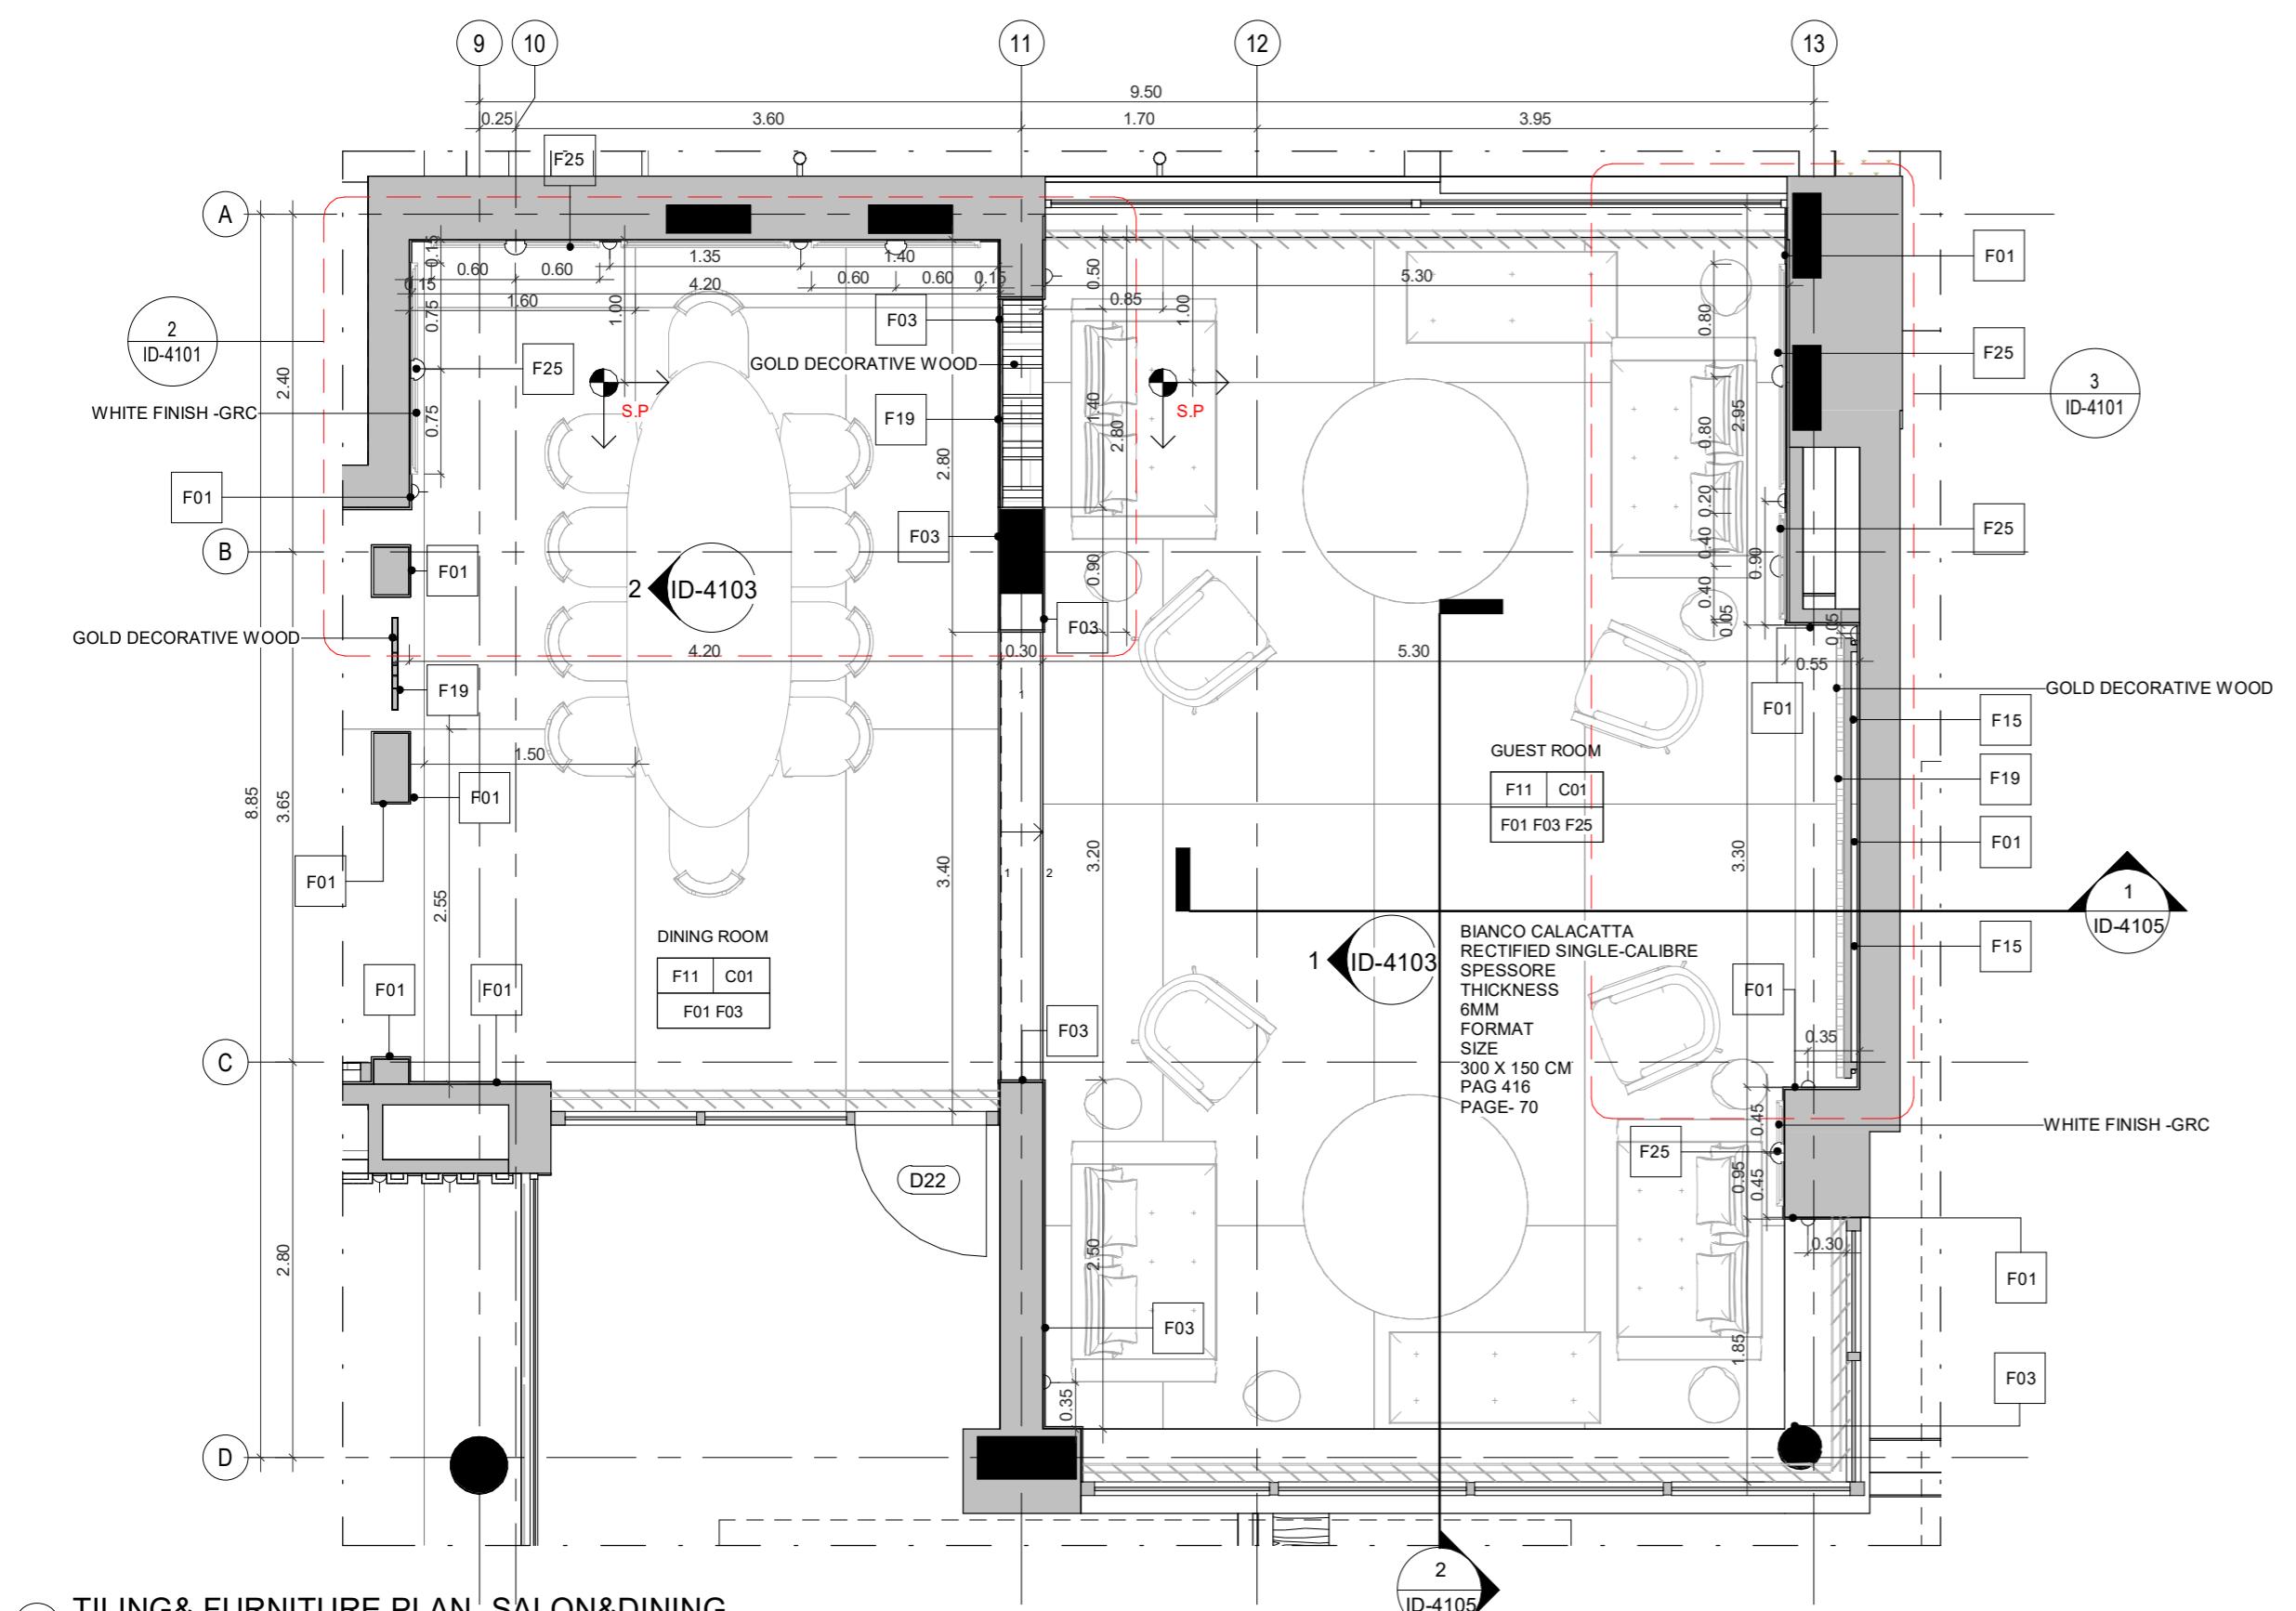

PROJECT NAME

APARTMENTS BUILDING

NOTES

FOR FINISHES REFER TO SHEETS:
ID-6000
ID-6001

FINISHES SCHEDULE	
Material: Mark	DESCRIPTION
F01	WHITE PAINT
F02	GOLD WOOD
F03	GOLD STONE
F04	DARK WOOD
F05	DECORATIVE STONE
F06	WOOD
F07	BLACK MARBLE
F08	BEIGE MARBLE
F09	GREY STONE
F10	WALL PAPER
F11	KITCHENETTE WOOD
F12	SWIMMING POOL MARBLE
F13	BLACK PAINT
F14	CALCATTAA
FINISHES SCHEDULE	
Material: Mark	DESCRIPTION
F15	BEIGE PAINT
F16	TRAVERTINO MARBLE
F17	LEATHER
F18	PAINT GOLD METAL EFFECT
F19	DECORATIVE WOOD
F20	GREY STONE
F21	CONCRETE FINISH
F22	KITCHENETTE WOOD
F23	SWIMMING POOL WALL FINISH
F24	PARQUET
F25	WHITE FINISH GRC


	SPOT RECESSED LIGHT
	PENDANT LIGHT
	HIDDEN LIGHT
	CHANDELIER
	WALL MOUNTED
	NEON RECTANGULAR

Project Type	Residential
Owner	Khalid Khadir Hasan AL-Saeed
Location	Amman
Plot No.	1659
Basin No.	19
Designed by	A.Shaker Khulief 4809


SHEET NAME	GROUND FLOOR- SALON & DINING ROOM
------------	-----------------------------------




ID-4102

Date 08/10/2019
Scale As indicated

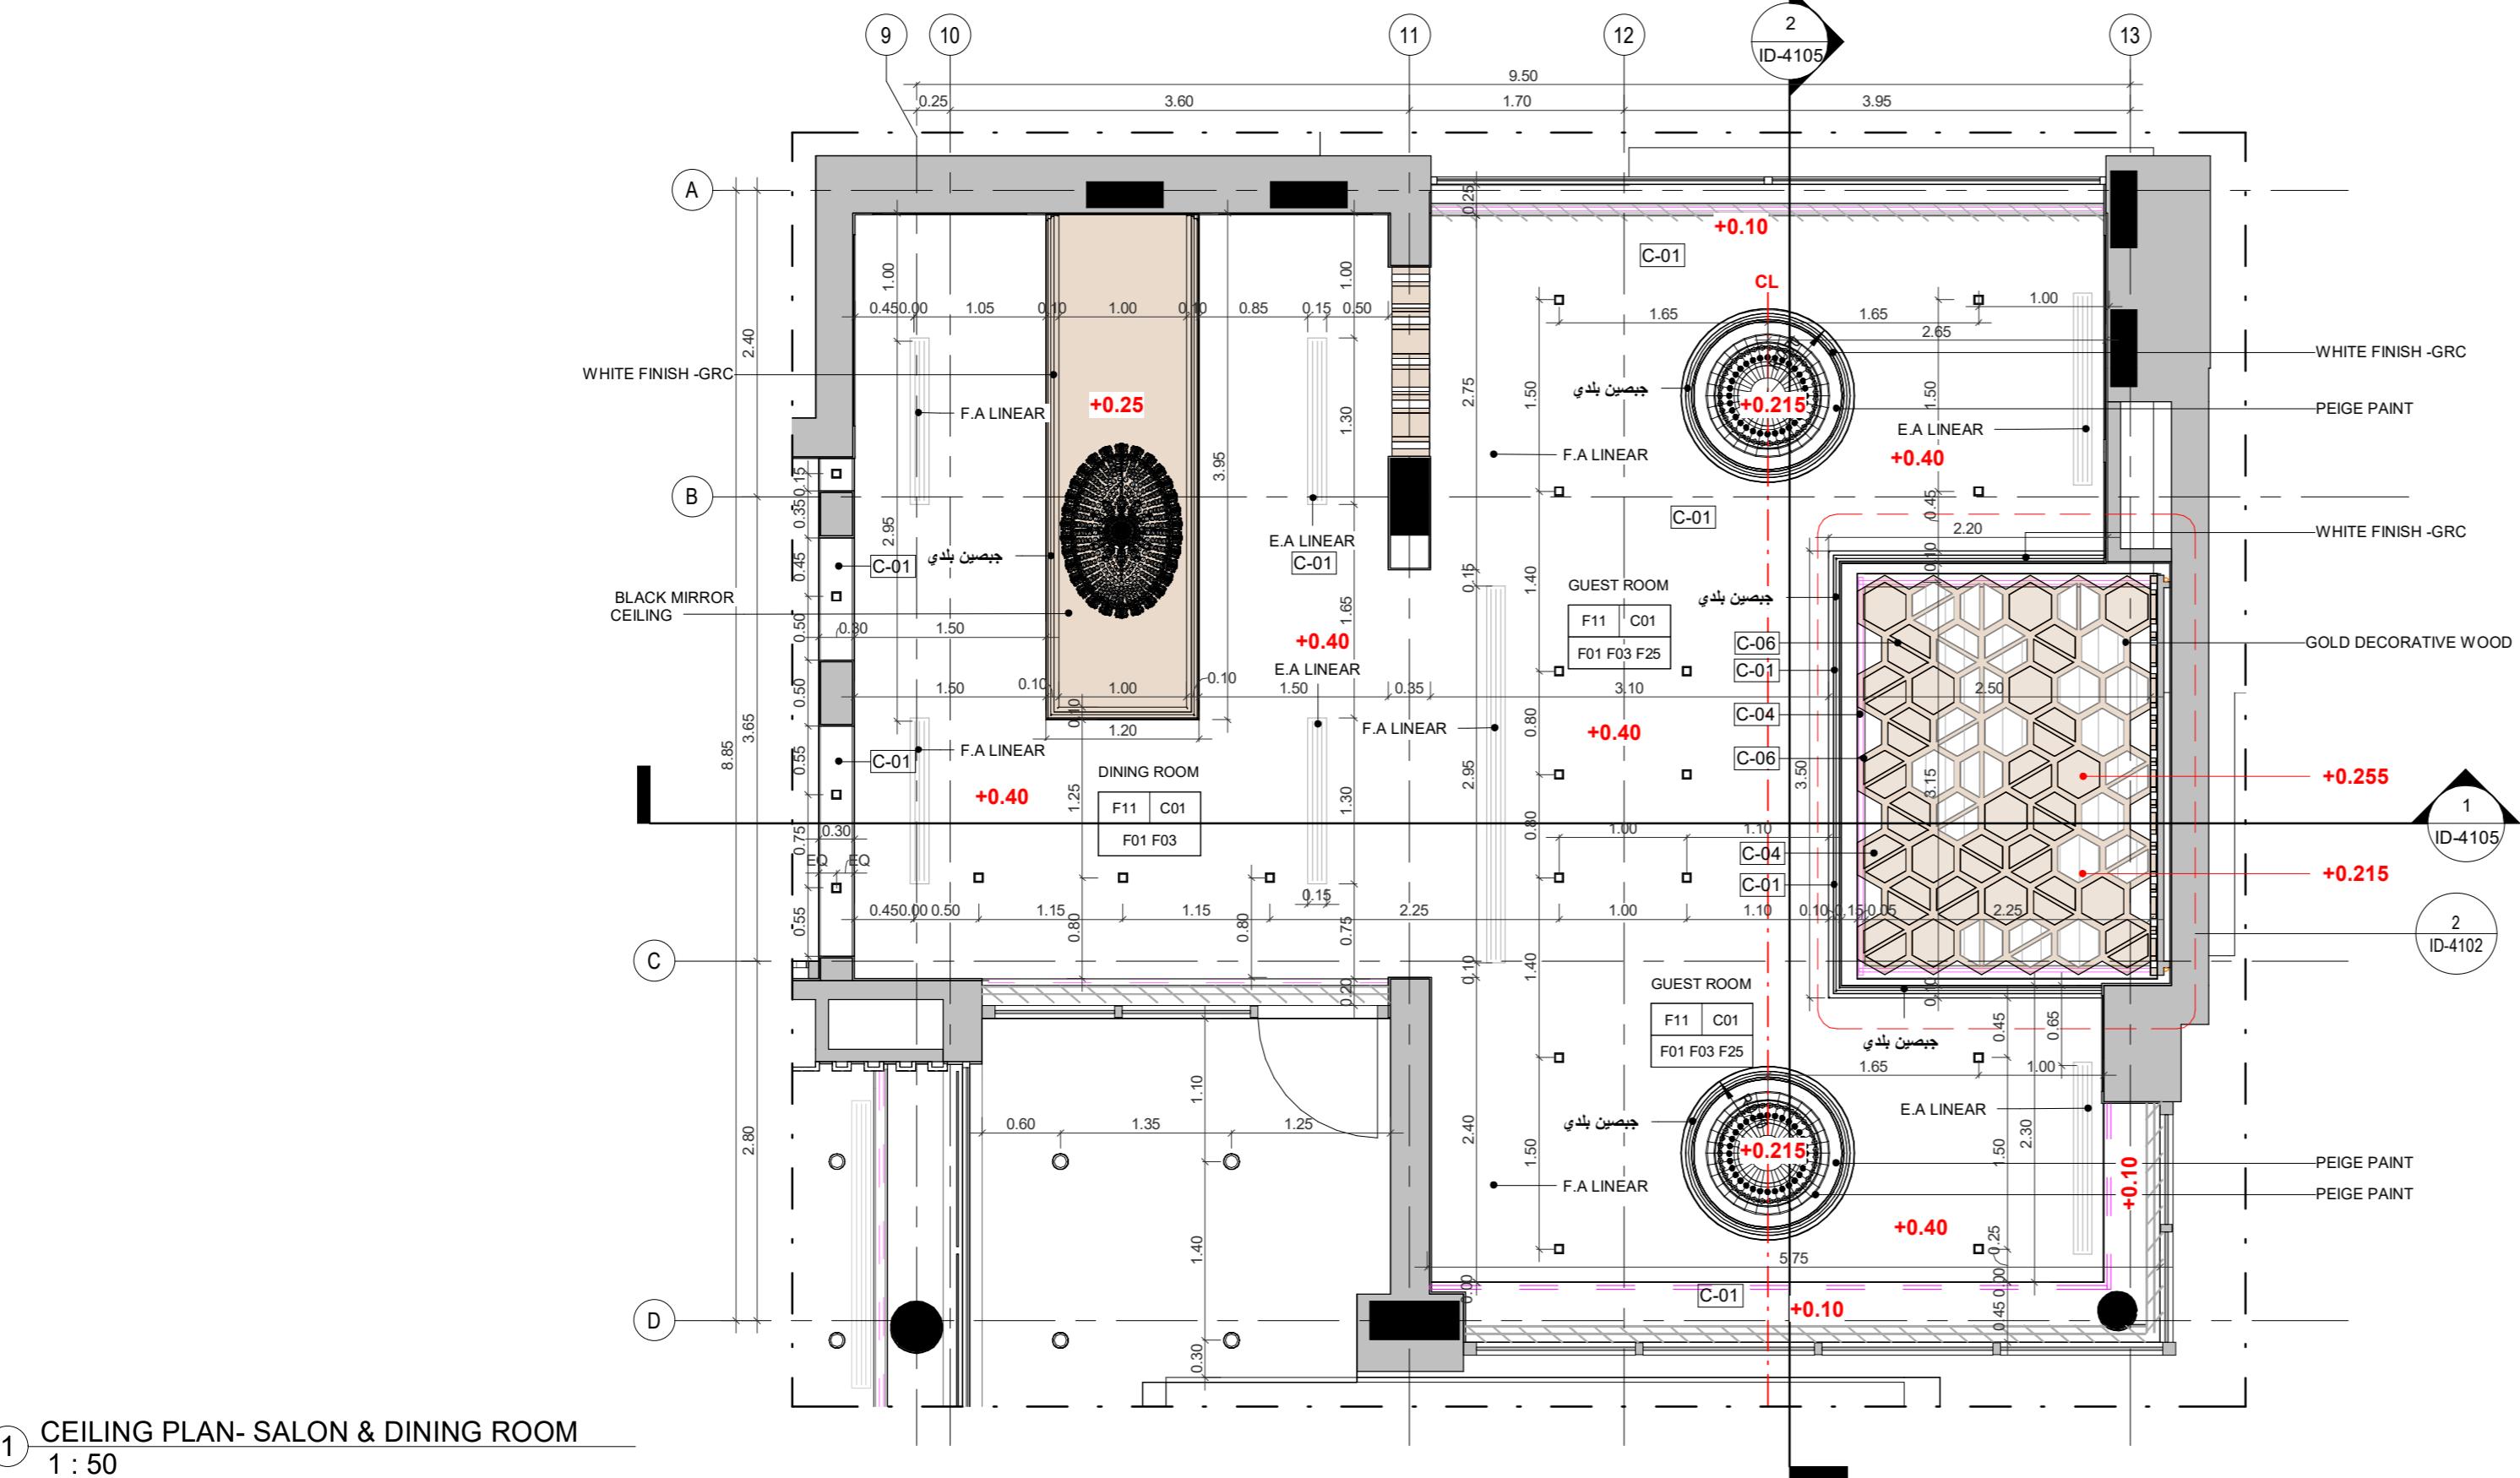

1 CEILING PLAN- SALON & DINING ROOM
1 : 50

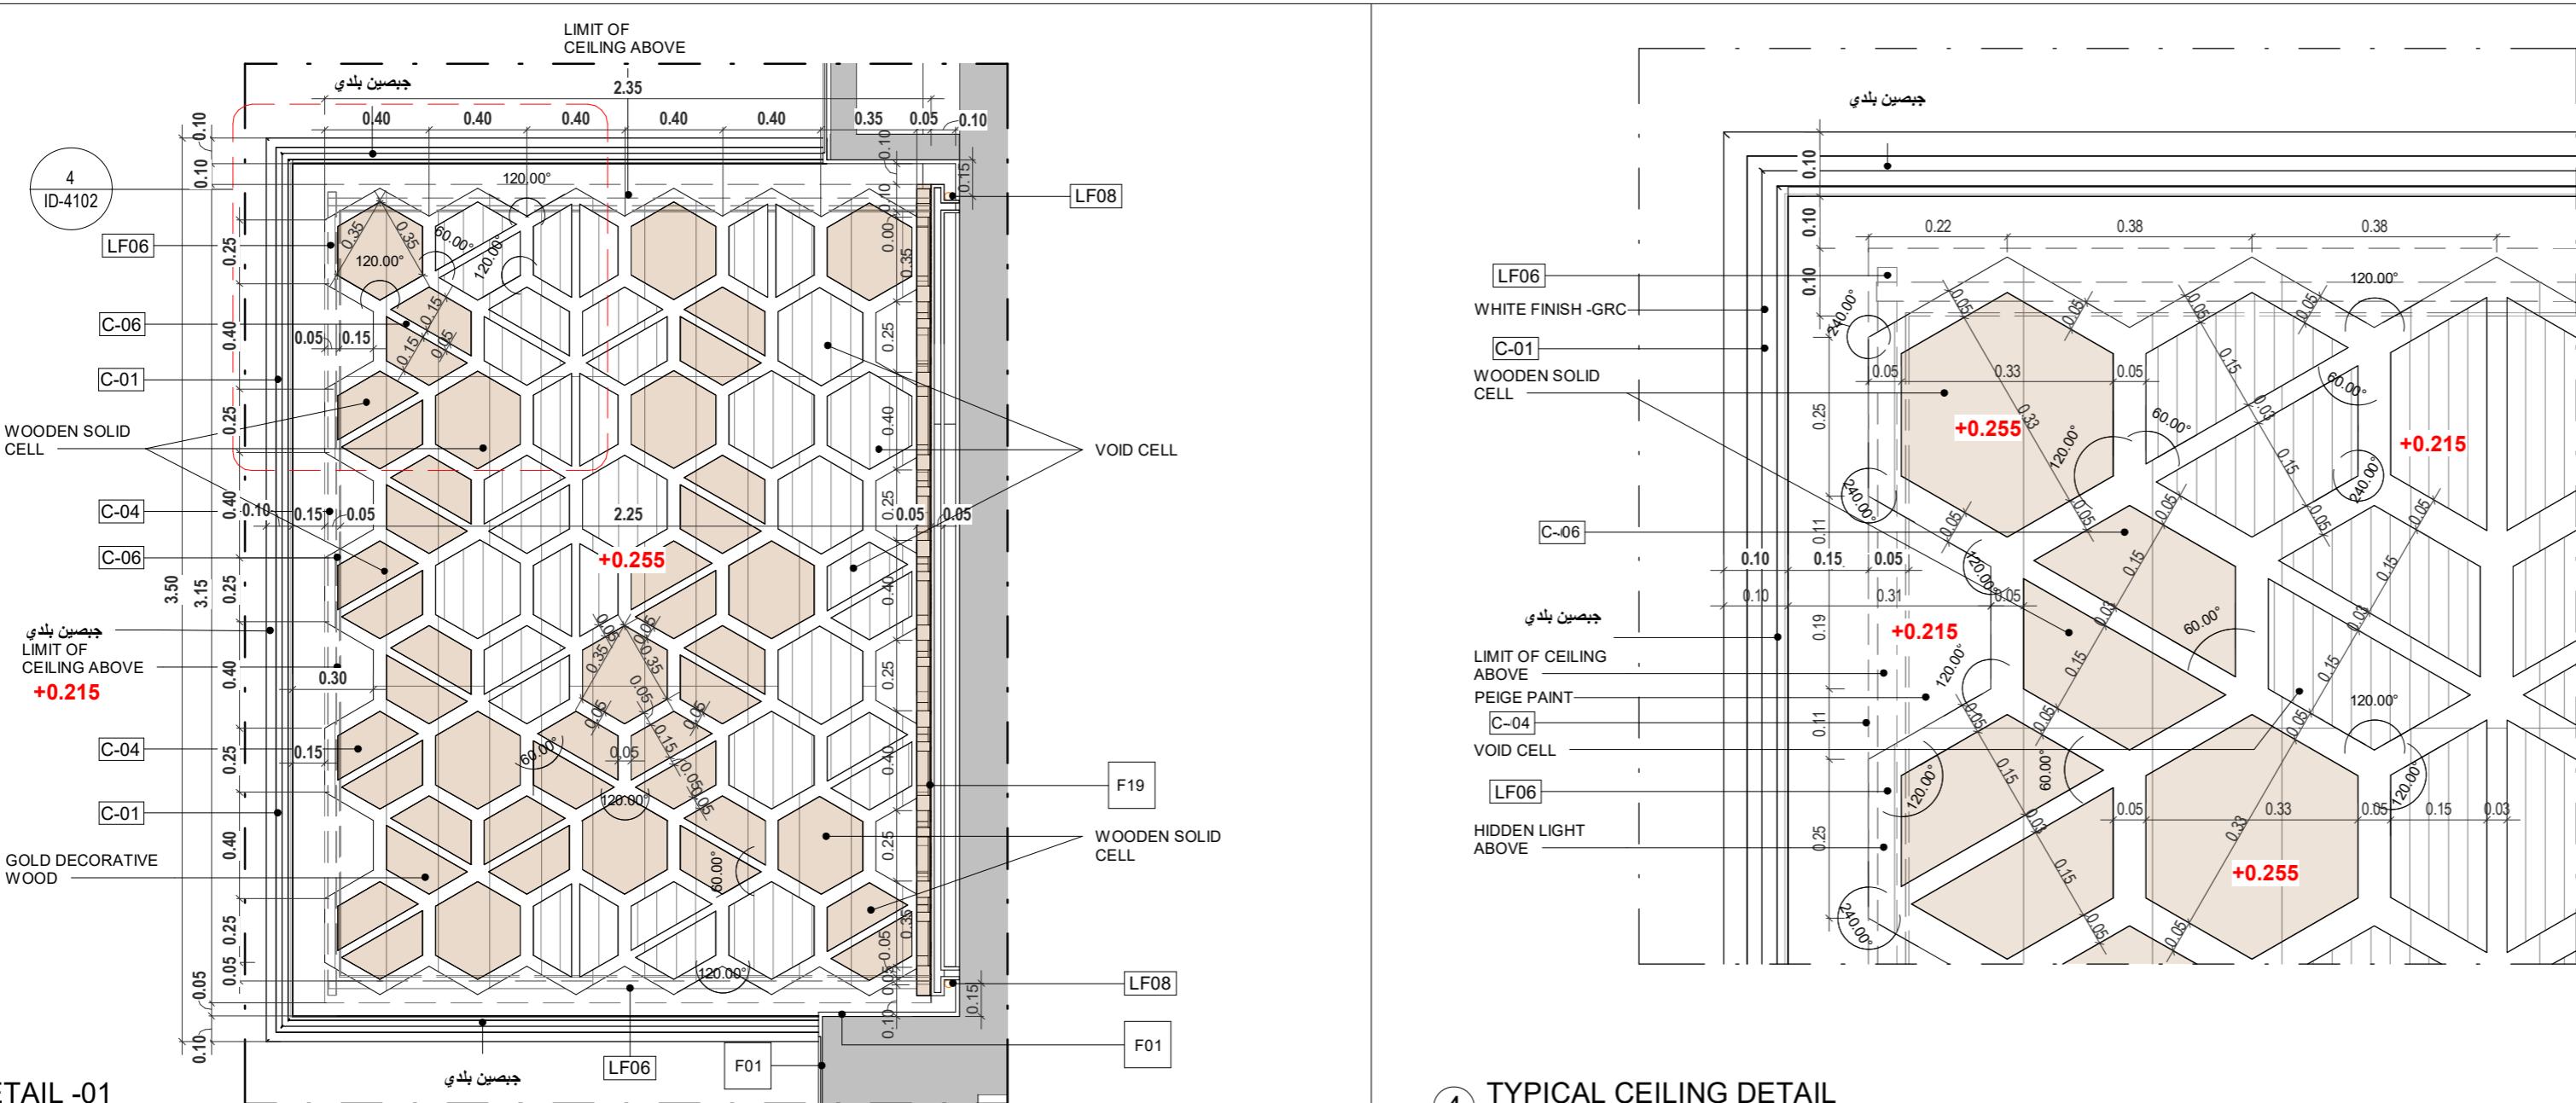

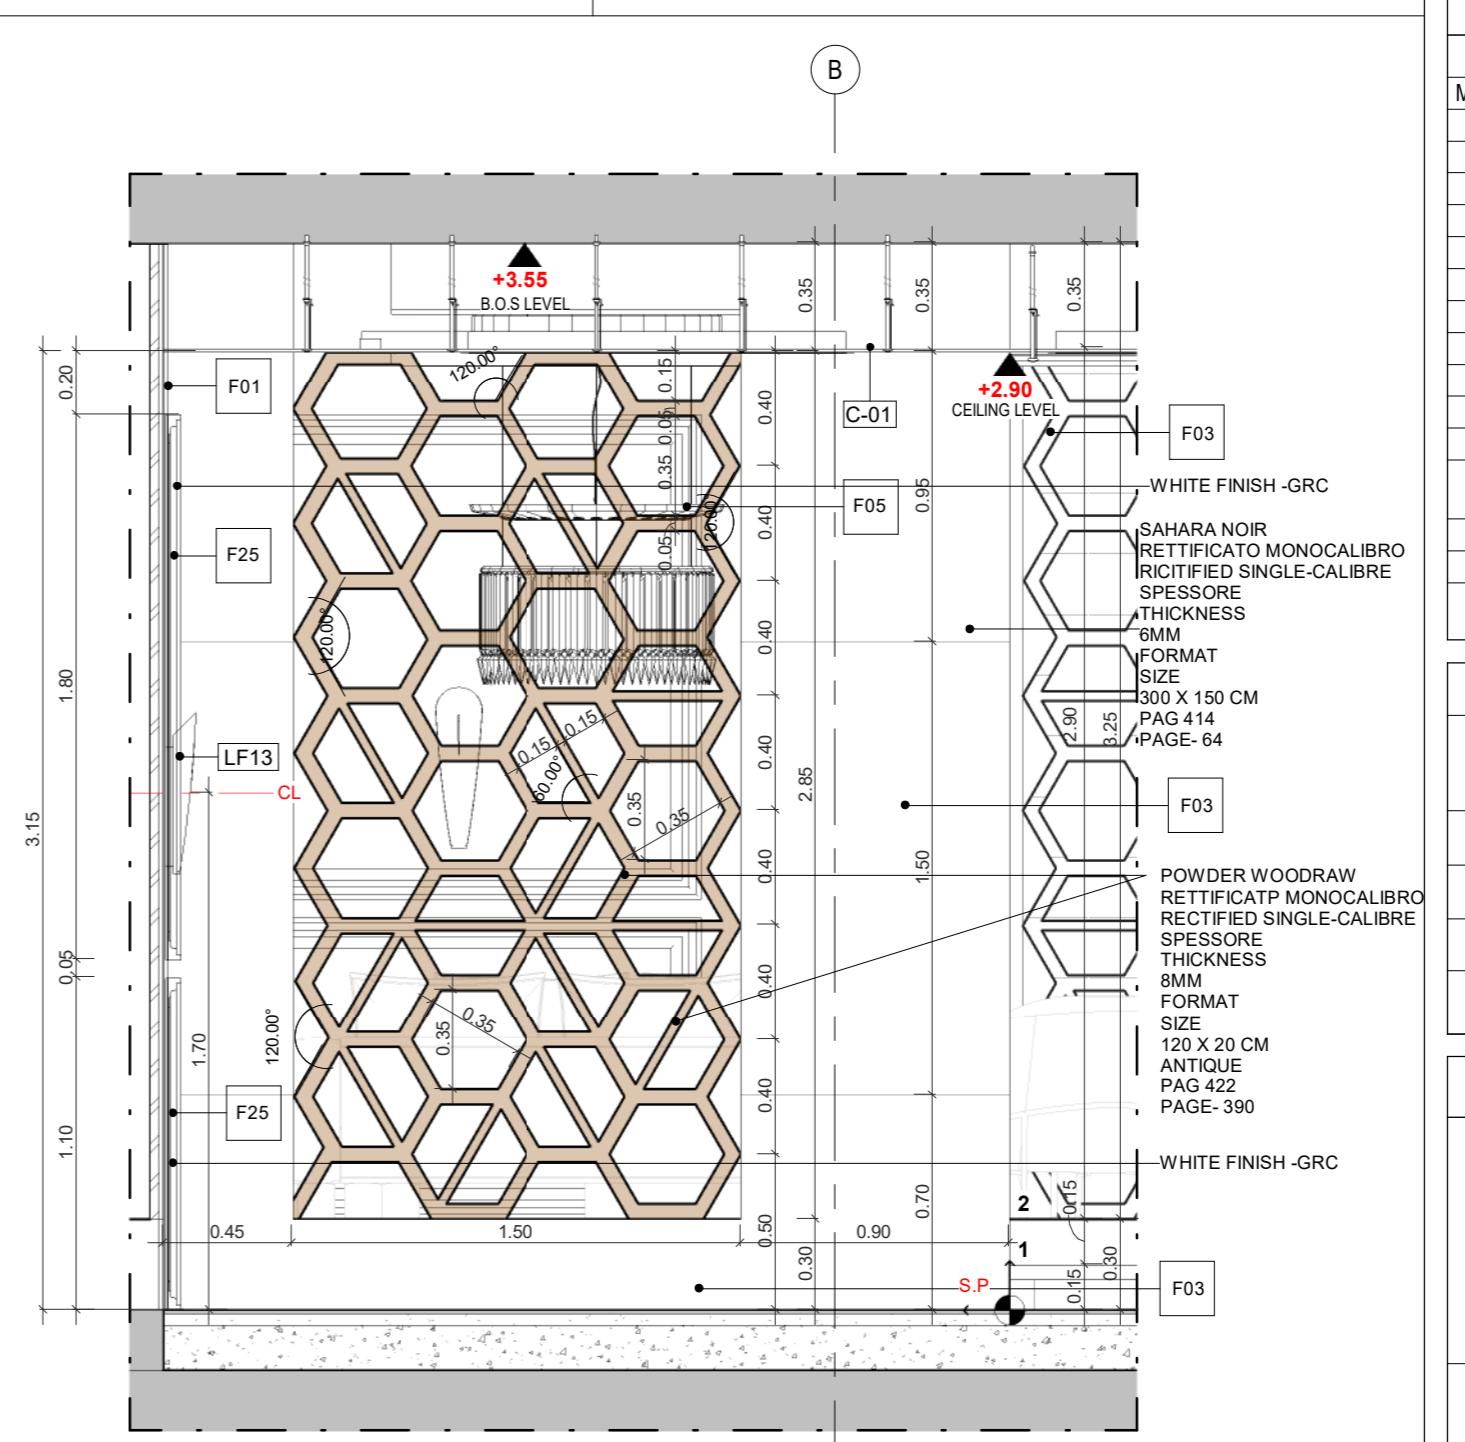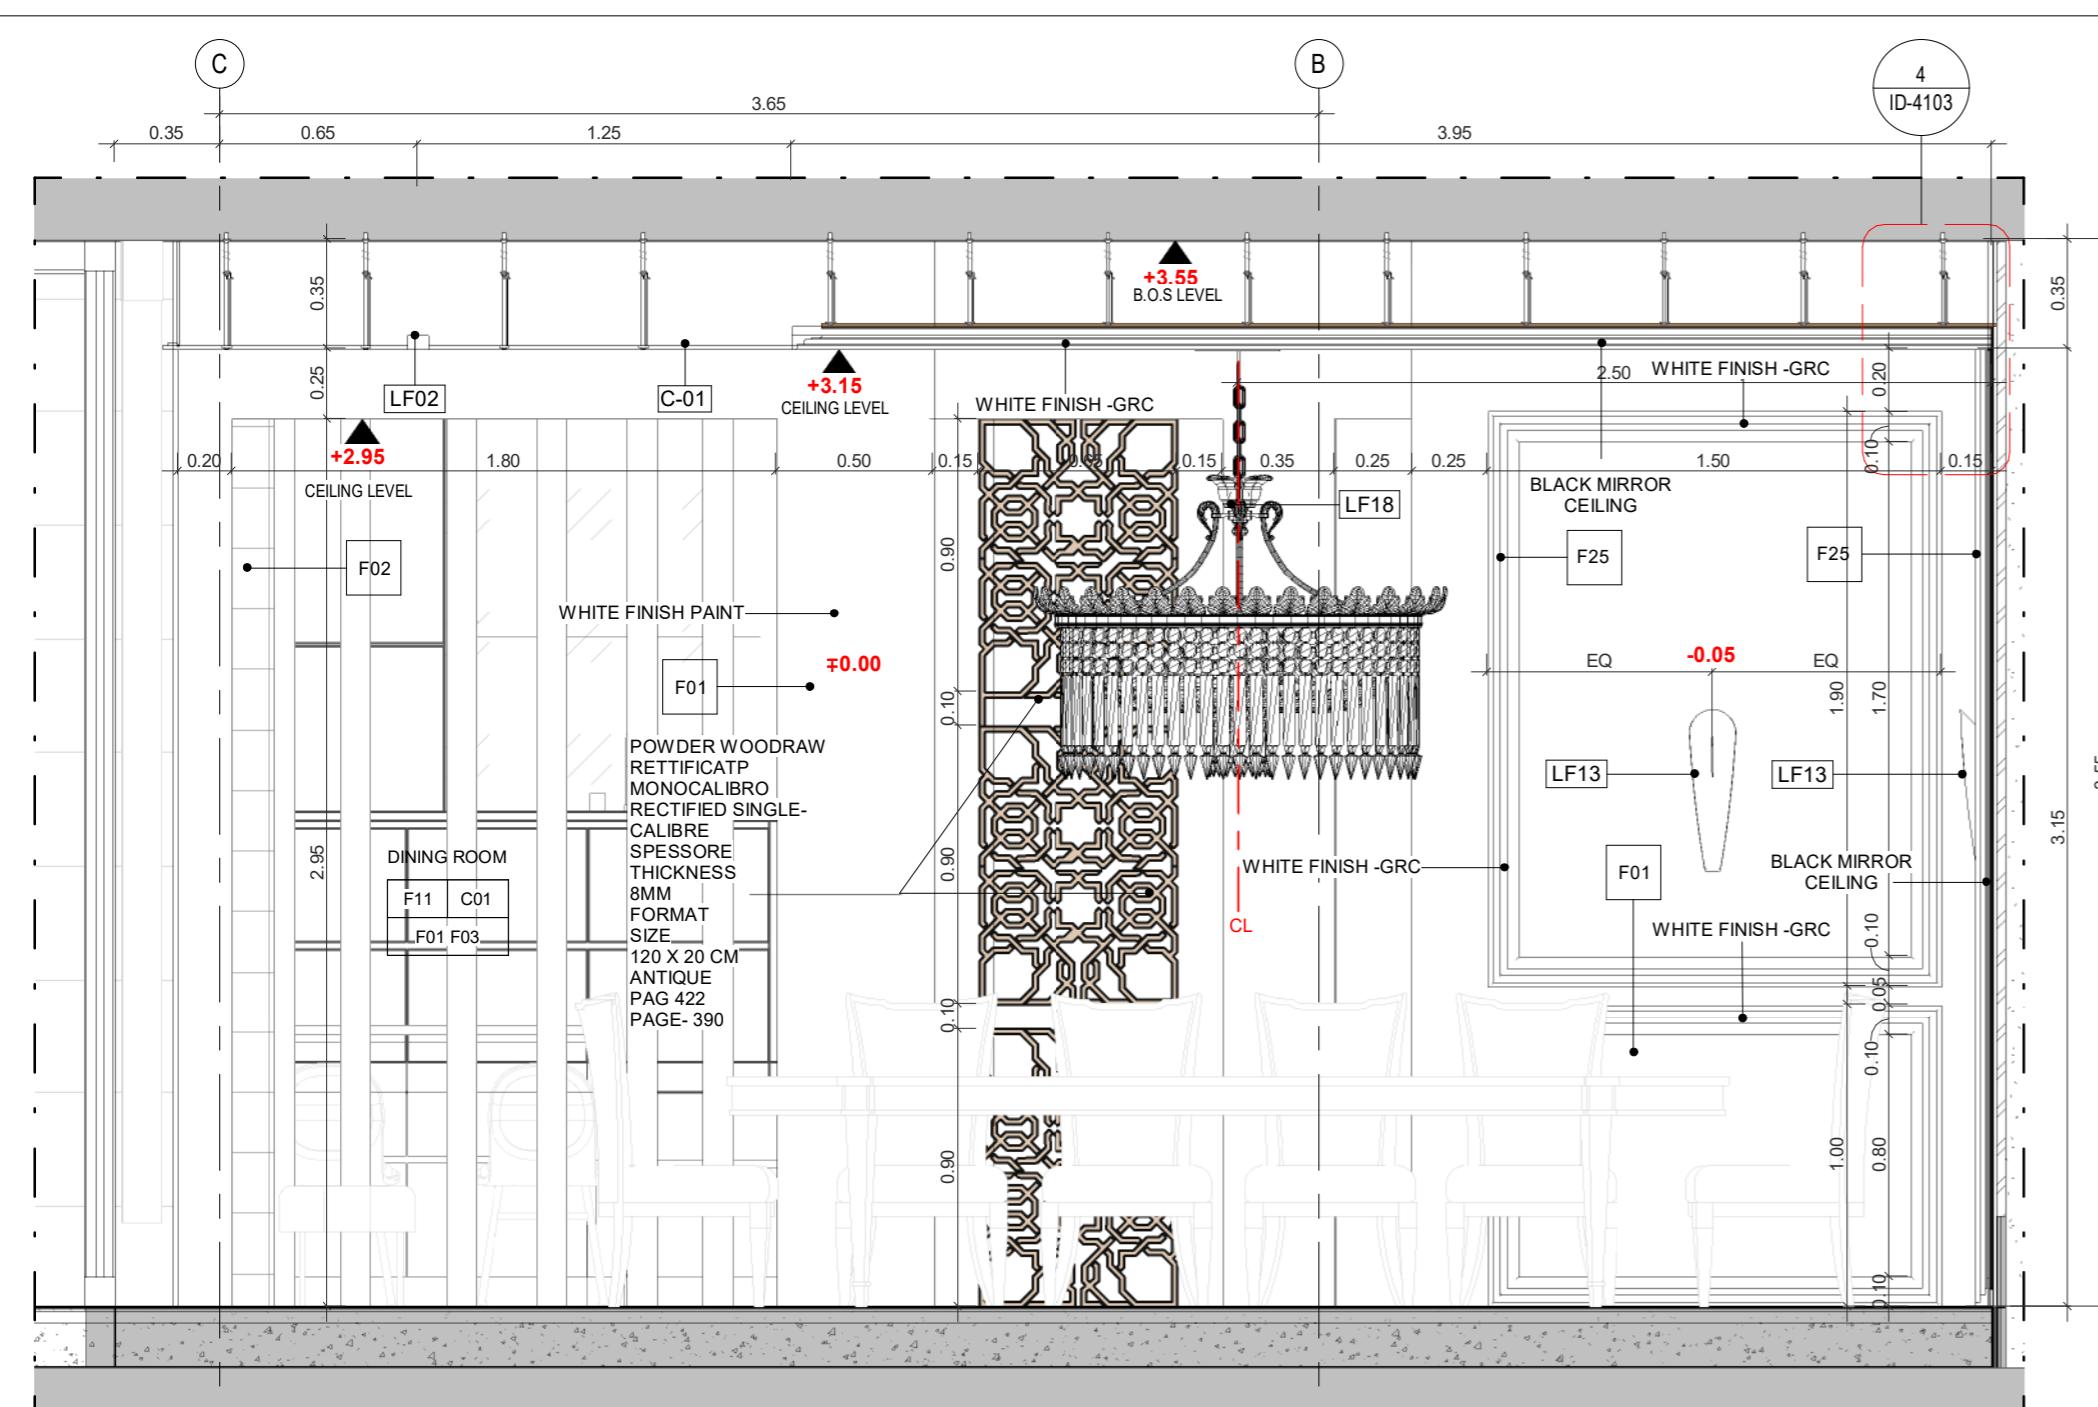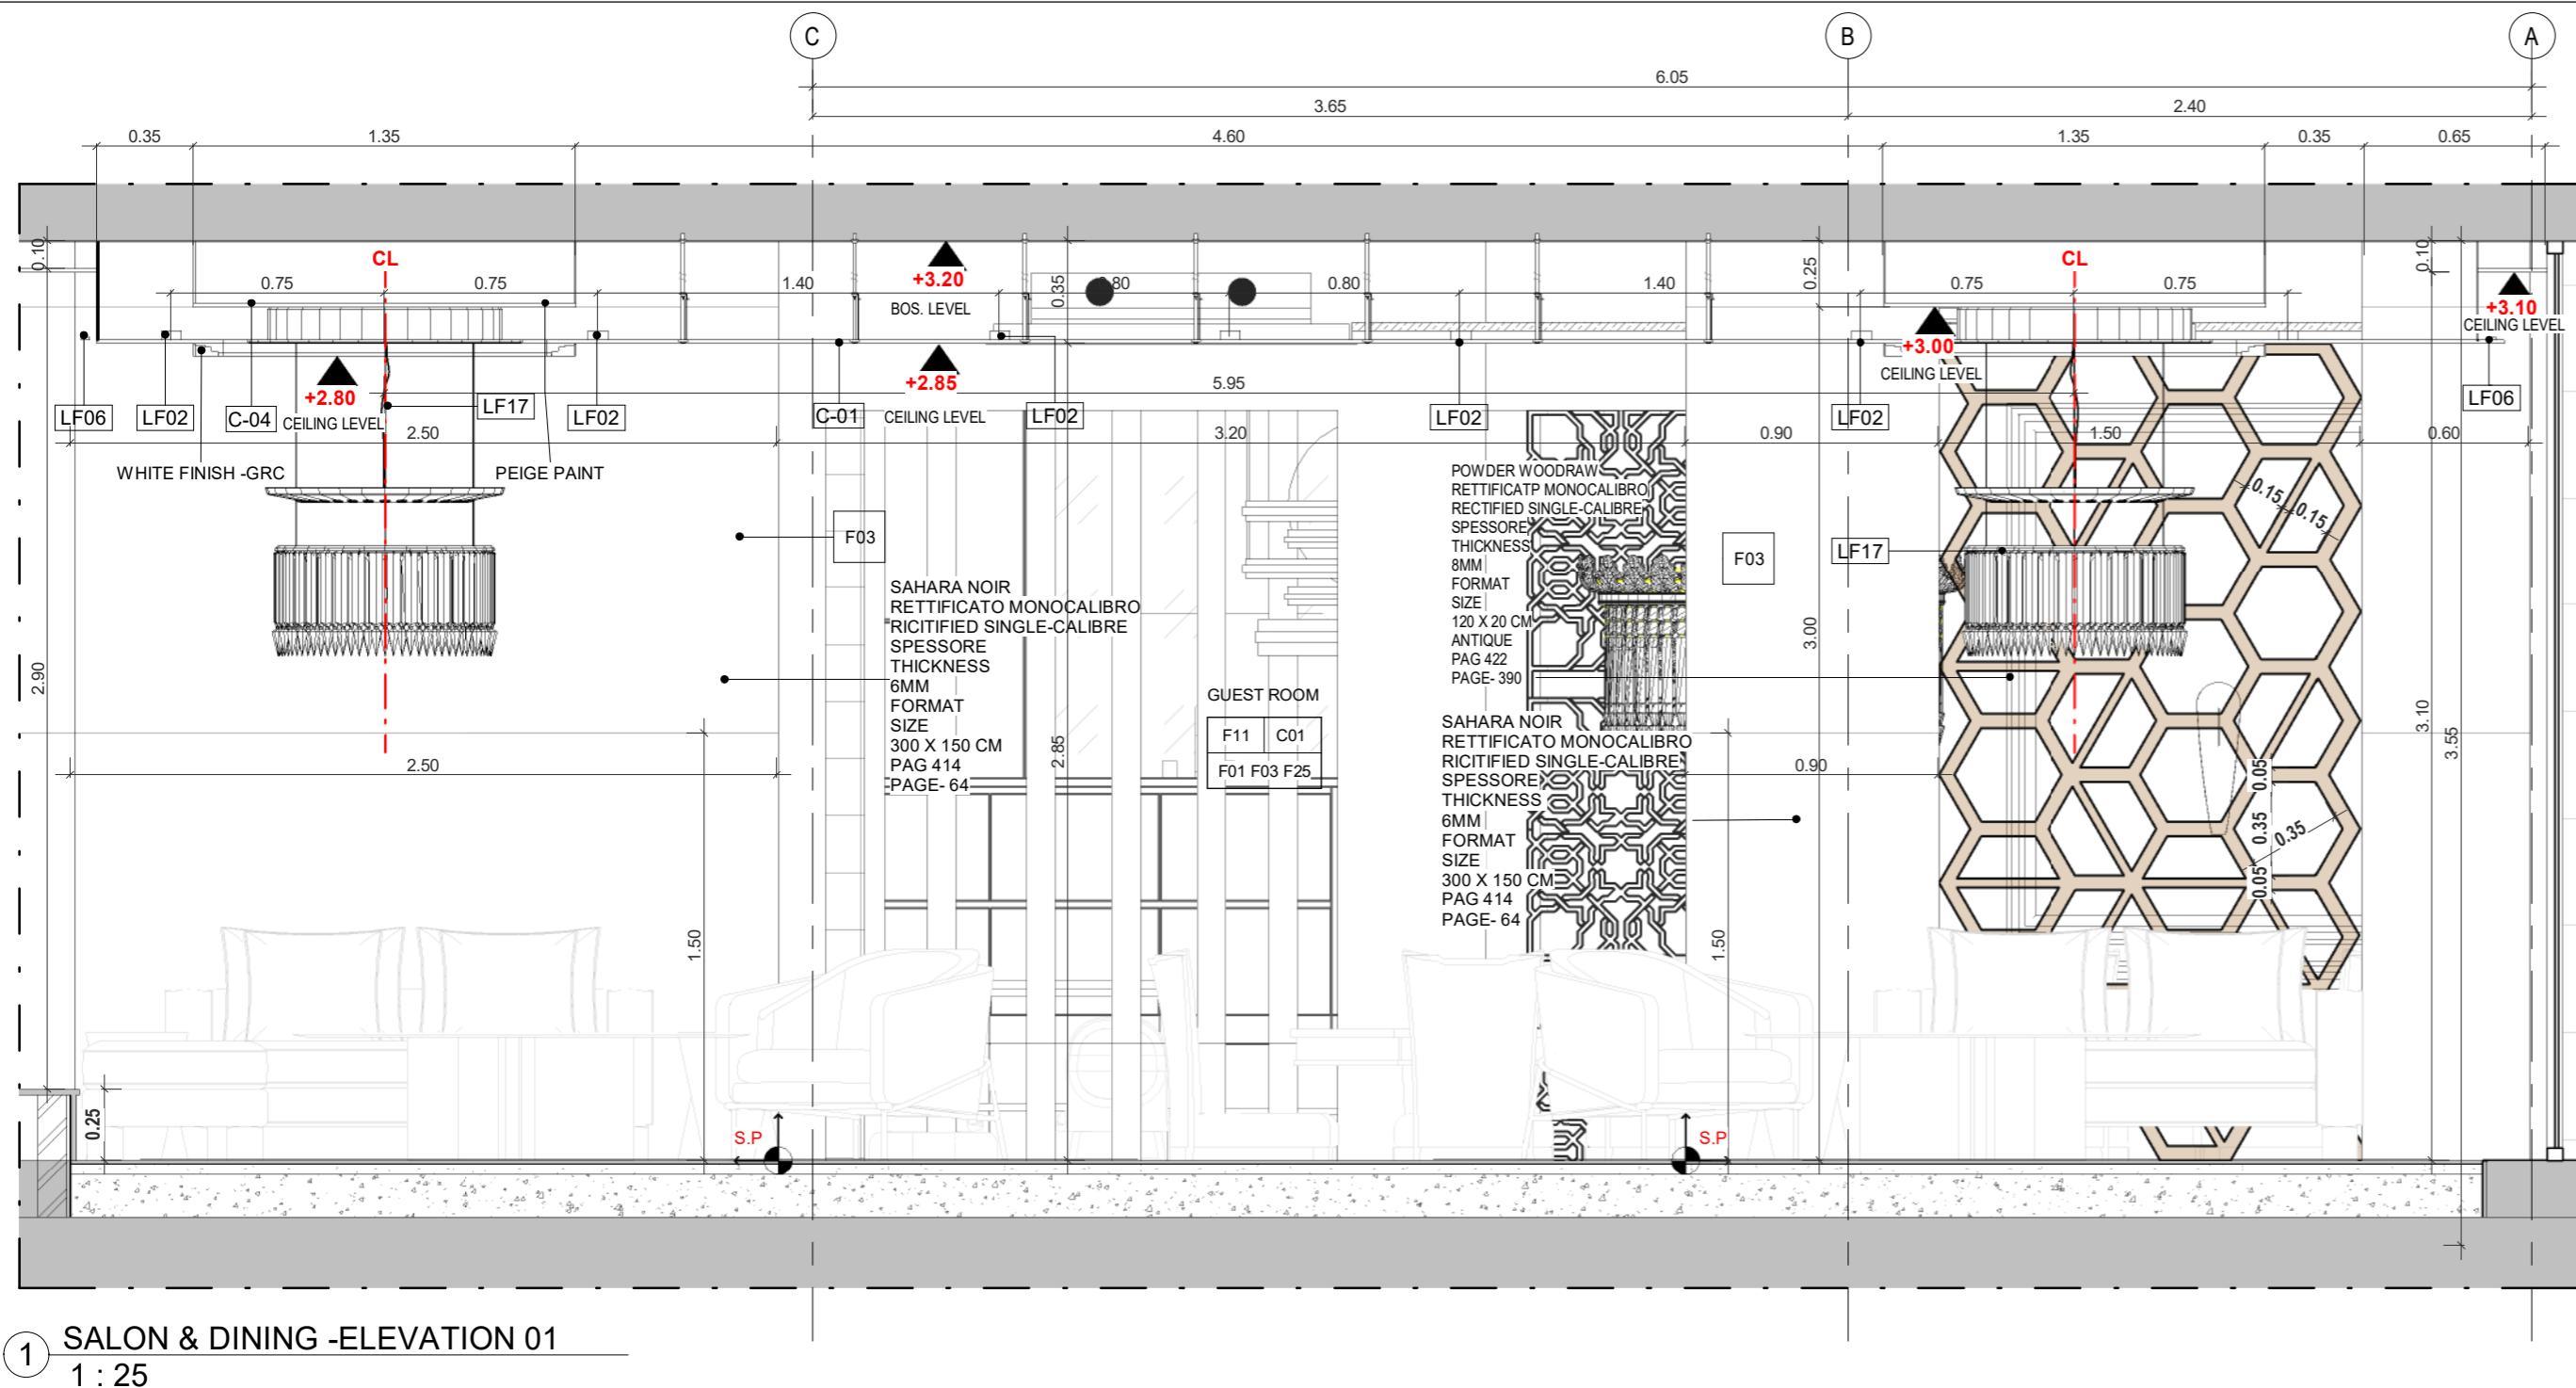

AL-BOUCA'I
ENGINEERING CONSULTING BUREAU
مكتب البقاعي
للاستشارات الهندسية

The logo for BIM Lab Engineering Services. The word "BIM" is written in large, bold, orange letters with a geometric, polygonal texture. A vertical grey line is positioned to the right of "BIM". To the right of the line, the word "Lab" is written in a smaller, lowercase, black sans-serif font. Below "BIM" and "Lab", the words "Engineering Services" are written in a smaller, black, sans-serif font.

PROJECT NAME

APARTMENTS BUILDING

NOTES

**FOR FINISHES REFER TO SHEETS:
ID-6000
ID-6001**

ROOM NAME

FLOOR FINISH

WALL FINISH

FINISHES SCHEDULE		FINISHES SCHEDULE	
Material: Mark	DESCRIPTION	Material: Mark	DESCRIPTION
F01	WHITE PAINT	F15	BEIGE PAINT
F02	GOLD WOOD	F16	TRAVERTINO MARBLE
F03	GOLD STONE	F17	LEATHER
F04	DARK WOOD	F18	PAINT GOLD METAL EFFECT
F05	DECORATIVE STONE	F19	DECORATIVE WOOD
F06	WOOD	F20	GREY STONE
F07	BLACK MARBLE	F21	CONCRETE FINISH
F08	BEIGE MARBLE	F22	KITCHENNETE WOOD
F09	GREY STONE	F23	SWIMMING POOL WALL FINISH
F10	WALL PAPER	F24	PARQUET
F11	CALCATTÀ	F25	WHITE FINISH GRC
F12	SWIMMING POOL MARBLE		
F13	BLACK PAINT		
F14	CALCATTÀ		

Project Type	Residential
Owner	Khalid Khadir Hasan AL-Saeed
Location	Amman
Plot No.	1659
Basin No.	19
Designed by	A.Shaker Khulief 4809

SHEET NAME

**GROUND FLOOR- SALON &
DINING ROOM**

ID-4103

Date	08/10/2019
Scale	As indicated




PROJECT NAME	APARTMENTS BUILDING	
NOTES	FOR FINISHES REFER TO SHEETS: ID-6000 ID-6001	
ROOM NAME	FLOOR FINISH	CEILING FINISH

WALL FINISH

FINISHES SCHEDULE		FINISHES SCHEDULE			
Material:	Mark	DESCRIPTION	Material:	Mark	DESCRIPTION
F01		WHITE PAINT	F15		BEIGE PAINT
F02		GOLD WOOD	F16		TRAVERTINO
F03		GOLD STONE	F04		MARBLE
F04		DARK WOOD	F17		LEATHER
F05		DECORATIVE STONE	F18		PAINT GOLD METAL EFFECT
F06		WOOD	F07		DECORATIVE WOOD
F08		BLACK MARBLE	F09		BEIGE MARBLE
F10		GREY STONE	F11		CONCRETE FINISH
F12		WALL PAPER	F13		KITCHENNETE WOOD
F14		CALCAGNA	F15		SWIMMING POOL MARBLE
F16			F17		PARQUET
F17			F18		CALCAGNA

Project Type	Residential
Owner	Khalid Khadir Hasan AL-Saeed
Location	Amman
Plot No.	1659
Basin No.	19
Designed by	A.Shaker Khalief 4809

SHEET NAME	GROUND FLOOR- SALON & DINING ROOM	
ID-4104		
Date	08/10/2019	
Scale	As indicated	

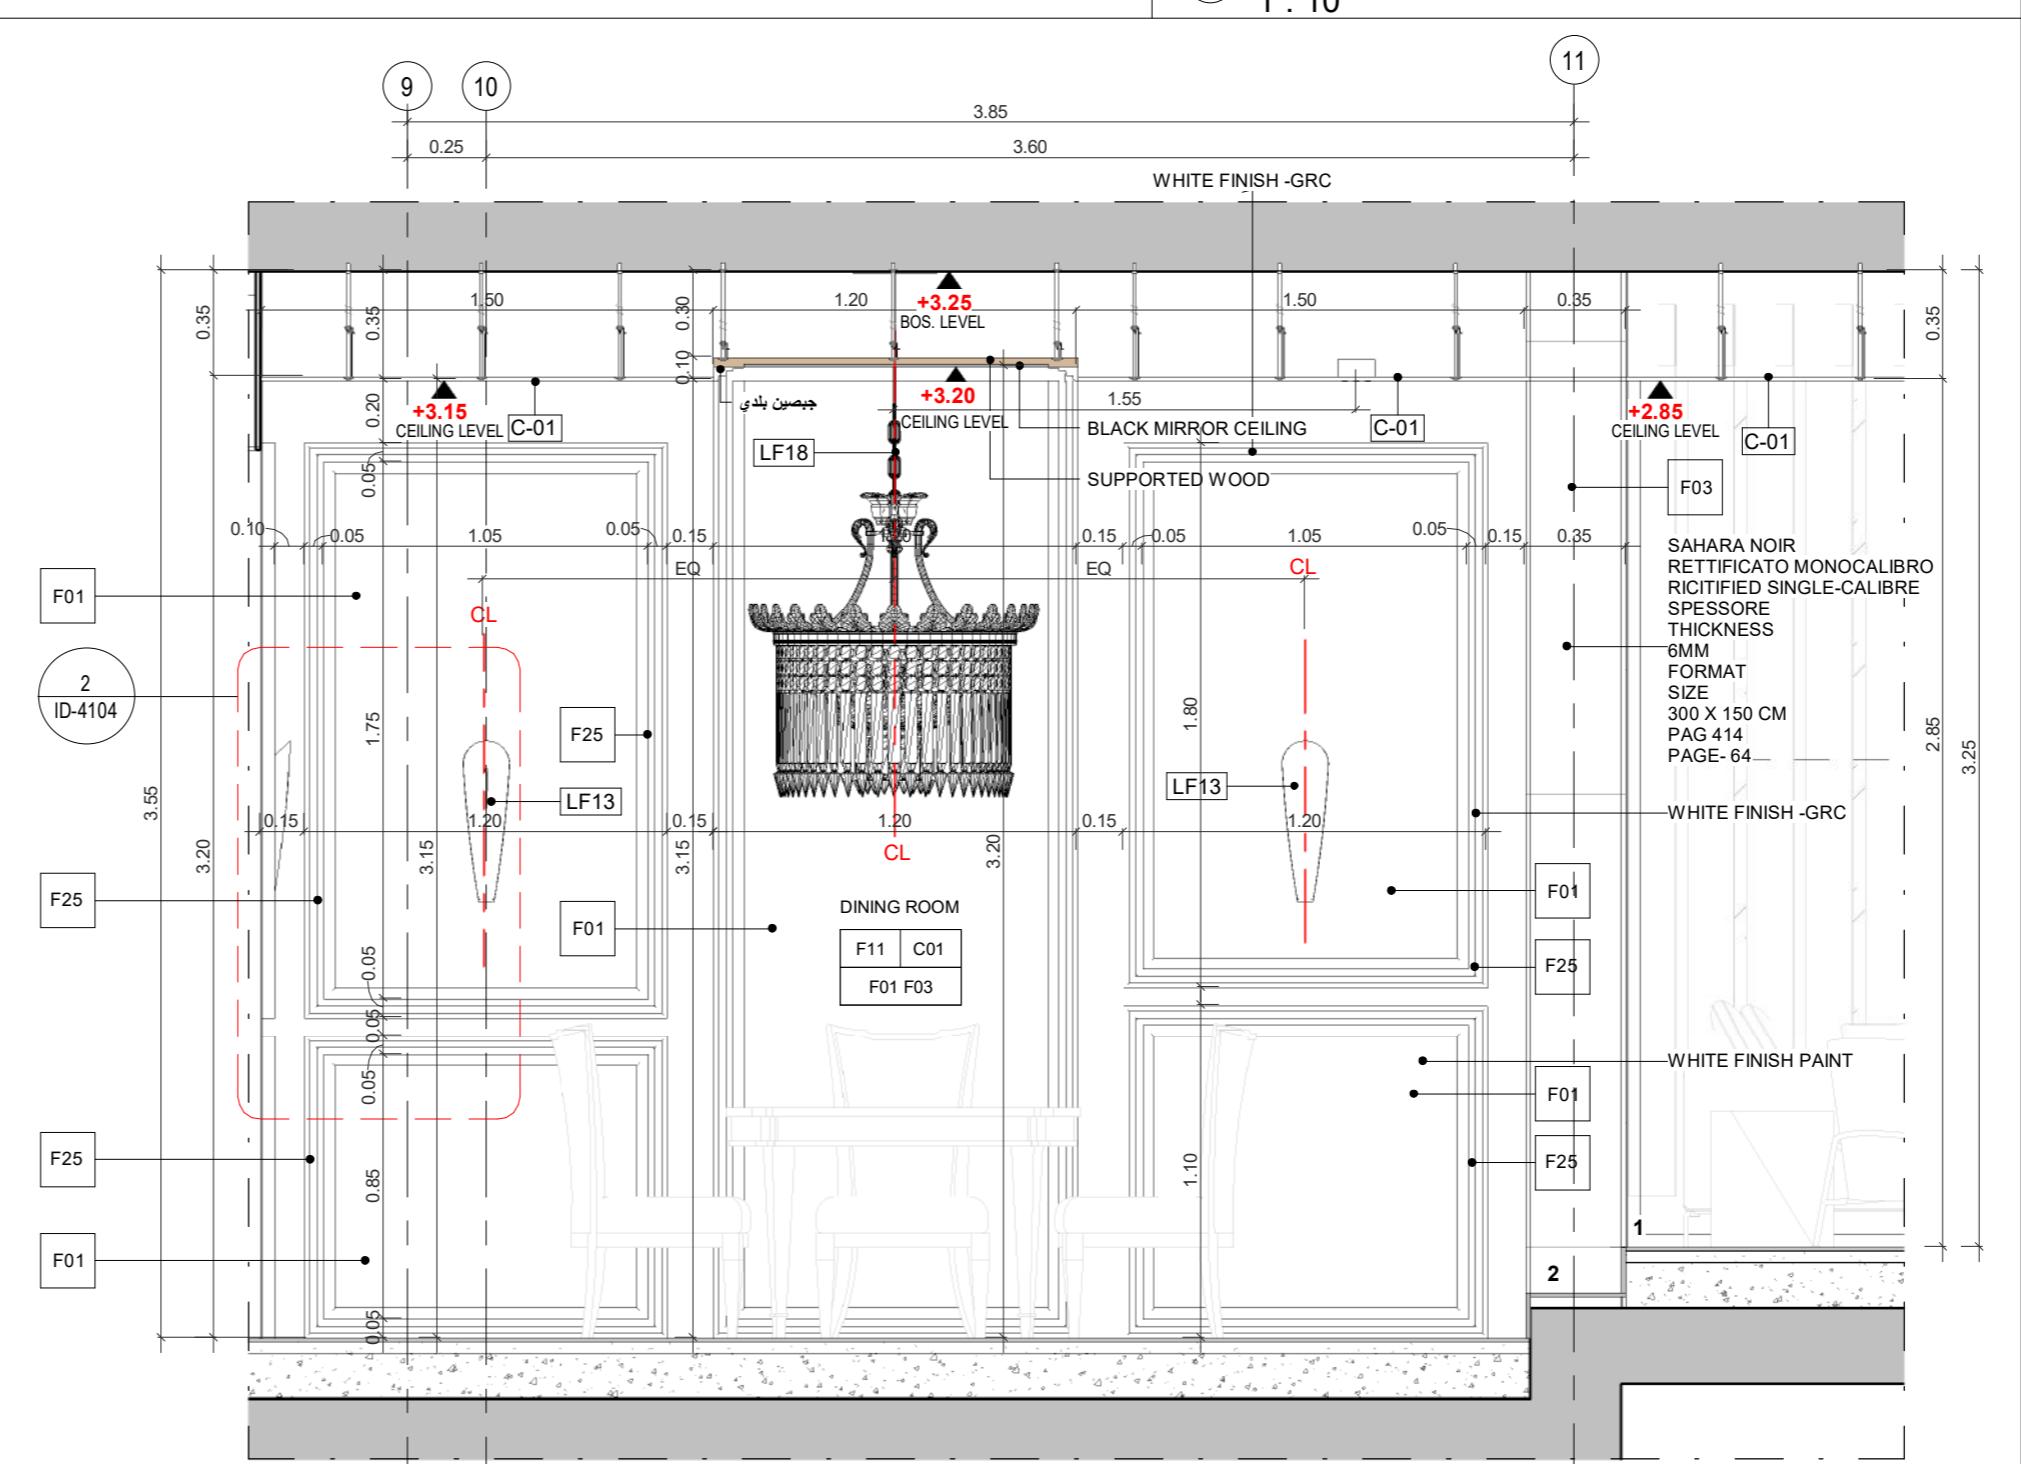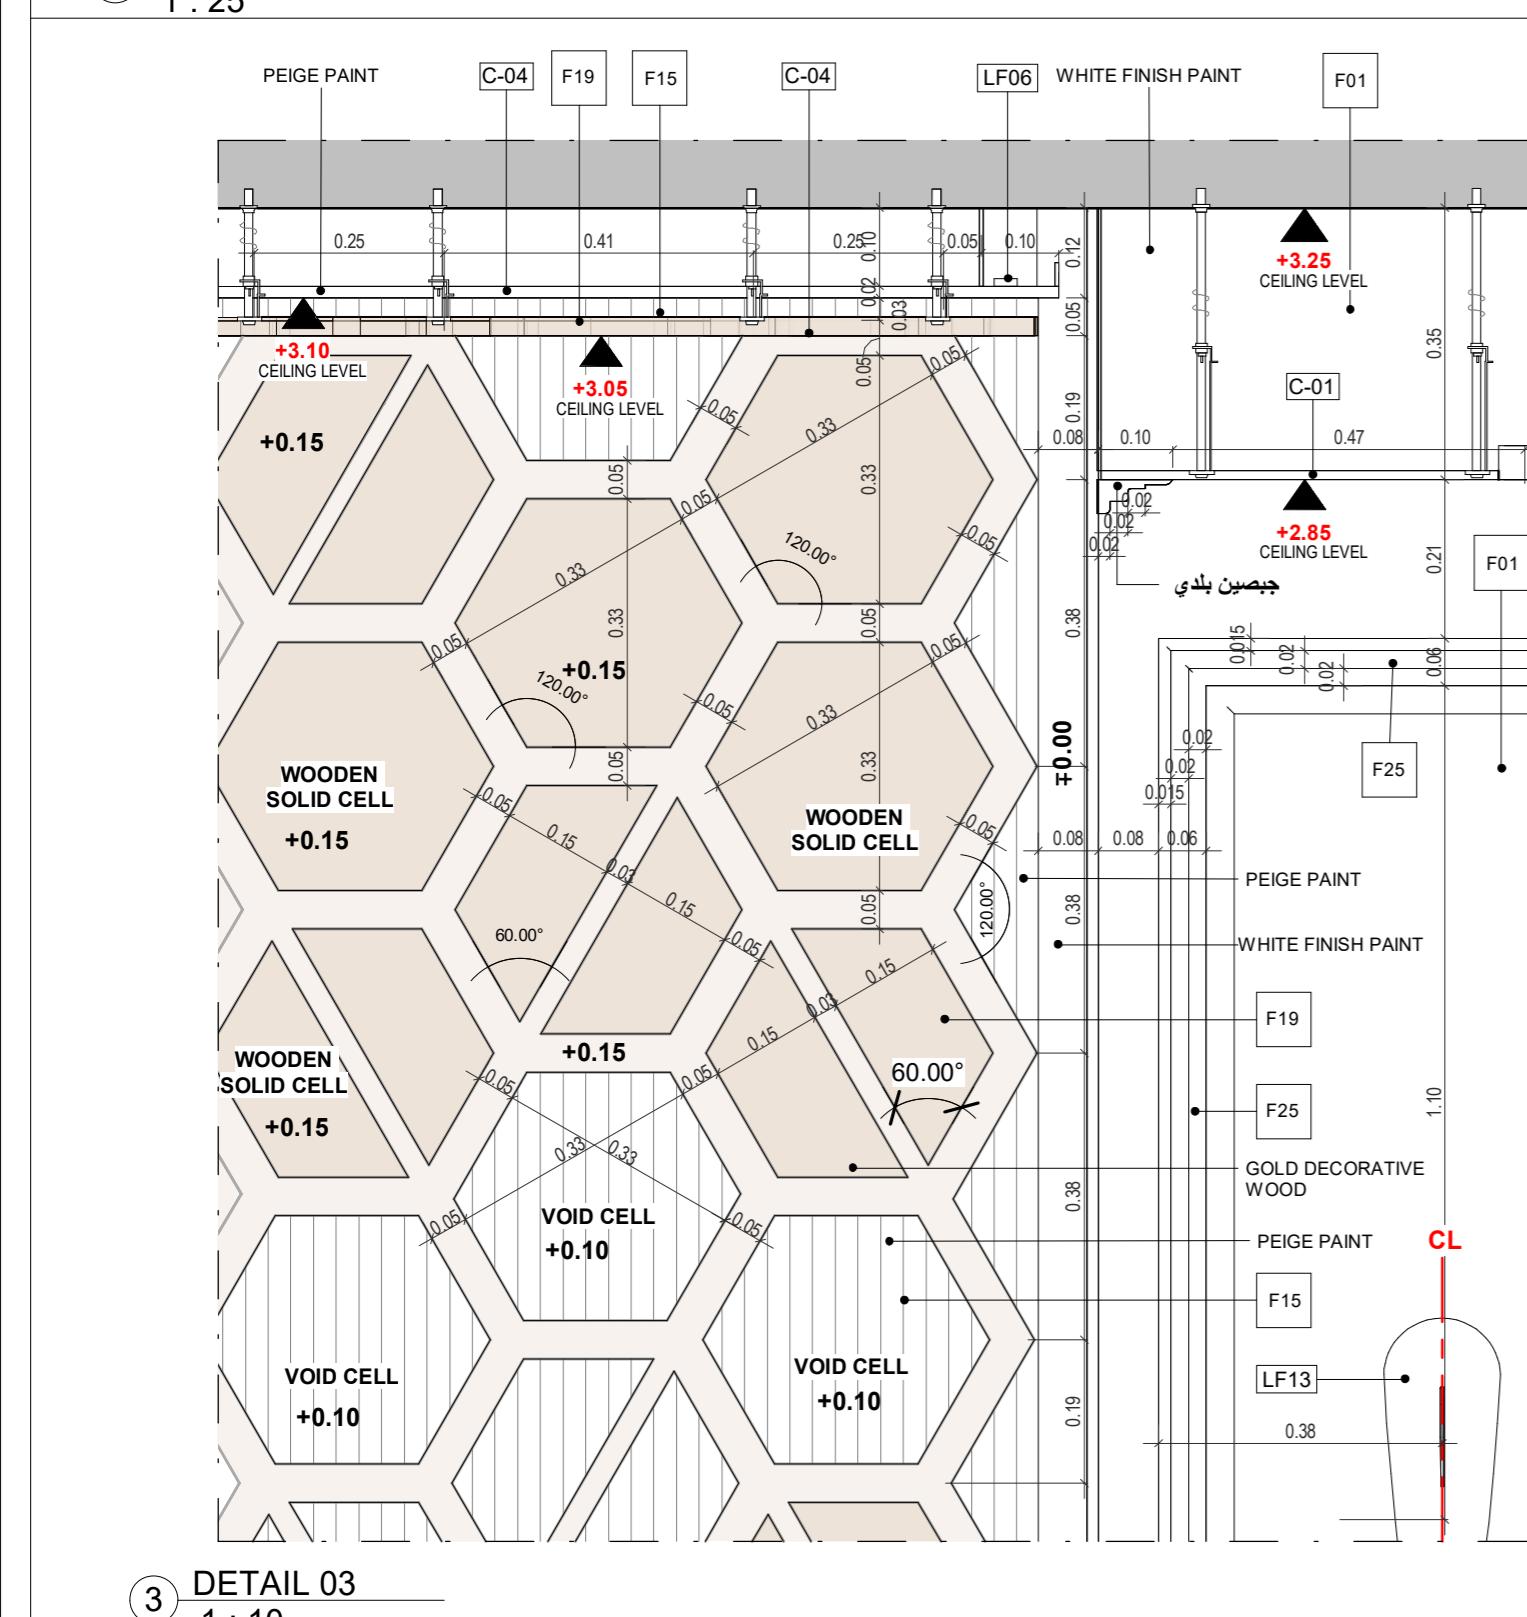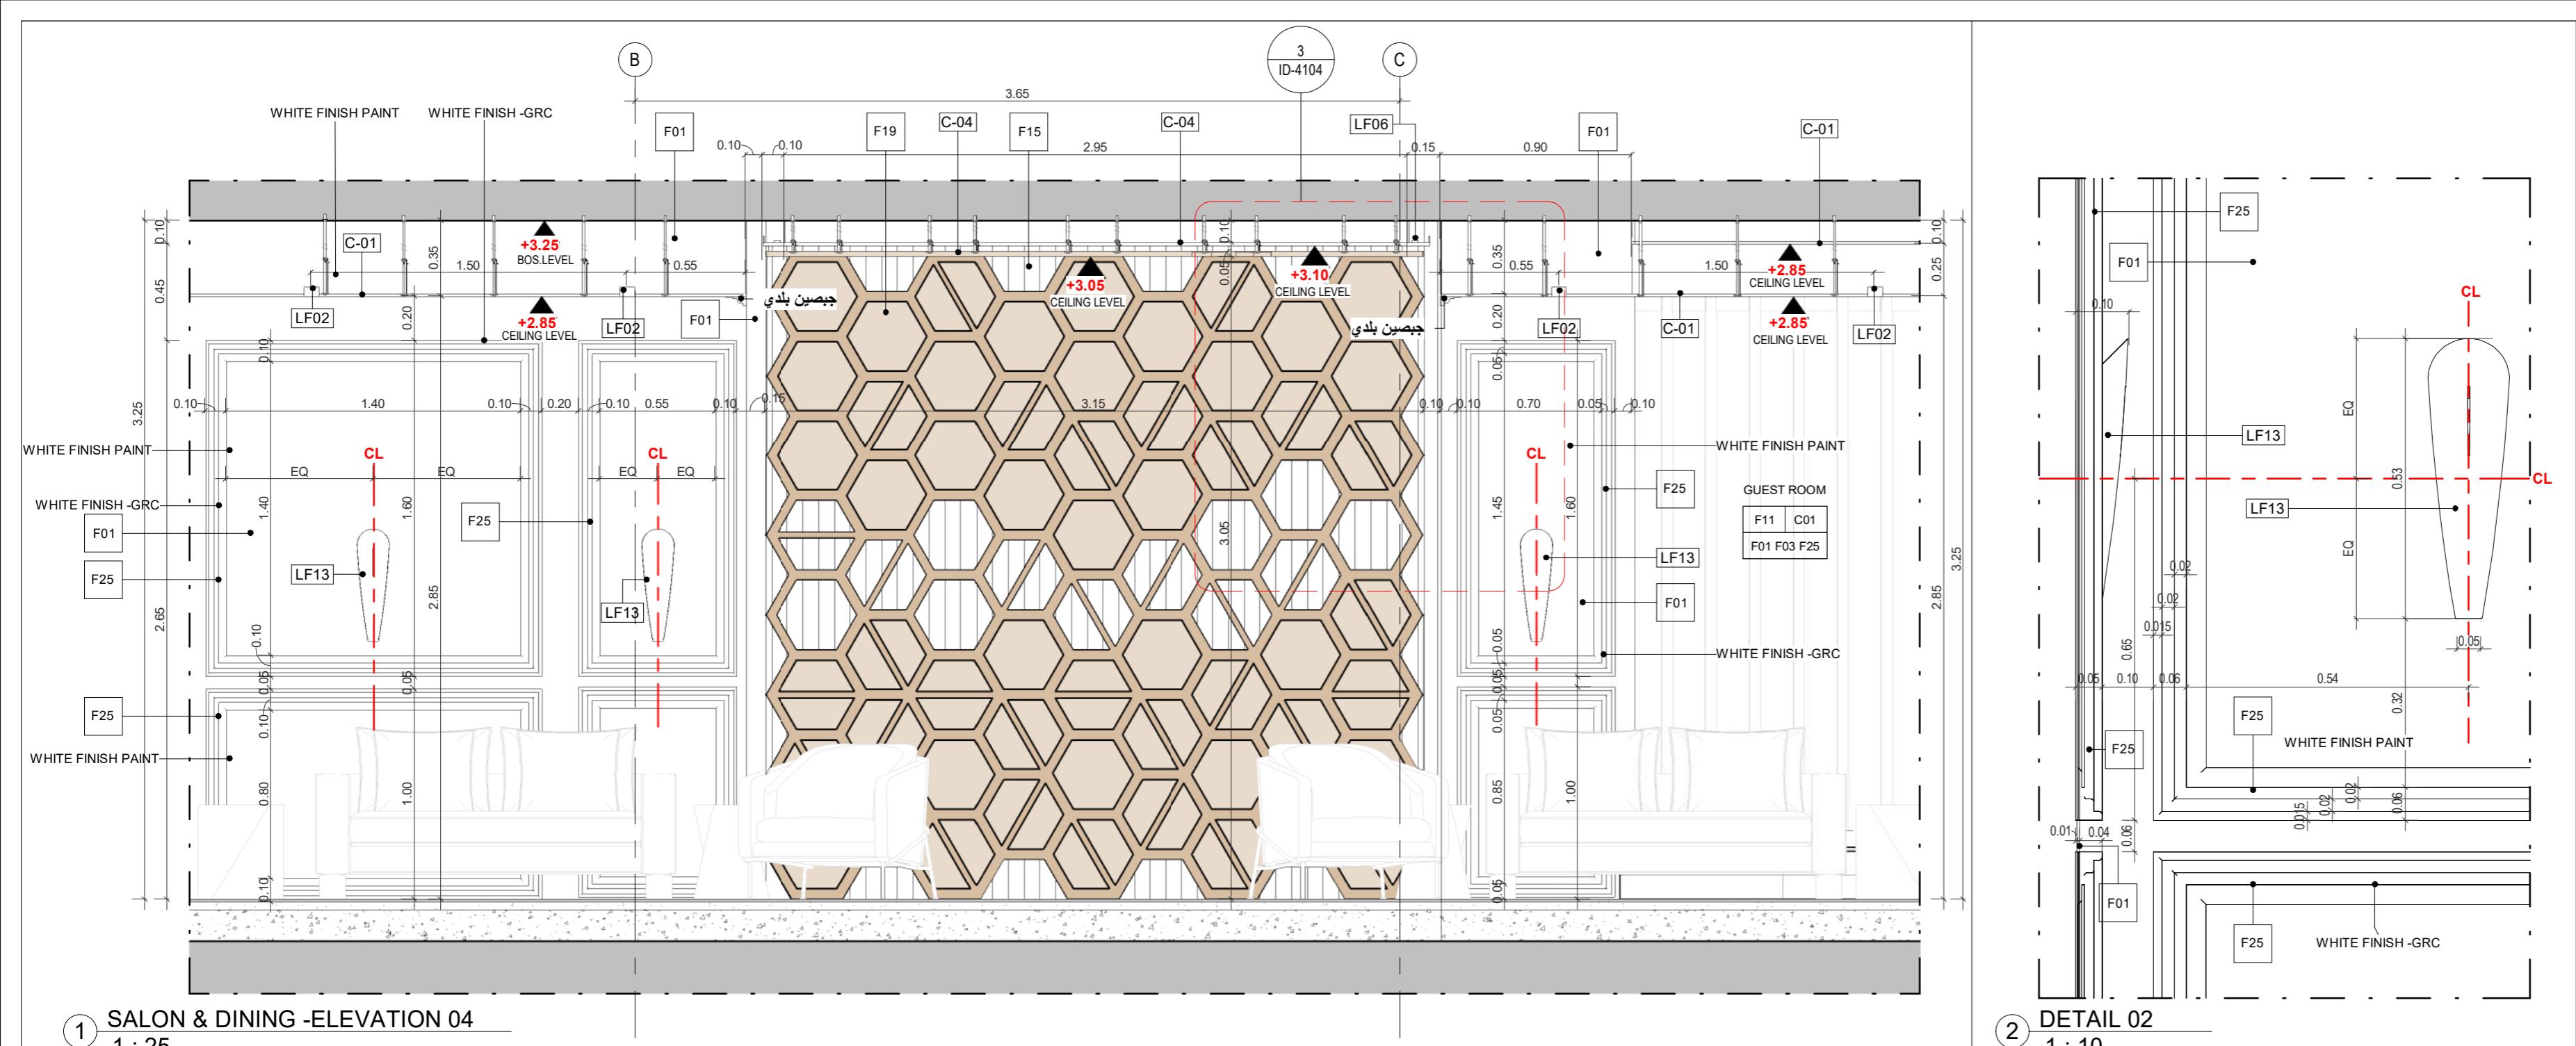

PROJECT NAME

APARTMENTS BUILDING

NOTES

FOR FINISHES REFER TO SHEETS:
ID-6000
ID-6001

ROOM NAME

FLOOR FINISH	CEILING FINISH
--------------	----------------

WALL FINISH

FINISHES SCHEDULE		FINISHES SCHEDULE	
Material:	Mark	Material:	Mark
F01	WHITE PAINT	F15	BEIGE PAINT
F02	GOLD WOOD	F16	TRAVERTINO MARBLE
F03	GOLD STONE	F17	LEATHER
F04	DARK WOOD	F18	PAINT GOLD METAL EFFECT
F05	DECORATIVE STONE	F06	WOOD
F06	WOOD	F07	BLACK MARBLE
F07	BLACK MARBLE	F08	BEIGE MARBLE
F08	BEIGE MARBLE	F09	GREY STONE
F09	GREY STONE	F10	WALL PAPER
F10	WALL PAPER	F11	CALCAGNA
F11	CALCAGNA	F12	SWIMMING POOL MARBLE
F12	SWIMMING POOL MARBLE	F13	BLACK PAINT
F13	BLACK PAINT	F14	WHITE FINISH GRC
F14	WHITE FINISH GRC		

— SPOT RECESSED LIGHT
— PENDANT LIGHT
— HIDDEN LIGHT
— CHANDELIER
— WALL MOUNTED
— NEON RECTANGULAR

Project Type Residential

Owner Khalid Khadir Hasan AL-Saeed

Location Amman

Plot No. 1659

Basin No. 19

Designed by A.Shaker Khulief 4809


SHEET NAME

GROUND FLOOR- SALON & DINING ROOM

ID-4105


Date 08/10/2019

Scale As indicated

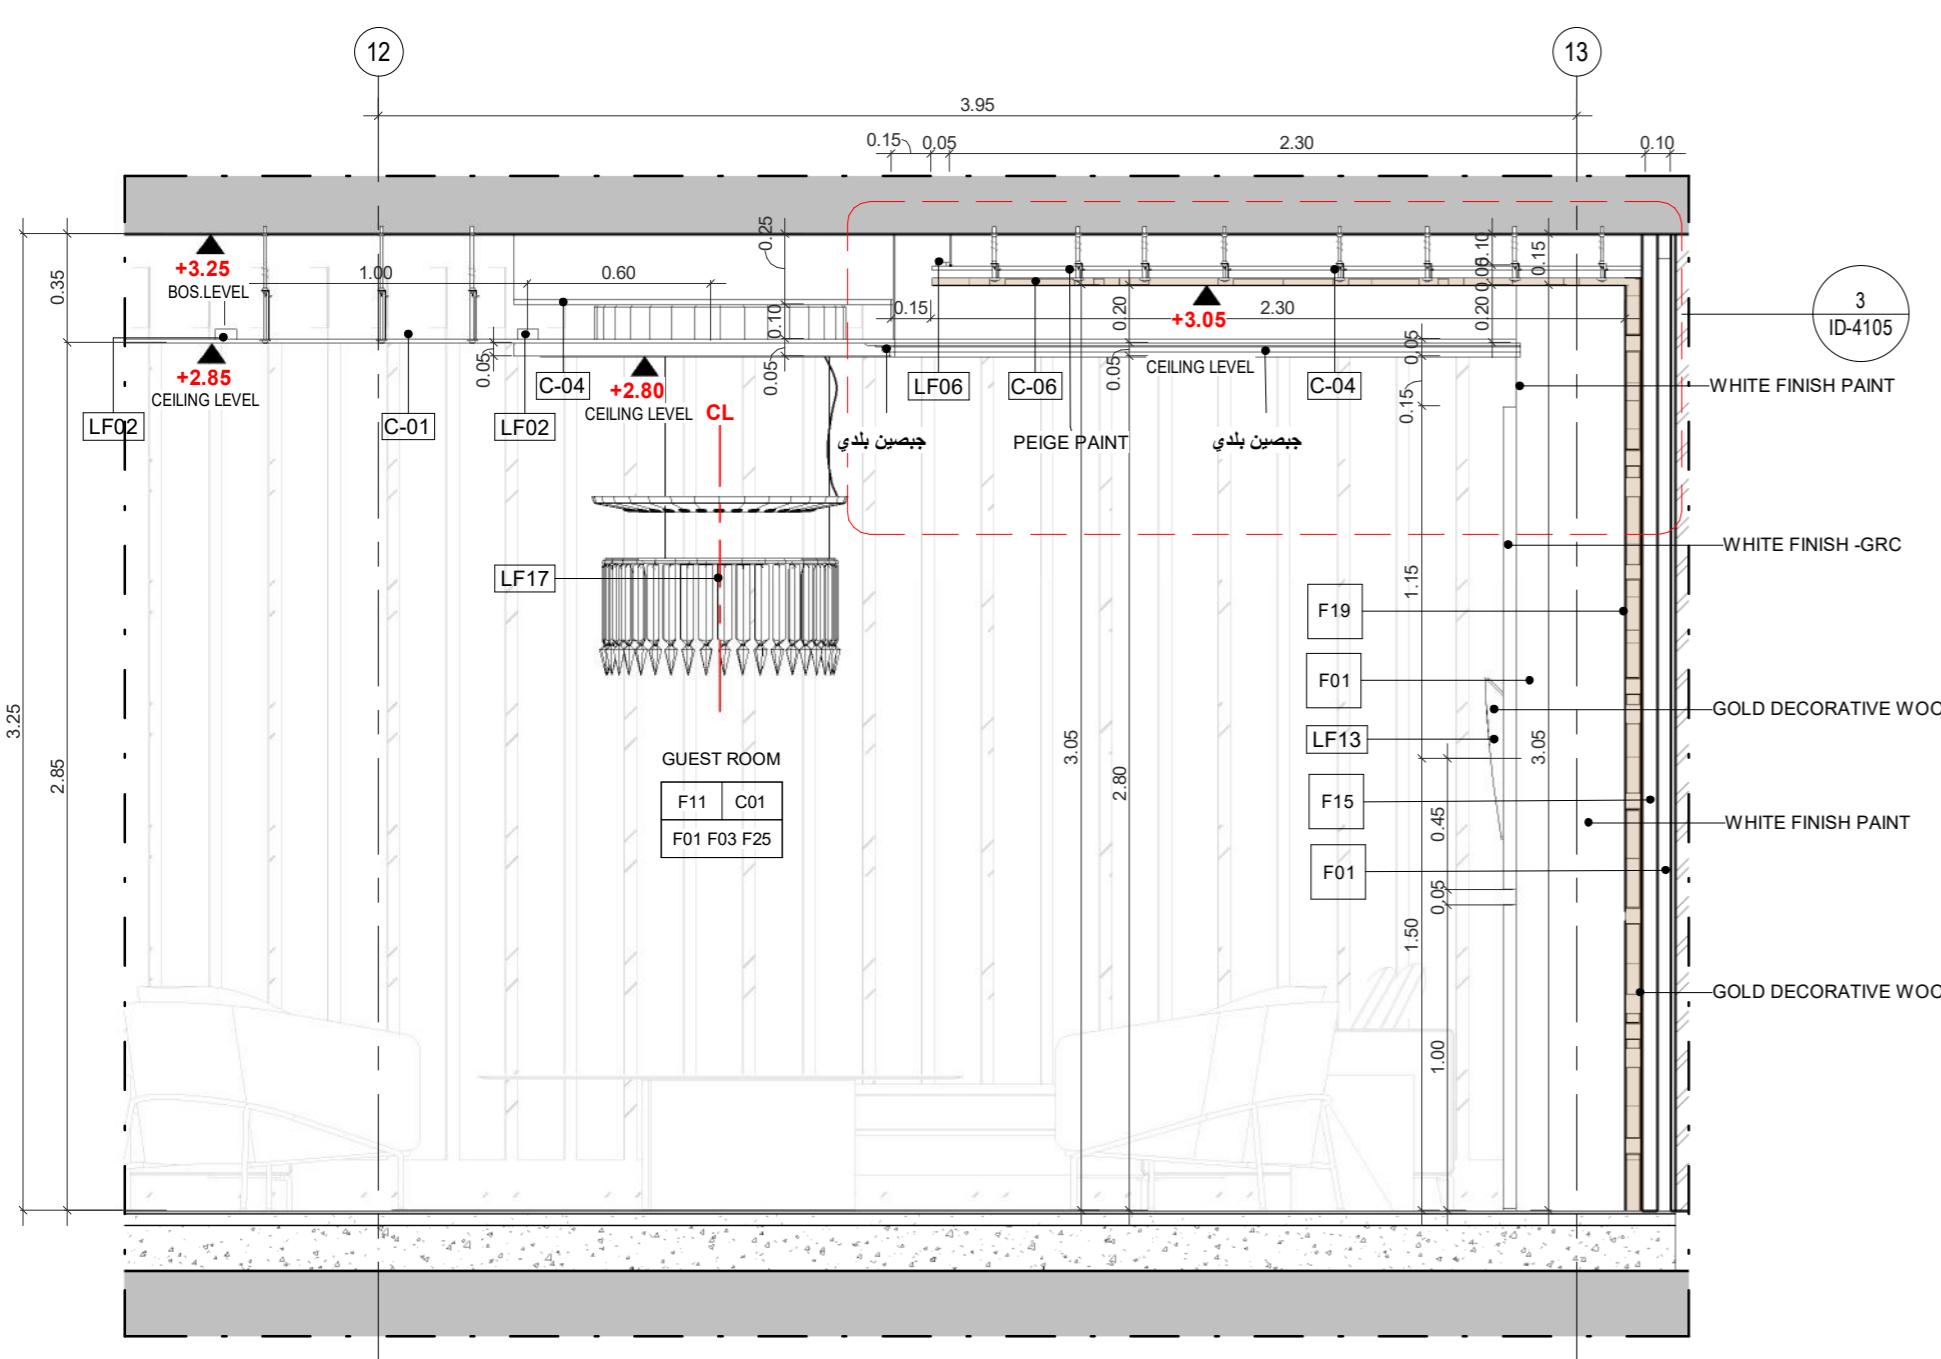


① SALON & DINING -SECTION 01

1 : 25

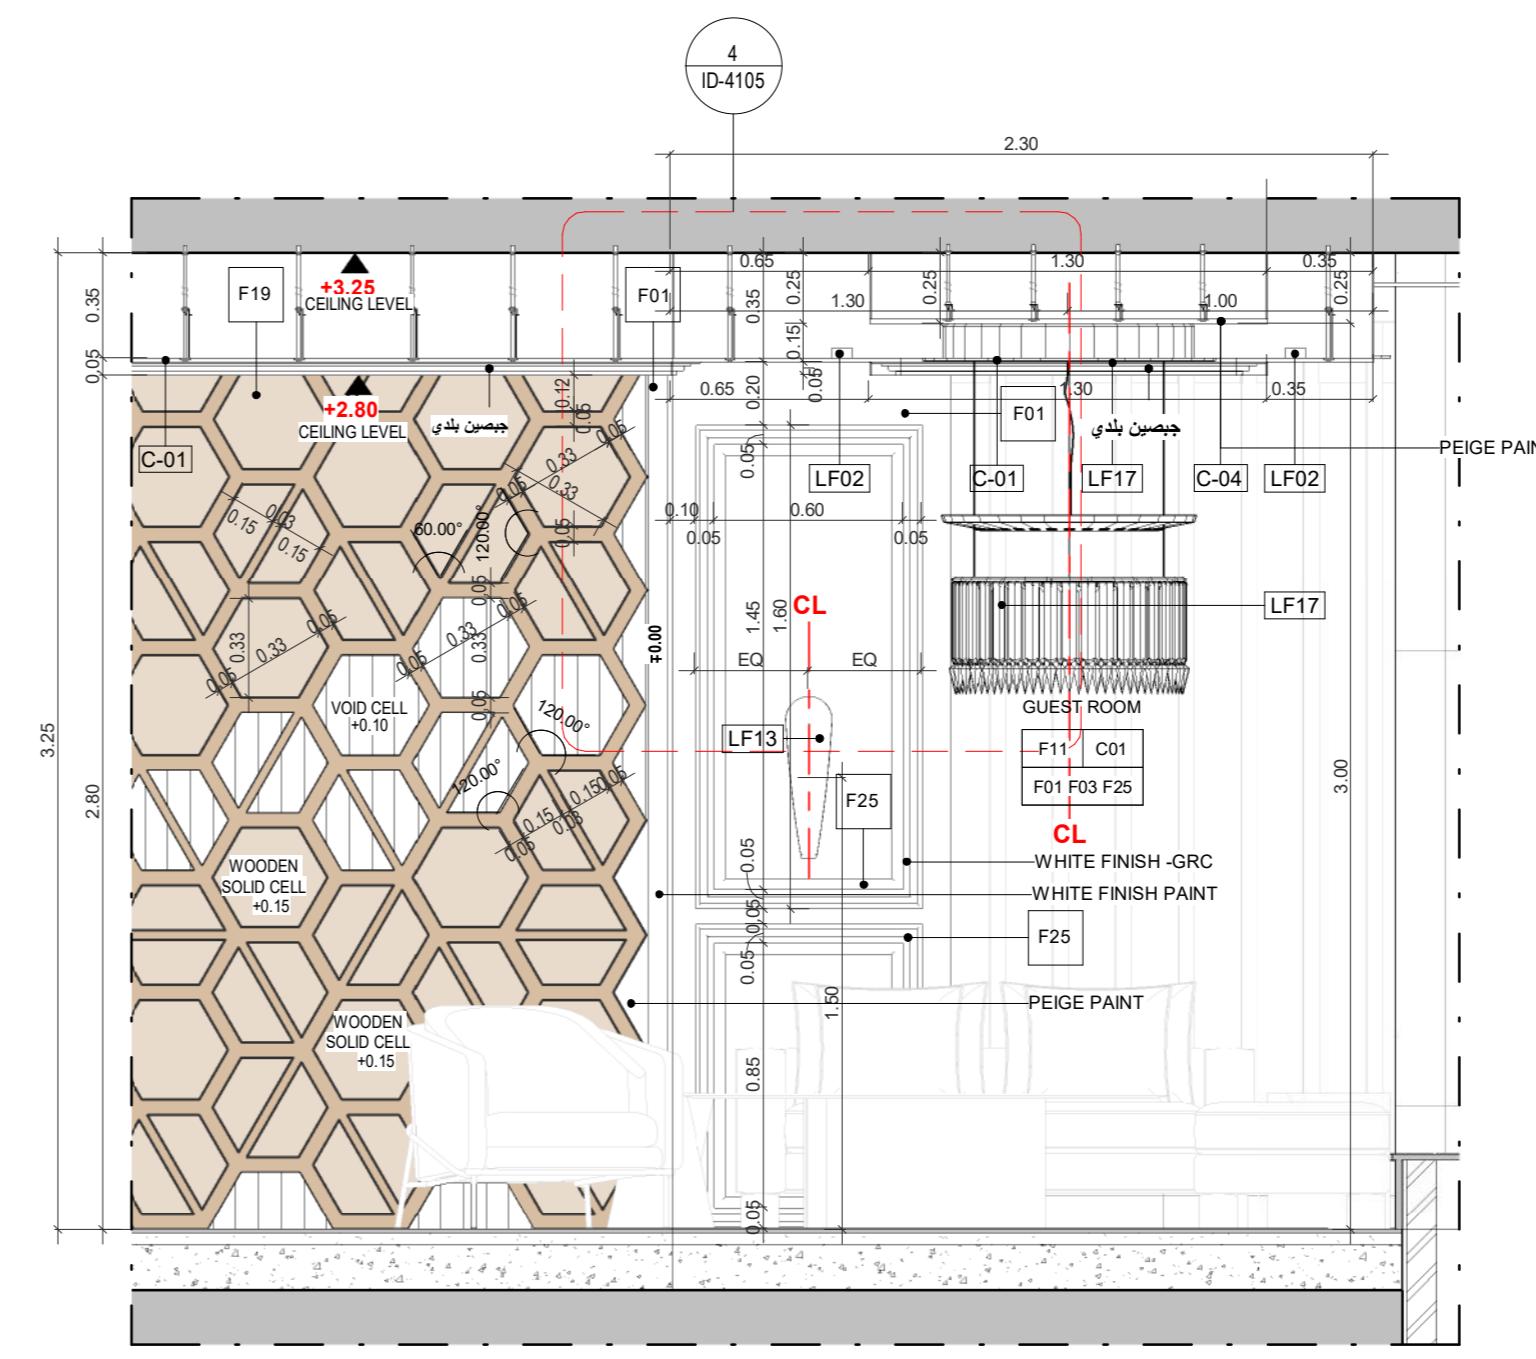


② SALON & DINING -SECTION 02

1 : 25

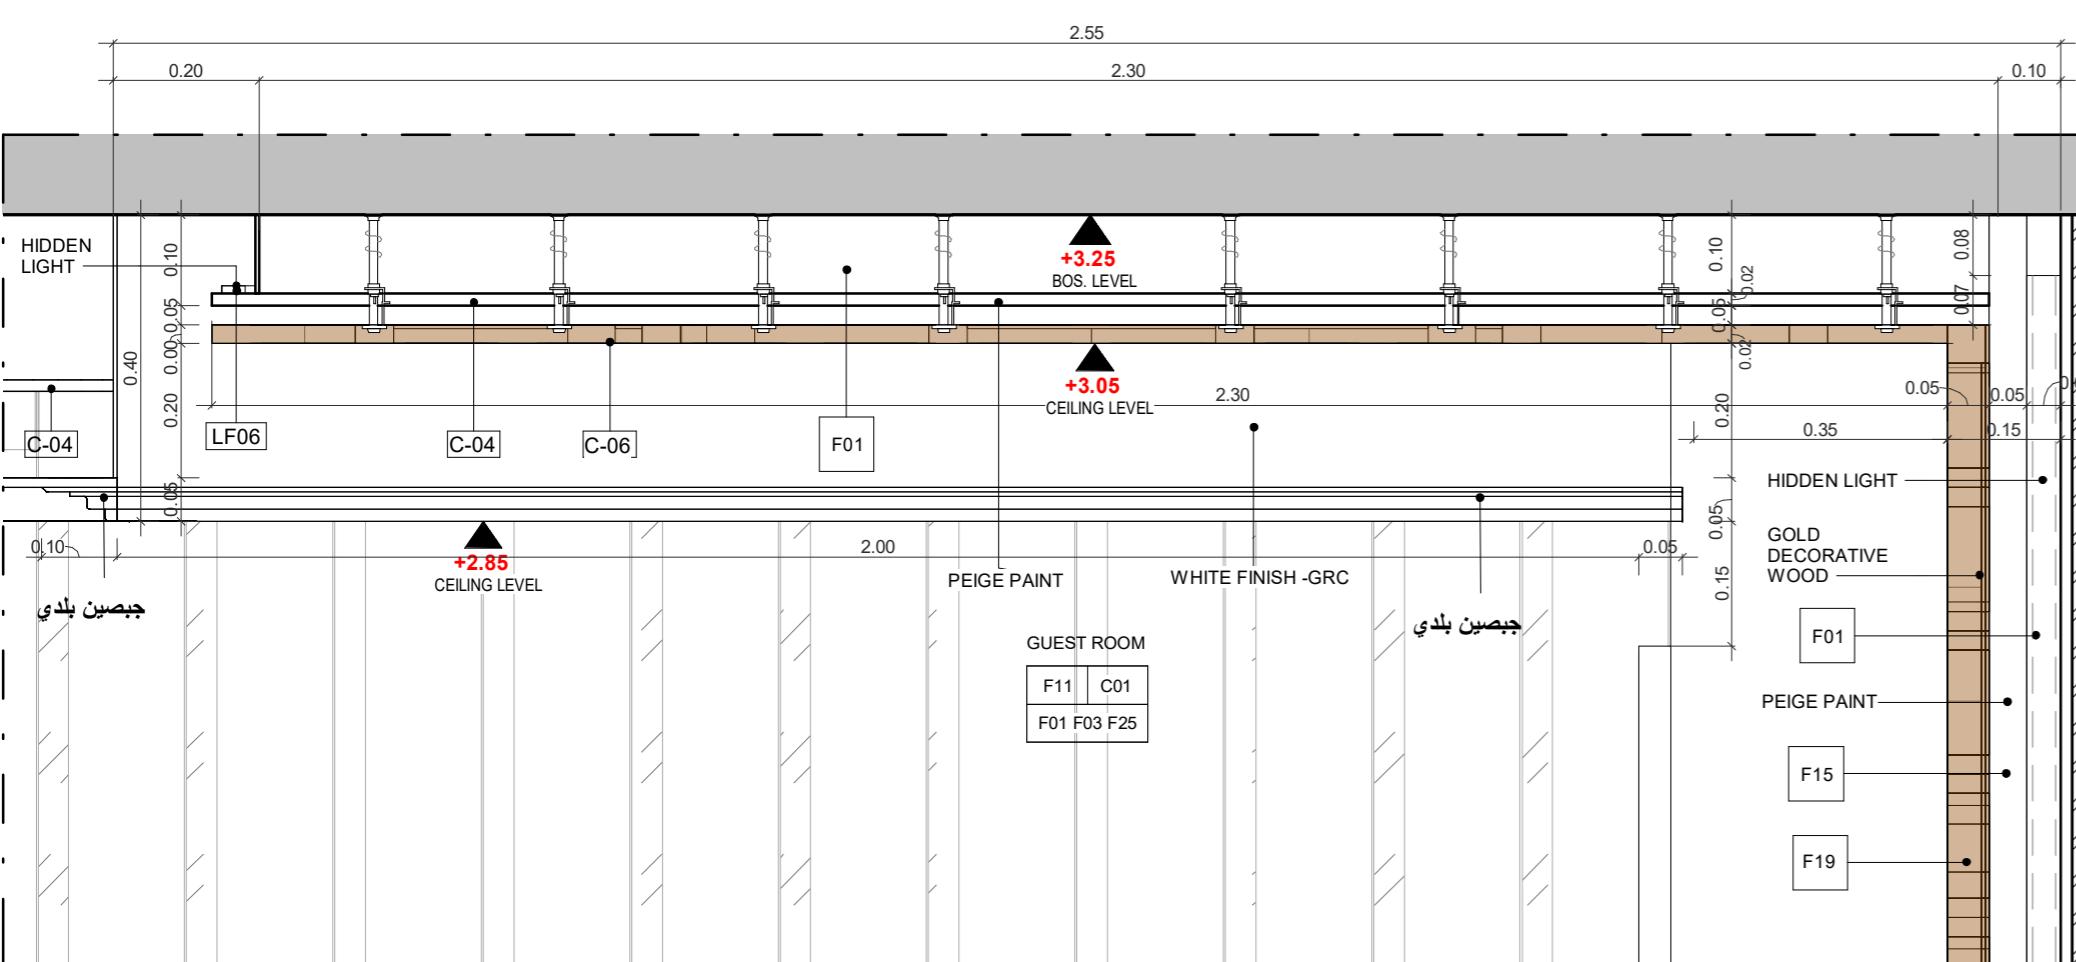

③ DETAIL 04

1 : 10

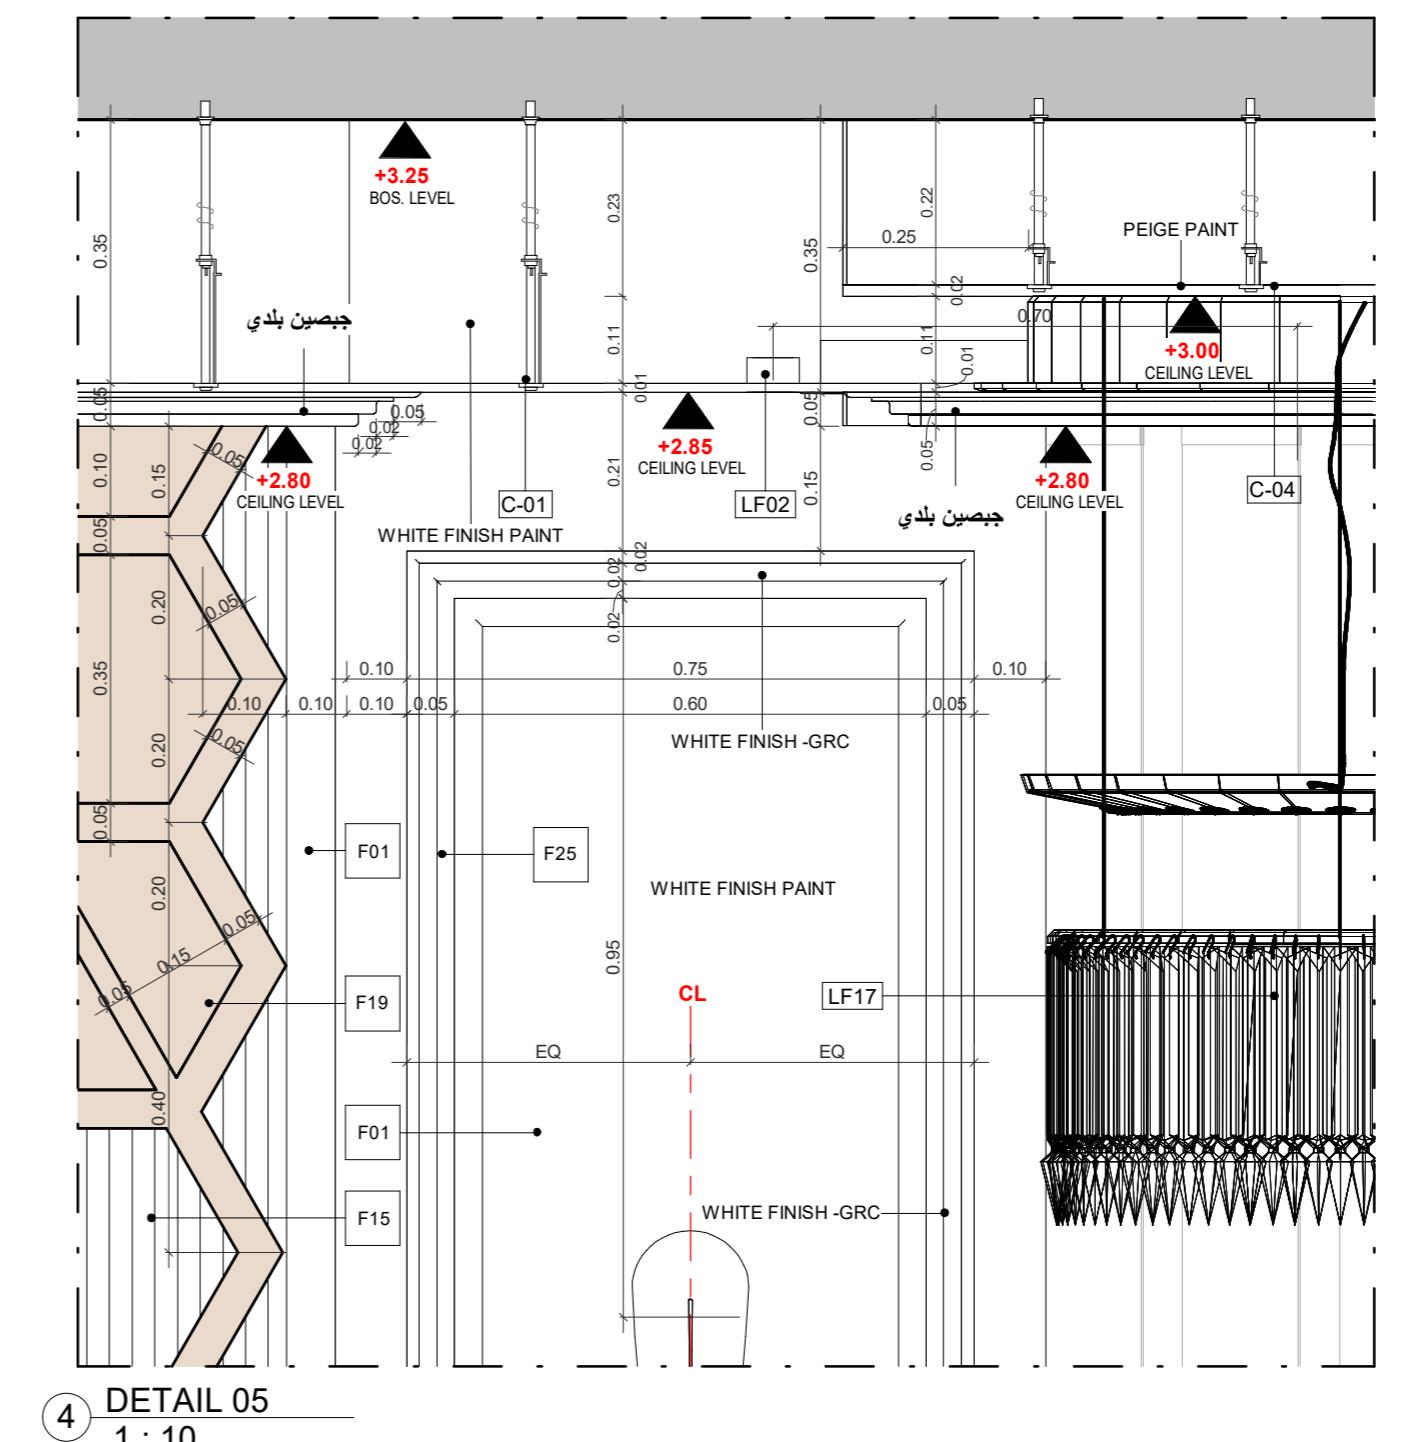


④ DETAIL 05

1 : 10

PROJECT NAME

APARTMENTS BUILDING

NOTES

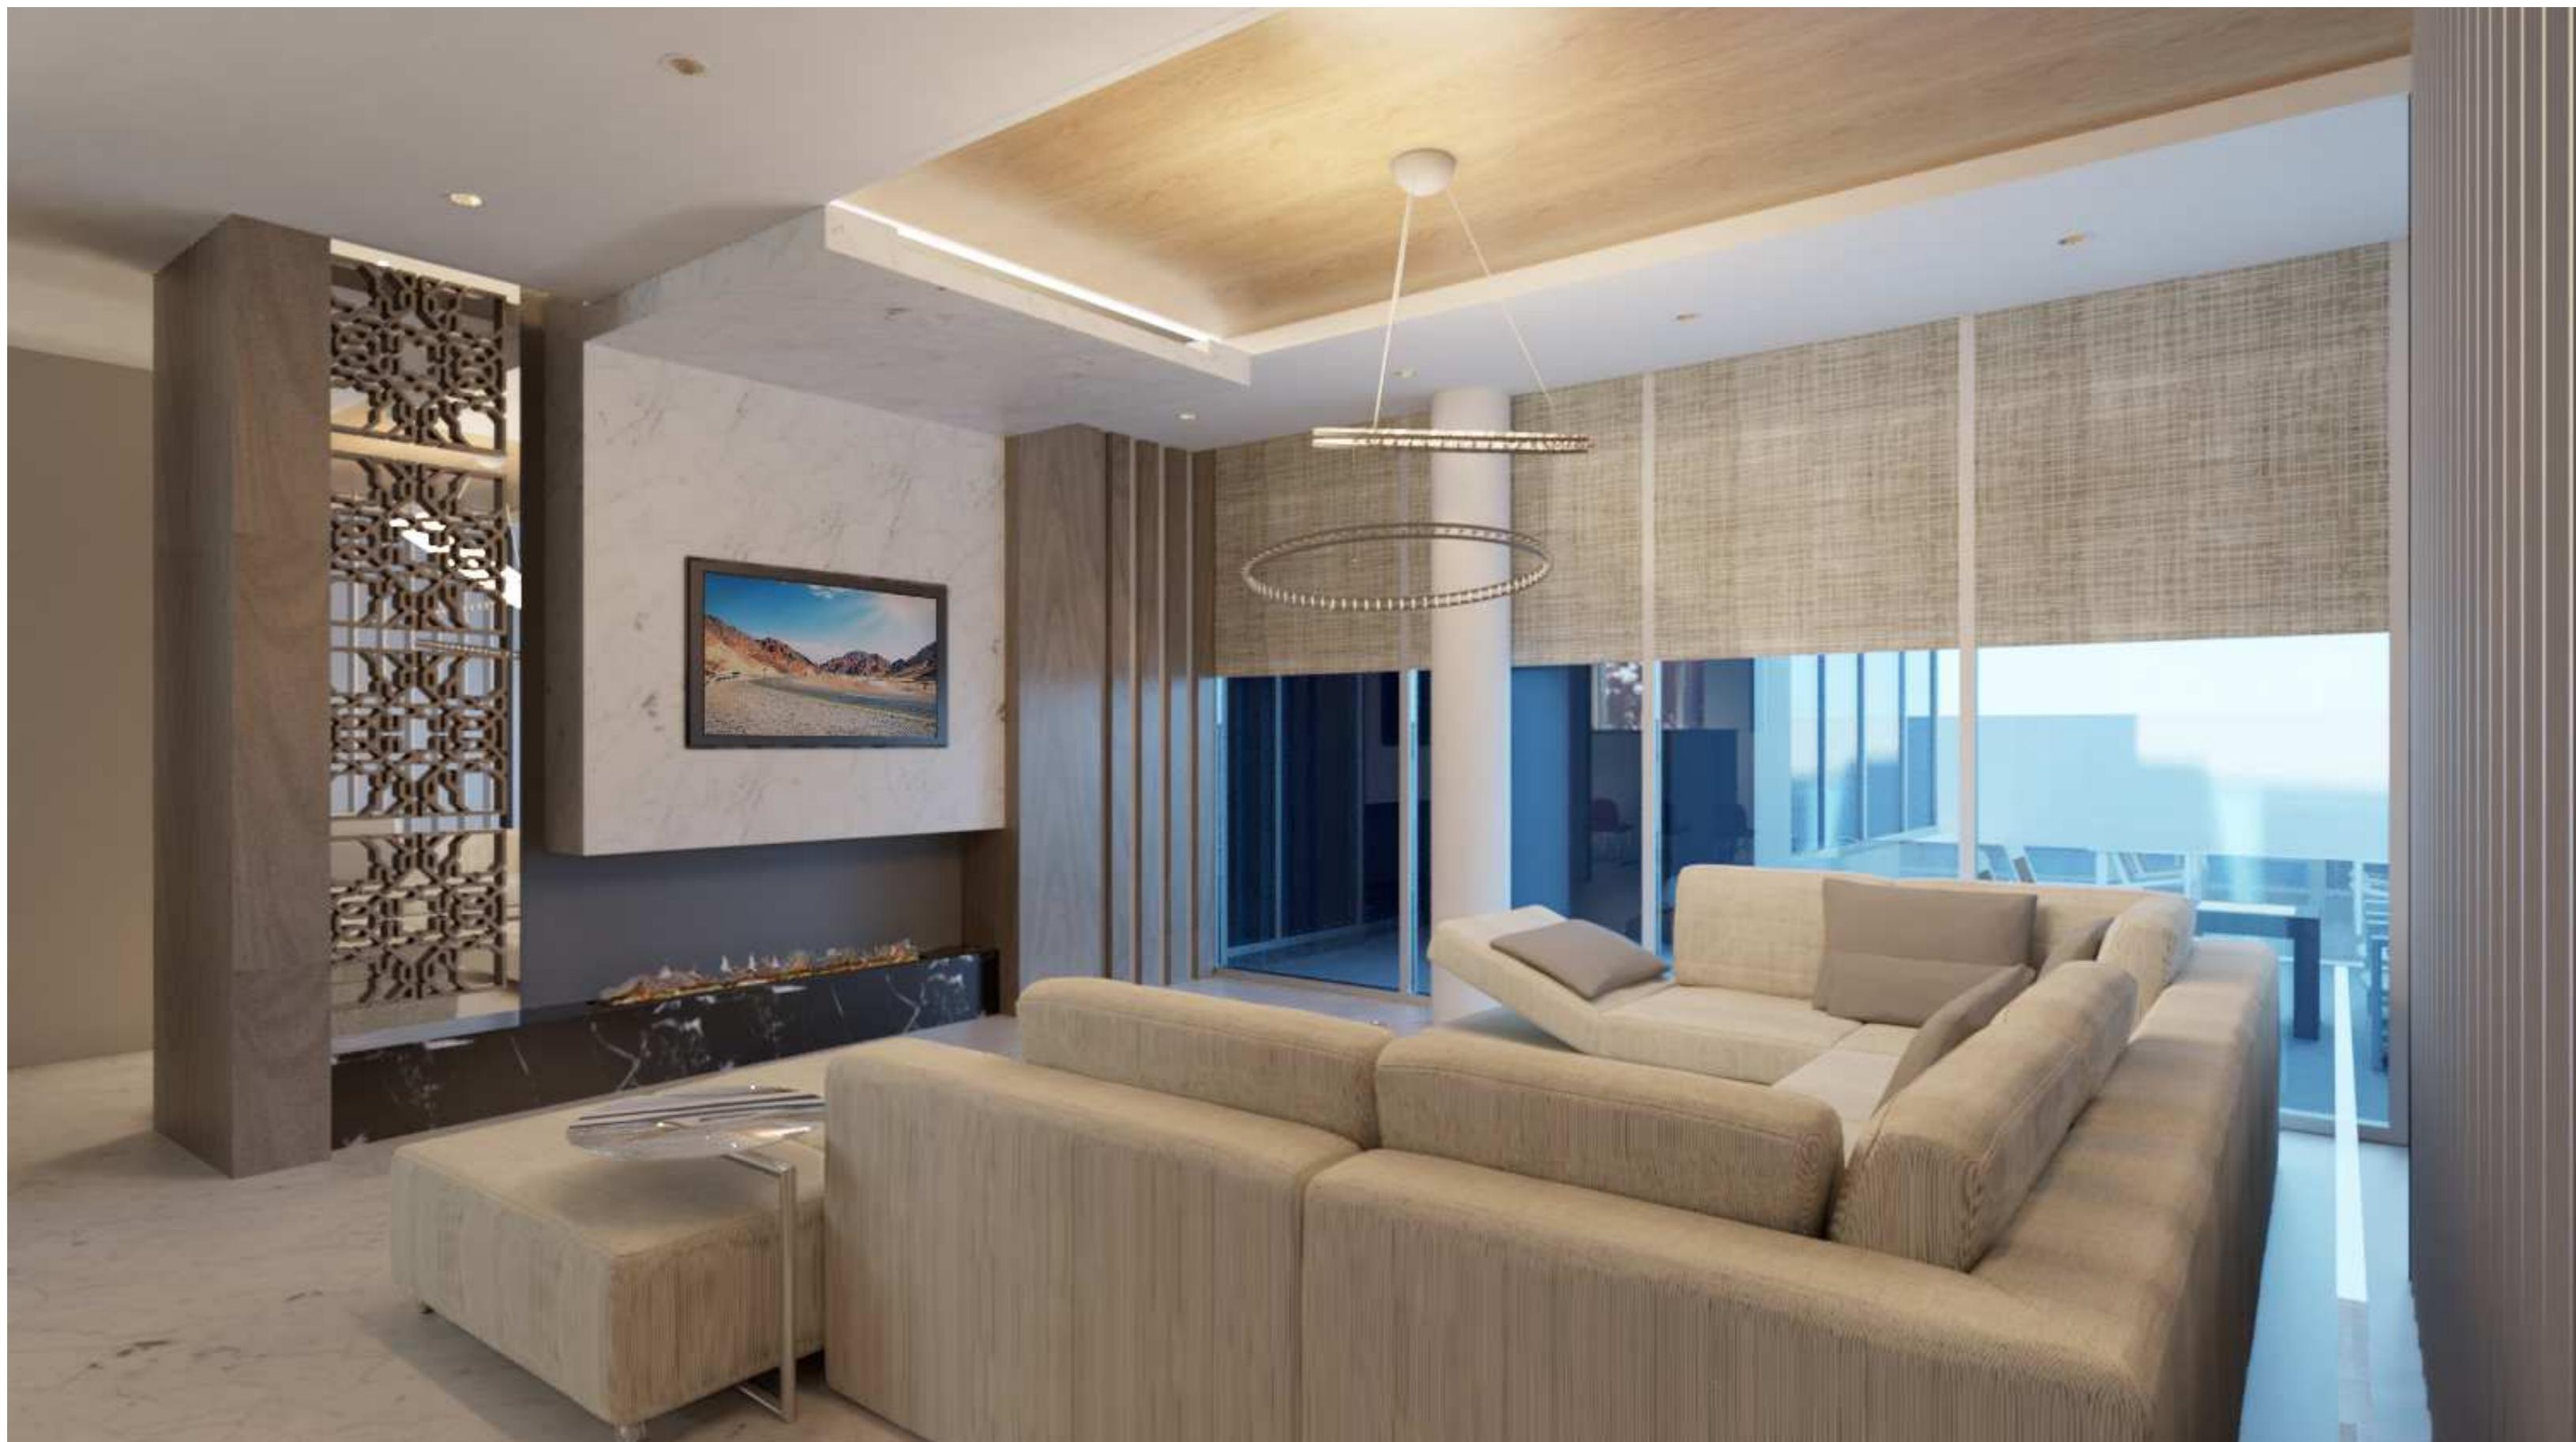

Project Type	Residential
Owner	Khalid Khadir Hasan AL-Saeed
Location	Amman
Plot No.	1659
Basin No.	19
Designed by	A.Shaker Khulief 4809

SHEET NAME
LIVING ROOM-SHOT

ID-4110

Date	08/10/2019
Scale	

PROJECT NAME

APARTMENTS BUILDING

NOTES

FOR FINISHES REFER TO SHEETS:
ID-6000
ID-6001

ROOM NAME

FLOOR FINISH	CEILING FINISH
--------------	----------------

WALL FINISH

FINISHES SCHEDULE		FINISHES SCHEDULE	
Material:	Mark	DESCRIPTION	DESCRIPTION
F01		WHITE PAINT	BEIGE PAINT
F02		GOLD WOOD	TRAVERTINO MARBLE
F03		GOLD STONE	
F04		DARK WOOD	LEATHER
F05		DECORATIVE STONE	PAINT GOLD METAL EFFECT
F06		WOOD	DECORATIVE WOOD
F07		BLACK MARBLE	BEIGE MARBLE
F08		GREY STONE	GREY STONE
F09		CONCRETE FINISH	KITCHENNE WOOD
F10		WALL PAPER	CALCATTÀ
F11			SWIMMING POOL MARBLE
F12			PARQUET
F13			CALCATTÀ
F14			WHITE FINISH GRC

SPOT RECESSED LIGHT

PENDANT LIGHT

HIDDEN LIGHT

CHANDELIER

WALL MOUNTED

NEON RECTANGULAR

Project Type	Residential
Owner	Khalid Khadir Hasan AL-Saeed
Location	Amman
Plot No.	1659
Basin No.	19
Designed by	A.Shaker Khulief 4809






SHEET NAME

GROUND FLOOR- LIVING ROOM

ID-4111

Date 08/10/2019

Scale As indicated

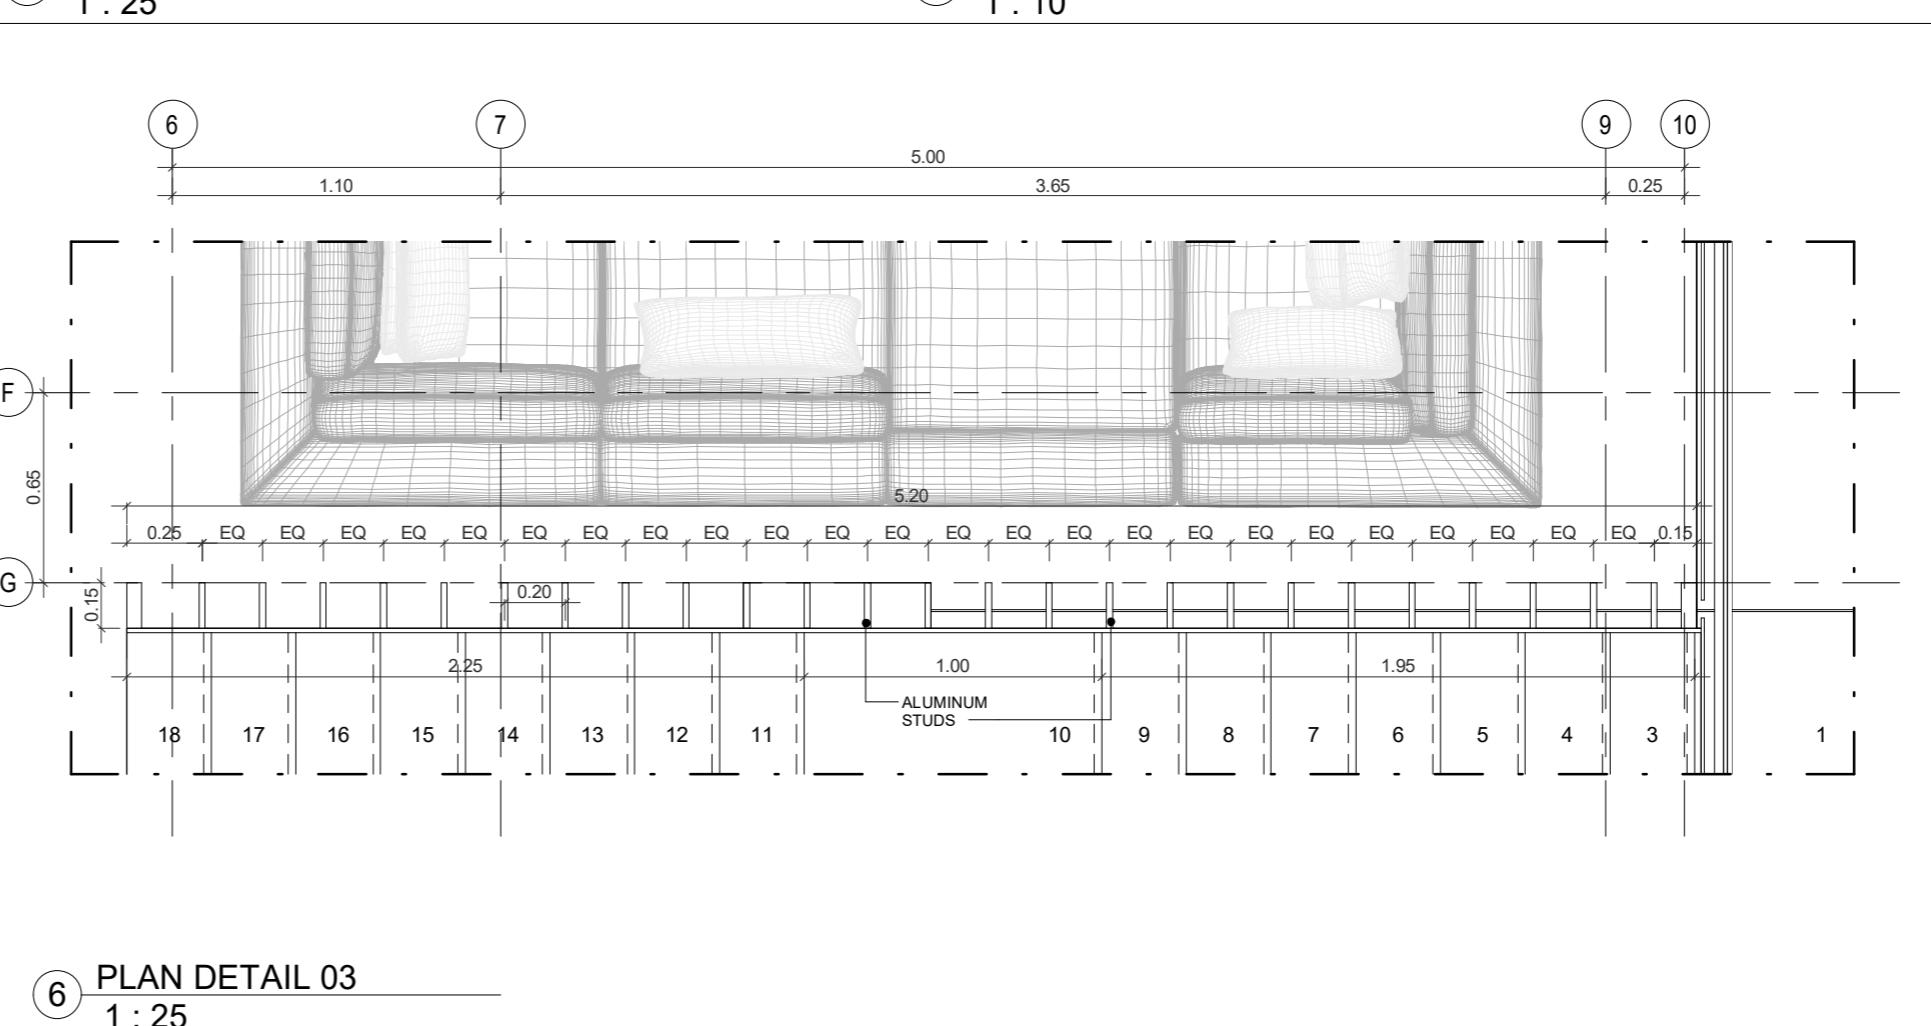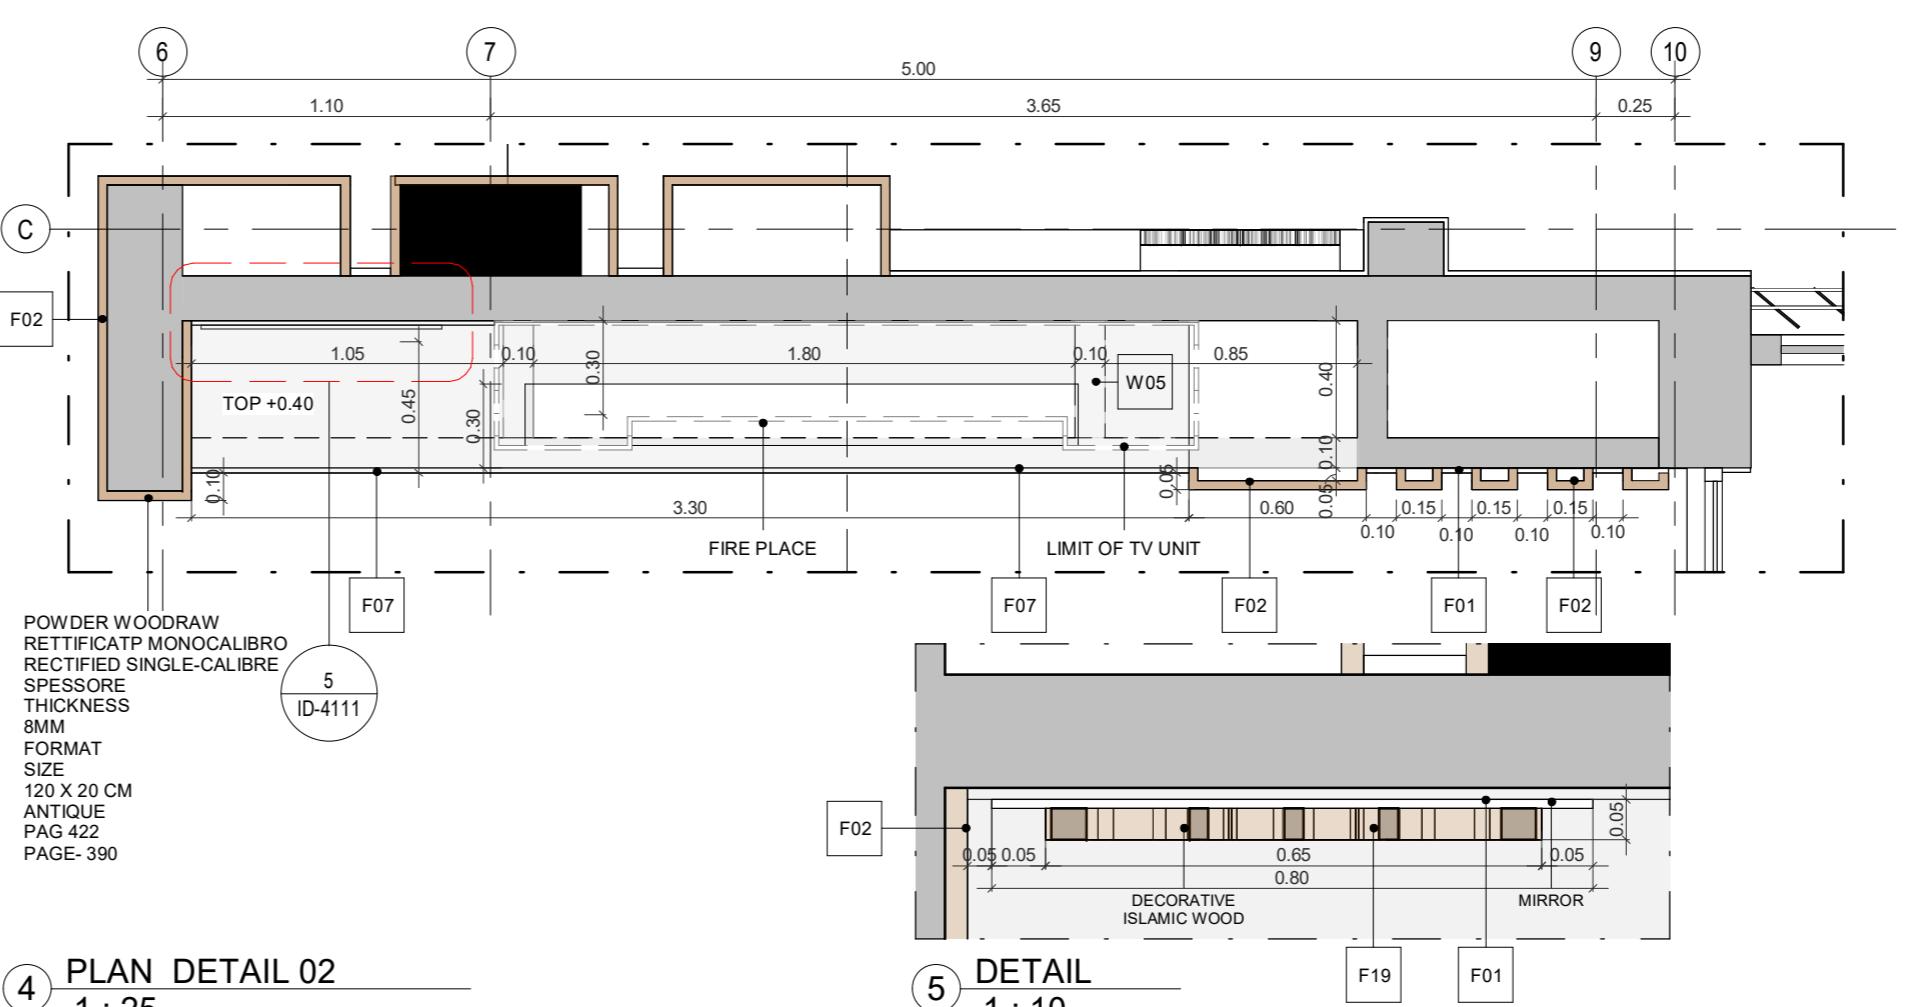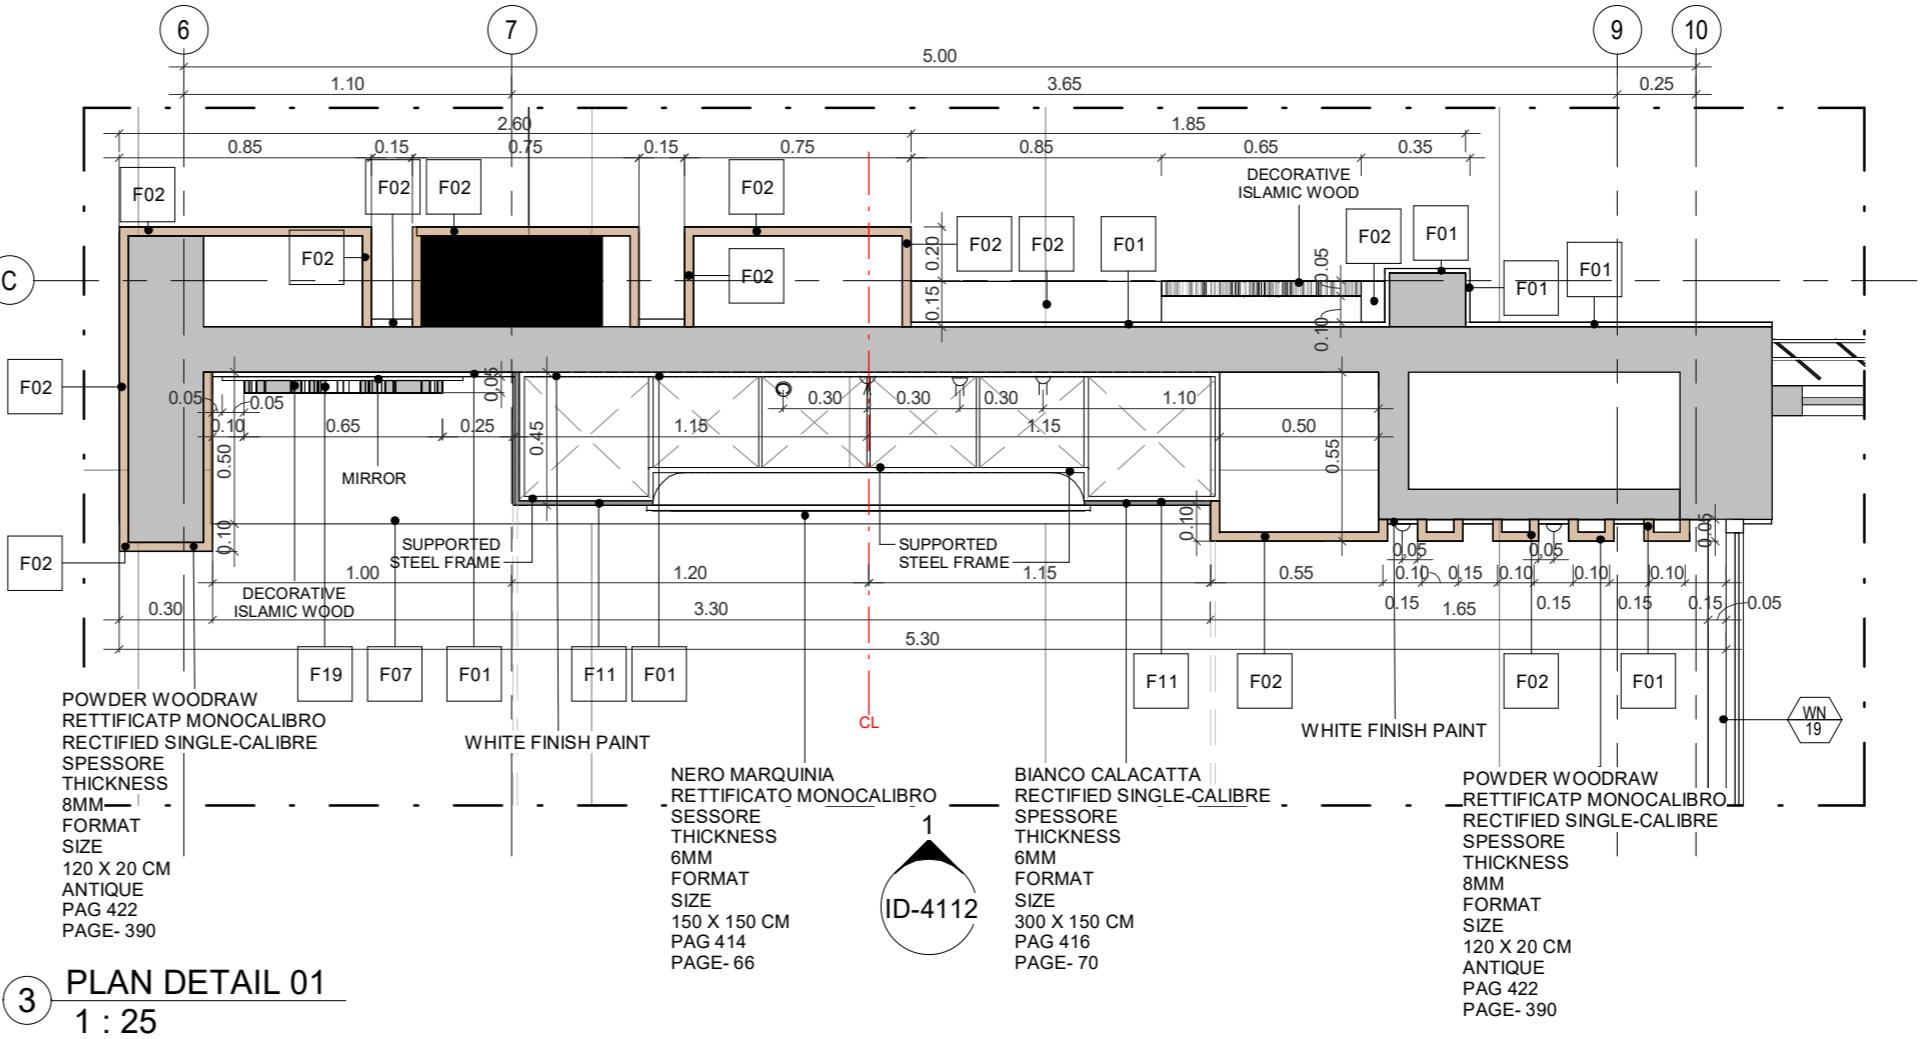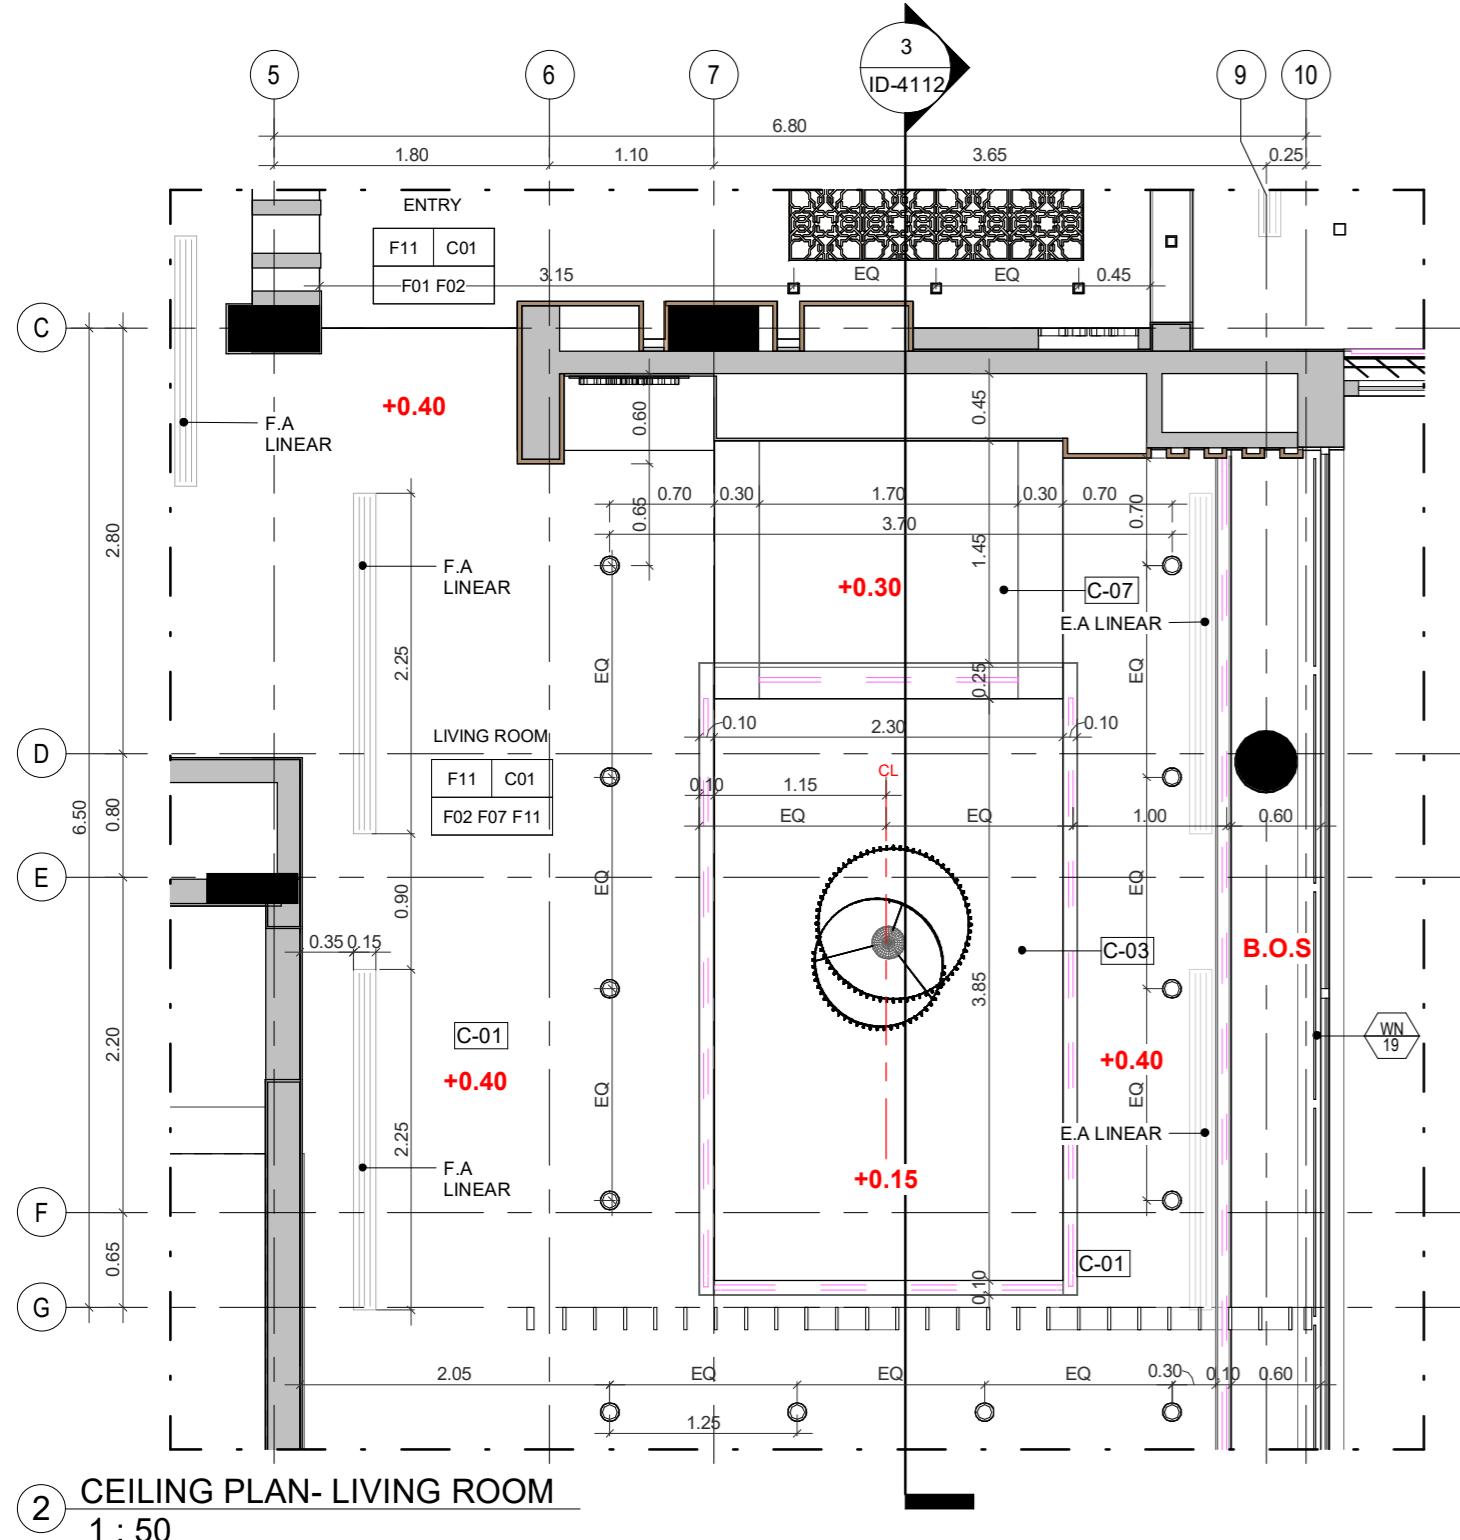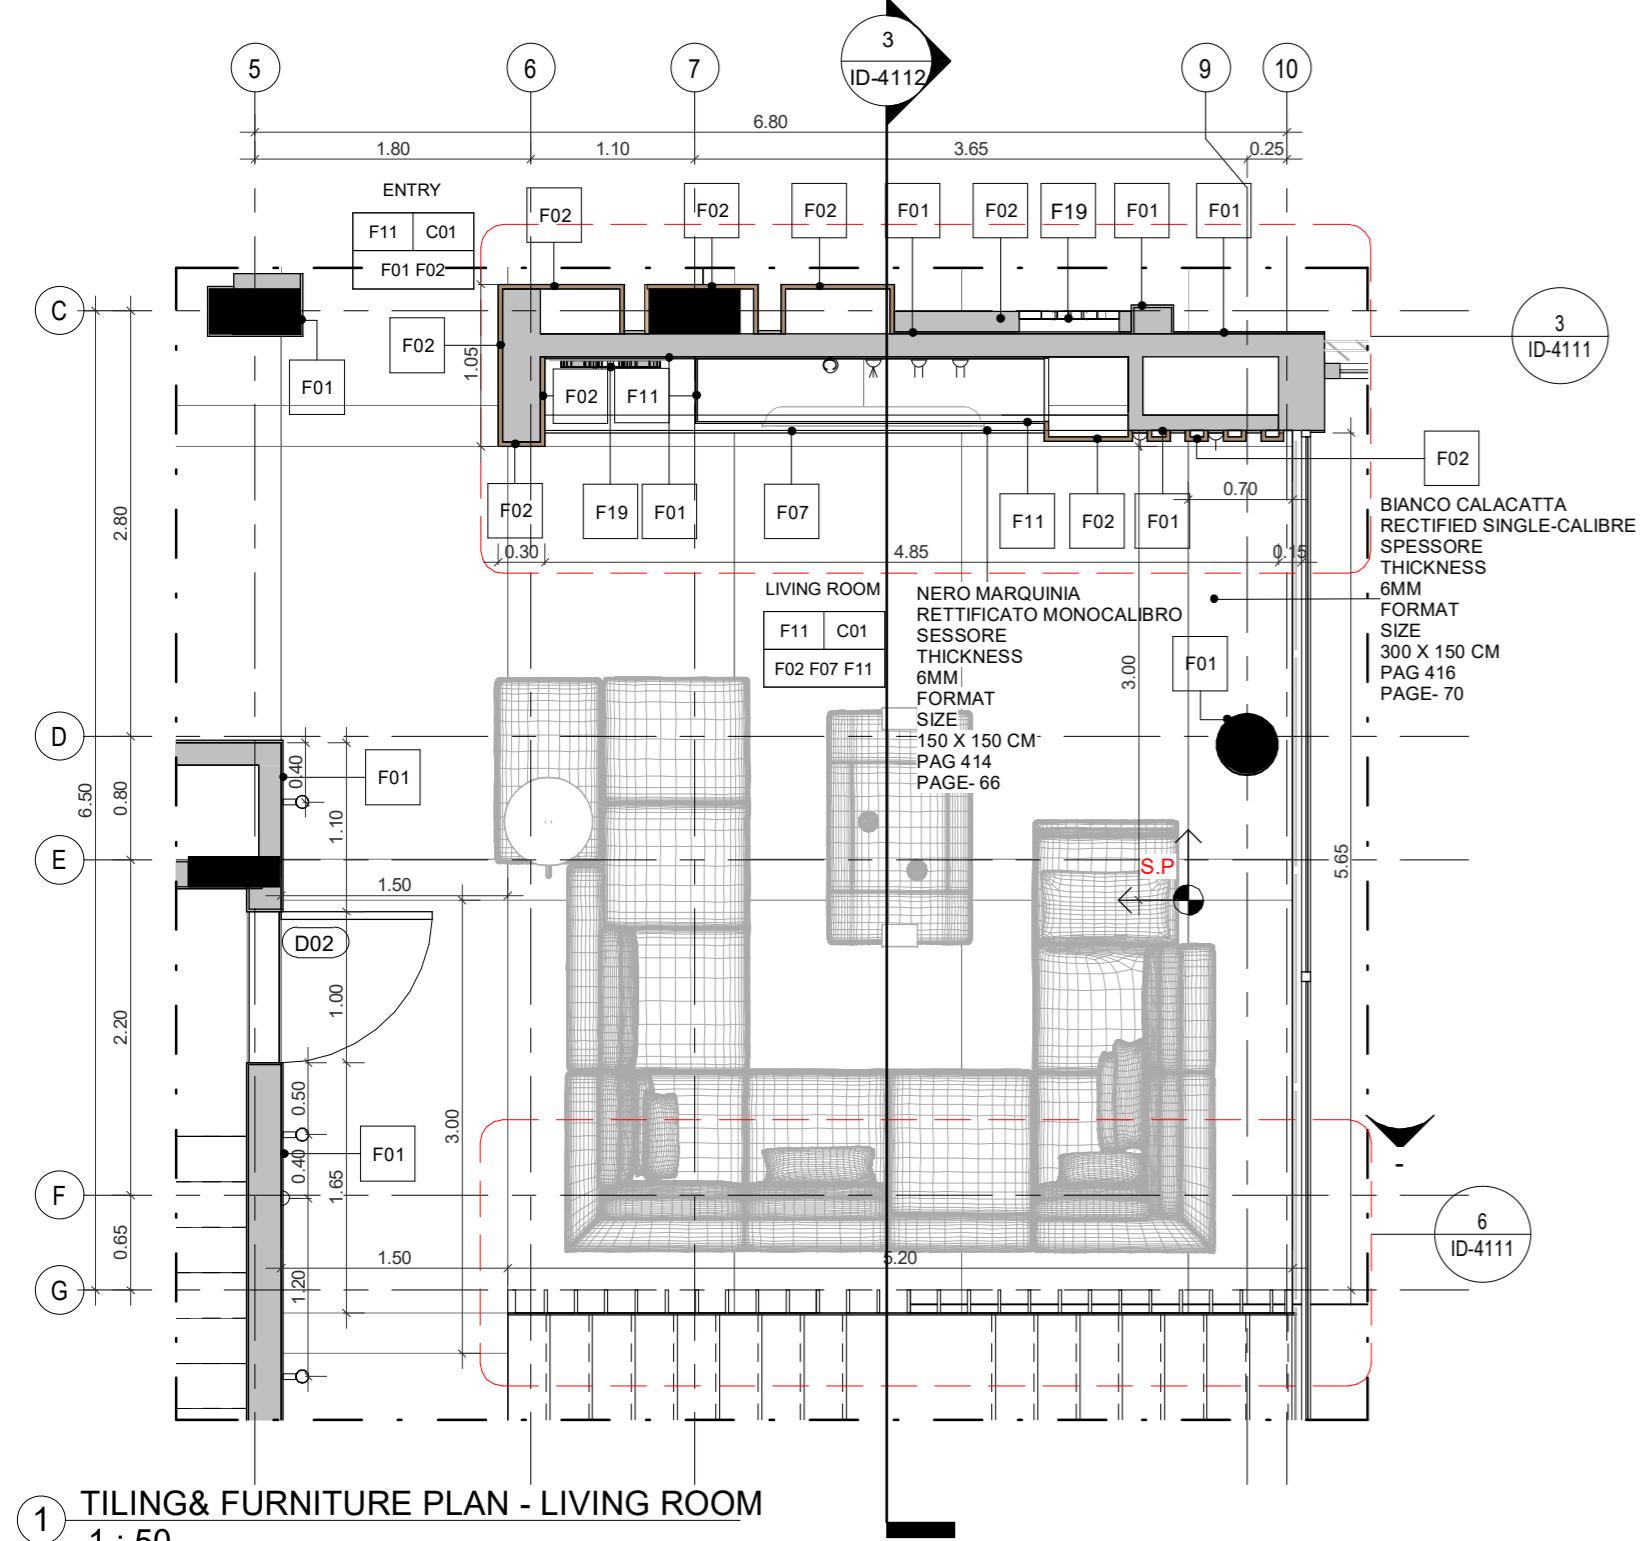

PROJECT NAME

APARTMENTS BUILDING

NOTES



Project Type	Residential
Owner	Khalid Khadir Hasan AL-Saeed
Location	Amman
Plot No.	1659
Basin No.	19
Designed by	A.Shaker Khulief 4809

SHEET NAME
MASTER BEDROOM &BATHROOM-SHOTS

ID-4120

Date	08/10/2019
Scale	

PROJECT NAME

APARTMENTS BUILDING

NOTES

SHOT 1



SHOT 2



Project Type	Residential
Owner	Khalid Khadir Hasan AL-Saeed
Location	Amman
Plot No.	1659
Basin No.	19
Designed by	A.Shaker Khulief 4809

SHEET NAME
MASTER BEDROOM &BATHROOM-SHOTS

ID-4121

Date	08/10/2019
Scale	

PROJECT NAME

APARTMENTS BUILDING

NOTES

FOR FINISHES REFER TO SHEETS:
ID-6000
ID-6001

ROOM NAME	FLOOR FINISH	CEILING FINISH
-----------	--------------	----------------

WALL FINISH

FINISHES SCHEDULE		FINISHES SCHEDULE	
Material: Mark	DESCRIPTION	Material: Mark	DESCRIPTION
F01	WHITE PAINT	F15	BEIGE PAINT
F02	GOLD WOOD	F16	TRAVERTINO MARBLE
F03	GOLD STONE	F17	LEATHER
F04	DARK WOOD	F18	PAINT GOLD METAL EFFECT
F05	DECORATIVE STONE WOOD	F19	DECORATIVE WOOD
F06	BLACK MARBLE	F20	GREY STONE
F07	BEIGE MARBLE	F21	CONCRETE FINISH
F08	ONICE GRIGIO	F10	KITCHENNETE WOOD
F09	RETIFICATO MONOCALIBRO	F11	CALCATTA
F10	SPESSORE THICKNESS	F12	SWIMMING POOL MARBLE
F11	FORMAT SIZE	F13	BLACK PAINT CALCATTA
F12	120 X 60 CM	F14	WHITE FINISH GRC
F13	PAG 415 PAGE- 124	F15	
F14		F16	
F15		F17	
F16		F18	
F17		F19	
F18		F20	
F19		F21	
F20		F10	
F21		F11	
F22		F12	
F23		F13	
F24		F14	
F25		F15	

Project Type	Residential
Owner	Khalid Khadir Hasan AL-Saeed
Location	Amman
Plot No.	1659
Basin No.	19
Designed by	A.Shaker Khulief 4809


SHEET NAME

GROUND FLOOR- MASTER BEDROOM & BATHROOM

ID-4122

Date 08/10/2019

Scale 1 : 25

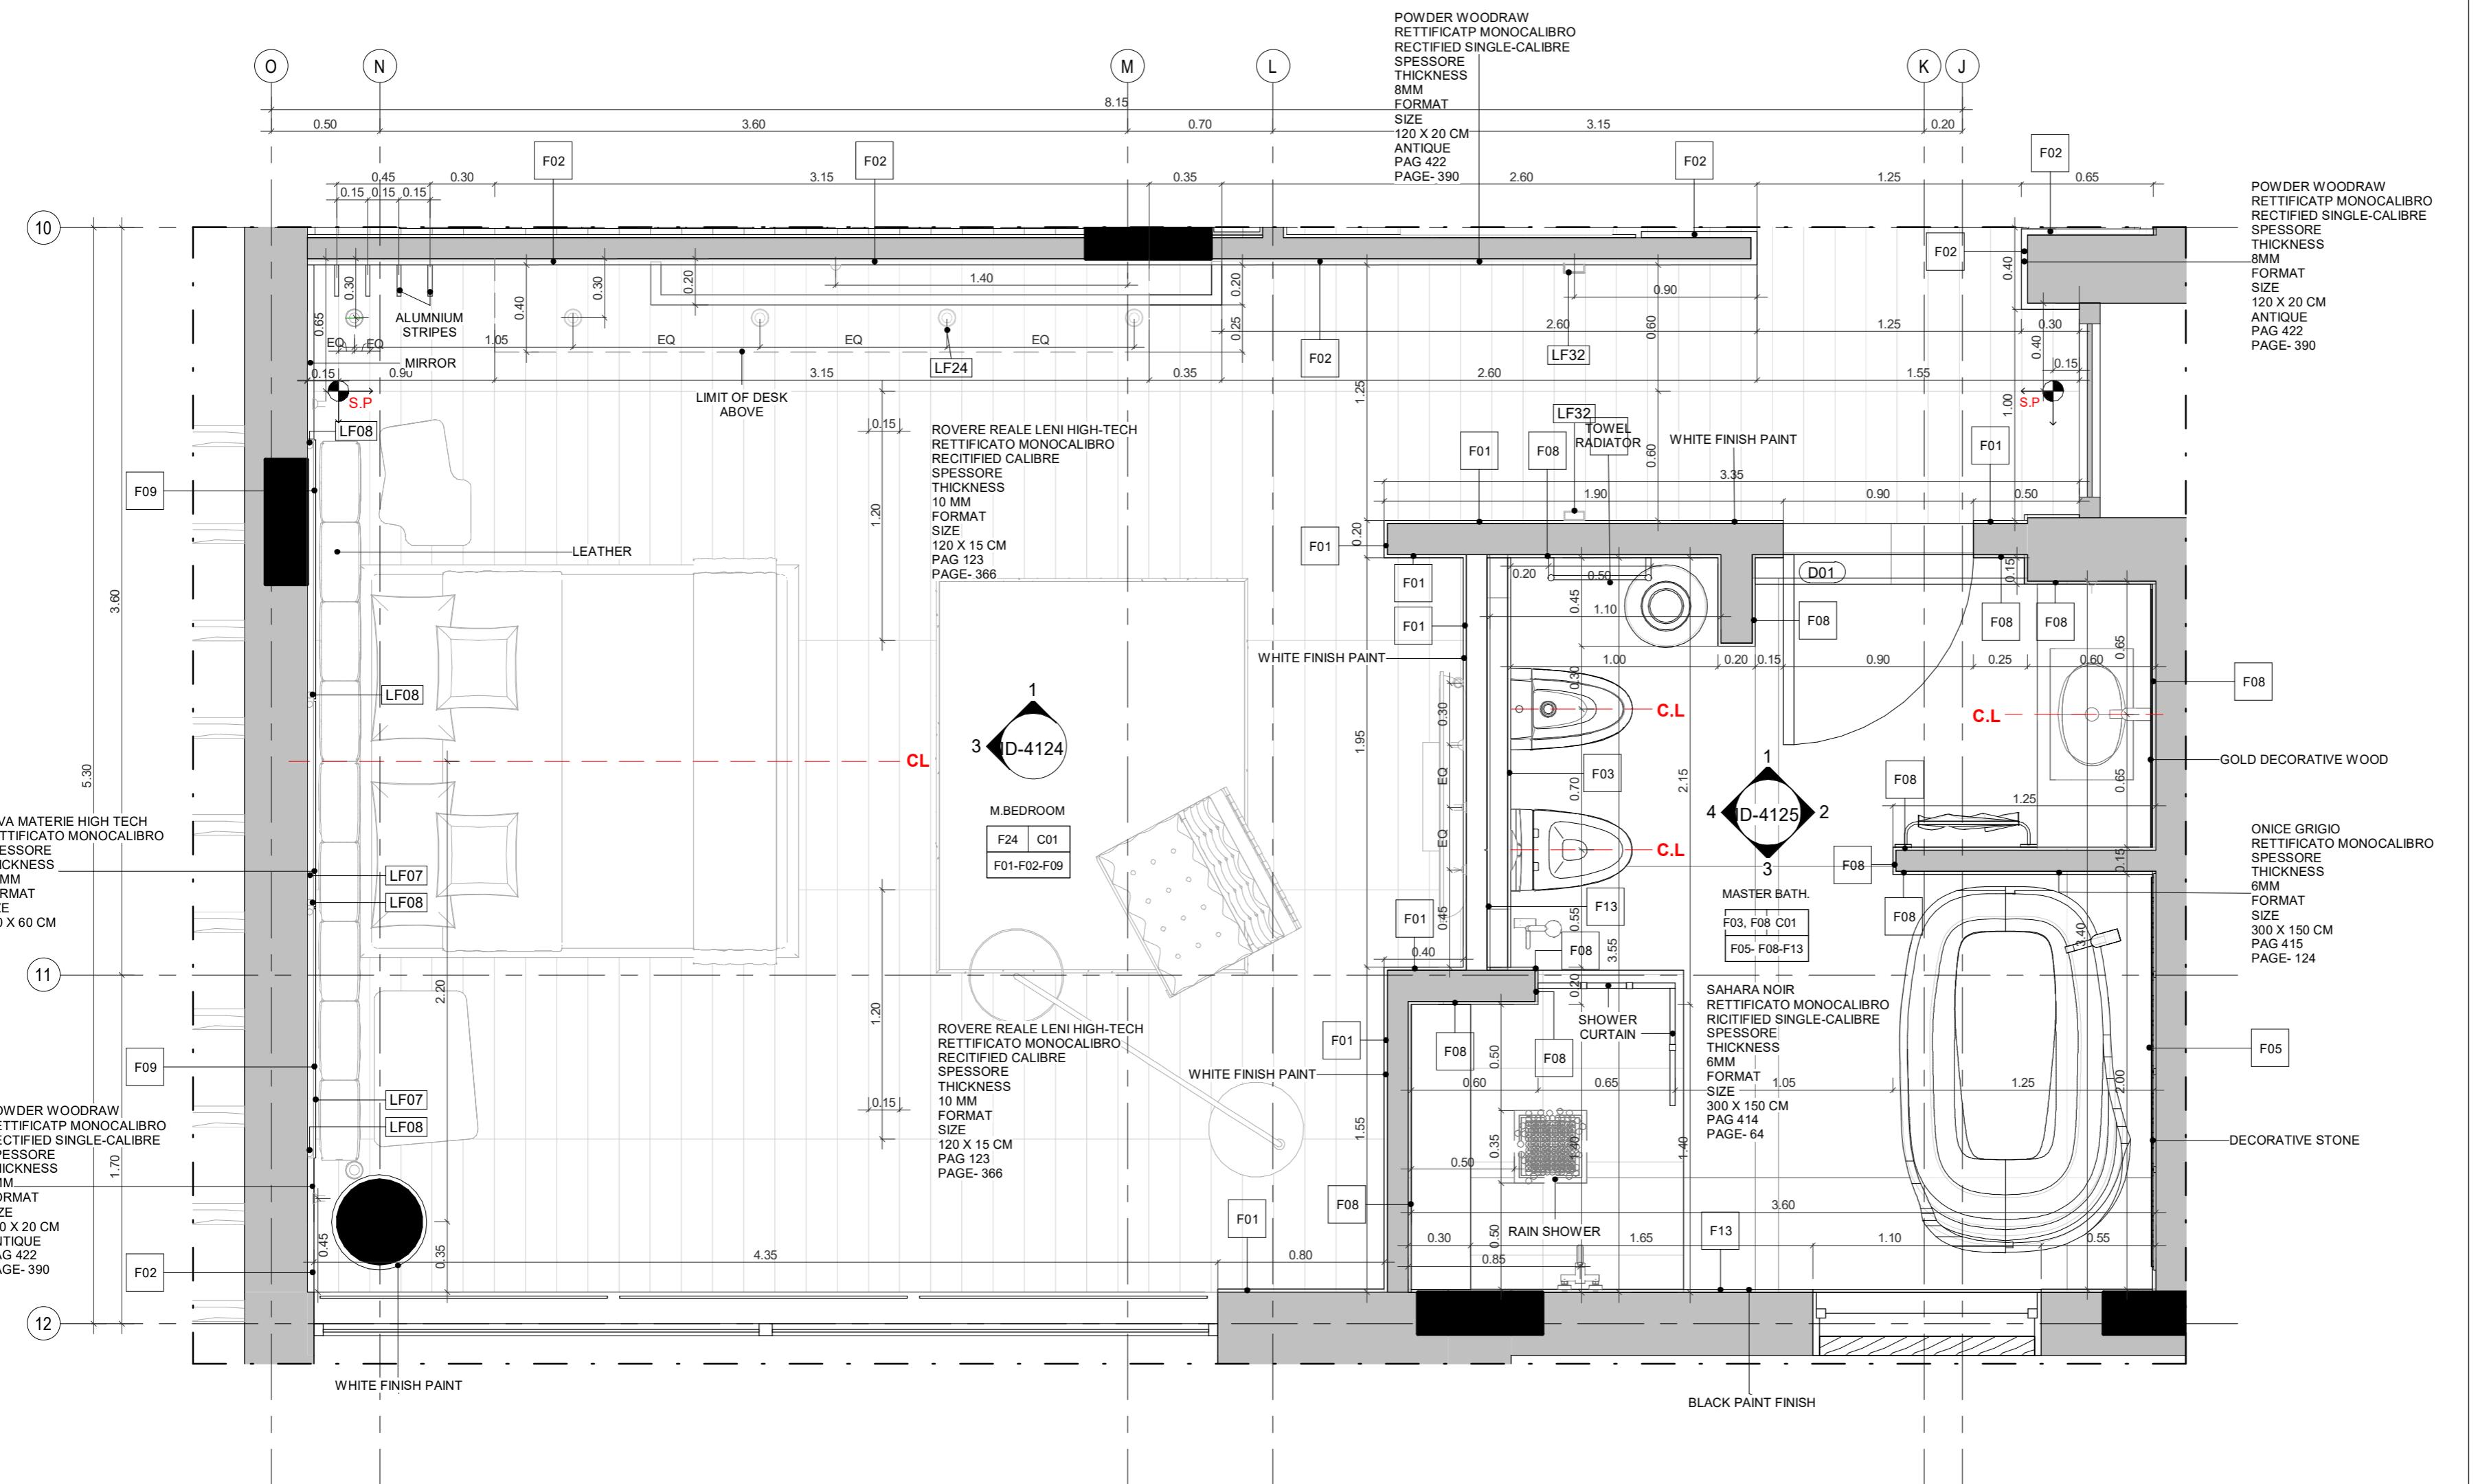

PROJECT NAME

APARTMENTS BUILDING

NOTES

FOR FINISHES REFER TO SHEETS:
ID-6000
ID-6001

ROOM NAME

FLOOR FINISH	CEILING FINISH
--------------	----------------

WALL FINISH

FINISHES SCHEDULE		FINISHES SCHEDULE	
Material: Mark	DESCRIPTION	Material: Mark	DESCRIPTION
F01	WHITE PAINT	F15	BEIGE PAINT
F02	GOLD WOOD	F16	TRAVERTINO MARBLE
F03	GOLD STONE	F17	LEATHER
F04	DARK WOOD	F18	PAINT GOLD METAL EFFECT
F05	DECORATIVE STONE	F19	DECORATIVE WOOD
F06	WOOD	F20	GREY STONE
F07	BLACK MARBLE	F21	CONCRETE FINISH
F08	BEIGE MARBLE	F11	CALCATTIA WOOD
F09	GREY STONE	F12	SWIMMING POOL MARBLE
F10	WALL PAPER	F23	SWIMMING POOL WALL FINISH
F11	CALCATTIA	F13	BLACK PAINT
F12	SWIMMING POOL MARBLE	F24	PARQUET
F13	WHITE FINISH GRC	F14	CALCATTIA

—	SPOT RECESSED LIGHT
—	PENDANT LIGHT
—	HIDDEN LIGHT
—	CHANDELIER
—	WALL MOUNTED
—	NEON RECTANGULAR

Project Type	Residential
Owner	Khalid Khadir Hasan AL-Saeed
Location	Amman
Plot No.	1659
Basin No.	19
Designed by	A.Shaker Khulief 4809


SHEET NAME

GROUND FLOOR- MASTER BEDROOM & BATHROOM

ID-4123

Date 08/10/2019

Scale As indicated

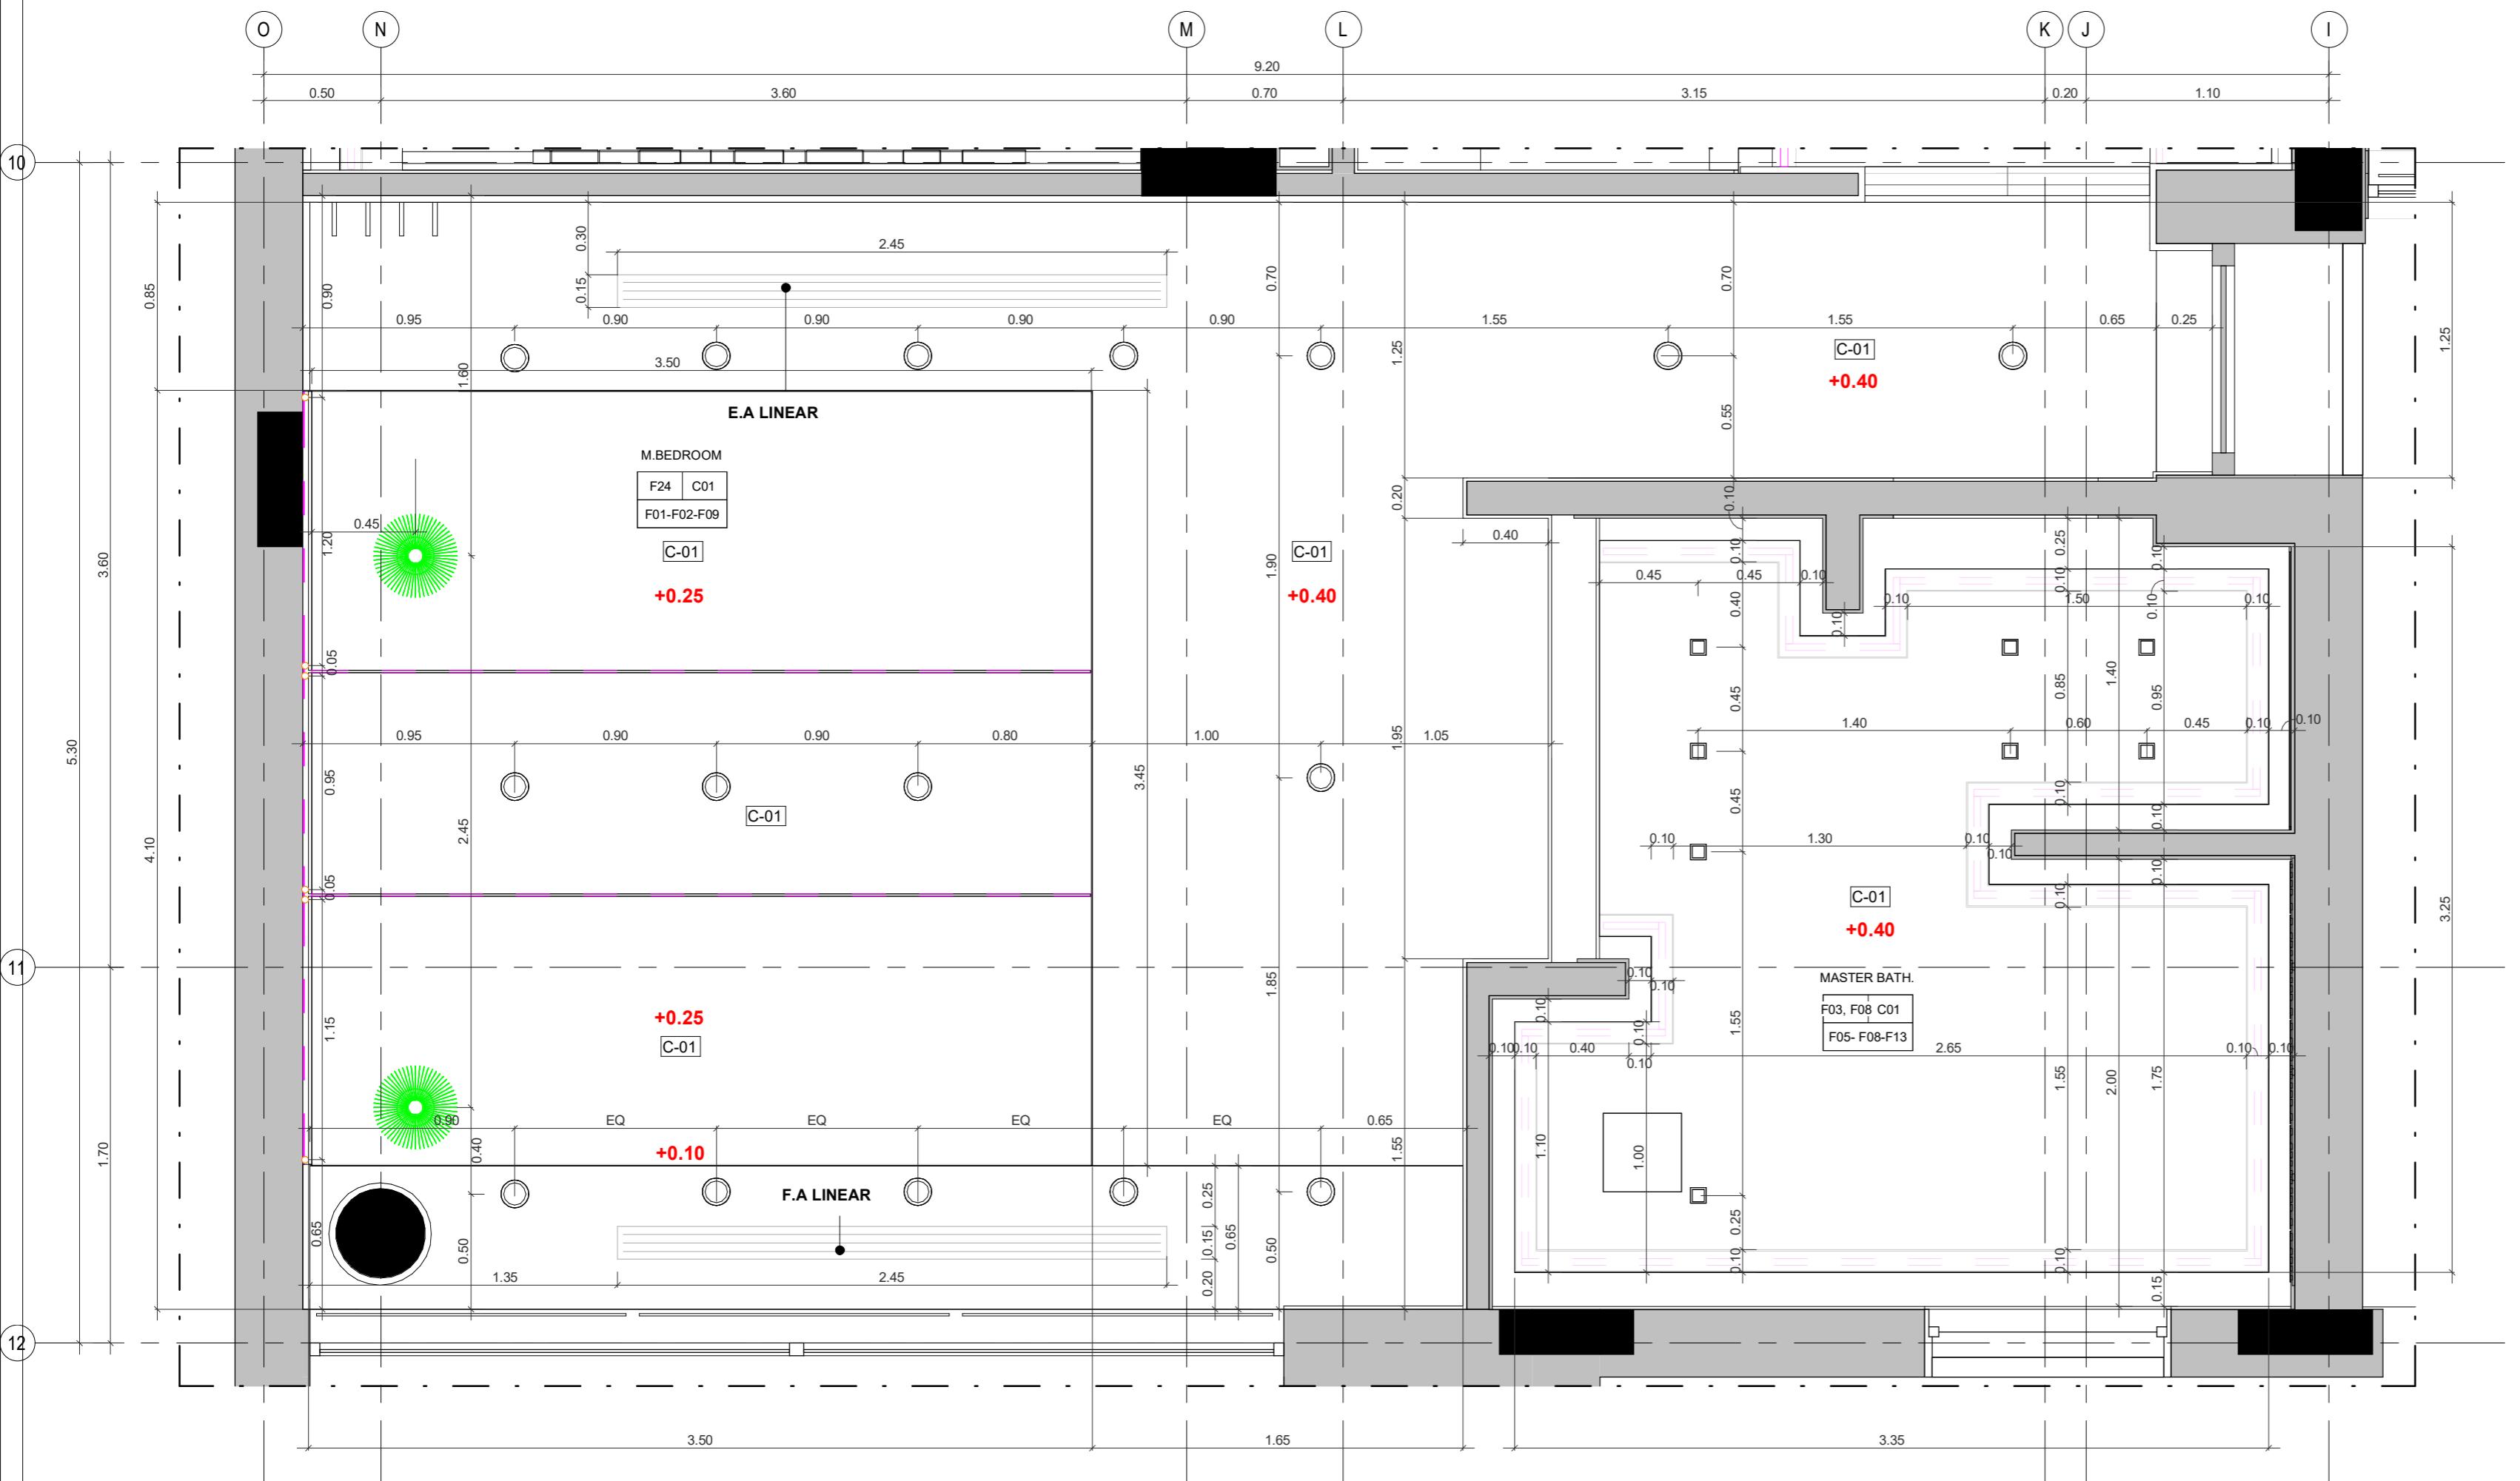



PROJECT NAME

APARTMENTS BUILDING

NOTES

FOR FINISHES REFER TO SHEETS:
ID-6000
ID-6001

ROOM NAME

FLOOR FINISH CEILING FINISH

WALL FINISH

FINISHES SCHEDULE		FINISHES SCHEDULE	
Material: Mark	DESCRIPTION	Material: Mark	DESCRIPTION
F01	WHITE PAINT	F15	BEIGE PAINT
F02	GOLD WOOD	F16	TRAVERTIMO MARBLE
F03	GOLD STONE	F17	LEATHER
F04	DARK WOOD	F18	PAINT GOLD METAL EFFECT
F05	DECORATIVE STONE	F19	DECORATIVE WOOD
F06	WOOD	F20	GREY STONE
F07	BLACK MARBLE	F21	CONCRETE FINISH
F08	BEIGE MARBLE	F22	KITCHENNETE WOOD
F09	GREY STONE	F23	SWIMMING POOL WALL FINISH
F10	WALL PAPER	F24	PARQUET
F11	CALCATTA	F25	WHITE FINISH GRC
F12	SWIMMING POOL MARBLE		
F13	BLACK PAINT		
F14	CALCATTA		


Project Type	Residential
Owner	Khalid Khadir Hasan AL-Saeed
Location	Amman
Plot No.	1659
Basin No.	19
Designed by	A.Shaker Khulief 4809

SHEET NAME


**GROUND FLOOR- MASTER
BEDROOM & BATHROOM**

ID-4124

Date	08/10/2019
Scale	1 : 25




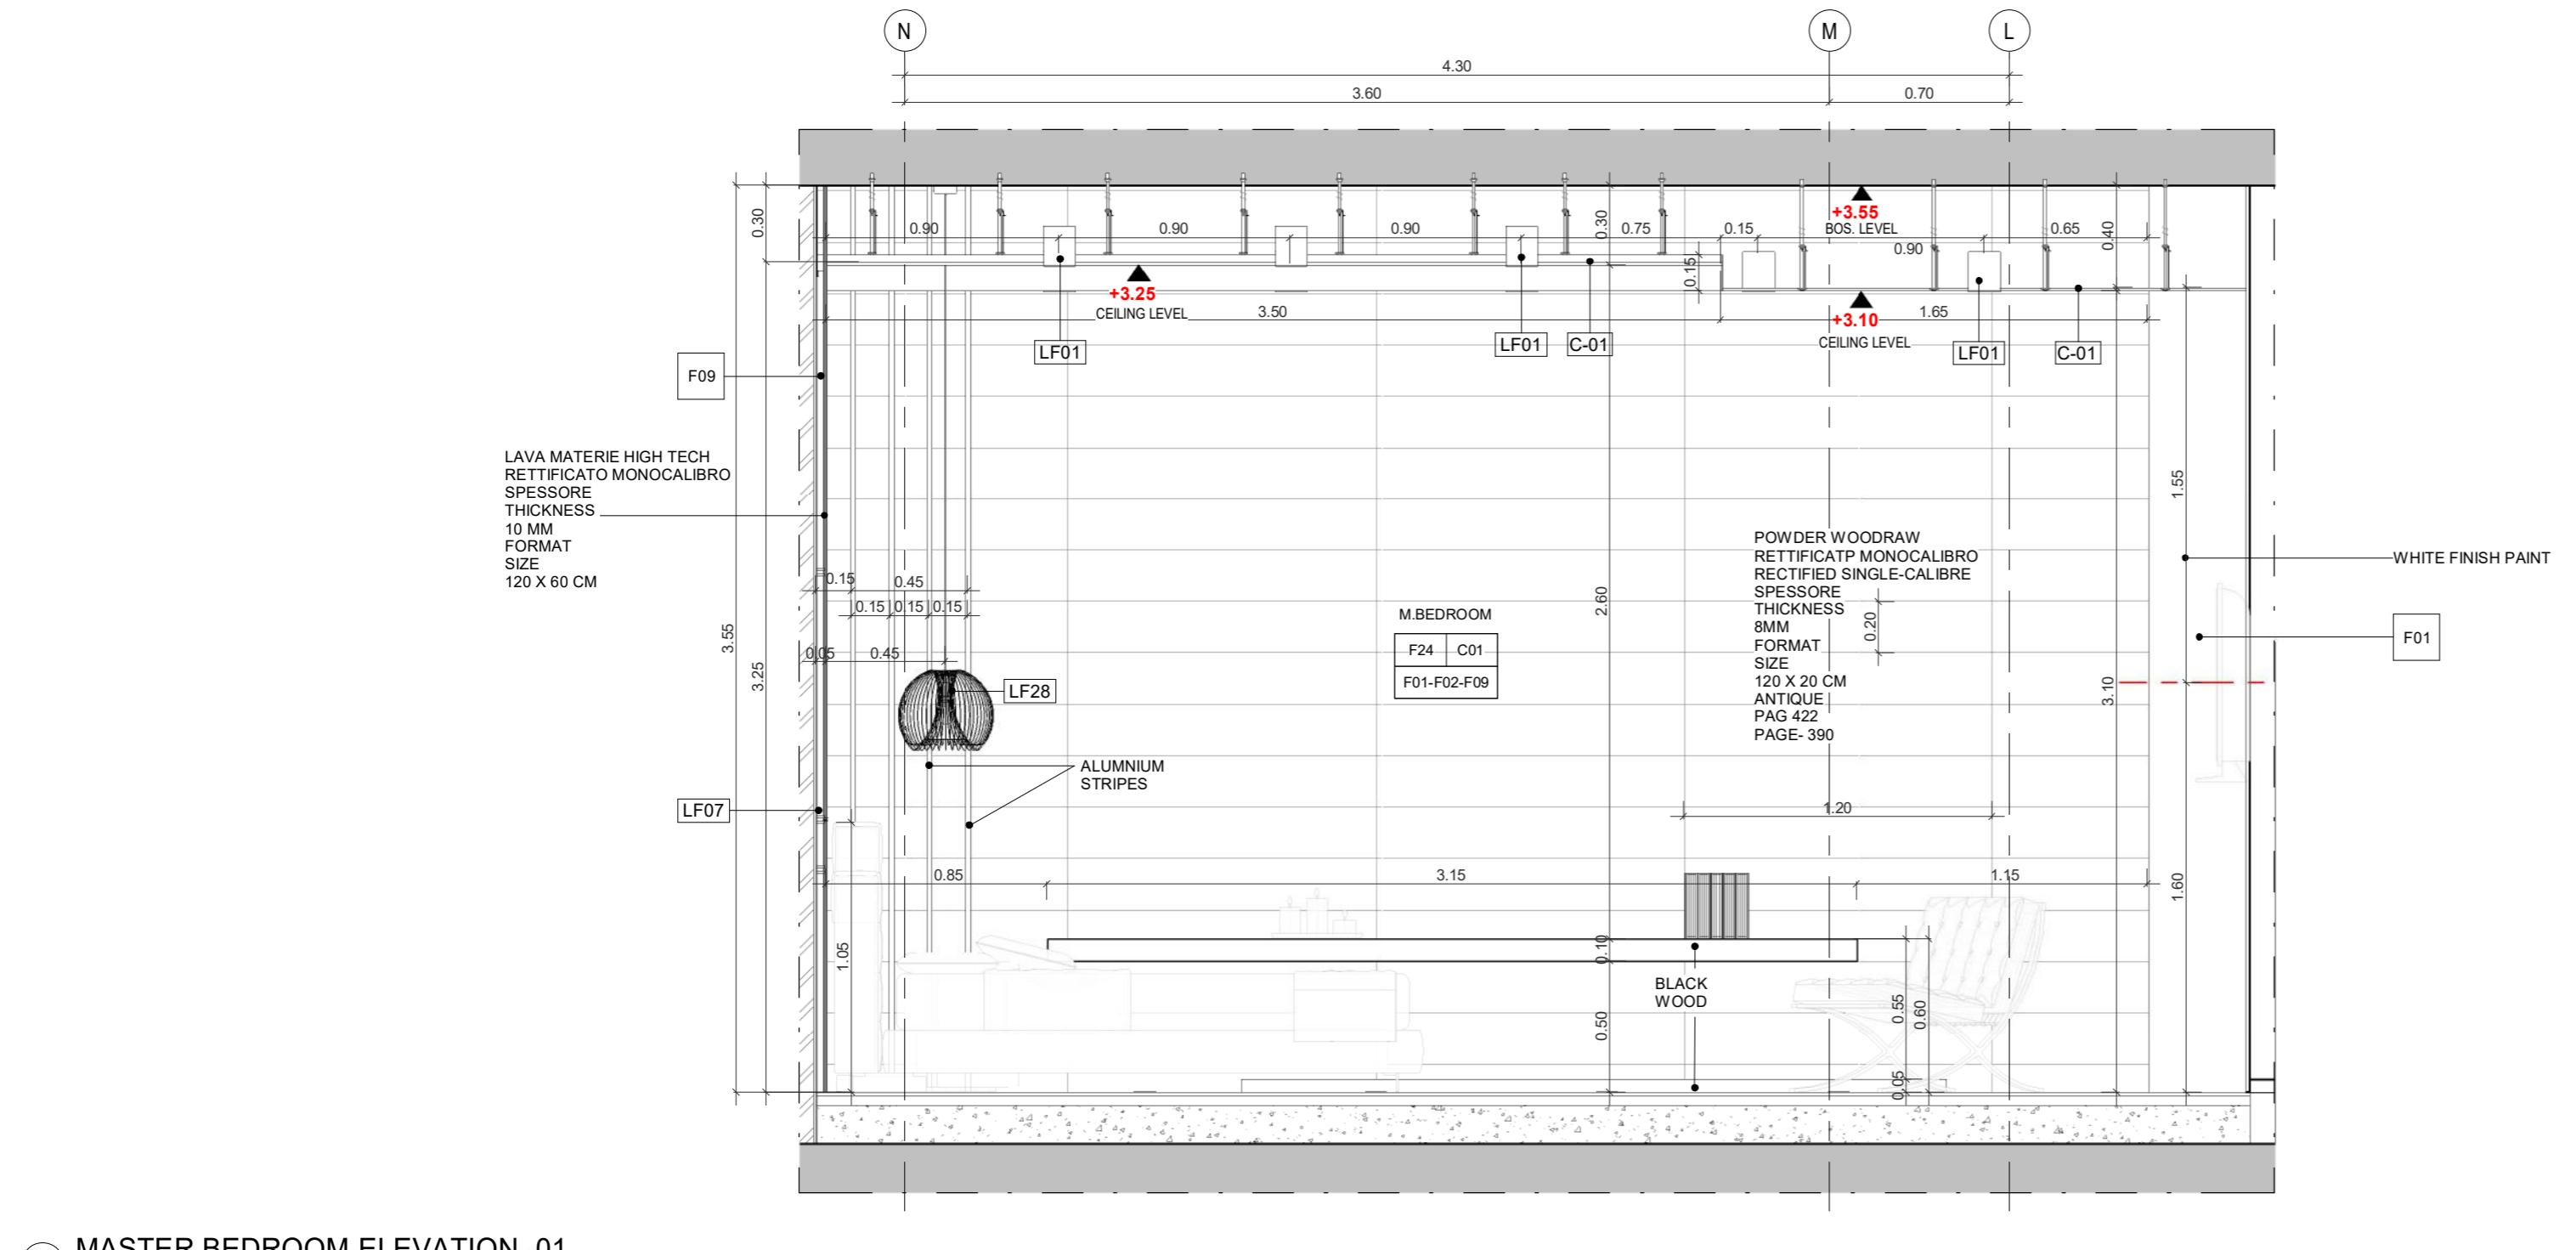


1 MASTER BEDROOM-ELEVATION -01
1 : 25

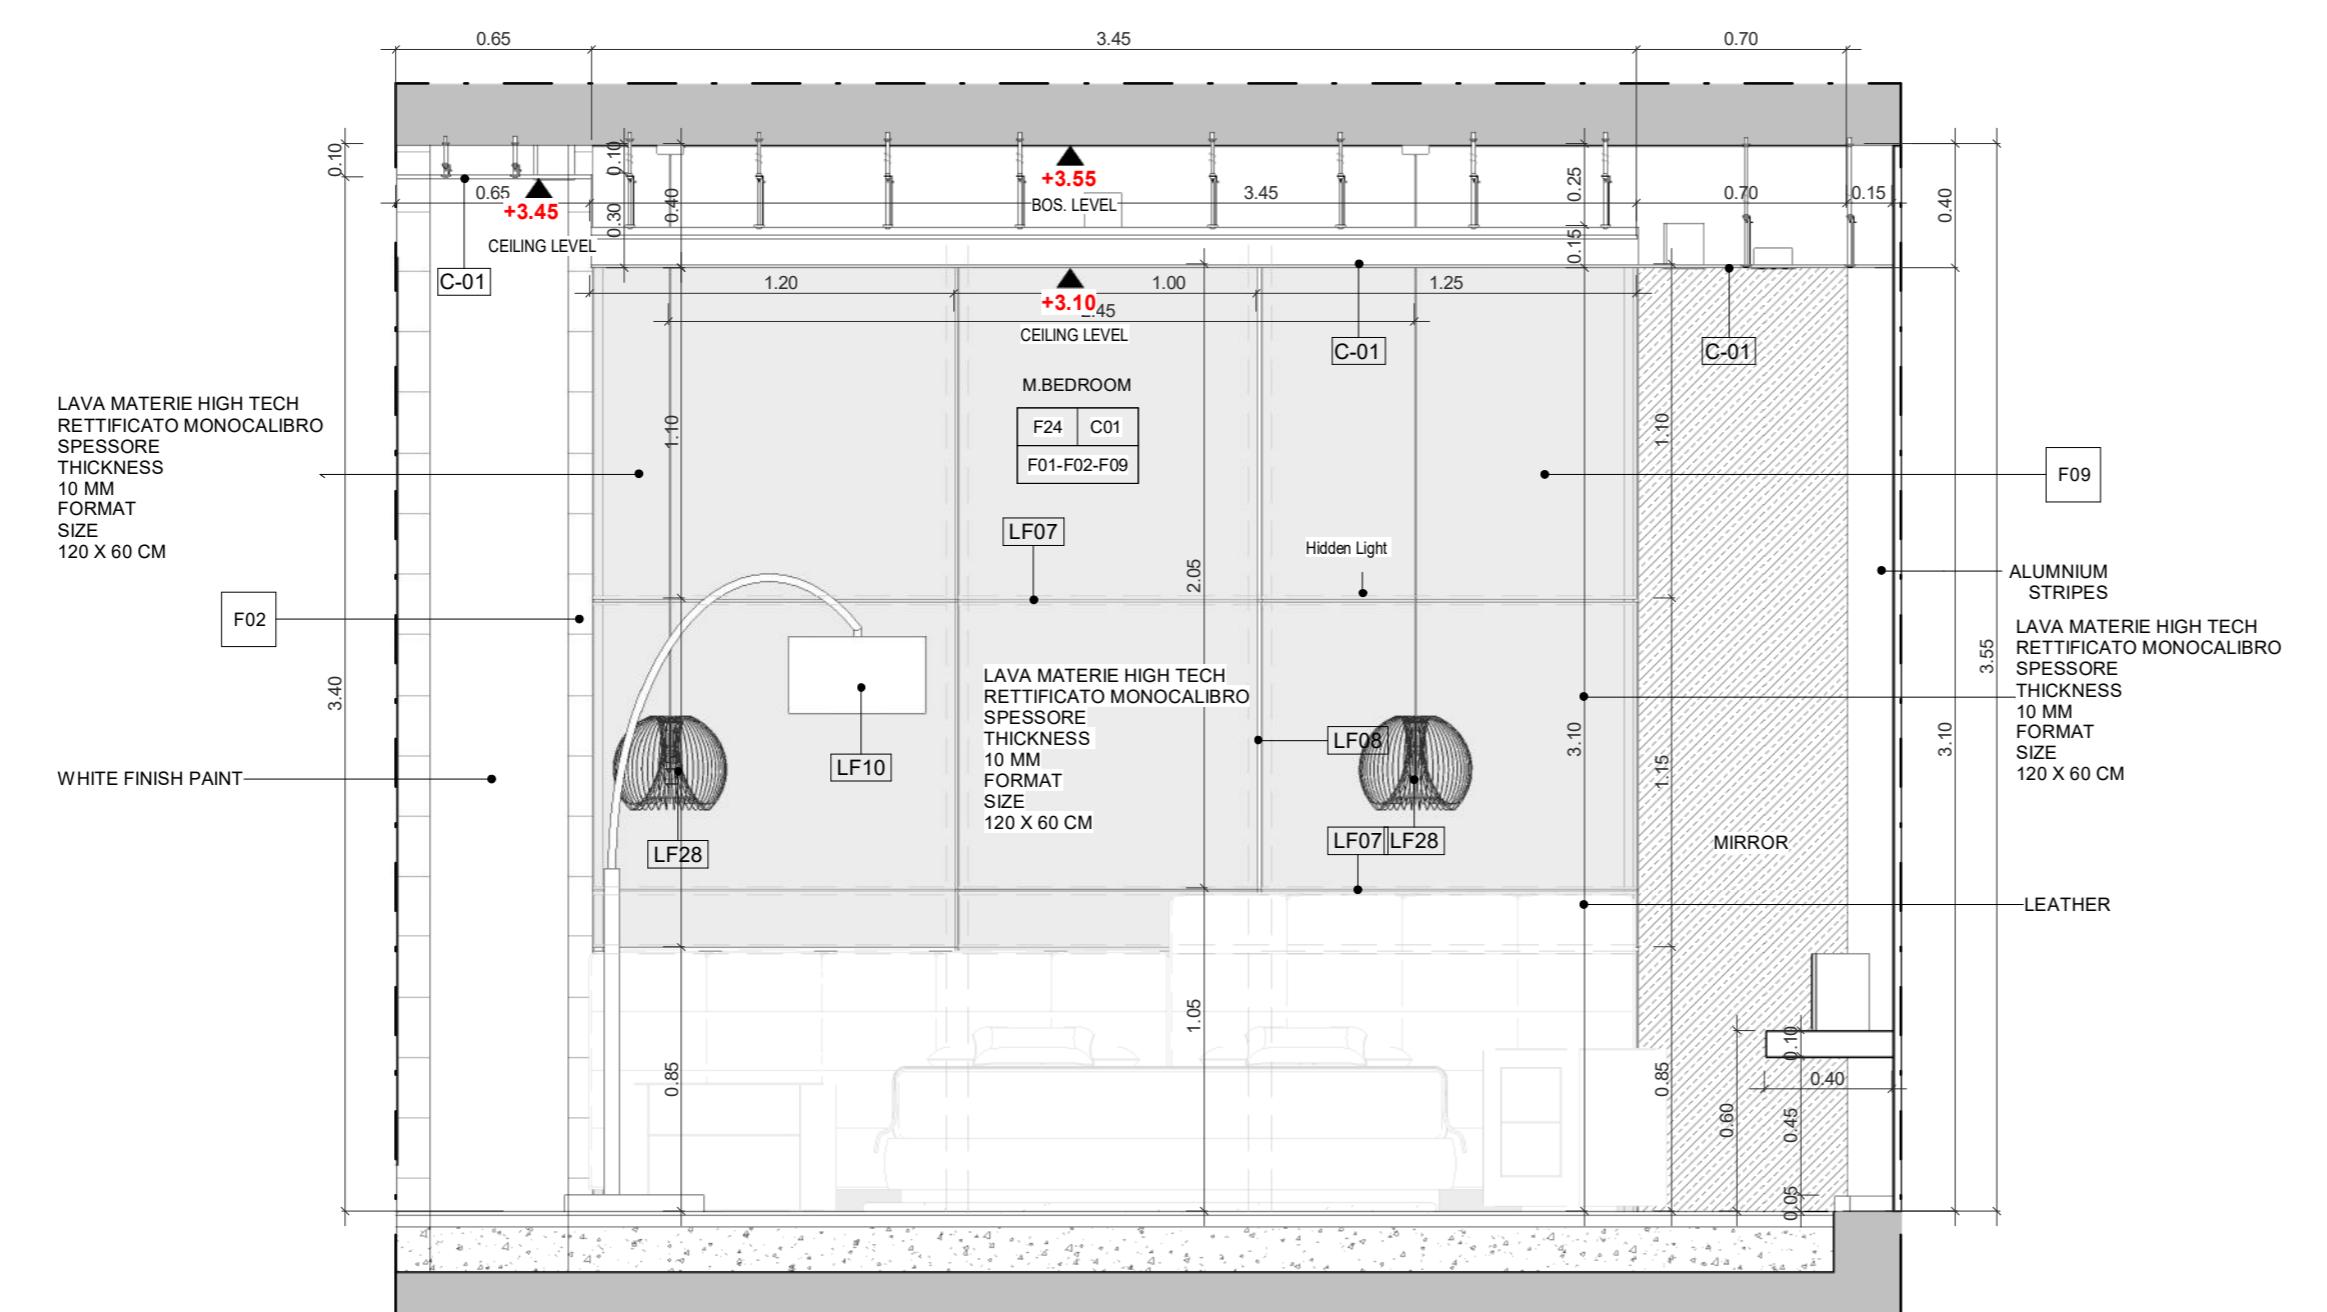

3 MASTER BEDROOM-ELEVATION -03
1 : 25

PROJECT NAME	APARTMENTS BUILDING		
NOTES			
ROOM NAME	FLOOR FINISH	CEILING FINISH	
WALL FINISH			
FINISHES SCHEDULE	FINISHES SCHEDULE		
Material: Mark	DESCRIPTION	Material: Mark	DESCRIPTION
F01	WHITE PAINT	F15	BEIGE PAINT
F02	GOLD WOOD	F16	TRAVERTINO MARBLE
F03	GOLD STONE	F17	LEATHER
F04	DARK WOOD	F18	PAINT GOLD METAL EFFECT
F05	DECORATIVE STONE	F19	DECORATIVE WOOD
F06	WOOD	F20	GREY STONE
F07	BLACK MARBLE	F21	CONCRETE FINISH
F08	BEIGE MARBLE	F10	KITCHENNETE WOOD
F09	GREY STONE	F11	CALCATTÀ
F10	WALL PAPER	F12	SWIMMING POOL MARBLE
F11	CALCATTÀ	F23	SWIMMING POOL WALL FINISH
F12	SWIMMING POOL MARBLE	F13	BLACK PAINT
F23	SWIMMING POOL WALL FINISH	F24	CALCATTÀ
F13	BLACK PAINT	F25	WHITE FINISH GRC
Project Type	Residential		
Owner	Khalid Khadir Hasan AL-Saeed		
Location	Amman		
Plot No.	1659		
Basin No.	19		
Designed by	A.Shaker Khulief 4809		
SHEET NAME	GROUND FLOOR- MASTER BEDROOM & BATHROOM		
ID-4125			
Date	08/10/2019		
Scale	1 : 25		

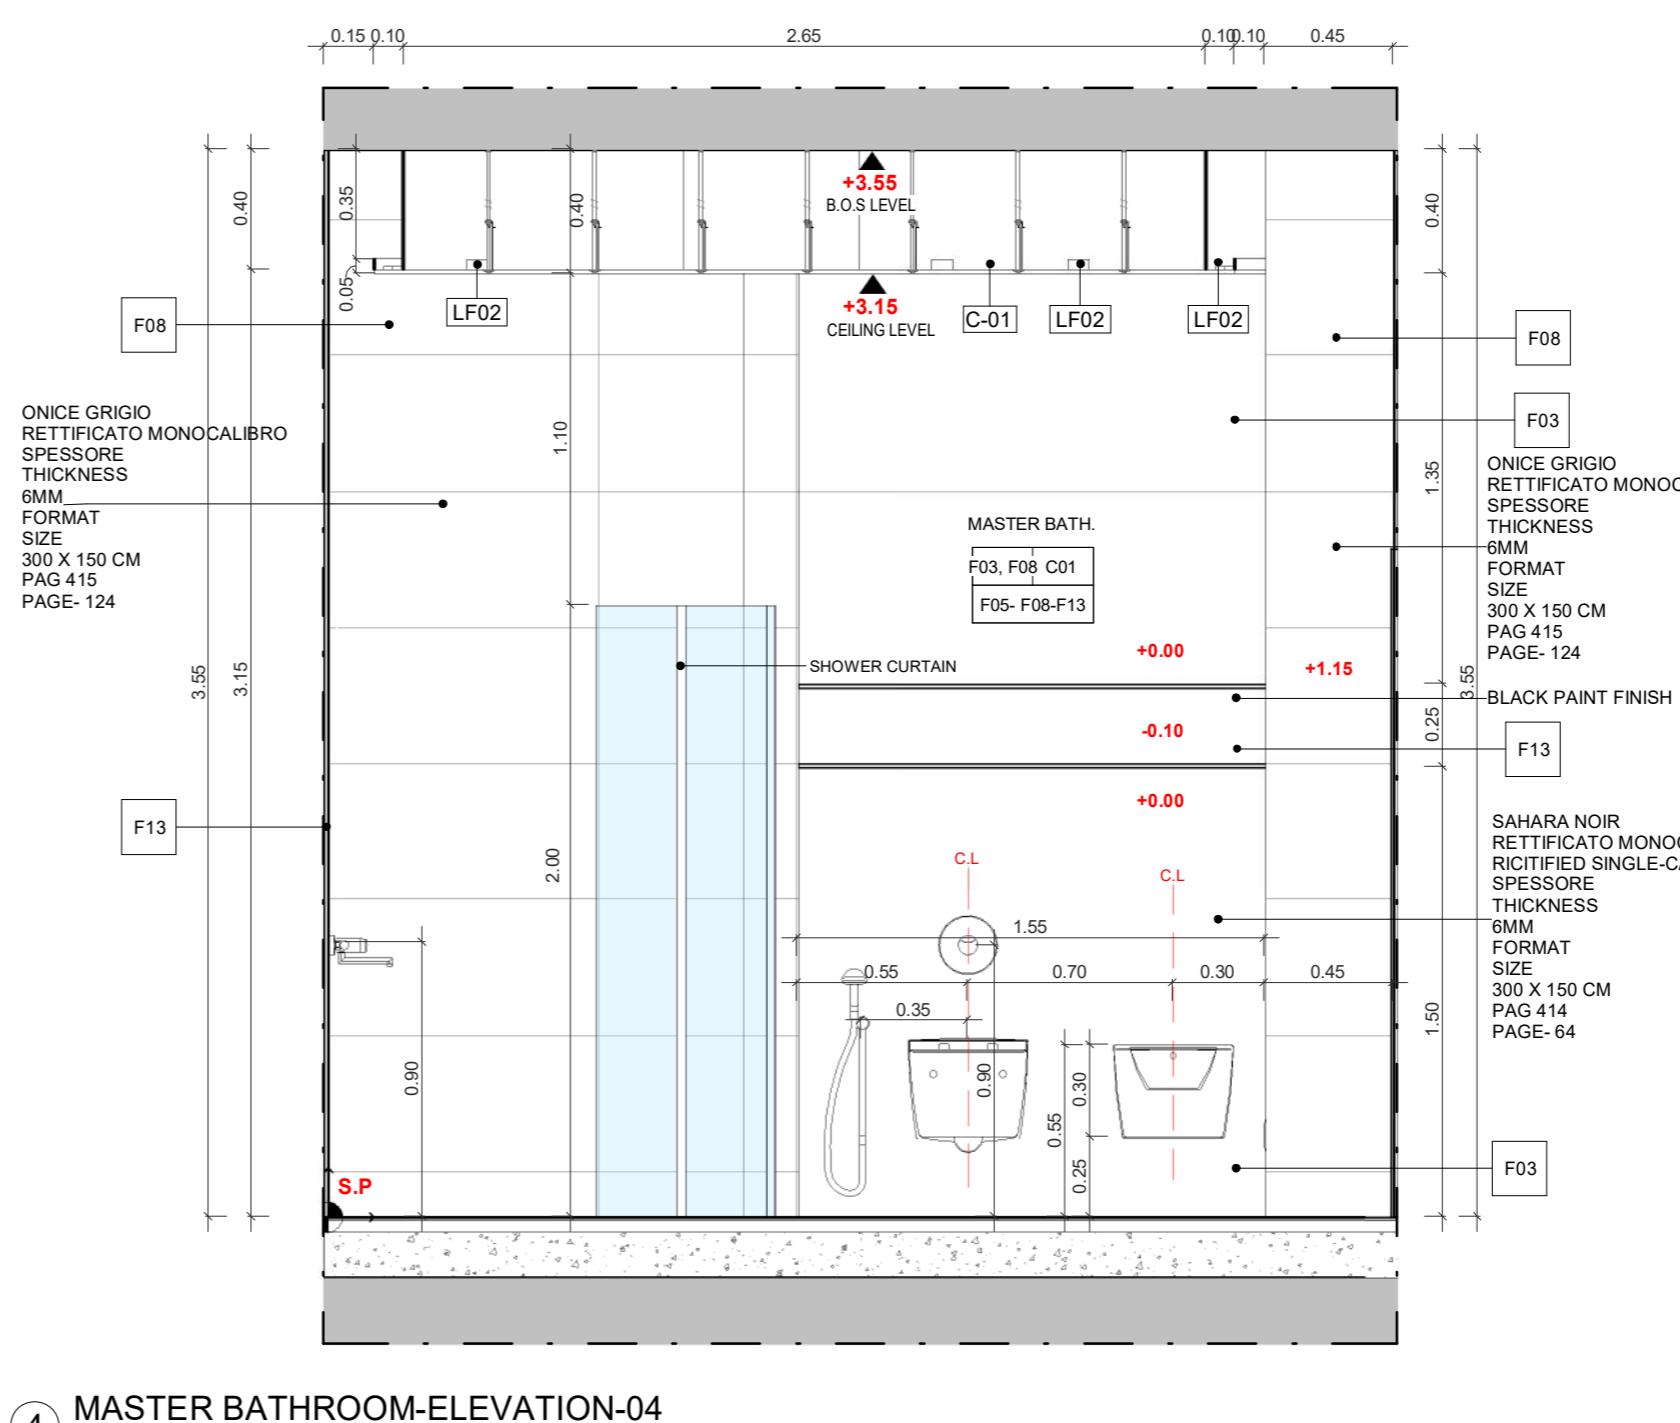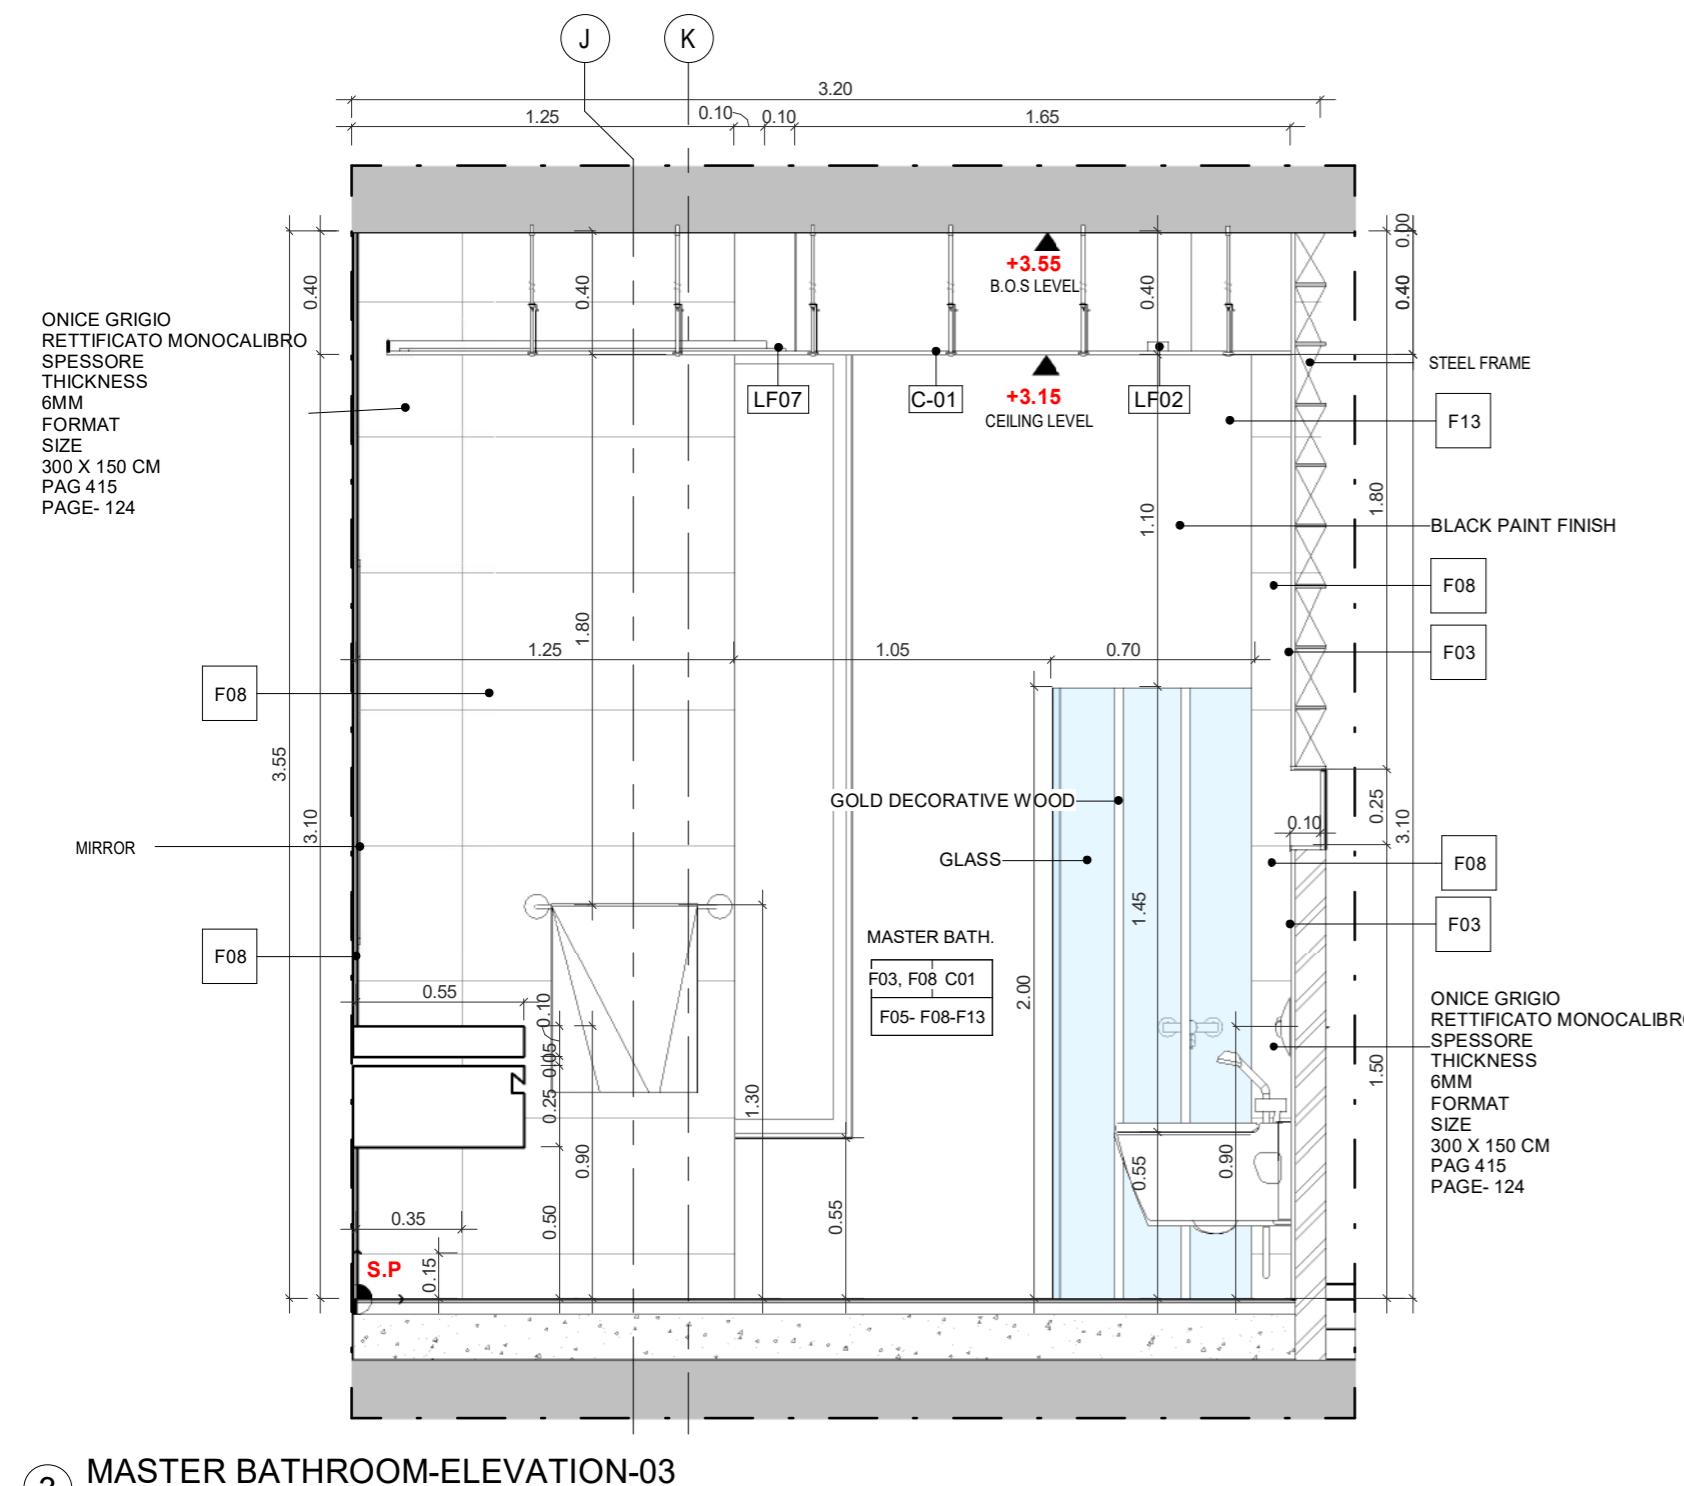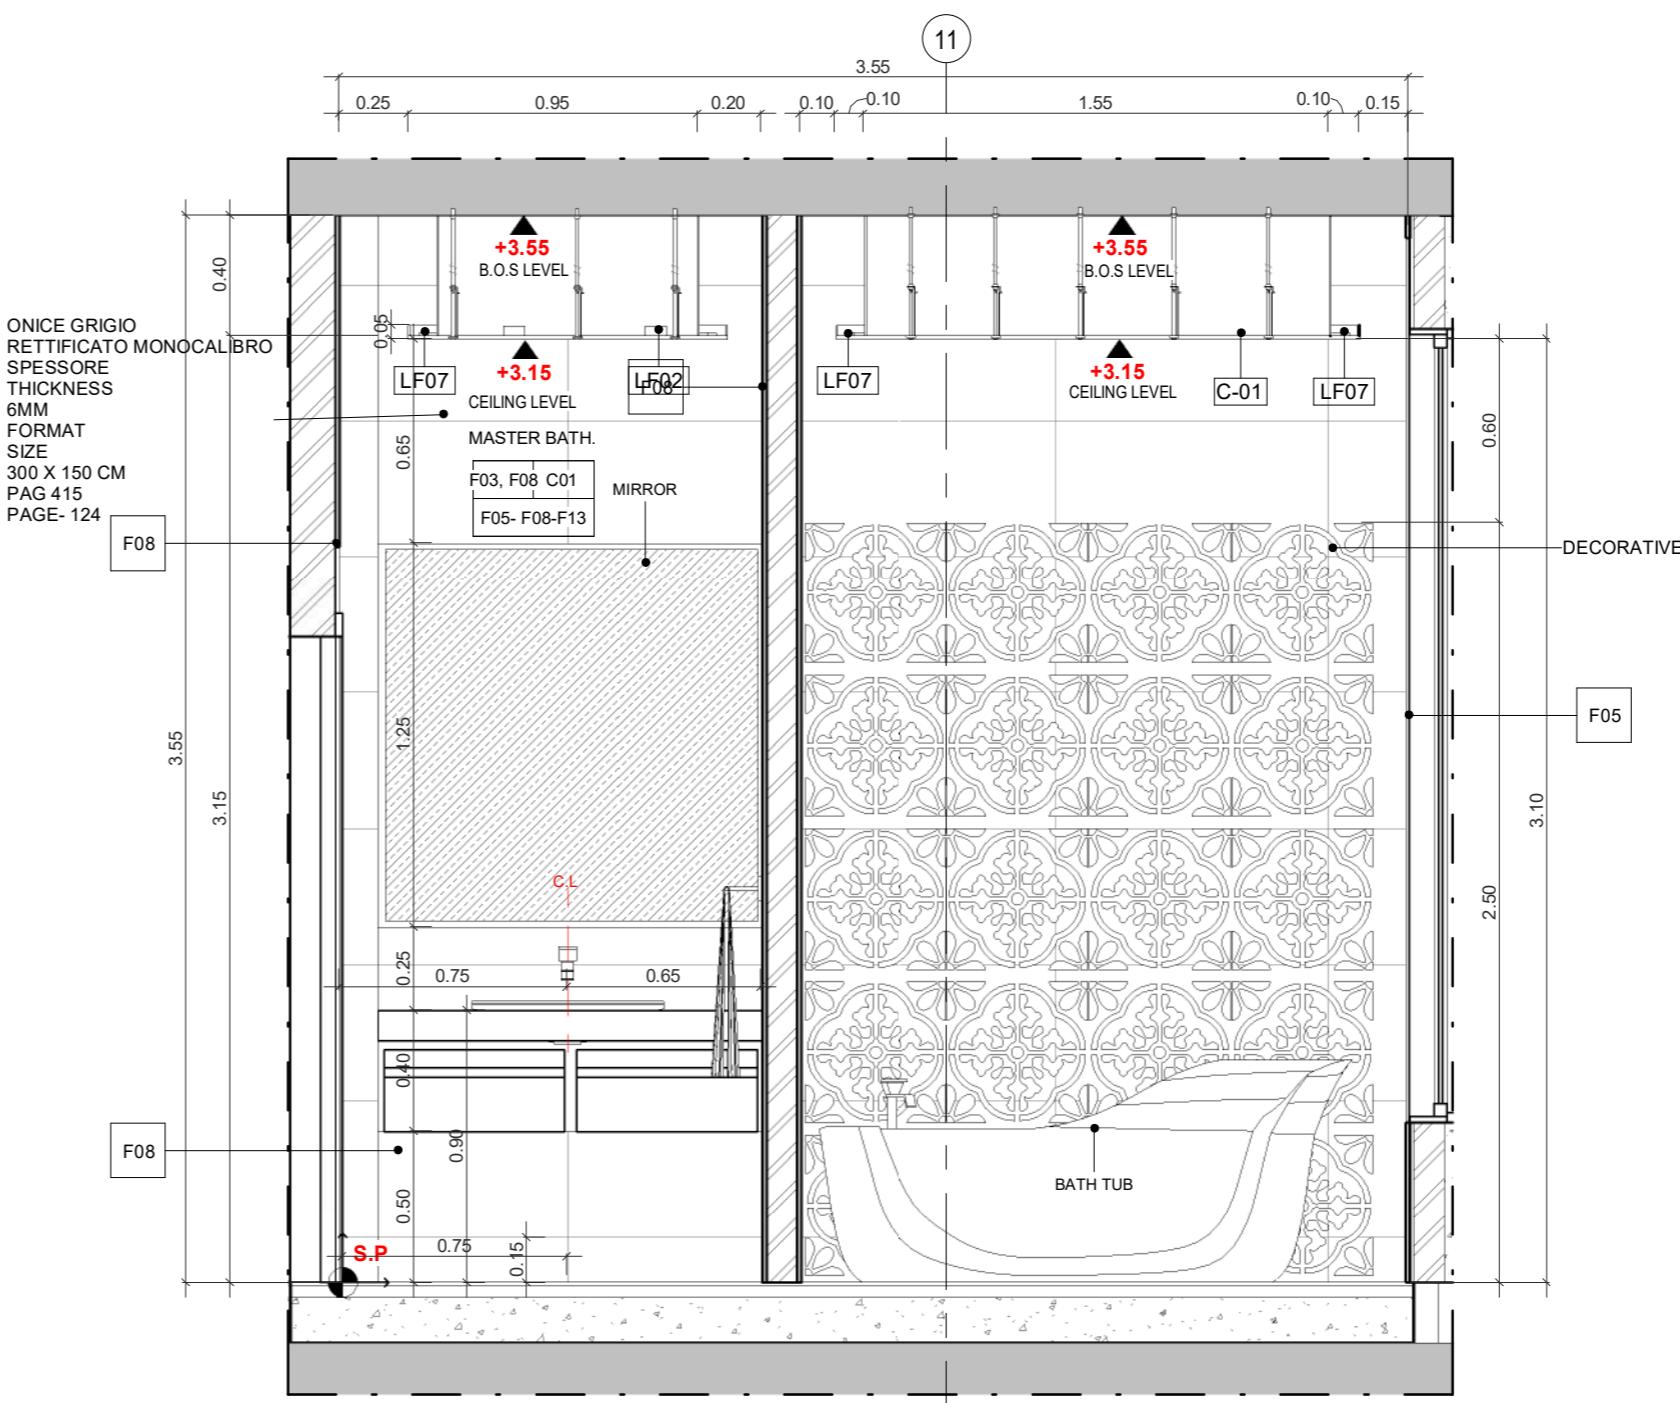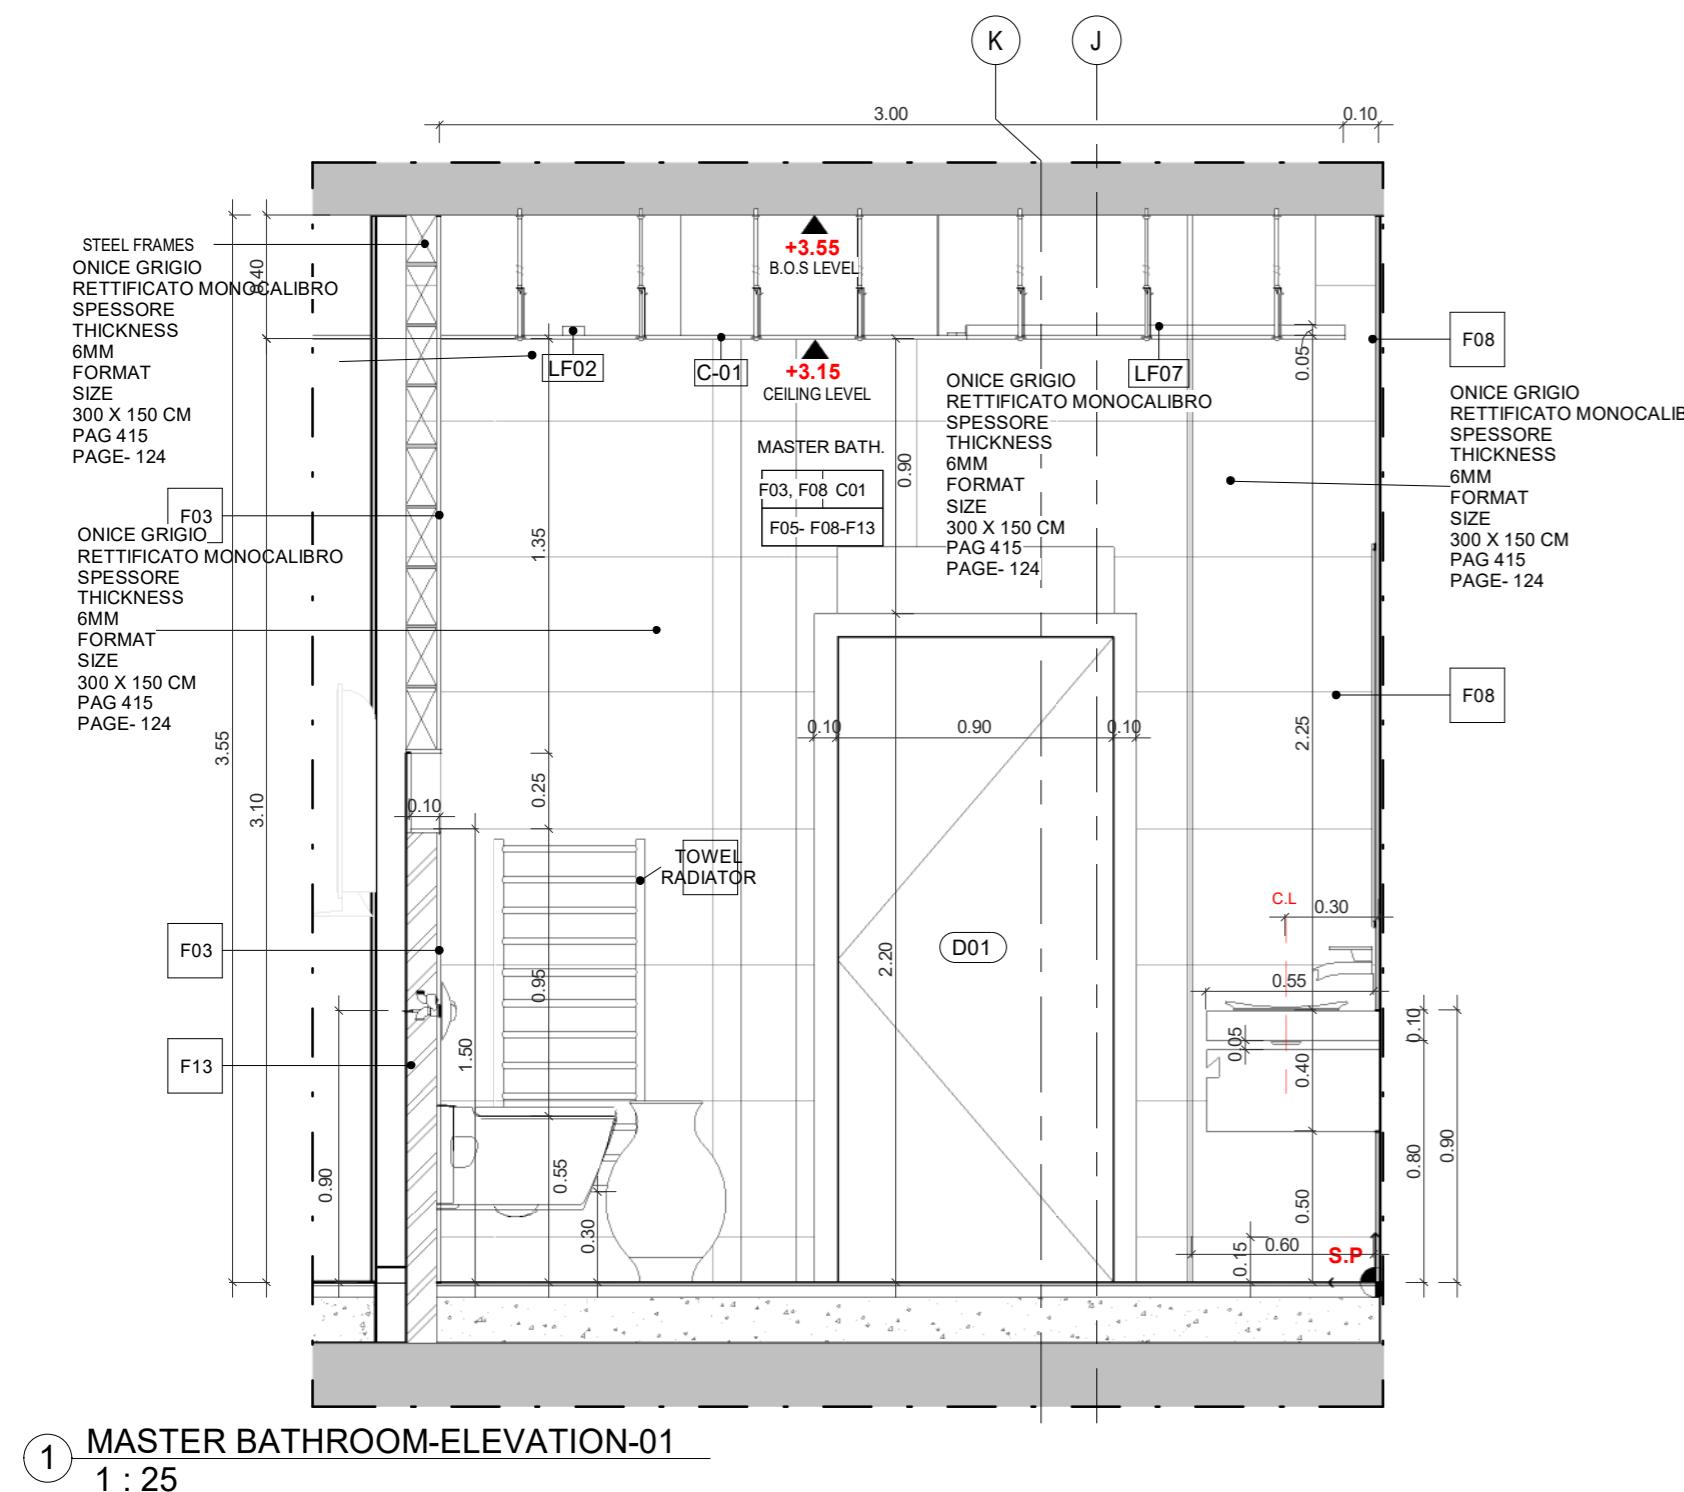

PROJECT NAME

APARTMENTS BUILDING

NOTES

FOR FINISHES REFER TO SHEETS:
ID-6000
ID-6001



Project Type	Residential
Owner	Khalid Khadir Hasan AL-Saeed
Location	Amman
Plot No.	1659
Basin No.	19
Designed by	A.Shaker Khulief 4809

SHEET NAME
GROUND FLOOR - MASTER BEDROOM 2 & BATHROOM-SHOTS

ID-4130

Date	08/10/2019
Scale	

PROJECT NAME

APARTMENTS BUILDING

NOTES

FOR FINISHES REFER TO SHEETS:
ID-6000
ID-6001

ROOM NAME

FLOOR FINISH	CEILING FINISH
--------------	----------------

WALL FINISH


FINISHES SCHEDULE		FINISHES SCHEDULE	
Material: Mark	Description	Material: Mark	Description
F01	WHITE PAINT	F15	BEIGE PAINT
F02	GOLD WOOD	F16	TRAVERTINO MARBLE
F03	GOLD STONE	F17	LEATHER
F04	DARK WOOD	F18	PAINT GOLD METAL EFFECT
F05	DECORATIVE STONE WOOD	F19	DECORATIVE WOOD
F06	BLACK MARBLE	F20	GREY STONE
F07	BEIGE MARBLE	F21	CONCRETE FINISH
F08	GREY STONE	F22	KITCHENNETE WOOD
F09	WALL PAPER	F23	SWIMMING POOL MARBLE
F10	CALCATTÀ	F24	SWIMMING POOL WALL FINISH
F11	SWIMMING POOL MARBLE	F13	BLACK PAINT
F12	CALCATTÀ	F14	PARQUET
F15	WHITE FINISH GRC	F25	WHITE FINISH GRC

Project Type	Residential
Owner	Khalid Khadir Hasan AL-Saeed
Location	Amman
Plot No.	1659
Basin No.	19
Designed by	A.Shaker Khulief 4809

SHEET NAME
GROUND FLOOR - MASTER BEDROOM 2 & BATHROOM

ID-4131

Date	08/10/2019
Scale	1 : 25

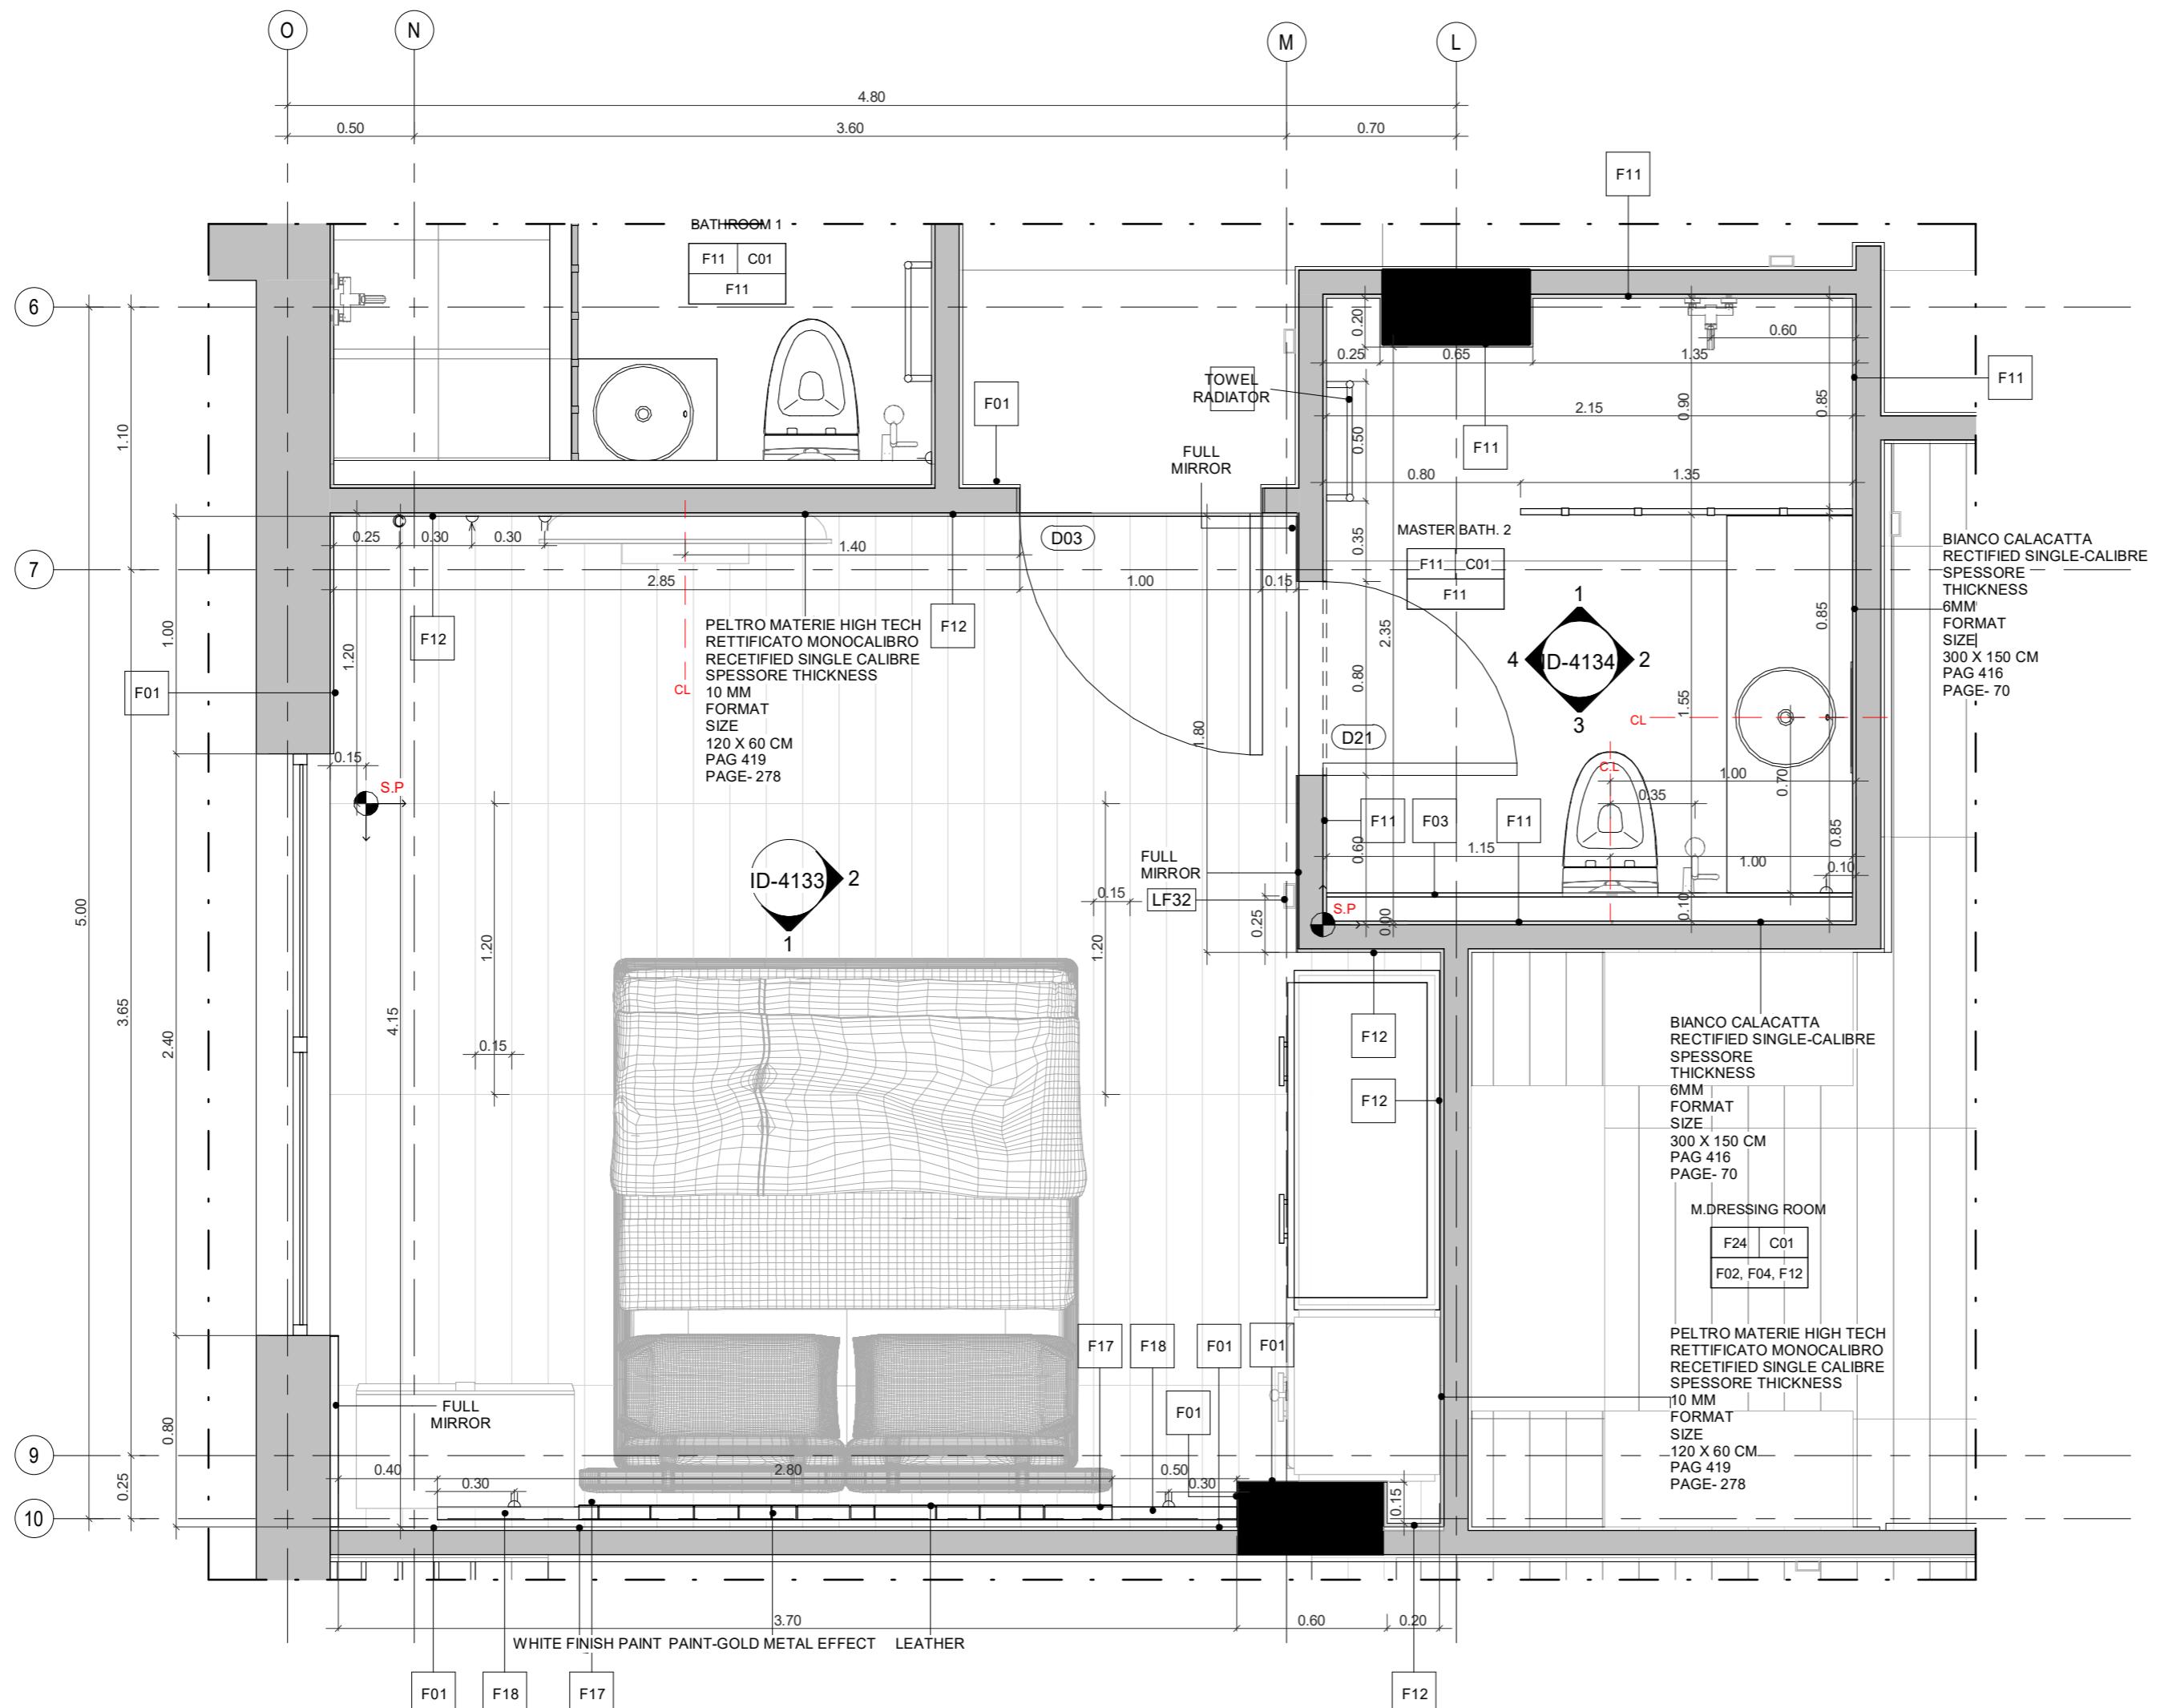

PROJECT NAME

APARTMENTS BUILDING

NOTES

FOR FINISHES REFER TO SHEETS:
ID-6000
ID-6001

ROOM NAME

FLOOR FINISH	CEILING FINISH
--------------	----------------

WALL FINISH

FINISHES SCHEDULE		FINISHES SCHEDULE	
Material: Mark	DESCRIPTION	Material: Mark	DESCRIPTION
F01	WHITE PAINT	F15	BEIGE PAINT
F02	GOLD WOOD	F16	TRAVERTINO MARBLE
F03	GOLD STONE	F17	LEATHER
F04	DARK WOOD	F05	DECORATIVE STONE
F06	WOOD	F18	PAINT GOLD METAL EFFECT
F07	BLACK MARBLE	F19	DECORATIVE WOOD
F08	BEIGE MARBLE	F20	GREY STONE
F09	GREY STONE	F21	CONCRETE FINISH
F10	WALL PAPER	F11	KITCHENNETE WOOD
F12	CALCATTAA	F12	SWIMMING POOL WALL FINISH
F13	BLACK PAINT	F13	PARQUET
F14	CALCATTAA	F14	WHITE FINISH GRC

SPOT RECESSED LIGHT

PENDANT LIGHT

HIDDEN LIGHT

CHANDELIER

WALL MOUNTED

NEON RECTANGULAR


Project Type	Residential
Owner	Khalid Khadir Hasan AL-Saeed
Location	Amman
Plot No.	1659
Basin No.	19
Designed by	A.Shaker Khulief 4809


SHEET NAME	GROUND FLOOR - MASTER BEDROOM 2 & BATHROOM
------------	--

ID-4132

Date 08/10/2019


Scale As indicated

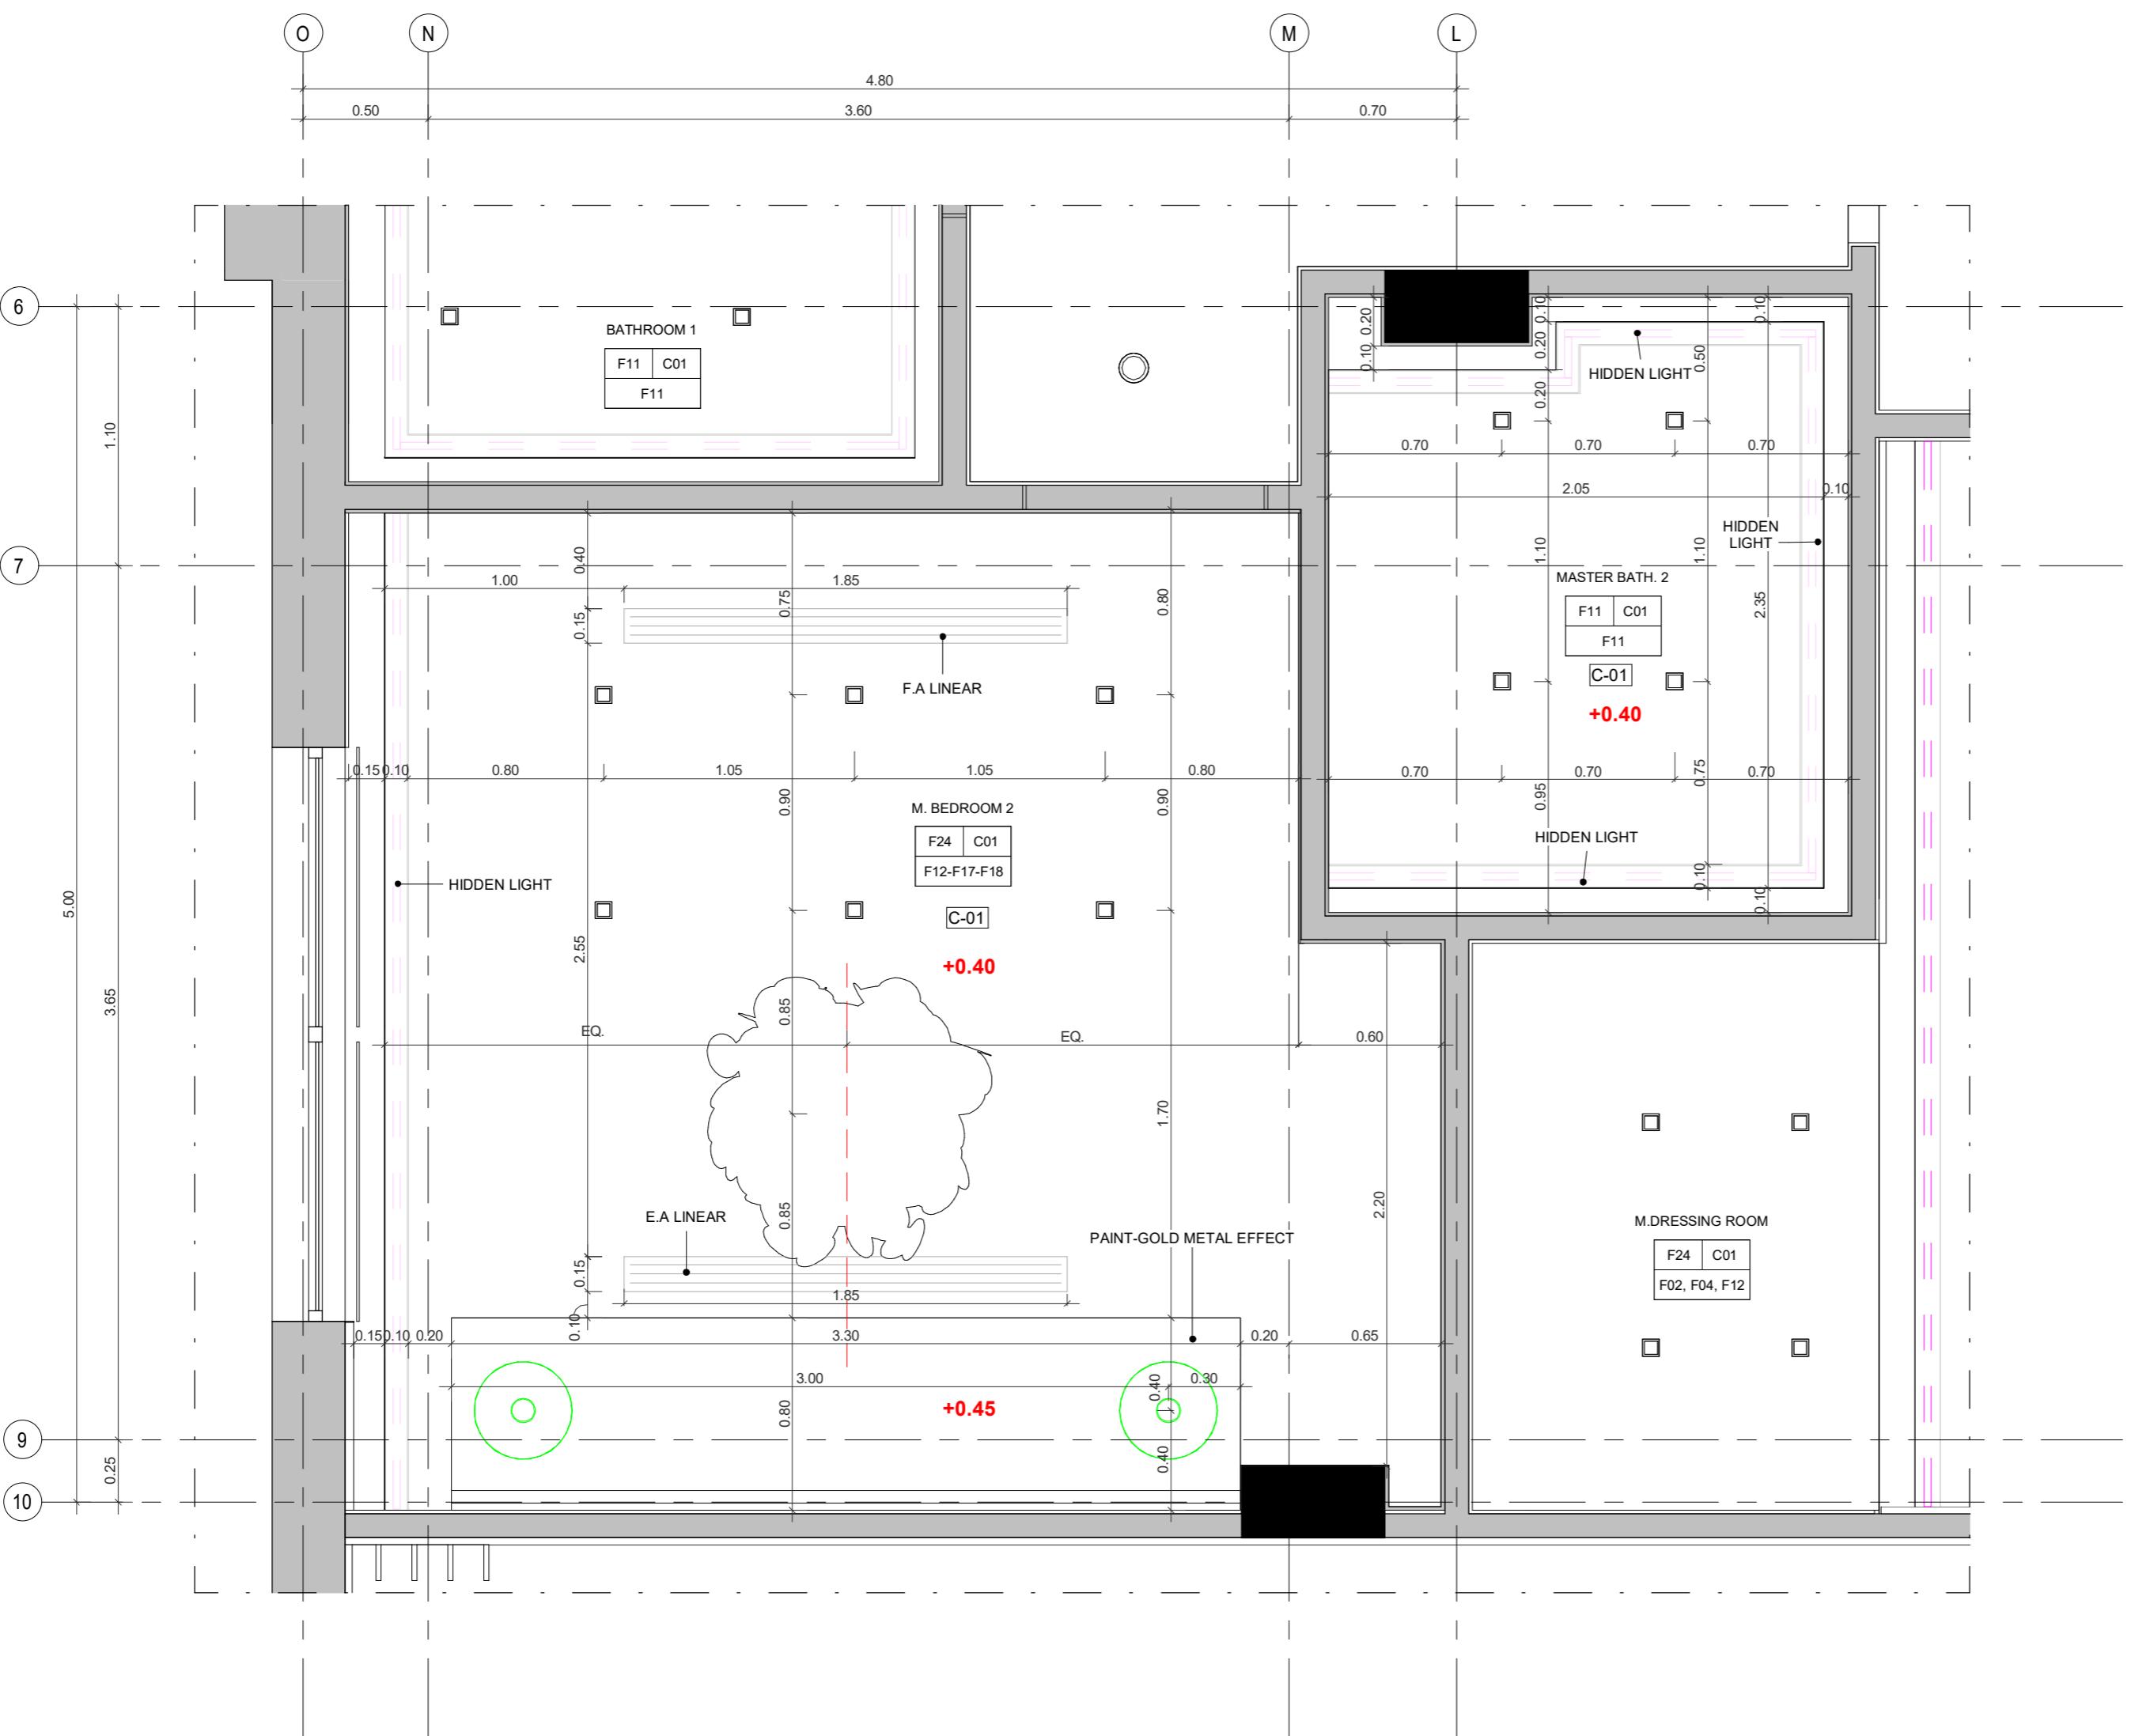

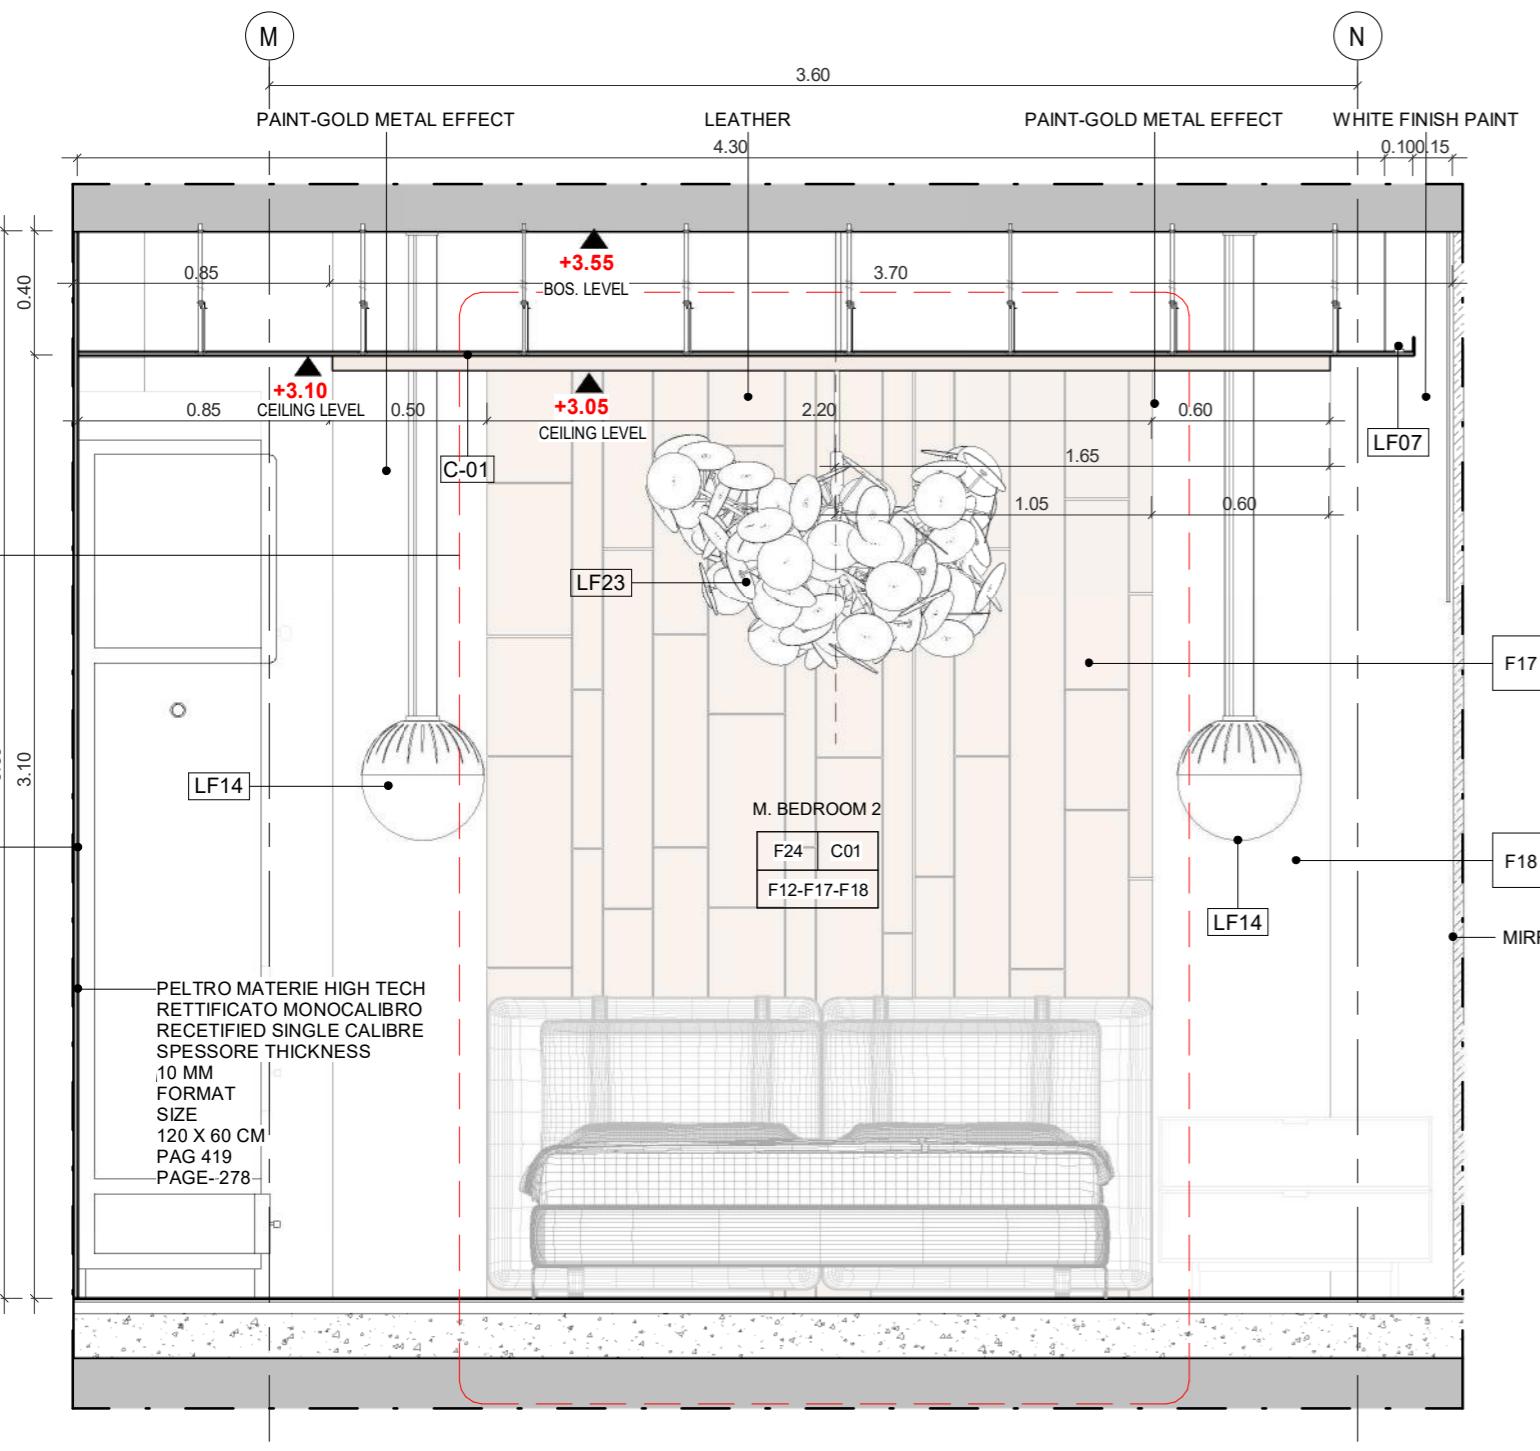


1 MASTER BEDROOM 2 -ELEVATION 01
1 : 25

1 : 25

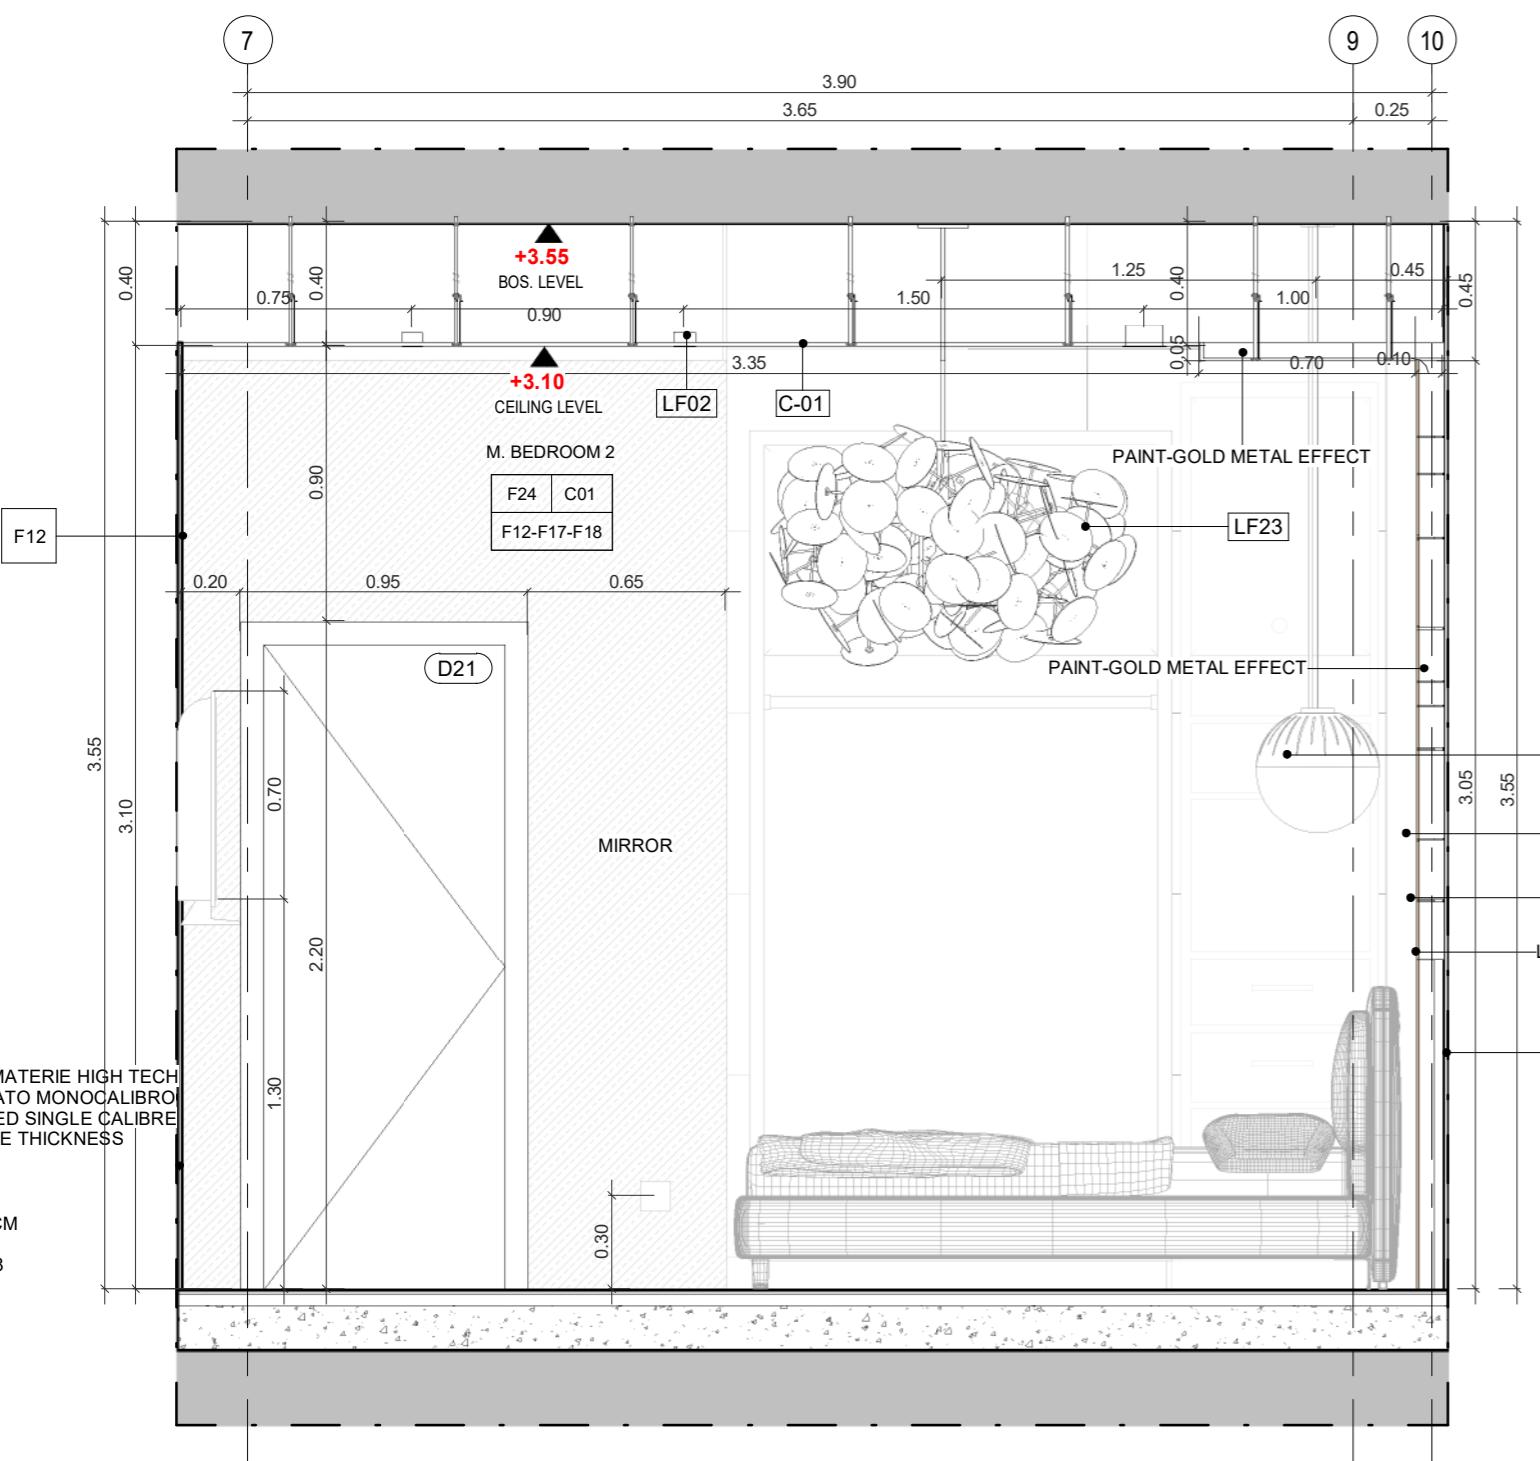

MASTER BEDROOM 2 -ELEVATION 02
1-25

1 : 2

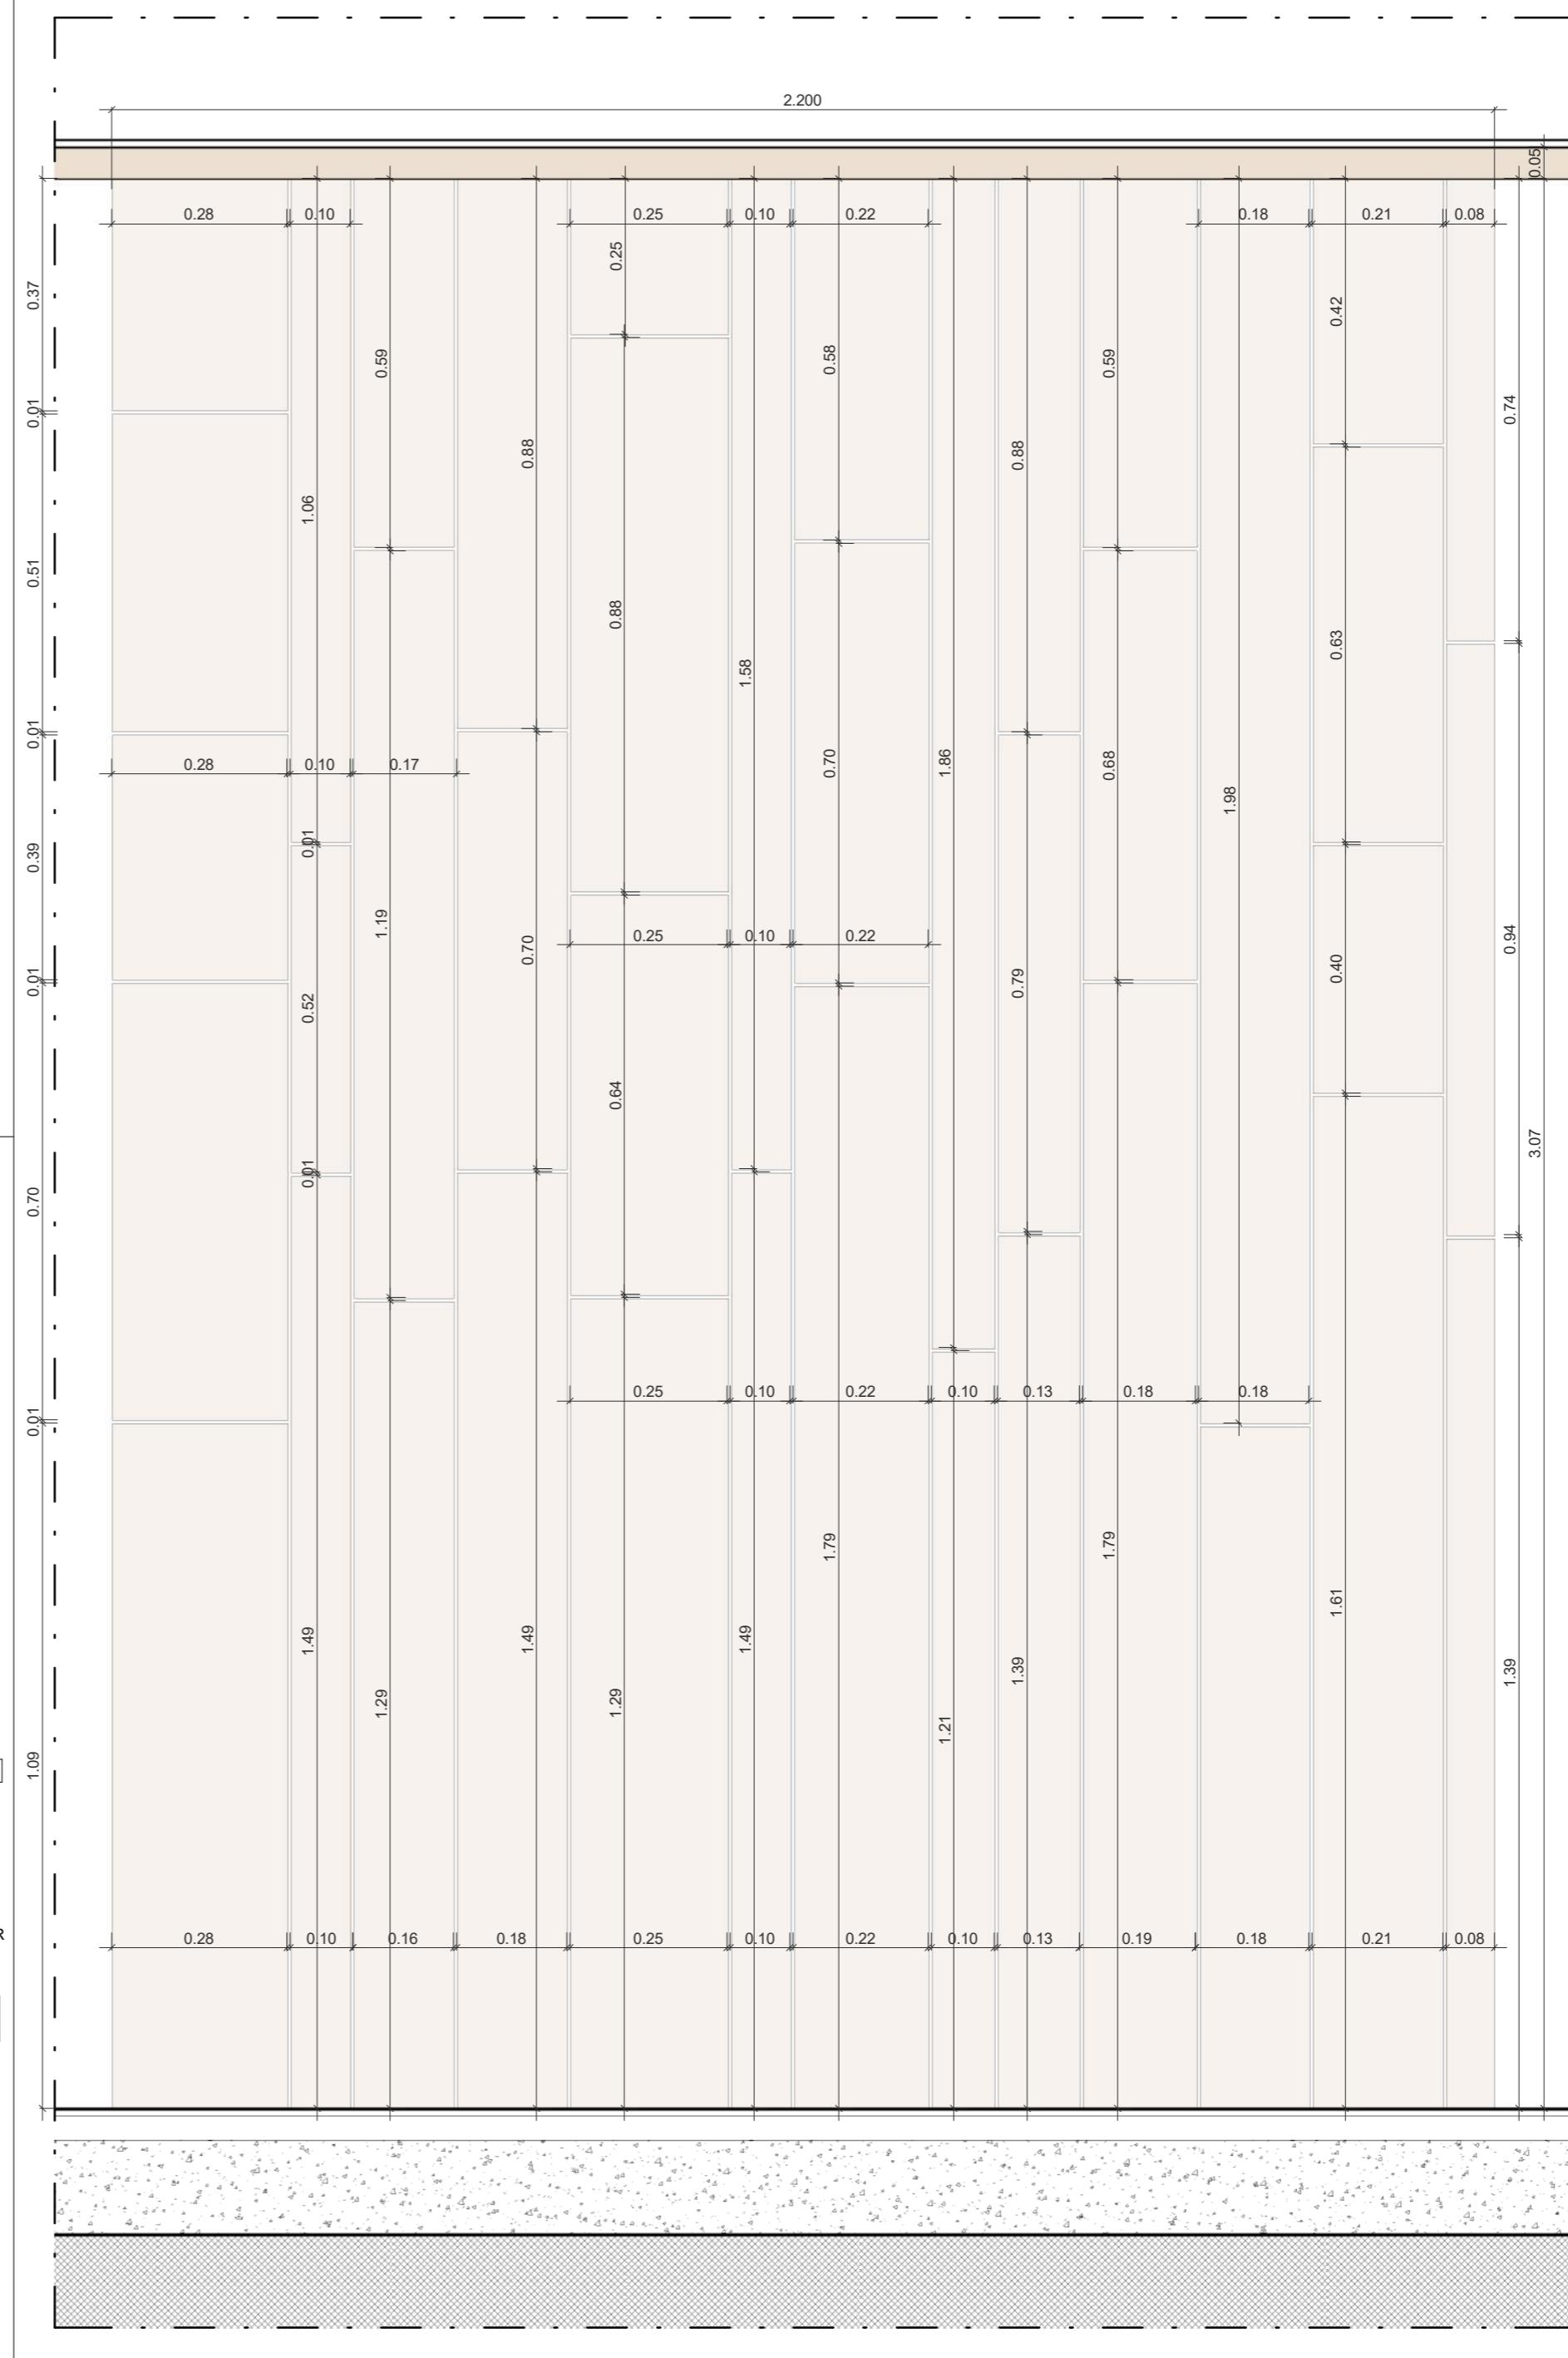


(3) ELEVATION DETAIL

1 : 1




PROJECT NAME																																	
APARTMENTS BUILDING																																	
NOTES																																	
FOR FINISHES REFER TO SHEETS: ID-6000 ID-6001																																	
ROOM NAME																																	
FLOOR FINISH	CEILING FINISH																																
WALL FINISH																																	
<table border="1"> <thead> <tr> <th colspan="2">FINISHES SCHEDULE</th> </tr> <tr> <th>Material: Mark</th> <th>DESCRIPTION</th> </tr> </thead> <tbody> <tr><td>F01</td><td>WHITE PAINT</td></tr> <tr><td>F02</td><td>GOLD WOOD</td></tr> <tr><td>F03</td><td>GOLD STONE</td></tr> <tr><td>F04</td><td>DARK WOOD</td></tr> <tr><td>F05</td><td>DECORATIVE STONE</td></tr> <tr><td>F06</td><td>WOOD</td></tr> <tr><td>F07</td><td>BLACK MARBLE</td></tr> <tr><td>F08</td><td>BEIGE MARBLE</td></tr> <tr><td>F09</td><td>GREY STONE</td></tr> <tr><td>F10</td><td>WALL PAPER</td></tr> <tr><td>F11</td><td>CALCATTAA</td></tr> <tr><td>F12</td><td>SWIMMING POOL MARBLE</td></tr> <tr><td>F13</td><td>BLACK PAINT</td></tr> <tr><td>F14</td><td>CALCATTAA</td></tr> </tbody> </table>		FINISHES SCHEDULE		Material: Mark	DESCRIPTION	F01	WHITE PAINT	F02	GOLD WOOD	F03	GOLD STONE	F04	DARK WOOD	F05	DECORATIVE STONE	F06	WOOD	F07	BLACK MARBLE	F08	BEIGE MARBLE	F09	GREY STONE	F10	WALL PAPER	F11	CALCATTAA	F12	SWIMMING POOL MARBLE	F13	BLACK PAINT	F14	CALCATTAA
FINISHES SCHEDULE																																	
Material: Mark	DESCRIPTION																																
F01	WHITE PAINT																																
F02	GOLD WOOD																																
F03	GOLD STONE																																
F04	DARK WOOD																																
F05	DECORATIVE STONE																																
F06	WOOD																																
F07	BLACK MARBLE																																
F08	BEIGE MARBLE																																
F09	GREY STONE																																
F10	WALL PAPER																																
F11	CALCATTAA																																
F12	SWIMMING POOL MARBLE																																
F13	BLACK PAINT																																
F14	CALCATTAA																																
<table border="1"> <thead> <tr> <th colspan="2">FINISHES SCHEDULE</th> </tr> <tr> <th>Material: Mark</th> <th>DESCRIPTION</th> </tr> </thead> <tbody> <tr><td>F15</td><td>BEIGE PAINT</td></tr> <tr><td>F16</td><td>TRAVERTINO MARBLE</td></tr> <tr><td>F17</td><td>LEATHER</td></tr> <tr><td>F18</td><td>PAINT GOLD METAL EFFECT</td></tr> <tr><td>F19</td><td>DECORATIVE WOOD</td></tr> <tr><td>F20</td><td>GREY STONE</td></tr> <tr><td>F21</td><td>CONCRETE FINISH</td></tr> <tr><td>F22</td><td>KITCHENNETE WOOD</td></tr> <tr><td>F23</td><td>SWIMMING POOL WALL FINISH</td></tr> <tr><td>F24</td><td>PARQUET</td></tr> <tr><td>F25</td><td>WHITE FINISH GRC</td></tr> </tbody> </table>		FINISHES SCHEDULE		Material: Mark	DESCRIPTION	F15	BEIGE PAINT	F16	TRAVERTINO MARBLE	F17	LEATHER	F18	PAINT GOLD METAL EFFECT	F19	DECORATIVE WOOD	F20	GREY STONE	F21	CONCRETE FINISH	F22	KITCHENNETE WOOD	F23	SWIMMING POOL WALL FINISH	F24	PARQUET	F25	WHITE FINISH GRC						
FINISHES SCHEDULE																																	
Material: Mark	DESCRIPTION																																
F15	BEIGE PAINT																																
F16	TRAVERTINO MARBLE																																
F17	LEATHER																																
F18	PAINT GOLD METAL EFFECT																																
F19	DECORATIVE WOOD																																
F20	GREY STONE																																
F21	CONCRETE FINISH																																
F22	KITCHENNETE WOOD																																
F23	SWIMMING POOL WALL FINISH																																
F24	PARQUET																																
F25	WHITE FINISH GRC																																
<table border="1"> <tr> <td>Project Type</td> <td>Residential</td> </tr> <tr> <td>Owner</td> <td>Khalid Khadir Hasan AL-Saeed</td> </tr> <tr> <td>Location</td> <td>Amman</td> </tr> <tr> <td>Plot No.</td> <td>1659</td> </tr> <tr> <td>Basin No.</td> <td>19</td> </tr> <tr> <td>Designed by</td> <td>A.Shaker Khulief 4809</td> </tr> </table>		Project Type	Residential	Owner	Khalid Khadir Hasan AL-Saeed	Location	Amman	Plot No.	1659	Basin No.	19	Designed by	A.Shaker Khulief 4809																				
Project Type	Residential																																
Owner	Khalid Khadir Hasan AL-Saeed																																
Location	Amman																																
Plot No.	1659																																
Basin No.	19																																
Designed by	A.Shaker Khulief 4809																																
SHEET NAME																																	
GROUND FLOOR - MASTER BEDROOM 2 & BATHROOM ELEVATIONS																																	
ID-4133																																	
Date	08/10/2019																																
Scale	As indicated																																


PROJECT NAME	APARTMENTS BUILDING		
NOTES			
ROOM NAME	FLOOR FINISH	CEILING FINISH	
WALL FINISH			
FINISHES SCHEDULE	FINISHES SCHEDULE		
Material: Mark	DESCRIPTION	Material: Mark	DESCRIPTION
F01	WHITE PAINT	F15	BEIGE PAINT
F02	GOLD WOOD	F16	TRAVERTINO MARBLE
F03	GOLD STONE	F17	LEATHER
F04	DARK WOOD	F18	PAINT GOLD METAL EFFECT
F05	DECORATIVE STONE	F06	WOOD
F06		F07	BLACK MARBLE
F07		F08	BEIGE MARBLE
F08		F09	GREY STONE
F09		F10	KITCHENNETE WOOD
F10		F11	CALCAGNA
F11		F12	SWIMMING POOL MARBLE
F12		F13	BLACK PAINT
F13		F14	CALCAGNA
F14		F15	WHITE FINISH GRC
Project Type	Residential		
Owner	Khalid Khadir Hasan AL-Saeed		
Location	Amman		
Plot No.	1659		
Basin No.	19		
Designed by	A.Shaker Khulief 4809		
SHEET NAME	GROUND FLOOR - MASTER BEDROOM 2 & BATHROOM ELEVATIONS		
ID-4134			
Date	08/10/2019		
Scale	1 : 25		

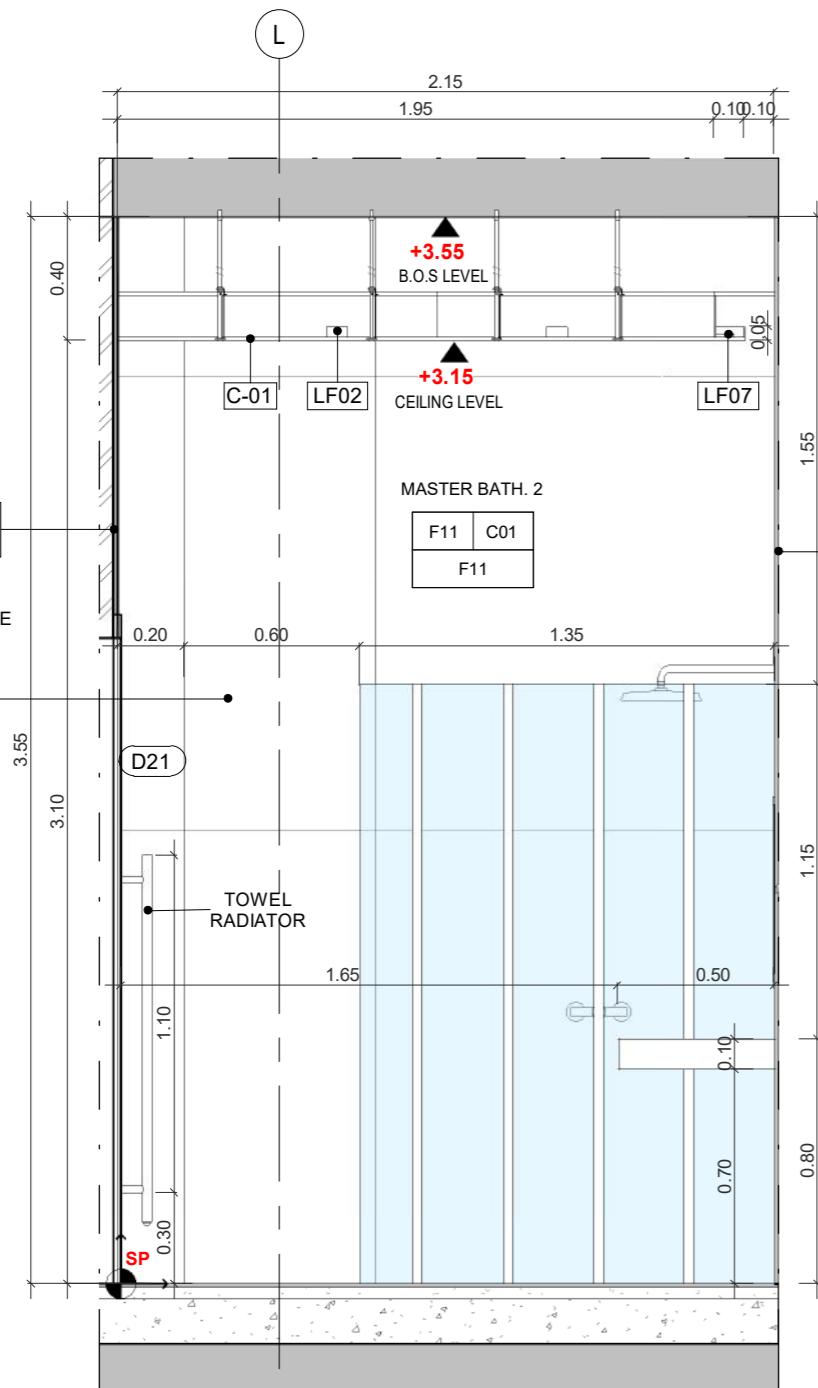


① MASTER BATHROOM 2-ELEVATION 01
1 : 25

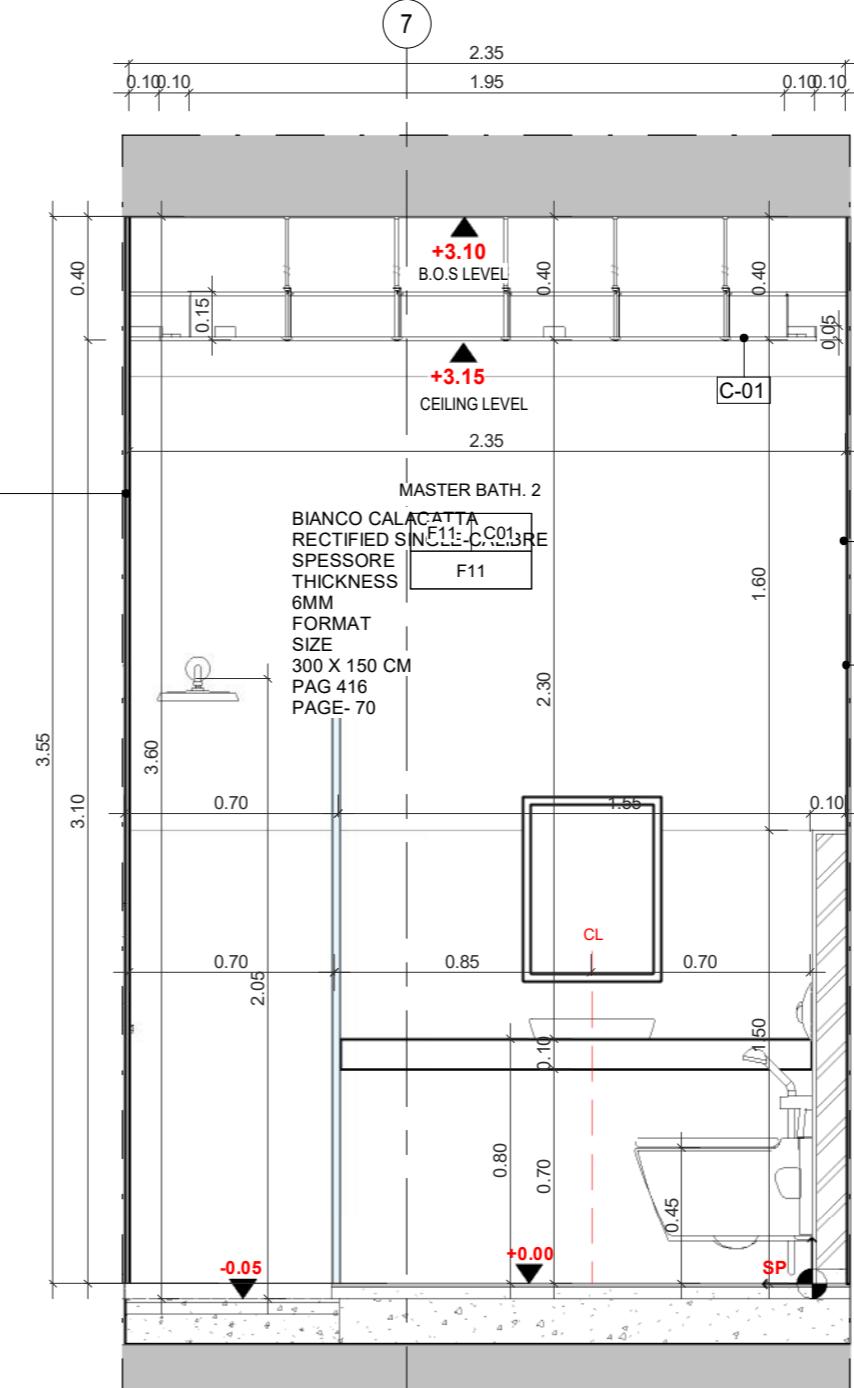

② MASTER BATHROOM 2 -ELEVATION 02
1 : 25

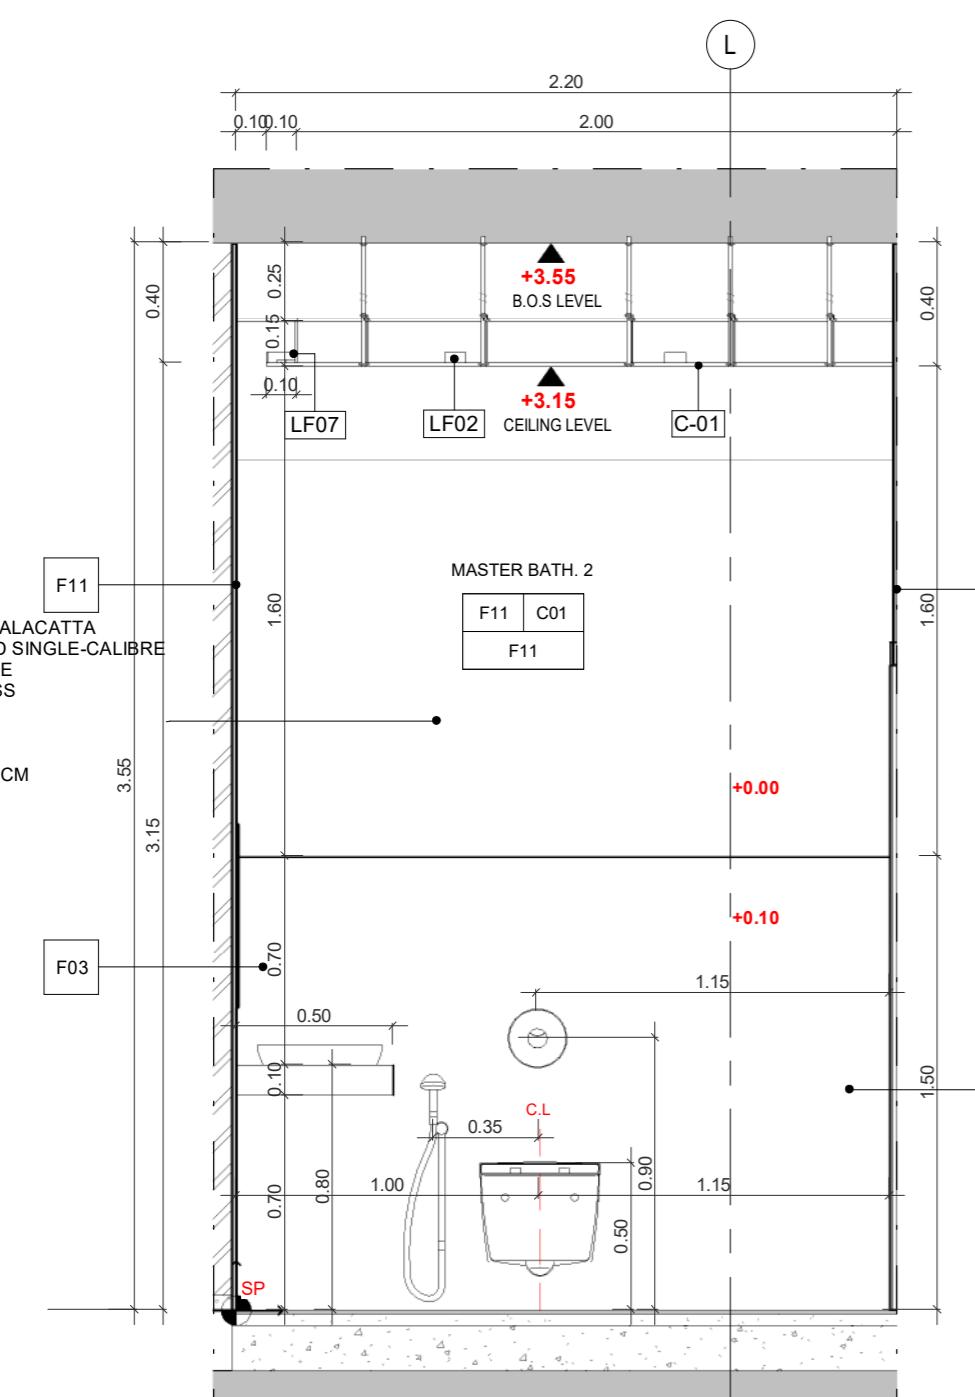

③ MASTER BATHROOM 2-ELEVATION 03
1 : 25

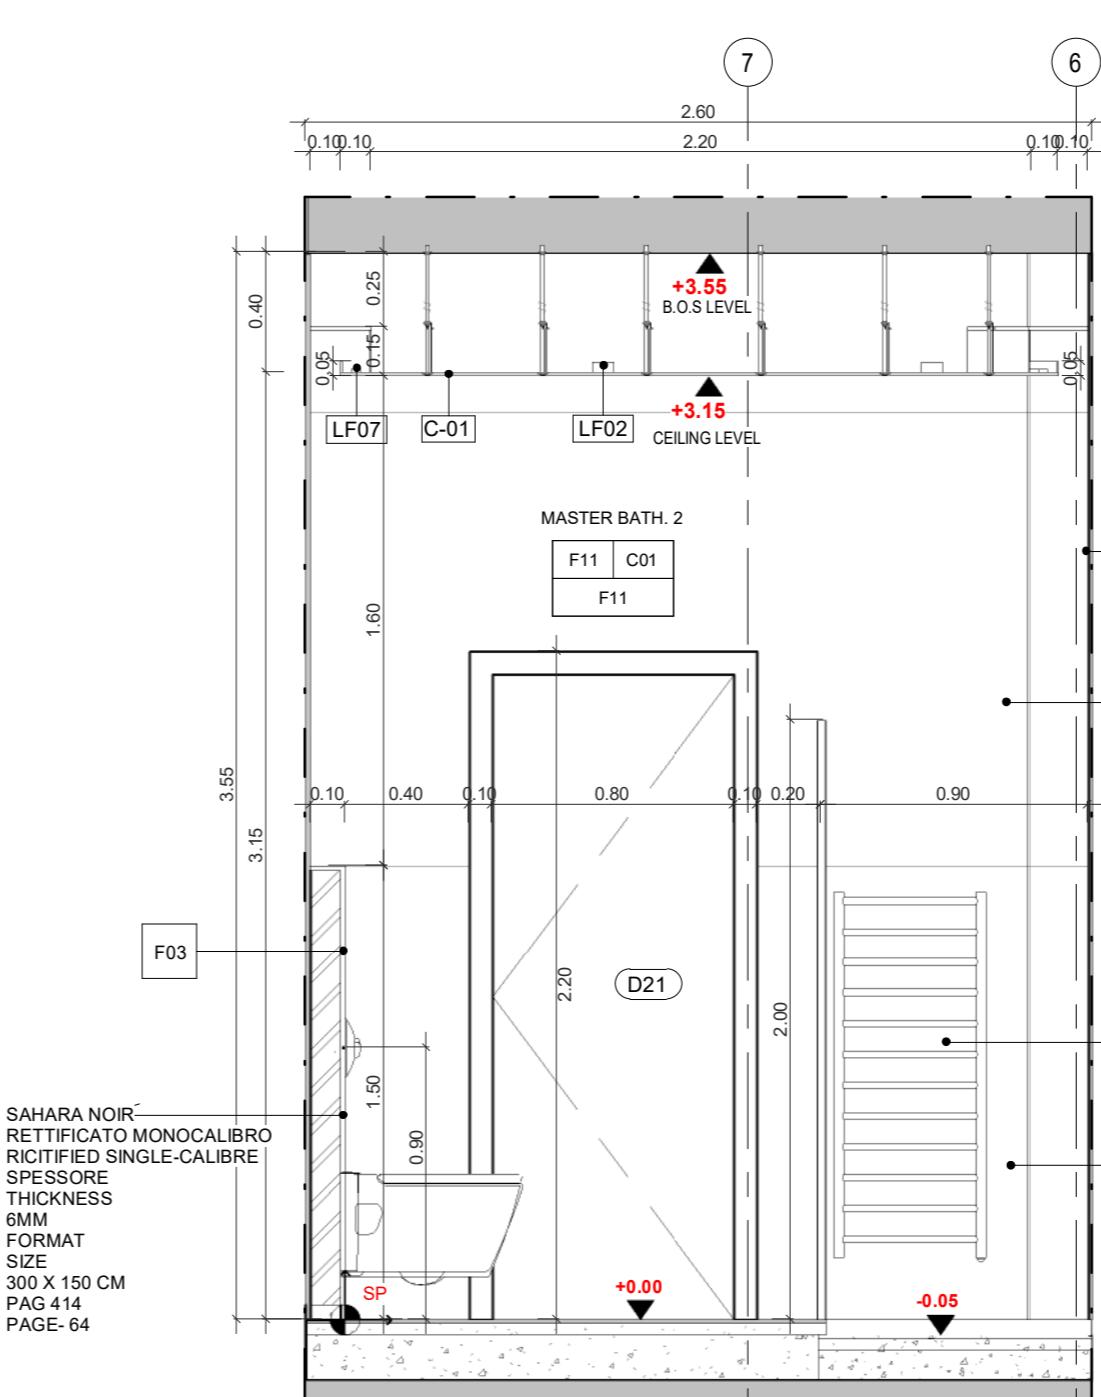

④ MASTER BATHROOM 02-ELEVATION 04
1 : 25

PROJECT NAME

APARTMENTS BUILDING

NOTES

FOR FINISHES REFER TO SHEETS:
ID-6000
ID-6001

ROOM NAME

FLOOR FINISH	CEILING FINISH
--------------	----------------

WALL FINISH

FINISHES SCHEDULE		FINISHES SCHEDULE			
Material:	Mark	DESCRIPTION	Material:	Mark	DESCRIPTION
F01		WHITE PAINT	F15		BEIGE PAINT
F02		GOLD WOOD	F16		TRAVERTINO MARBLE
F03		GOLD STONE	F17		LEATHER
F04		DARK WOOD	F05		PAINT GOLD METAL EFFECT
F06		DECORATIVE STONE	F06		WOOD
F07		BLACK MARBLE	F18		DECORATIVE WOOD
F08		BEIGE MARBLE	F19		GREY STONE
F09		GREY STONE	F20		KITCHENNETE
F10		WALL PAPER	F21		WOOD
F11		CALCAGNA	F22		SWIMMING POOL MARBLE
F12			F23		SWIMMING POOL WALL FINISH
F13			F24		BLACK PAINT
F14			F25		CALCAGNA
					WHITE FINISH GRC

SPOT RECESSED LIGHT
PENDANT LIGHT
HIDDEN LIGHT
CHANDELIER
WALL MOUNTED
NEON RECTANGULAR







Project Type	Residential
Owner	Khalid Khadir Hasan AL-Saeed
Location	Amman
Plot No.	1659
Basin No.	19
Designed by	A.Shaker Khulief 4809

SHEET NAME

GROUND FLOOR-BATHROOM 03

ID-4140

Date	08/10/2019
Scale	As indicated

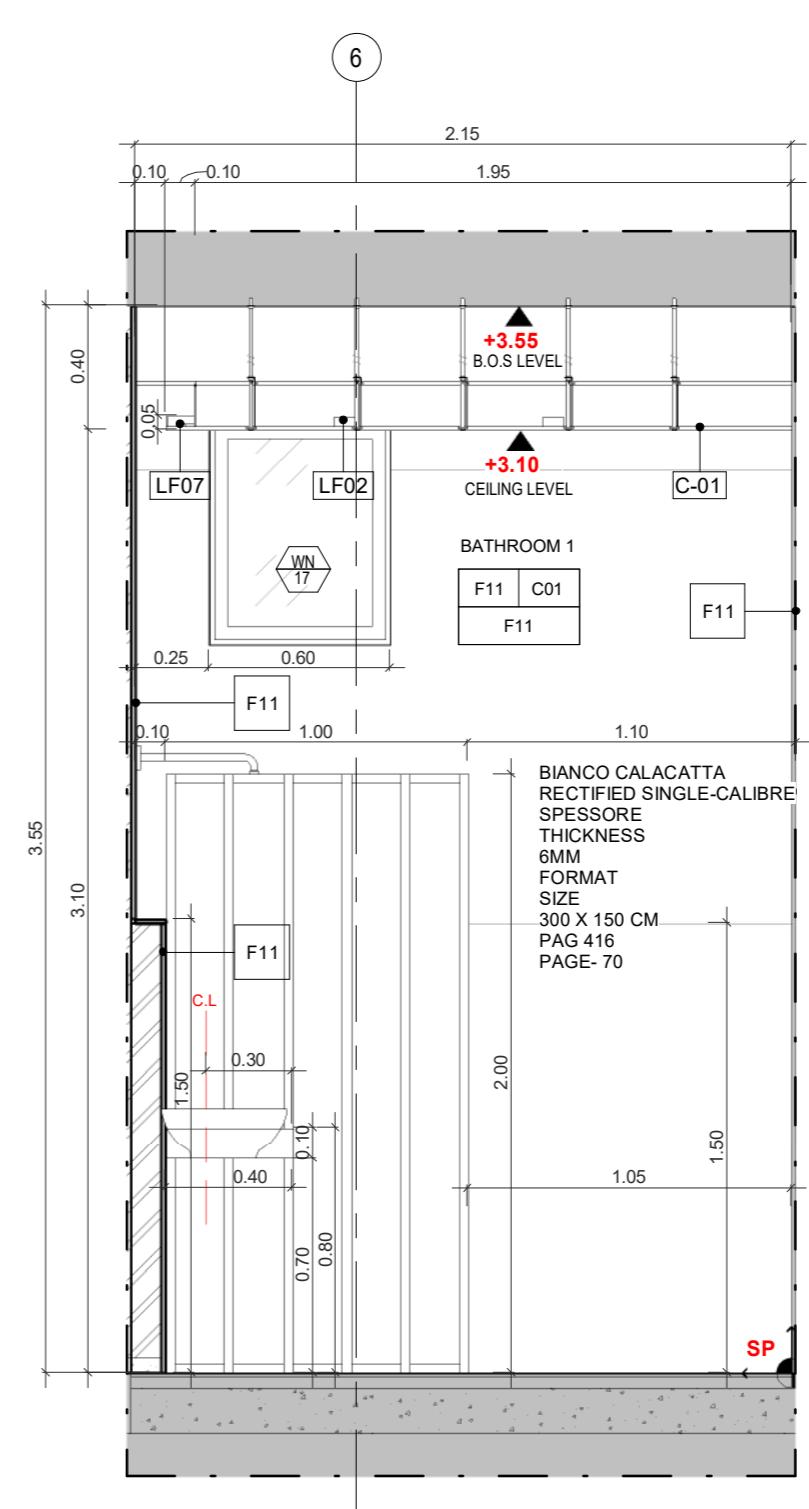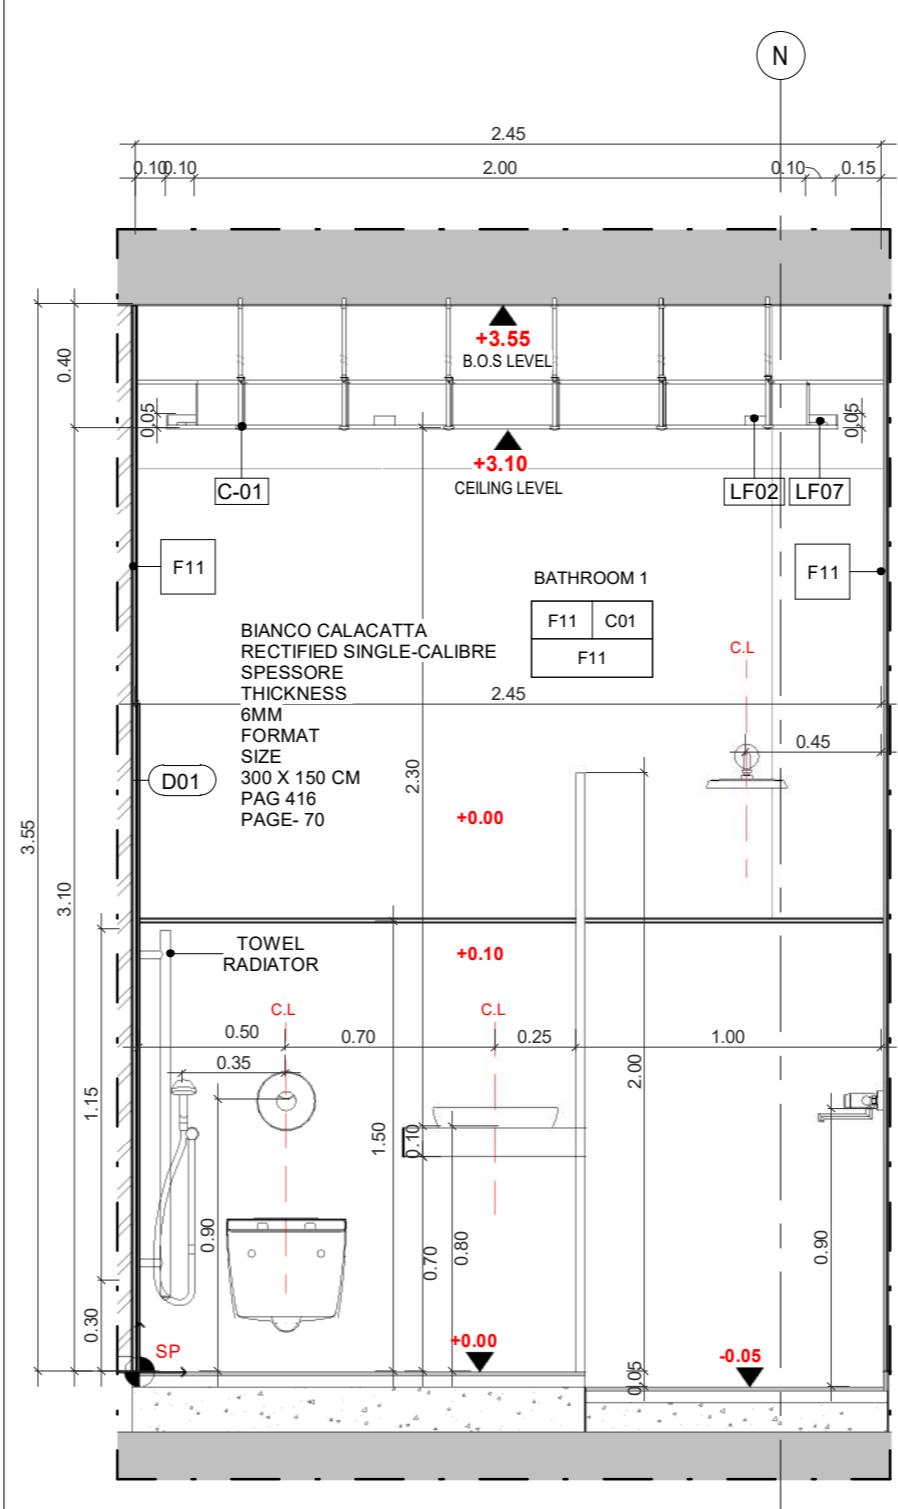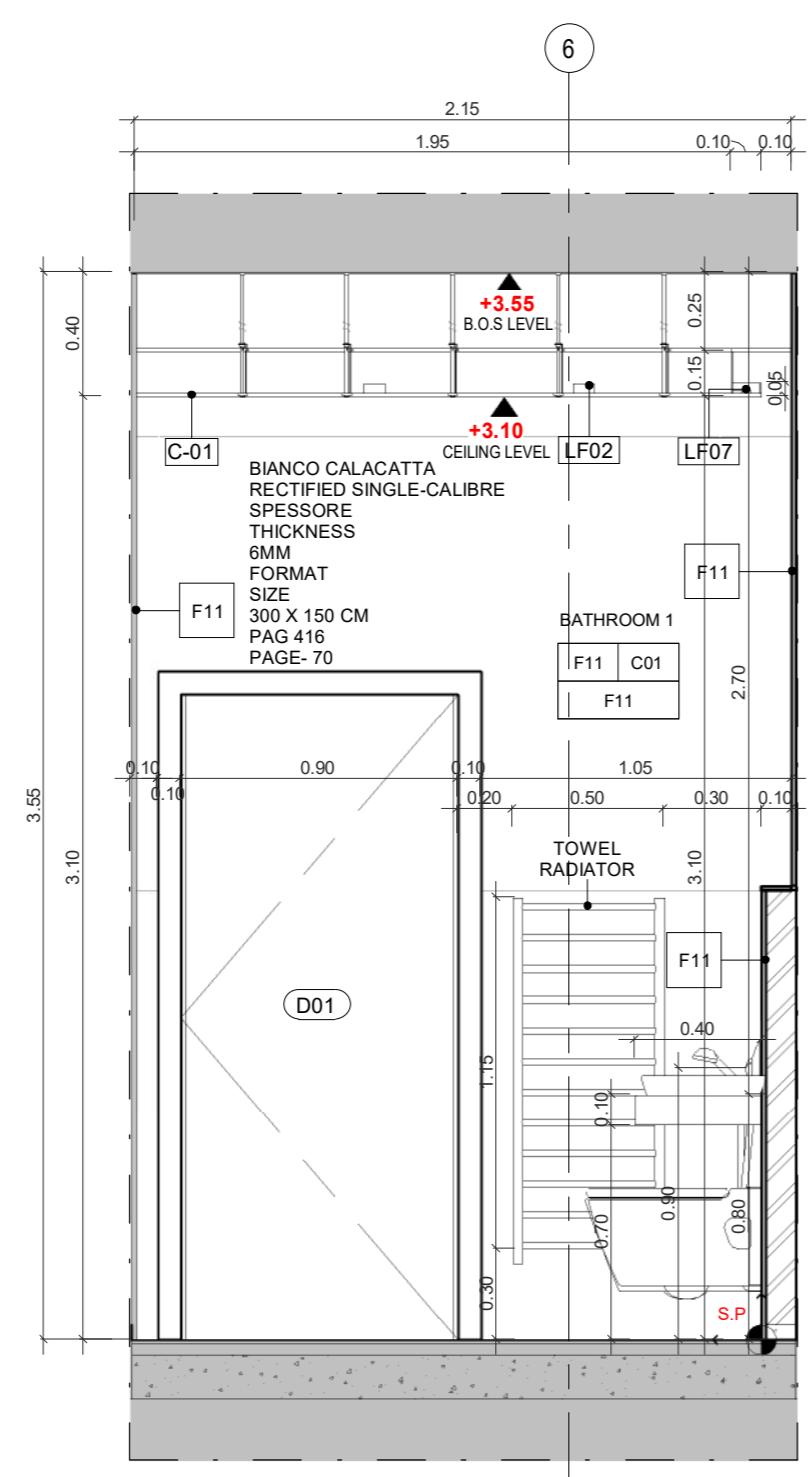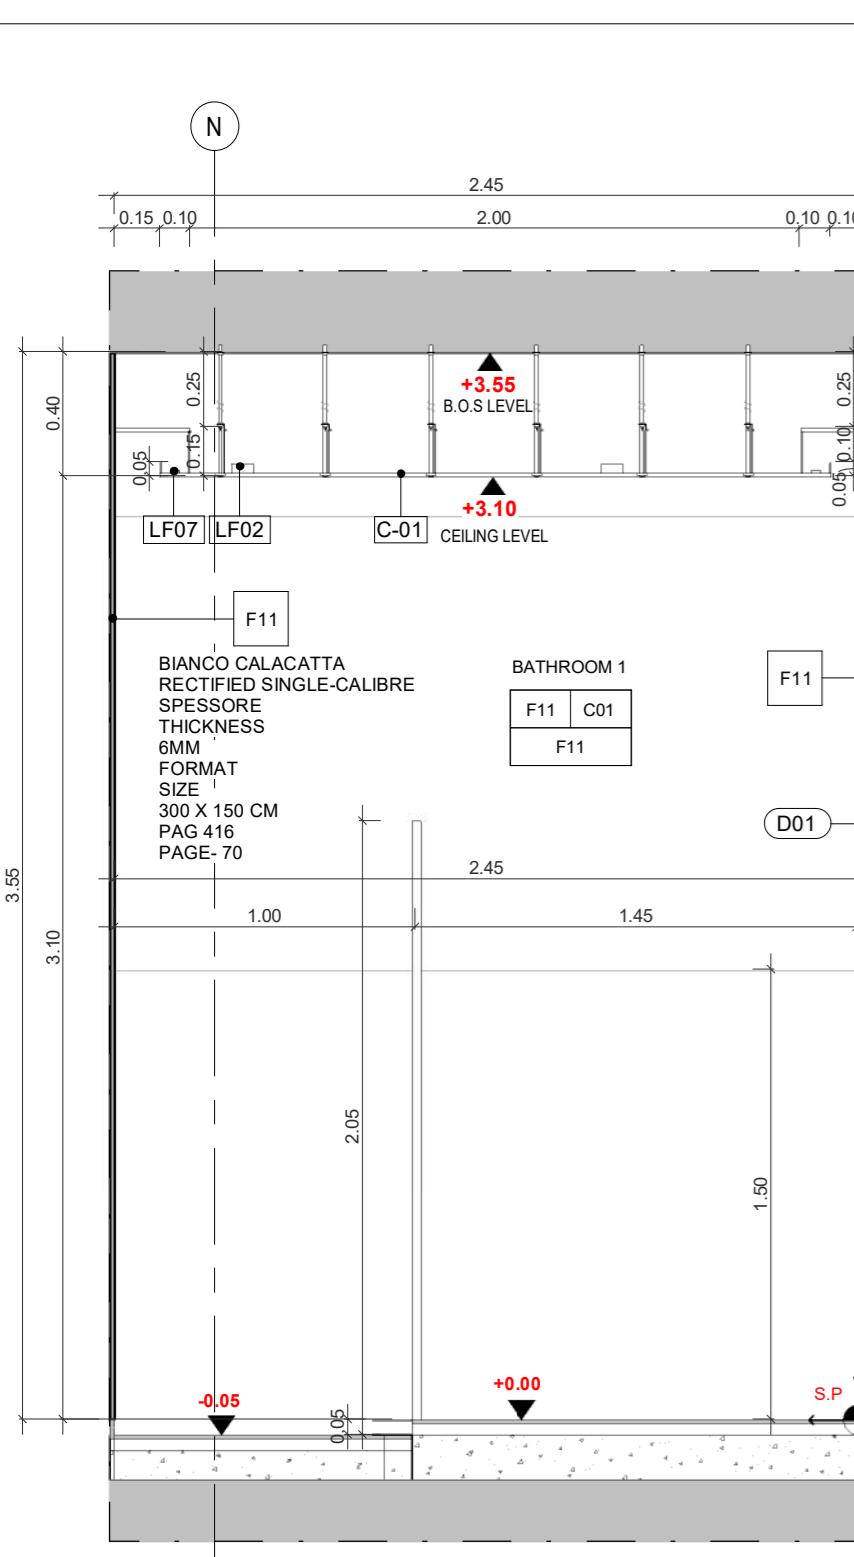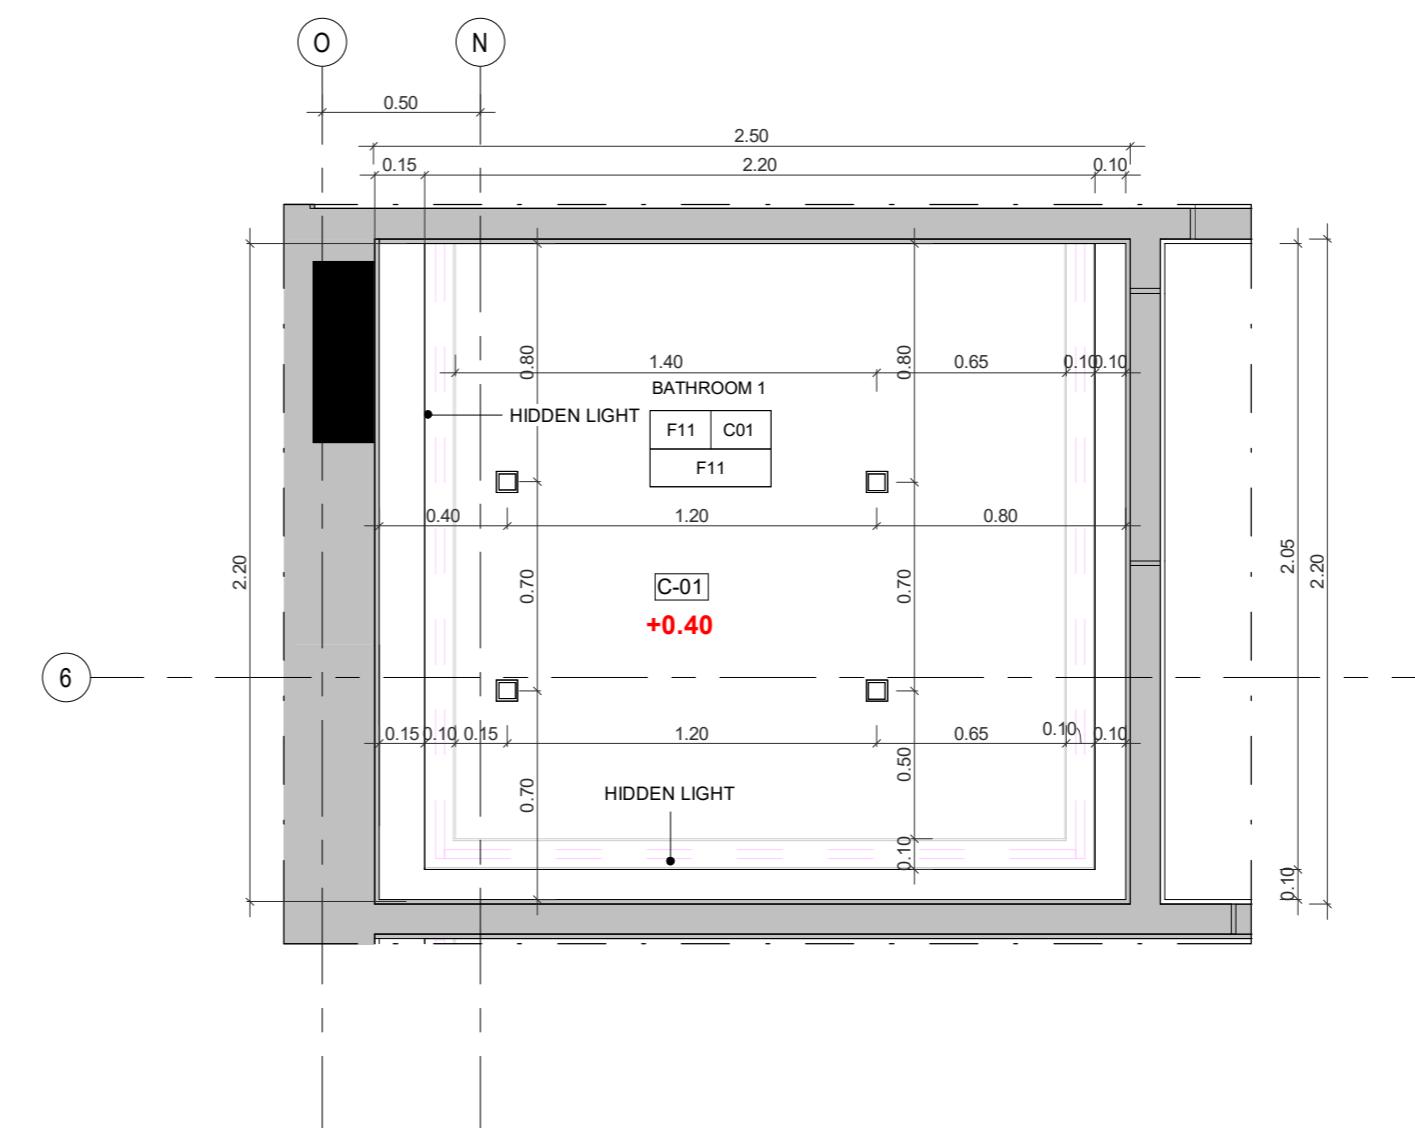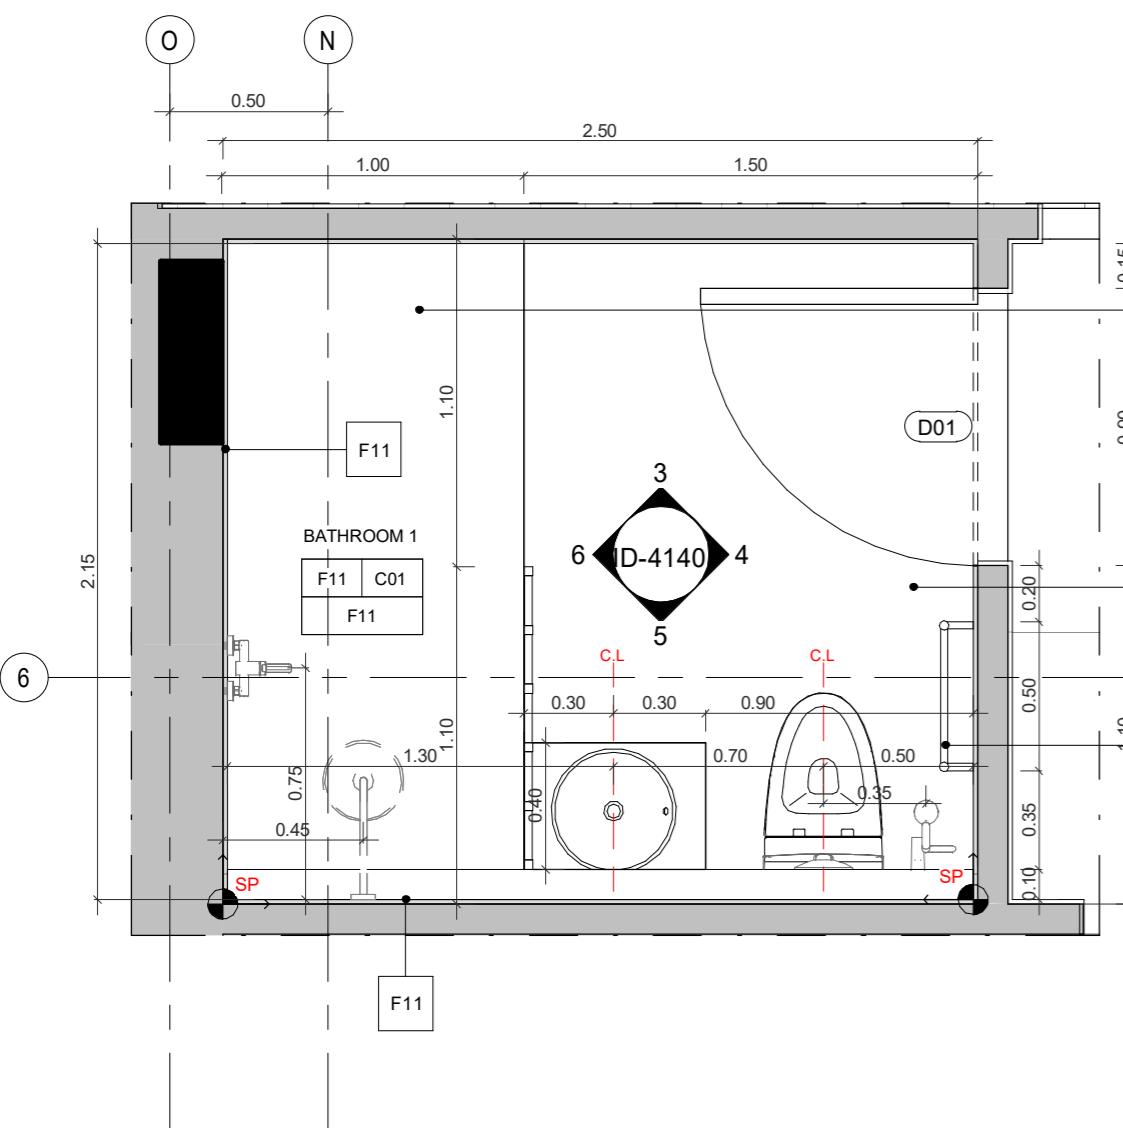

PROJECT NAME

APARTMENTS BUILDING

NOTES


FOR FINISHES REFER TO SHEETS:
ID-6000
ID-6001

ROOM NAME

FLOOR FINISH	CEILING FINISH
--------------	----------------

WALL FINISH

FINISHES SCHEDULE		FINISHES SCHEDULE	
Material: Mark	Description	Material: Mark	Description
F01	WHITE PAINT	F15	BEIGE PAINT
F02	GOLD WOOD	F16	TRAVERTINO MARBLE
F03	GOLD STONE	F17	LEATHER
F04	DARK WOOD	F05	DECORATIVE STONE
F06	WOOD	F18	PAINT GOLD METAL EFFECT
F07	BLACK MARBLE	F19	DECORATIVE WOOD
F08	BEIGE MARBLE	F20	GREY STONE
F09	GREY STONE	F21	CONCRETE FINISH
F10	WALL PAPER	F22	KITCHENNETE WOOD
F11	CALCATTÀ	F12	SWIMMING POOL MARBLE
F13	BLACK PAINT	F23	SWIMMING POOL WALL FINISH
F14	CALCATTÀ	F24	PARQUET
		F25	WHITE FINISH GRC

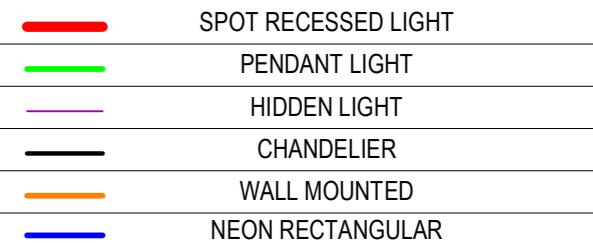

Project Type	Residential
Owner	Khalid Khadir Hasan AL-Saeed
Location	Amman
Plot No.	1659
Basin No.	19
Designed by	A.Shaker Khulief 4809





SHEET NAME

GROUND FLOOR - GUEST BATHROOM

ID-4150

Date 08/10/2019

Scale As indicated

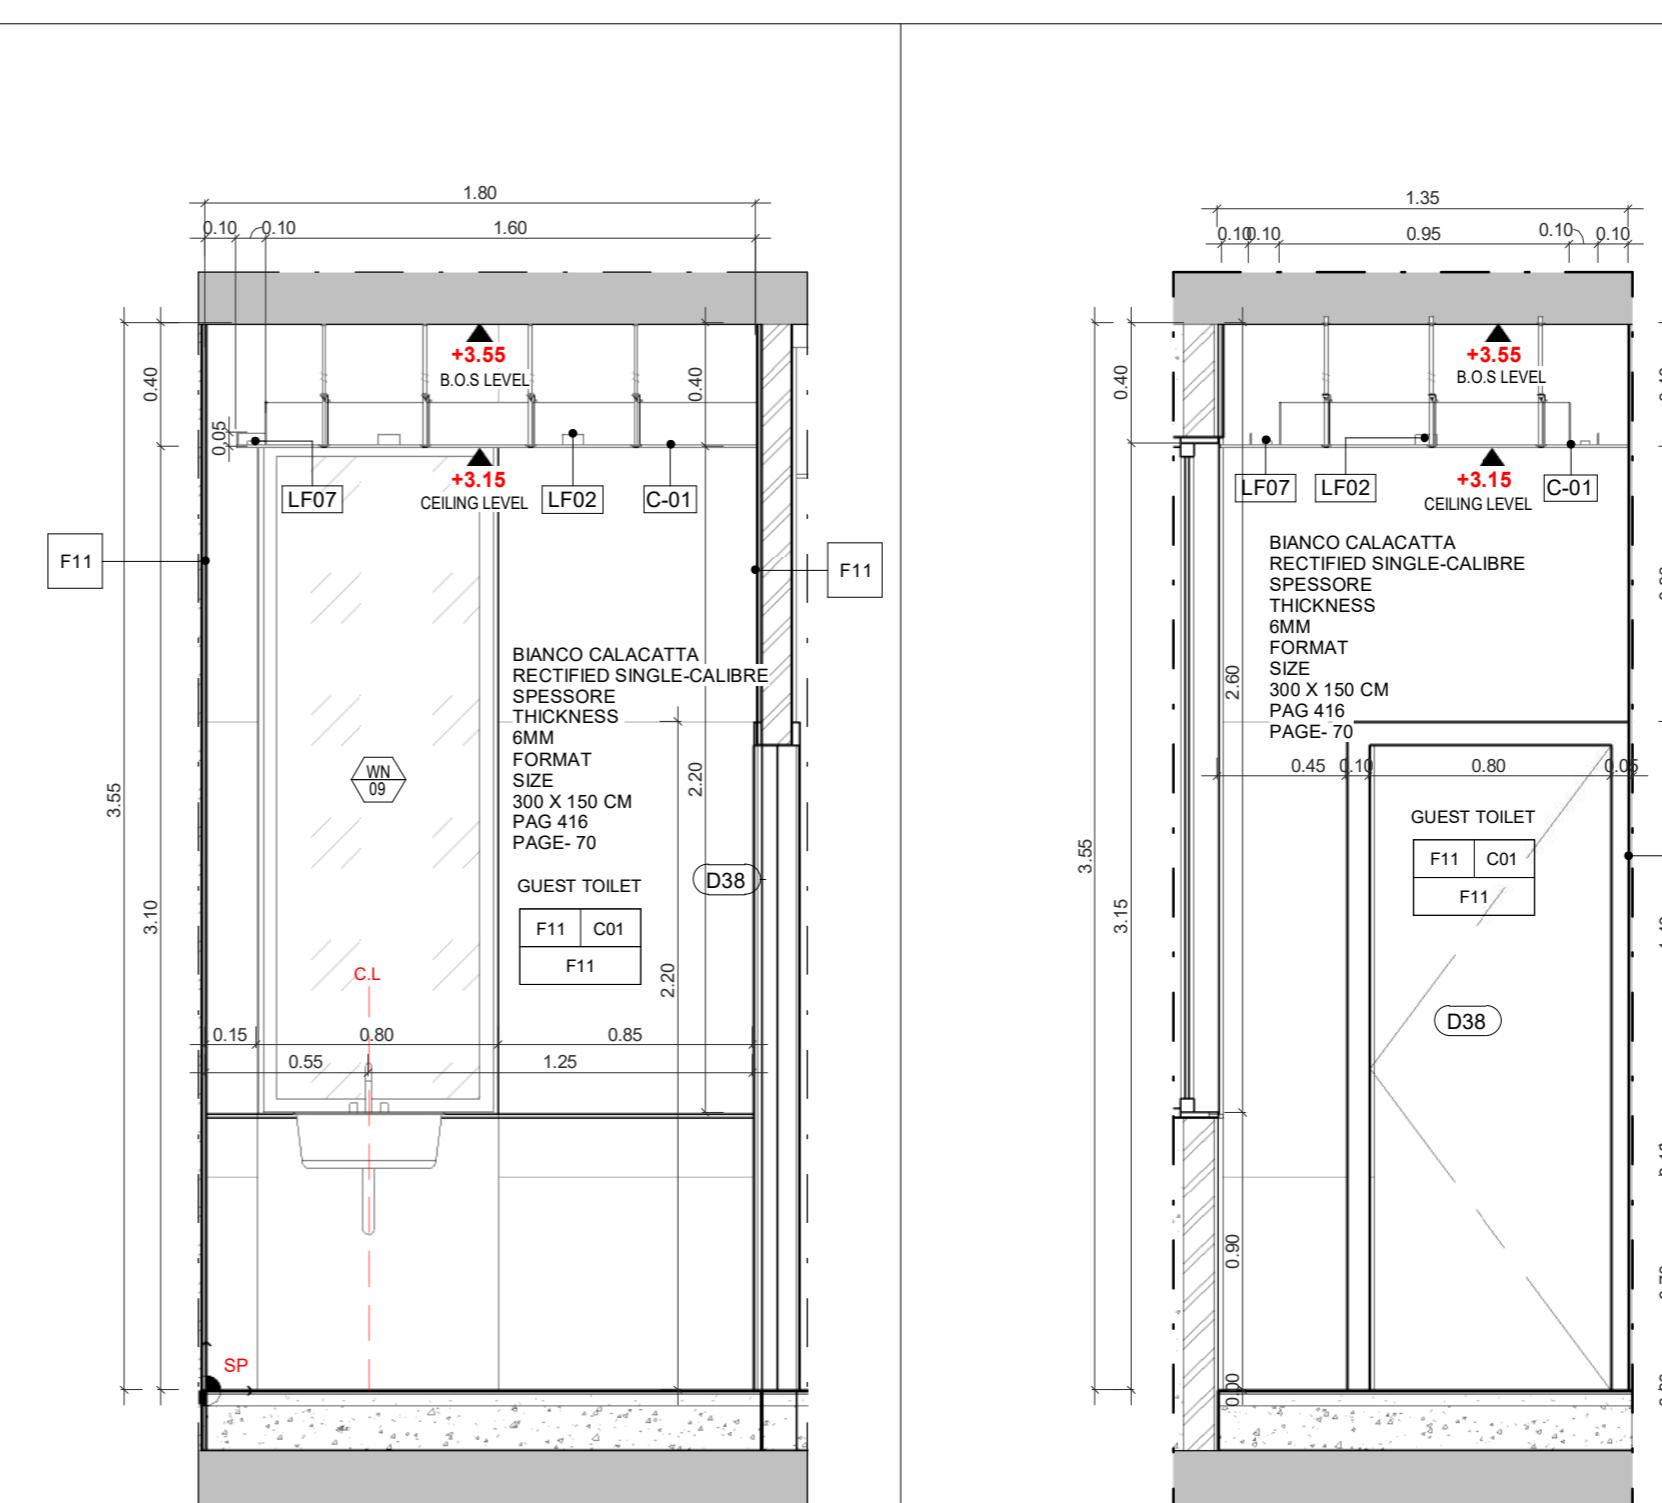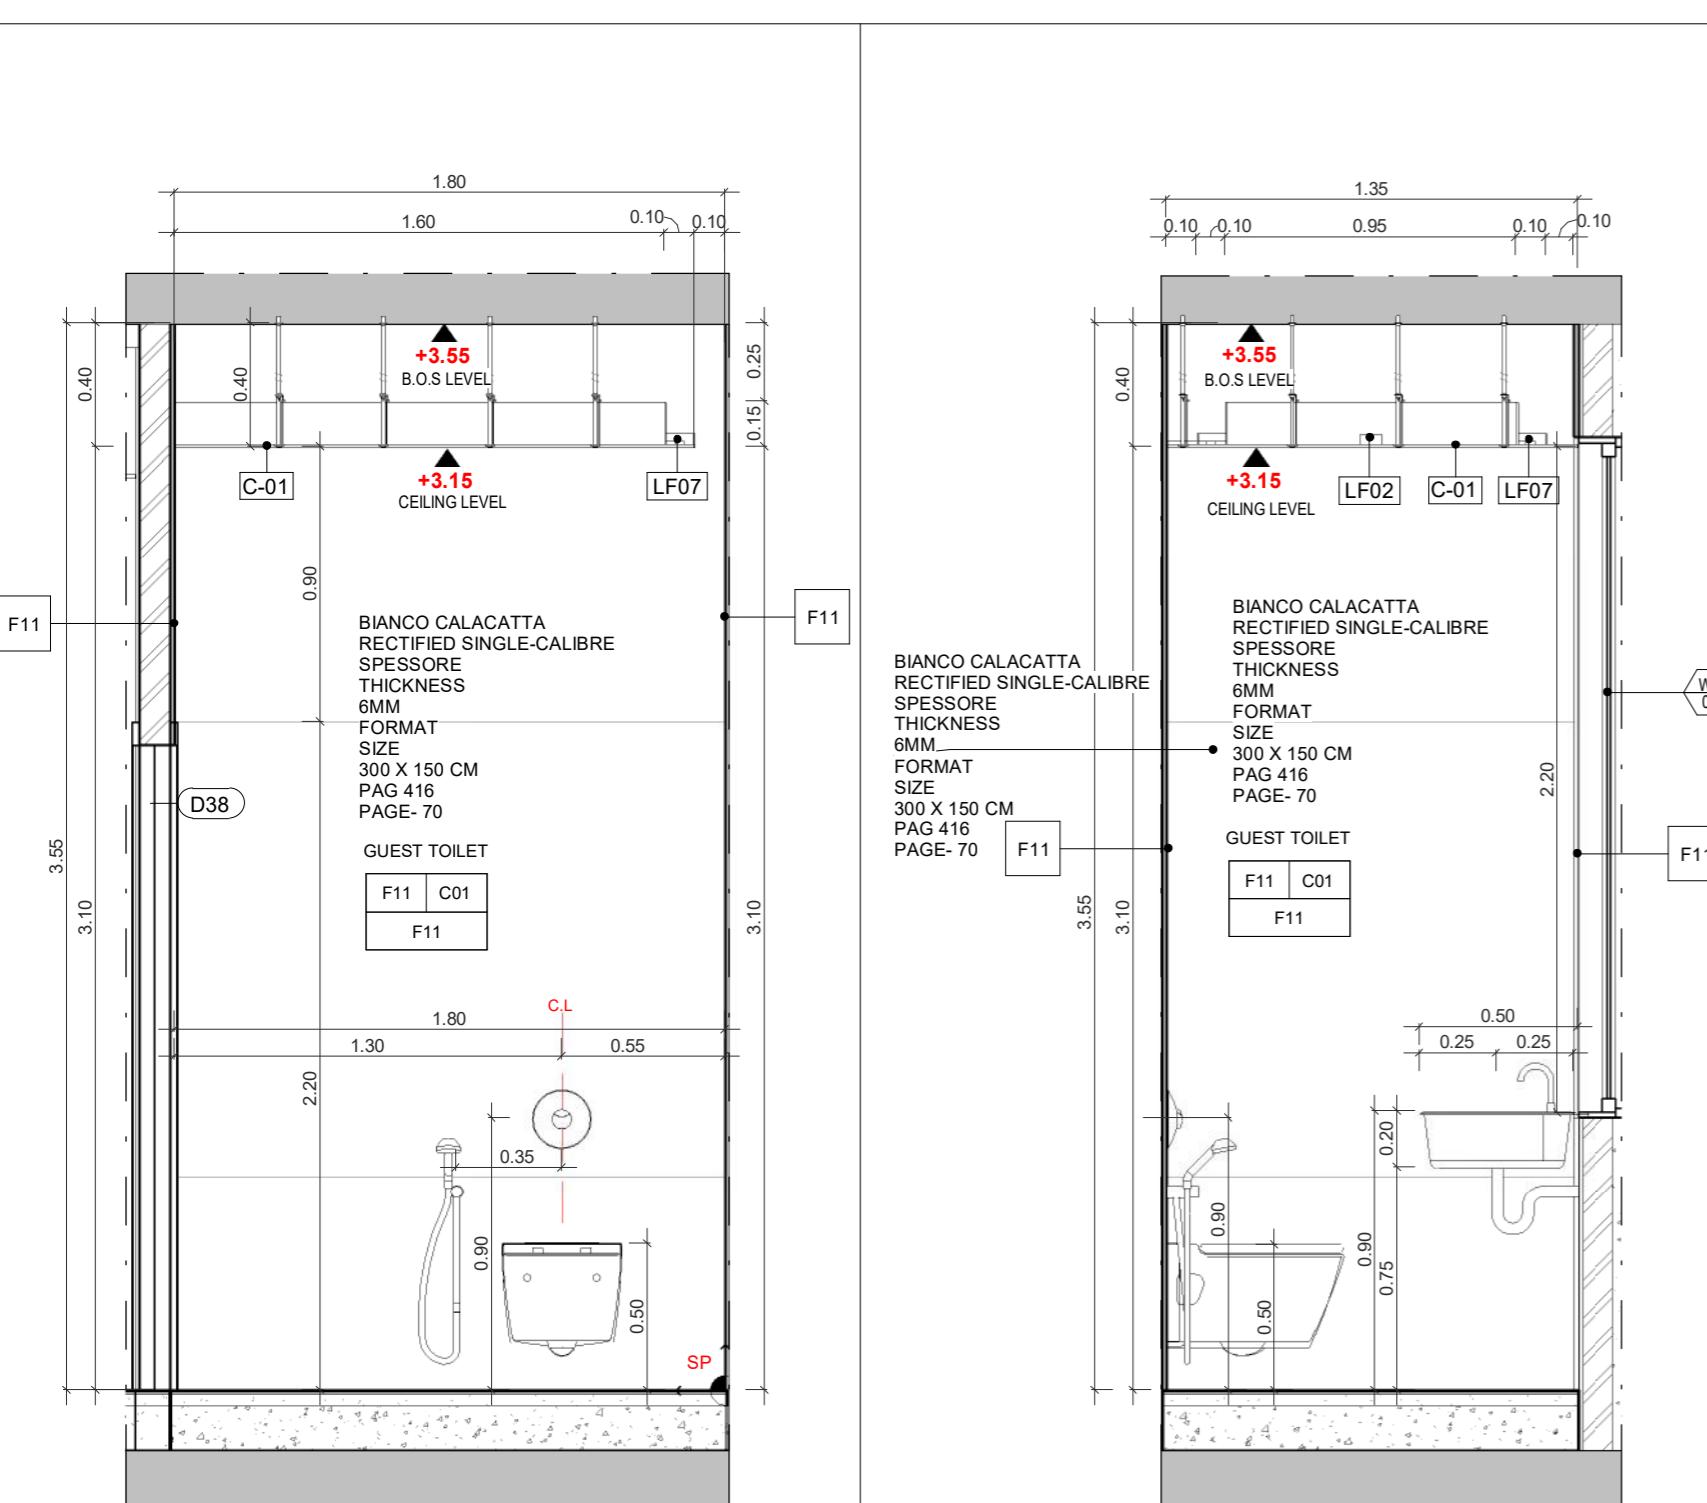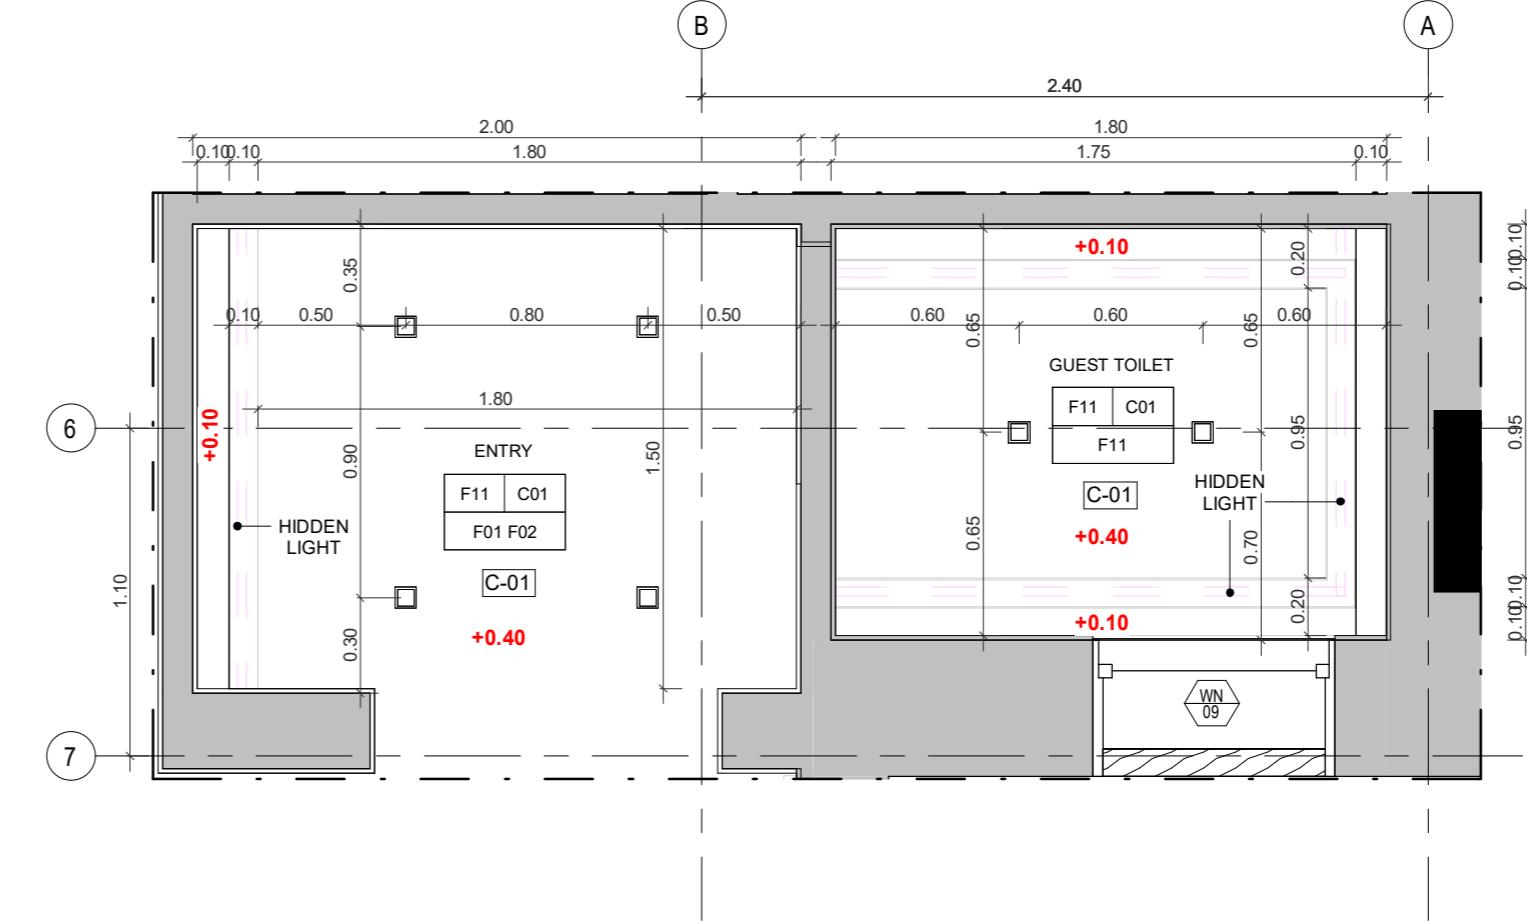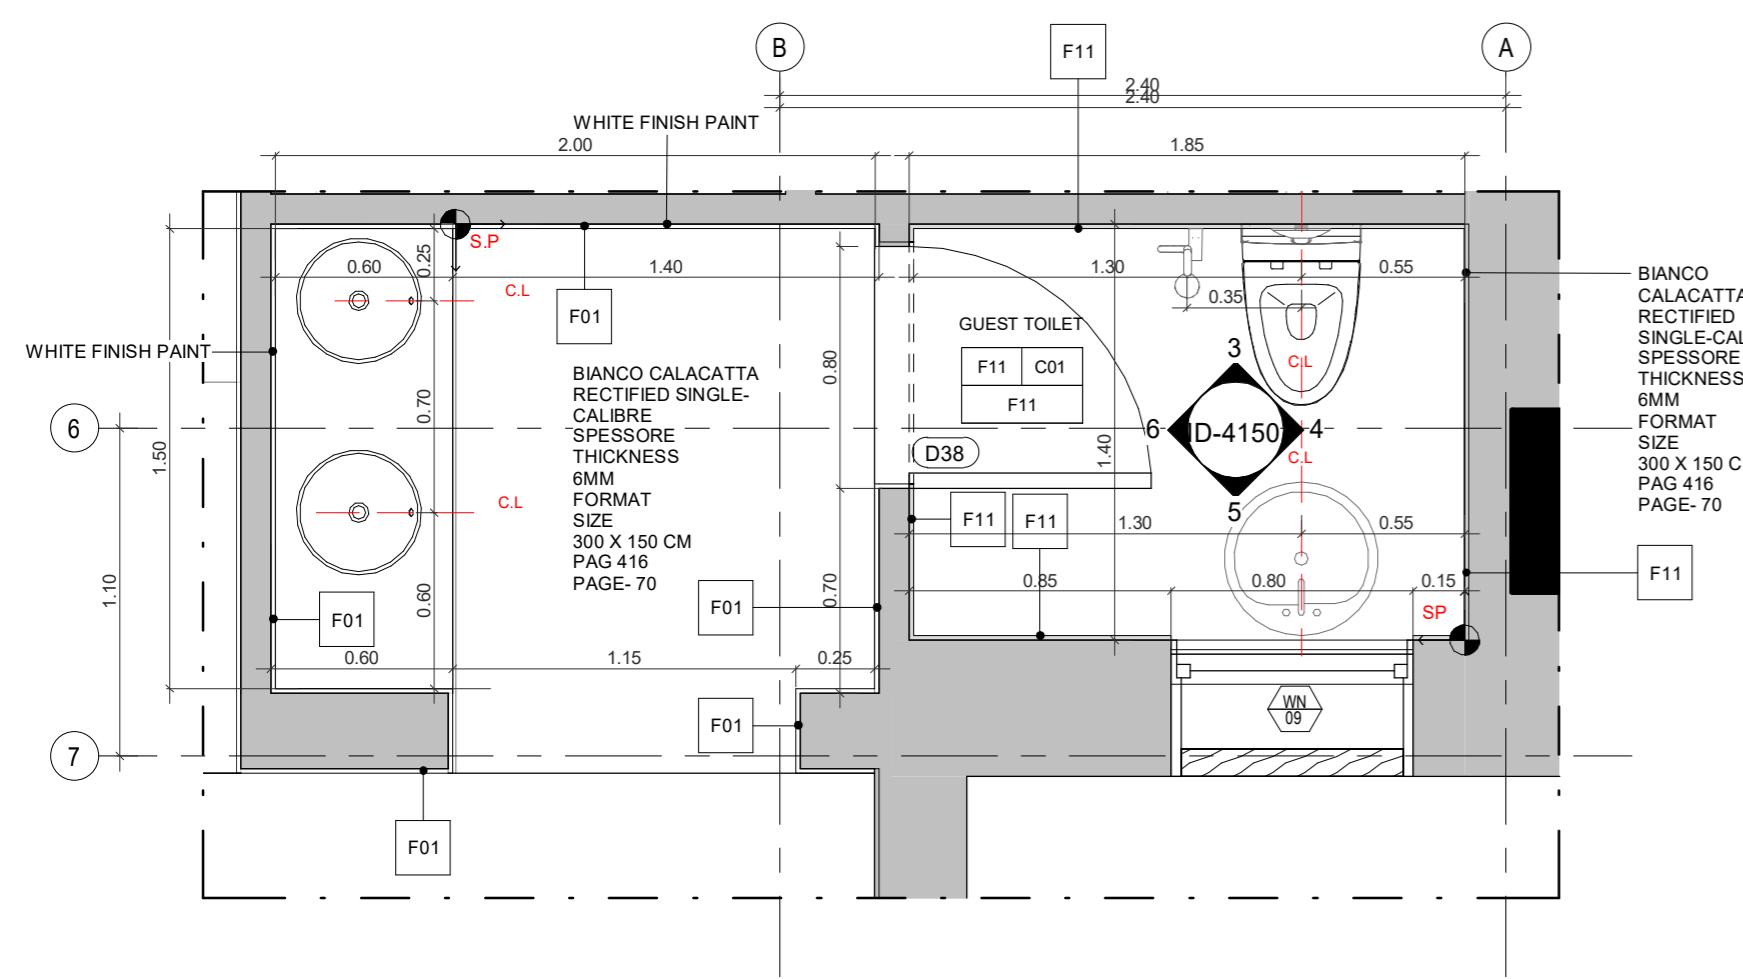

5 GUEST BATHROOM -ELEVATION 03
1 : 25

6 GUEST BATHROOM -ELEVATION 04
1 : 25

PROJECT NAME

APARTMENTS BUILDING

NOTES



Project Type	Residential
Owner	Khalid Khadir Hasan AL-Saeed
Location	Amman
Plot No.	1659
Basin No.	19
Designed by	A.Shaker Khulief 4809

SHEET NAME



LIVING ROOM-SHOT

ID-4200


Date 08/10/2019

Scale


PROJECT NAME	APARTMENTS BUILDING		
NOTES			
ROOM NAME	FLOOR FINISH	CEILING FINISH	
WALL FINISH			
FINISHES SCHEDULE	FINISHES SCHEDULE		
Material: Mark	DESCRIPTION	Material: Mark	DESCRIPTION
F01	WHITE PAINT	F15	BEIGE PAINT
F02	GOLD WOOD	F16	TRAVERTINO MARBLE
F03	GOLD STONE	F17	LEATHER
F04	DARK WOOD	F18	PAINT GOLD METAL EFFECT
F05	DECORATIVE STONE	F19	DECORATIVE WOOD
F06	WOOD	F20	GREY STONE
F07	BLACK MARBLE	F21	CONCRETE FINISH
F08	BEIGE MARBLE	F22	KITCHENNETE WOOD
F09	GREY STONE	F23	SWIMMING POOL MARBLE
F10	WALL PAPER	F24	SWIMMING POOL WALL FINISH
F11	CALCAGNA	F25	PARQUET
F12	SWIMMING POOL MARBLE		
F13	BLACK PAINT		
F14	CALCAGNA		
SPOT RECESSED LIGHT			
PENDANT LIGHT			
HIDDEN LIGHT			
CHANDELIER			
WALL MOUNTED			
NEON RECTANGULAR			
Project Type	Residential		
Owner	Khalid Khadir Hasan AL-Saeed		
Location	Amman		
Plot No.	1659		
Basin No.	19		
Designed by	A.Shaker Khulief 4809		
SHEET NAME	FIRST FLOOR - LIVING ROOM		
ID-4201			
Date	08/10/2019		
Scale	As indicated		

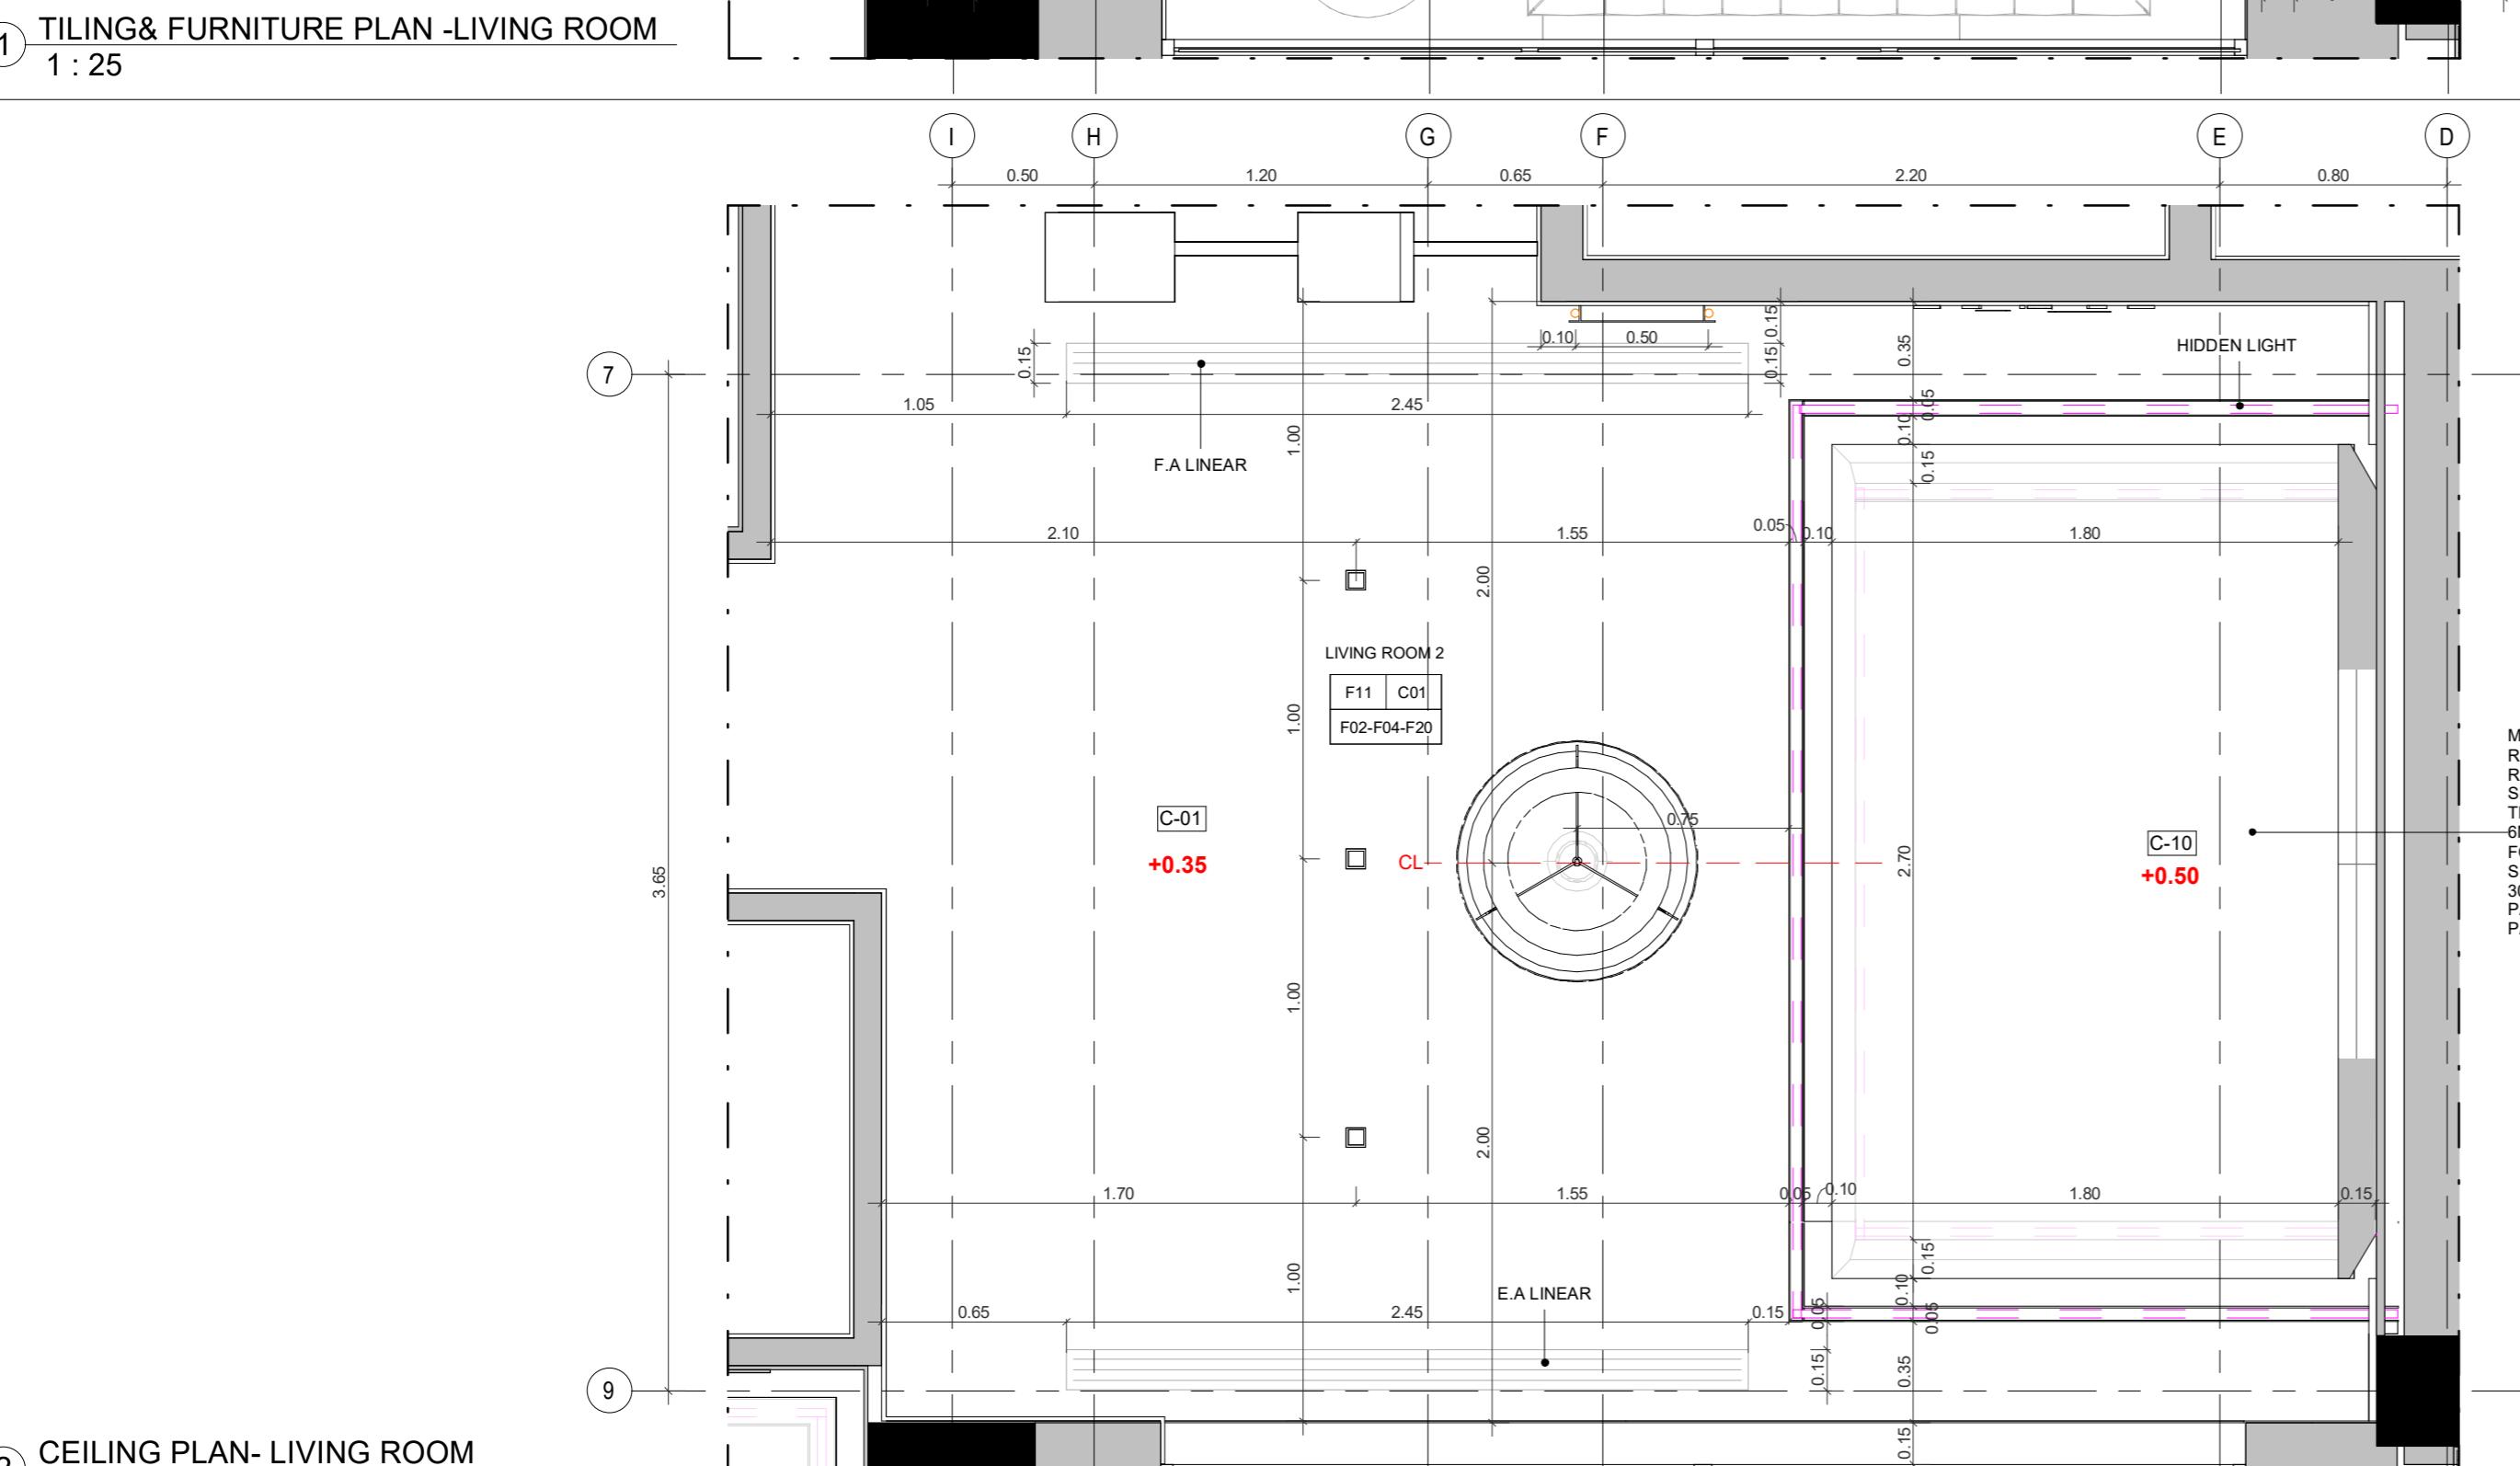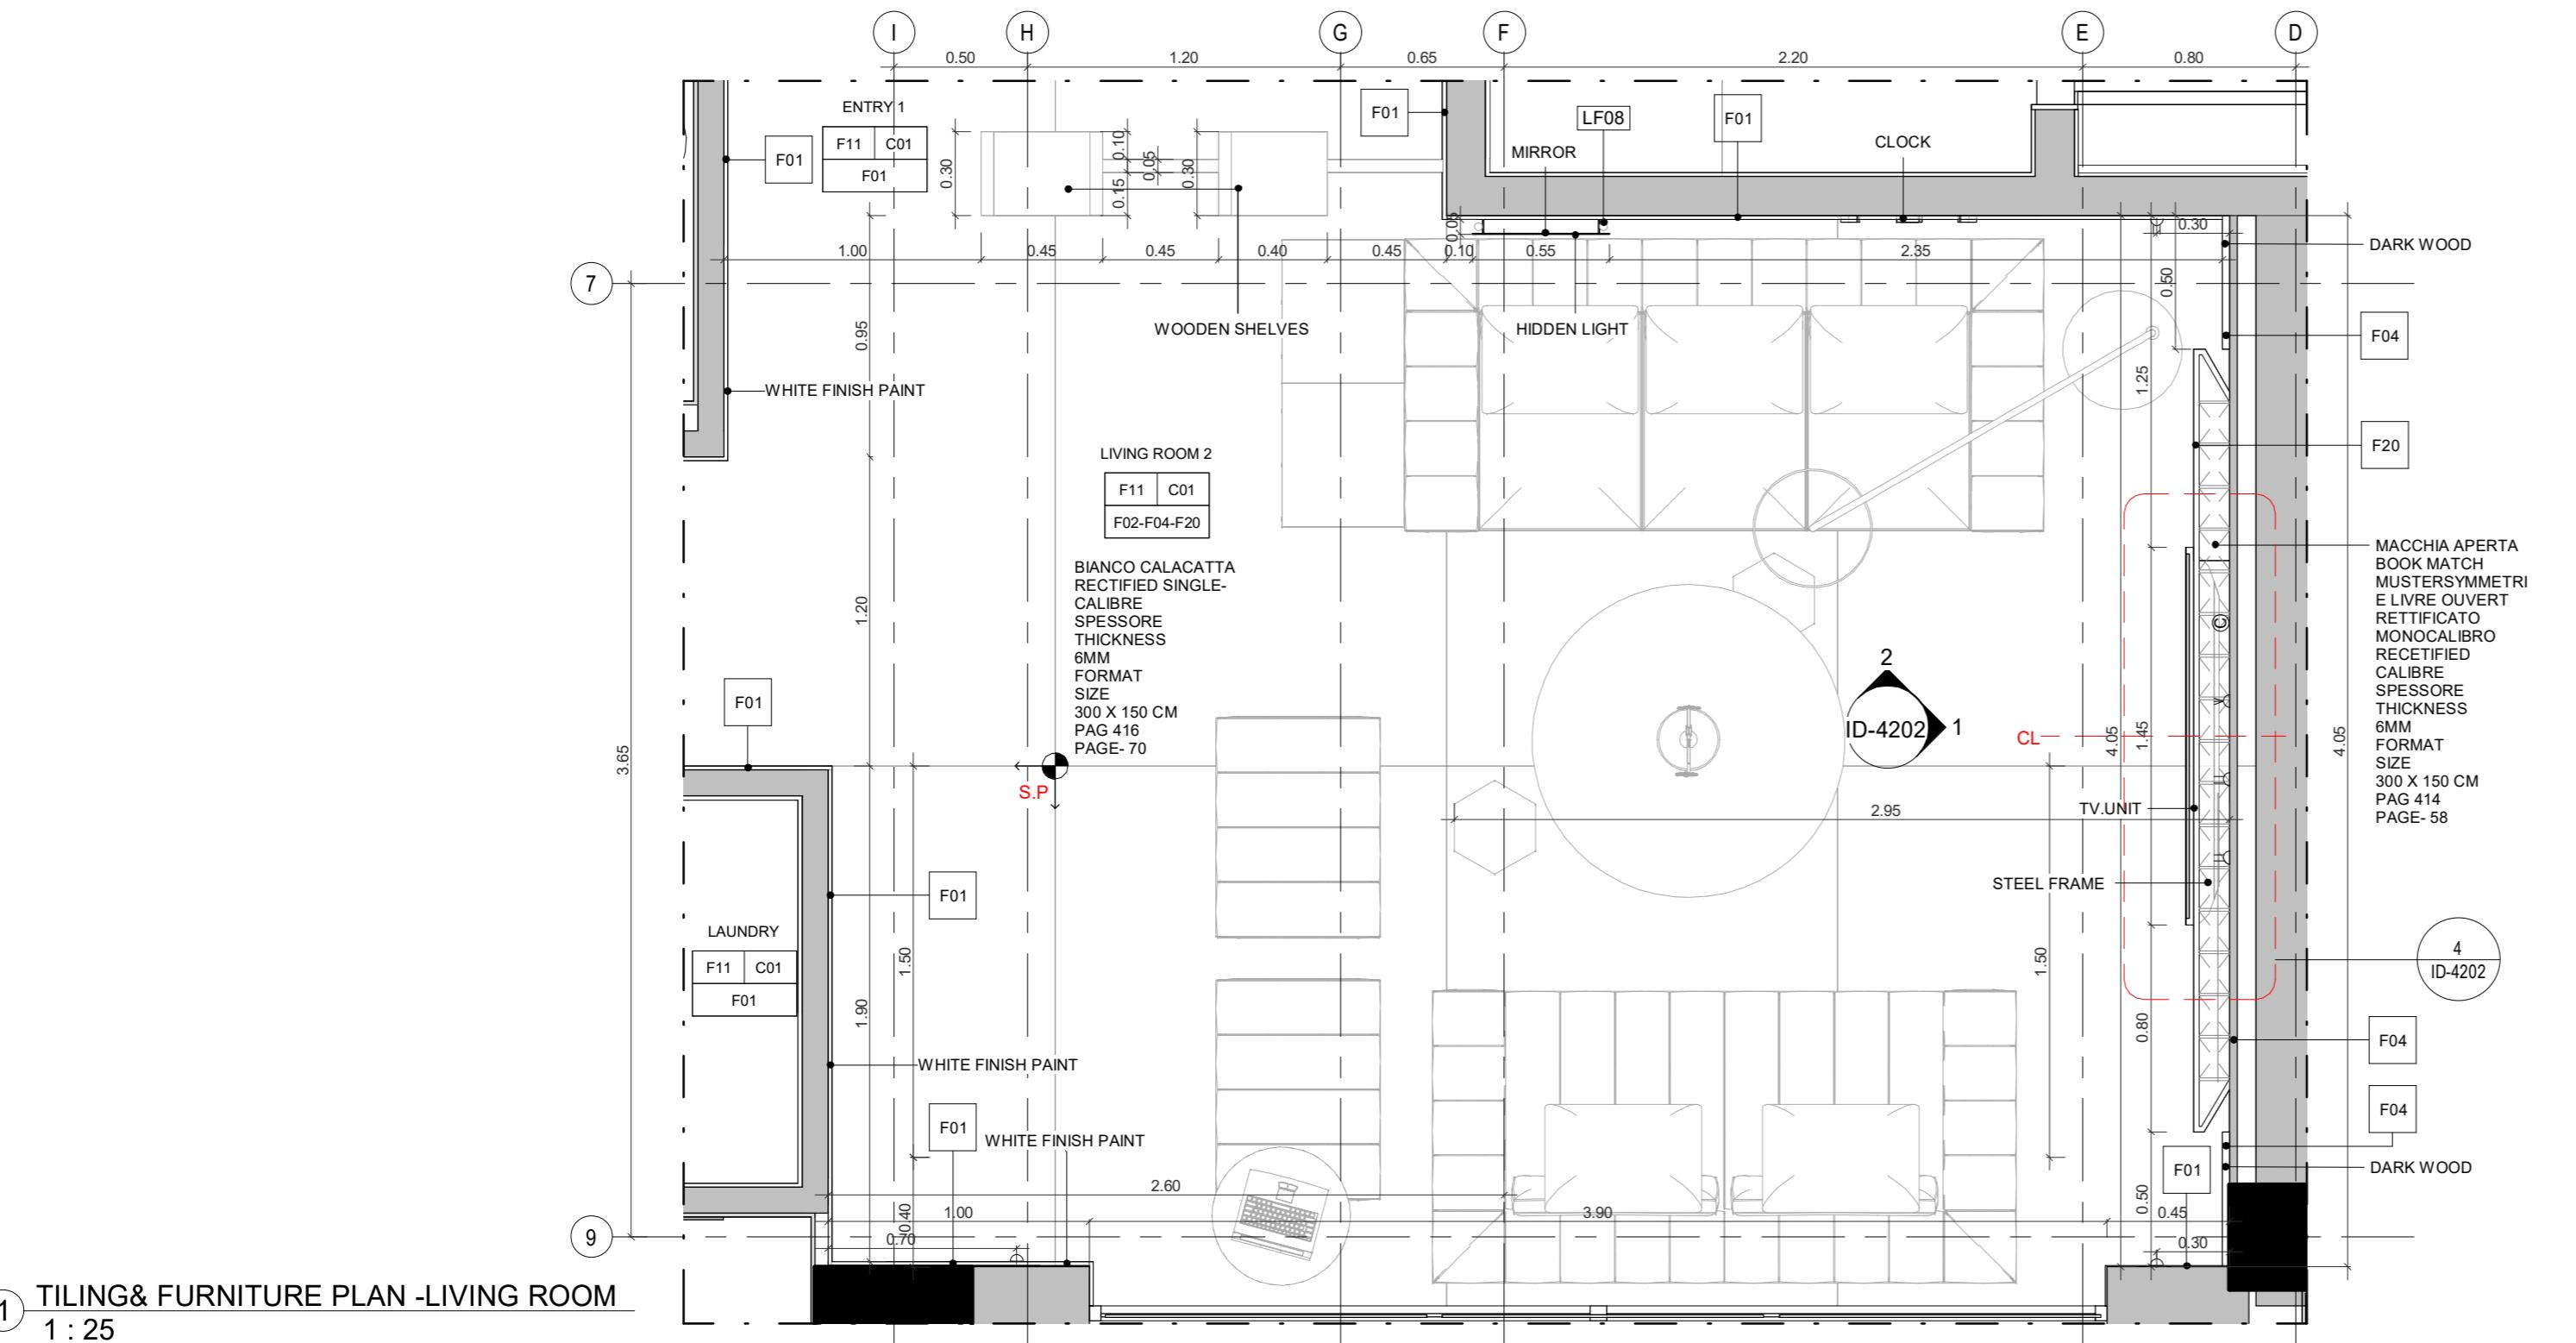


PROJECT NAME	APARTMENTS BUILDING	
NOTES	
ROOM NAME	FLOOR FINISH	CEILING FINISH	
WALL FINISH	
<table border="1"> <thead> <tr> <th colspan="2">FINISHES SCHEDULE</th> <th>FINISHES SCHEDULE</th> </tr> <tr> <th>Material: Mark</th> <th>DESCRIPTION</th> <th>Material: Mark</th> <th>DESCRIPTION</th> </tr> </thead> <tbody> <tr> <td>F01</td> <td>WHITE PAINT</td> <td>F15</td> <td>BEIGE PAINT</td> </tr> <tr> <td>F02</td> <td>GOLD WOOD</td> <td>F16</td> <td>TRAVERTINO MARBLE</td> </tr> <tr> <td>F03</td> <td>GOLD STONE</td> <td>F17</td> <td>LEATHER</td> </tr> <tr> <td>F04</td> <td>DARK WOOD</td> <td>F05</td> <td>DECORATIVE STONE</td> </tr> <tr> <td>F06</td> <td>WOOD</td> <td>F18</td> <td>PAINT GOLD METAL EFFECT</td> </tr> <tr> <td>F07</td> <td>BLACK MARBLE</td> <td>F19</td> <td>DECORATIVE WOOD</td> </tr> <tr> <td>F08</td> <td>BEIGE MARBLE</td> <td>F20</td> <td>GREY STONE</td> </tr> <tr> <td>F09</td> <td>GREY STONE</td> <td>F21</td> <td>CONCRETE FINISH</td> </tr> <tr> <td>F10</td> <td>WALL PAPER</td> <td>F22</td> <td>KITCHENNETE WOOD</td> </tr> <tr> <td>F11</td> <td>CALCATTÀ</td> <td>F12</td> <td>SWIMMING POOL MARBLE</td> </tr> <tr> <td>F13</td> <td>BLACK PAINT</td> <td>F23</td> <td>SWIMMING POOL WALL FINISH</td> </tr> <tr> <td>F14</td> <td>CALCATTÀ</td> <td>F24</td> <td>PARQUET</td> </tr> <tr> <td>F25</td> <td>WHITE FINISH GRC</td> <td>F25</td> <td>WHITE FINISH GRC</td> </tr> </tbody> </table>		FINISHES SCHEDULE		FINISHES SCHEDULE	Material: Mark	DESCRIPTION	Material: Mark	DESCRIPTION	F01	WHITE PAINT	F15	BEIGE PAINT	F02	GOLD WOOD	F16	TRAVERTINO MARBLE	F03	GOLD STONE	F17	LEATHER	F04	DARK WOOD	F05	DECORATIVE STONE	F06	WOOD	F18	PAINT GOLD METAL EFFECT	F07	BLACK MARBLE	F19	DECORATIVE WOOD	F08	BEIGE MARBLE	F20	GREY STONE	F09	GREY STONE	F21	CONCRETE FINISH	F10	WALL PAPER	F22	KITCHENNETE WOOD	F11	CALCATTÀ	F12	SWIMMING POOL MARBLE	F13	BLACK PAINT	F23	SWIMMING POOL WALL FINISH	F14	CALCATTÀ	F24	PARQUET	F25	WHITE FINISH GRC	F25	WHITE FINISH GRC
FINISHES SCHEDULE		FINISHES SCHEDULE	
Material: Mark	DESCRIPTION	Material: Mark	DESCRIPTION	
F01	WHITE PAINT	F15	BEIGE PAINT	
F02	GOLD WOOD	F16	TRAVERTINO MARBLE	
F03	GOLD STONE	F17	LEATHER	
F04	DARK WOOD	F05	DECORATIVE STONE	
F06	WOOD	F18	PAINT GOLD METAL EFFECT	
F07	BLACK MARBLE	F19	DECORATIVE WOOD	
F08	BEIGE MARBLE	F20	GREY STONE	
F09	GREY STONE	F21	CONCRETE FINISH	
F10	WALL PAPER	F22	KITCHENNETE WOOD	
F11	CALCATTÀ	F12	SWIMMING POOL MARBLE	
F13	BLACK PAINT	F23	SWIMMING POOL WALL FINISH	
F14	CALCATTÀ	F24	PARQUET	
F25	WHITE FINISH GRC	F25	WHITE FINISH GRC	
Project Type		Residential	
Owner	Khalid Khadir Hasan AL-Saeed	
Location	Amman	
Plot No.	1659	
Basin No.	19	
Designed by	A.Shaker Khulief 4809	
SHEET NAME	FIRST FLOOR- LIVING ROOM	
ID-4202	
Date	08/10/2019	
Scale	As indicated	

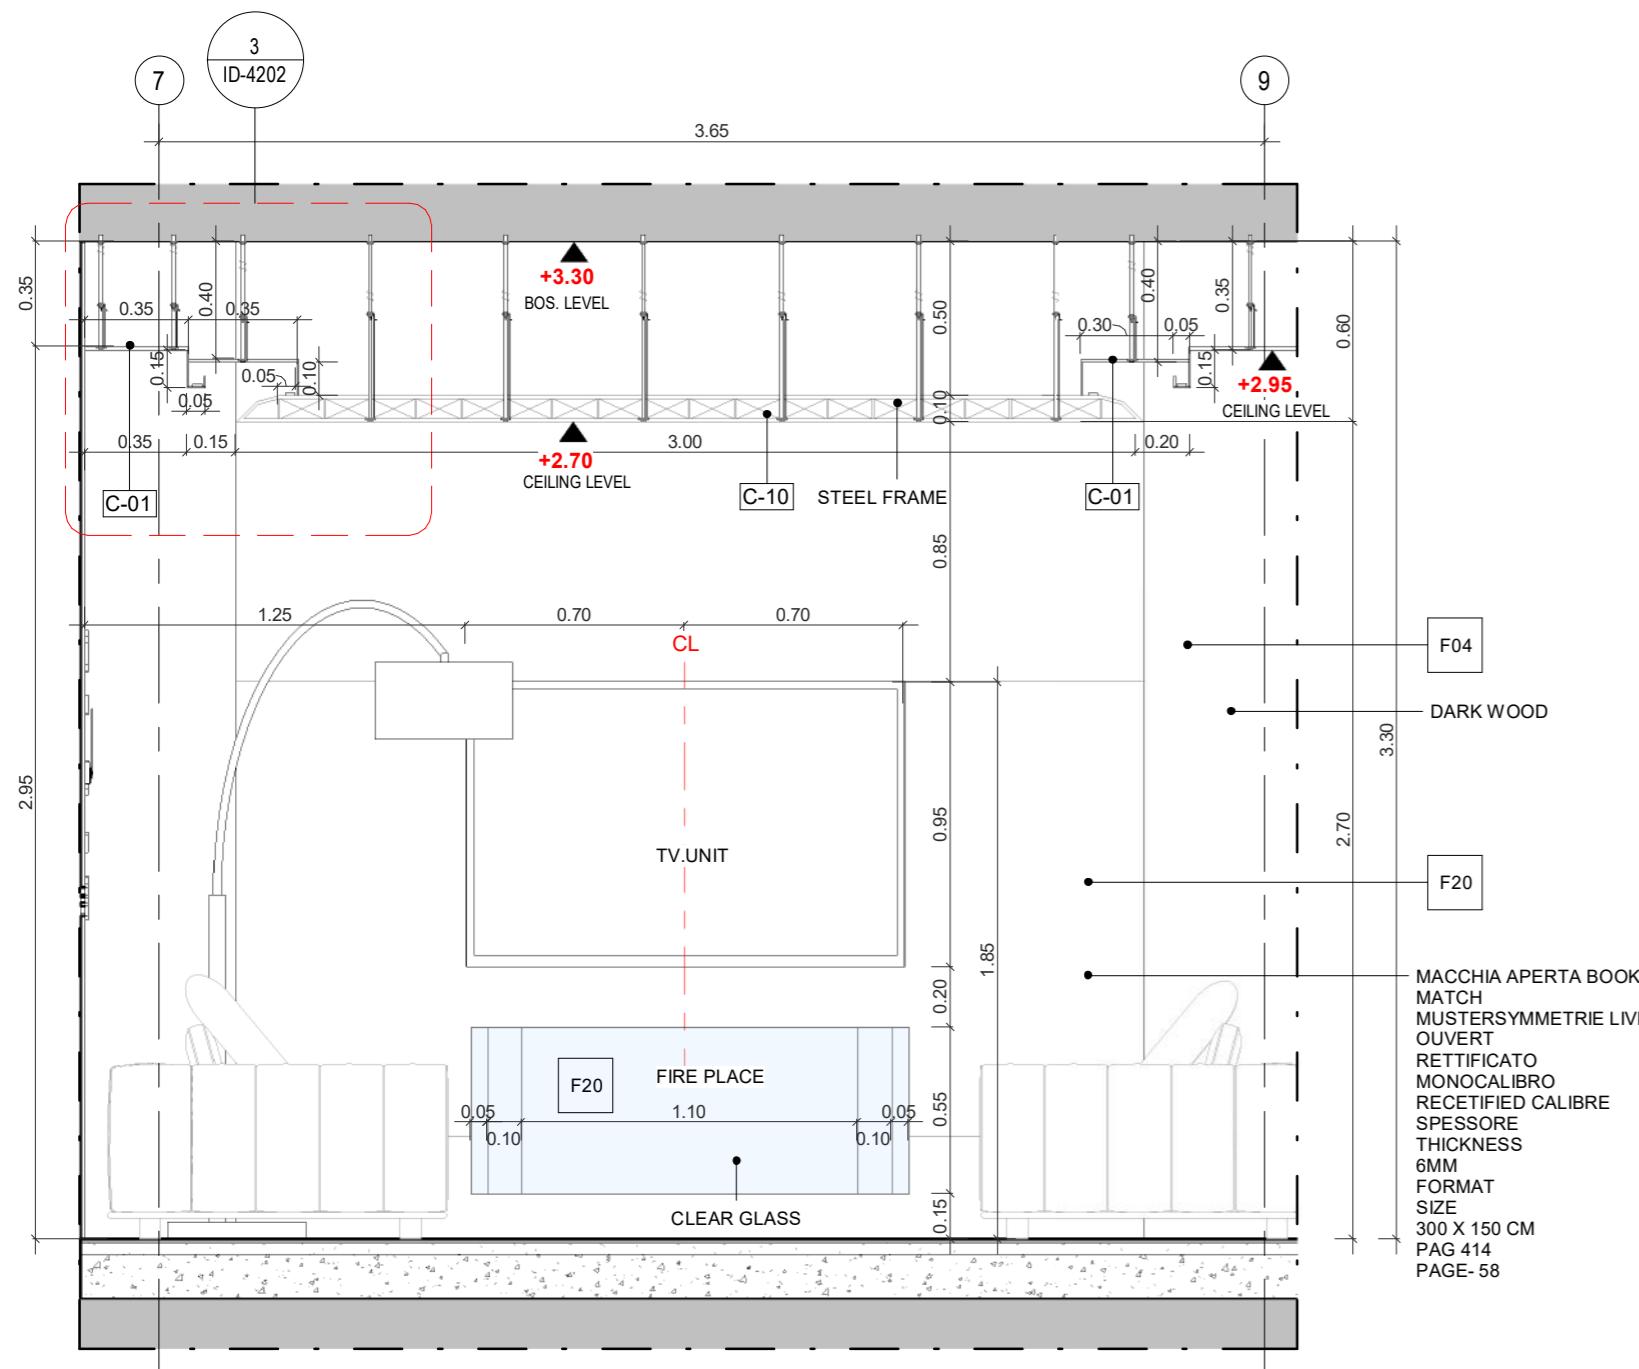


① LIVING ROOM -ELEVATION 01
1 : 25

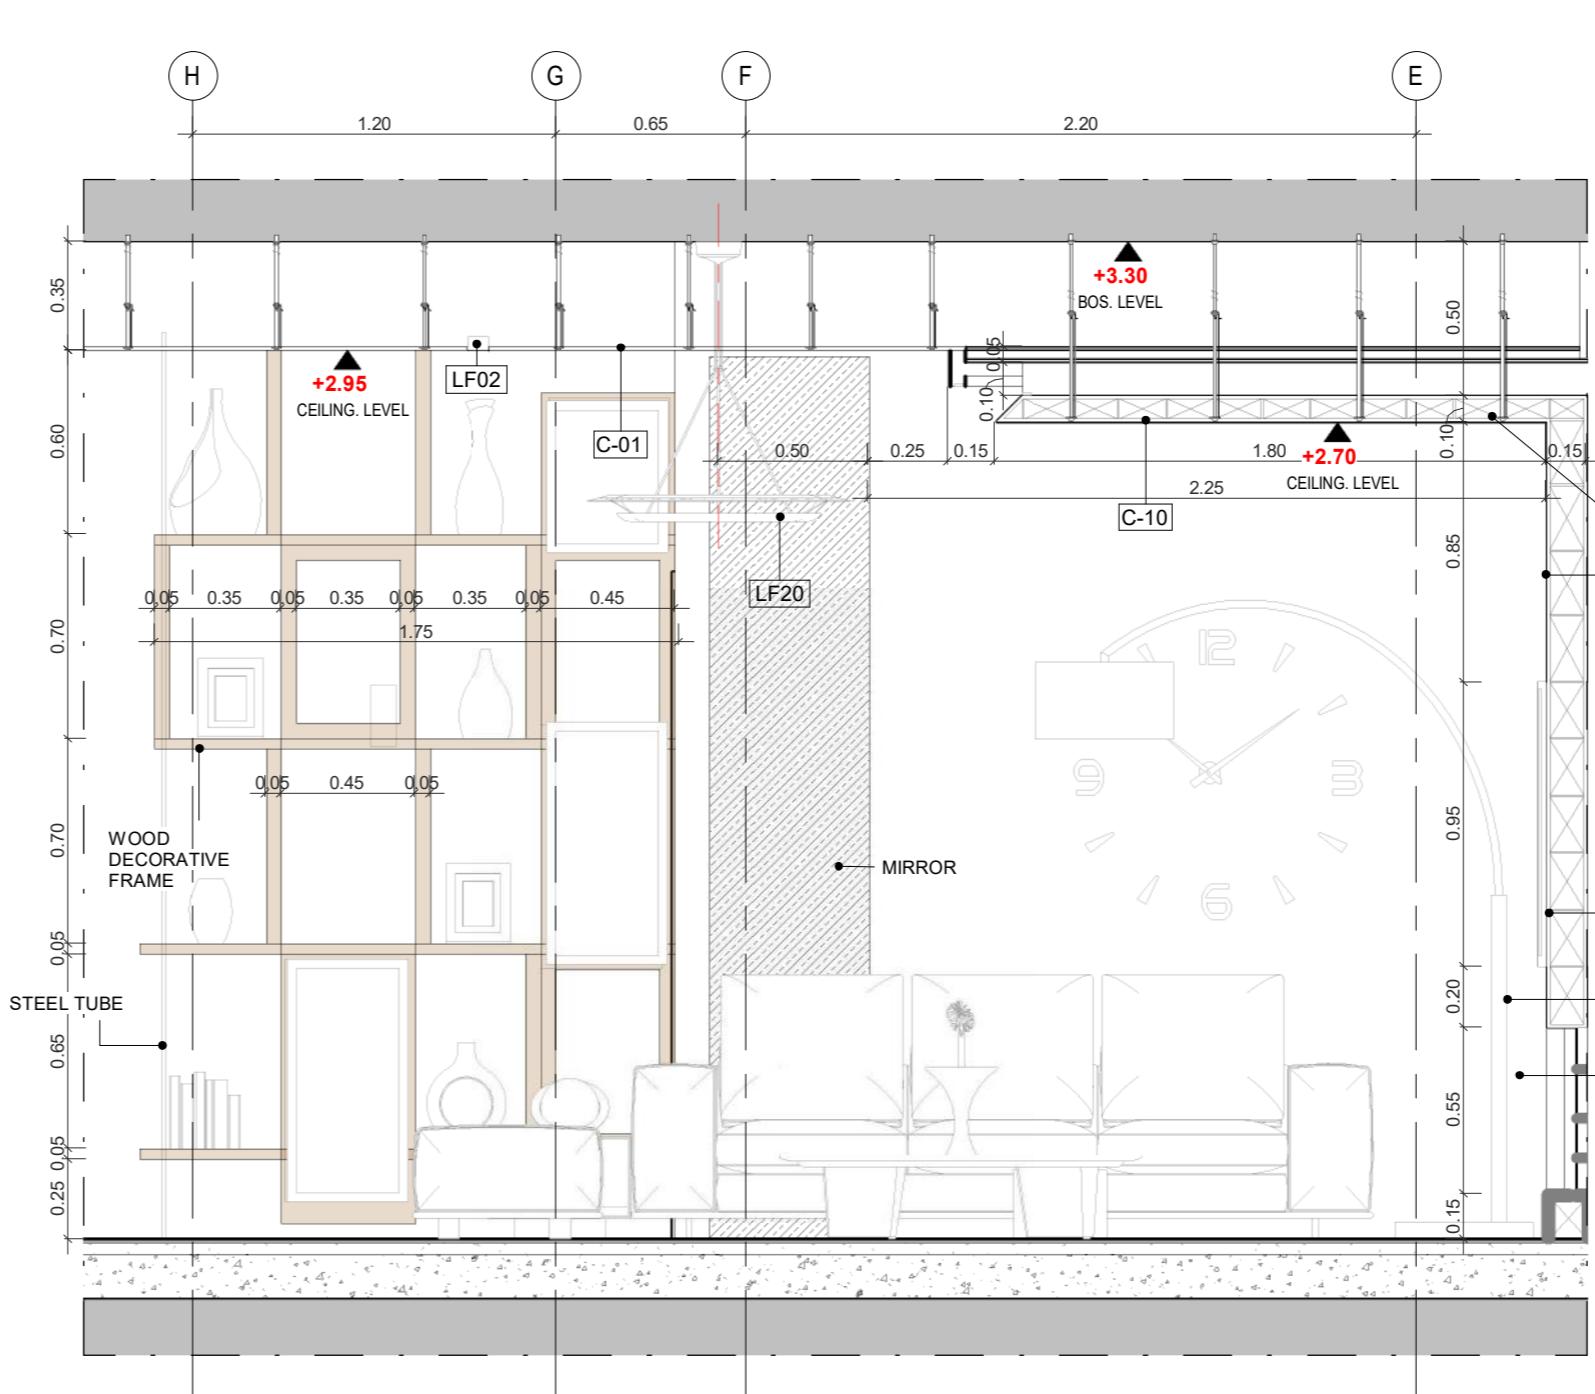

② LIVING ROOM -ELEVATION 02
1 : 25

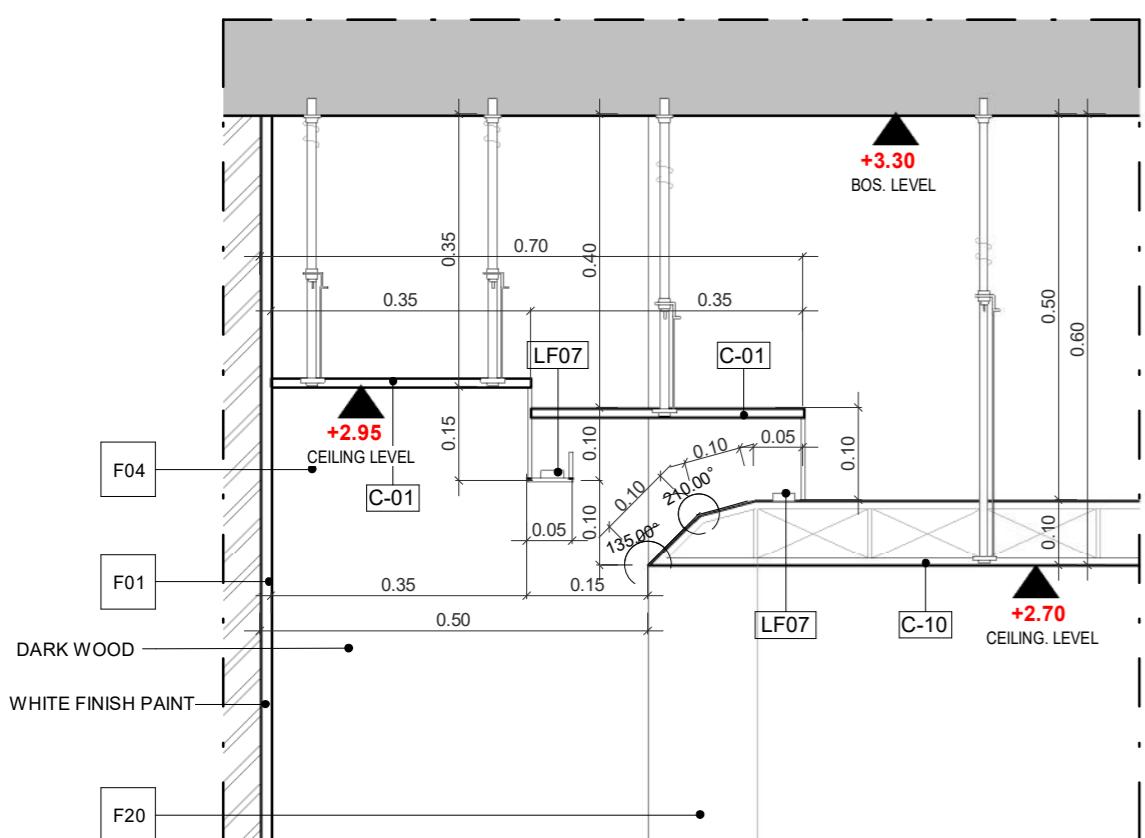

③ LIVING ROOM -CEILING DETAIL
1 : 10

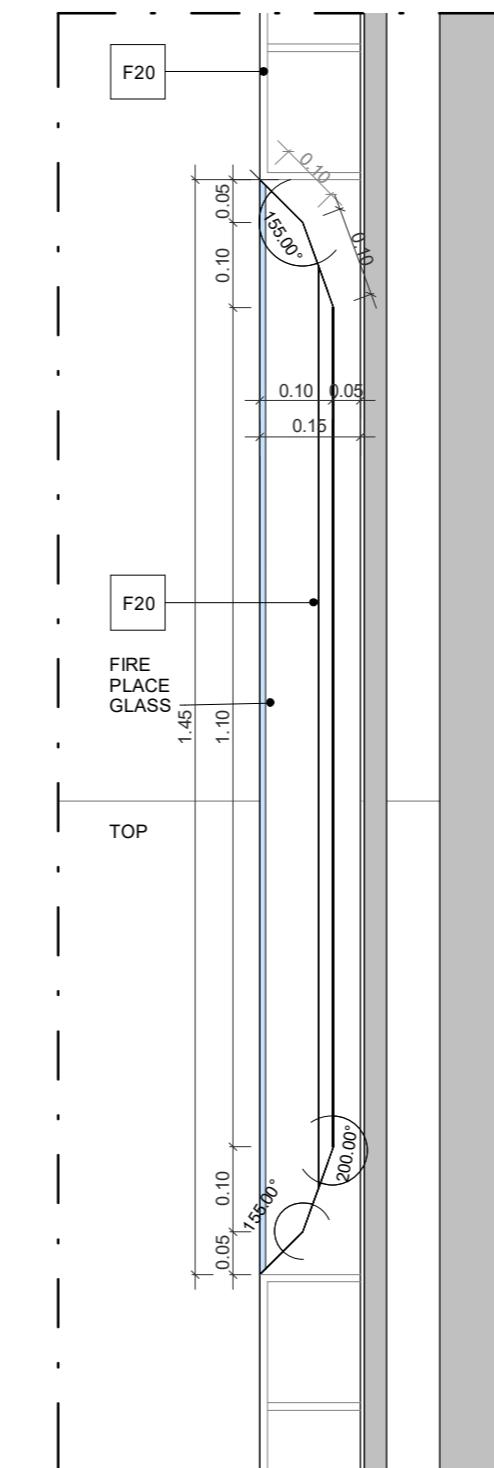

④ LIVING ROOM -PLAN DETAIL
1 : 10



AL-BOUCA'I

ENGINEERING CONSULTING BUREAU

مکتب البقاعی
للاستشارات الهندسية



BIM Lab
Engineering Services

PROJECT NAME

NOTES

**FOR FINISHES REFER TO SHEETS:
ID-6000
ID-6001**

ROOM NAME

FLOOR FINISH | CEILING FINISH

FINISHES	
FINISH TAG	COMMENTS
F01	
F02	
F03	GOLD STONE
F04	DARK WOOD
F05	DARK WOOD
F06	WOOD
F07	BLACK MARBLE
F08	BEIGE MARBLE
F09	GREY STONE
F10	WALL PAPER
F11	
F12	
F13	BLACK PAINT
FINISHES	
FINISH TAG	COMMENTS
F16	
F17	LEATHER
F18	PAINT-GOLD METAL EFFECT
F19	
F20	GREY STONE
F21	CONCRETE FINISH
F22	
F23	SWIMMING POOL WALL FINISHES

-  SPOT RECESSED LIGHT
-  PENDANT LIGHT
-  HIDDEN LIGHT
-  CHANDELIER
-  WALL MOUNTED
-  NEON RECTANGULAR


Project Type	Residential
Owner	Khalid Khadir Hasan AL-Saeed
Location	Amman
Plot No.	1659
Basin No.	19
Designed by	A.Shaker Khulief 4809

SHEET NAME


FIRST FLOOR BATHROOM 1

ID-4210


Date	08/10/2011
Scale	As indicated

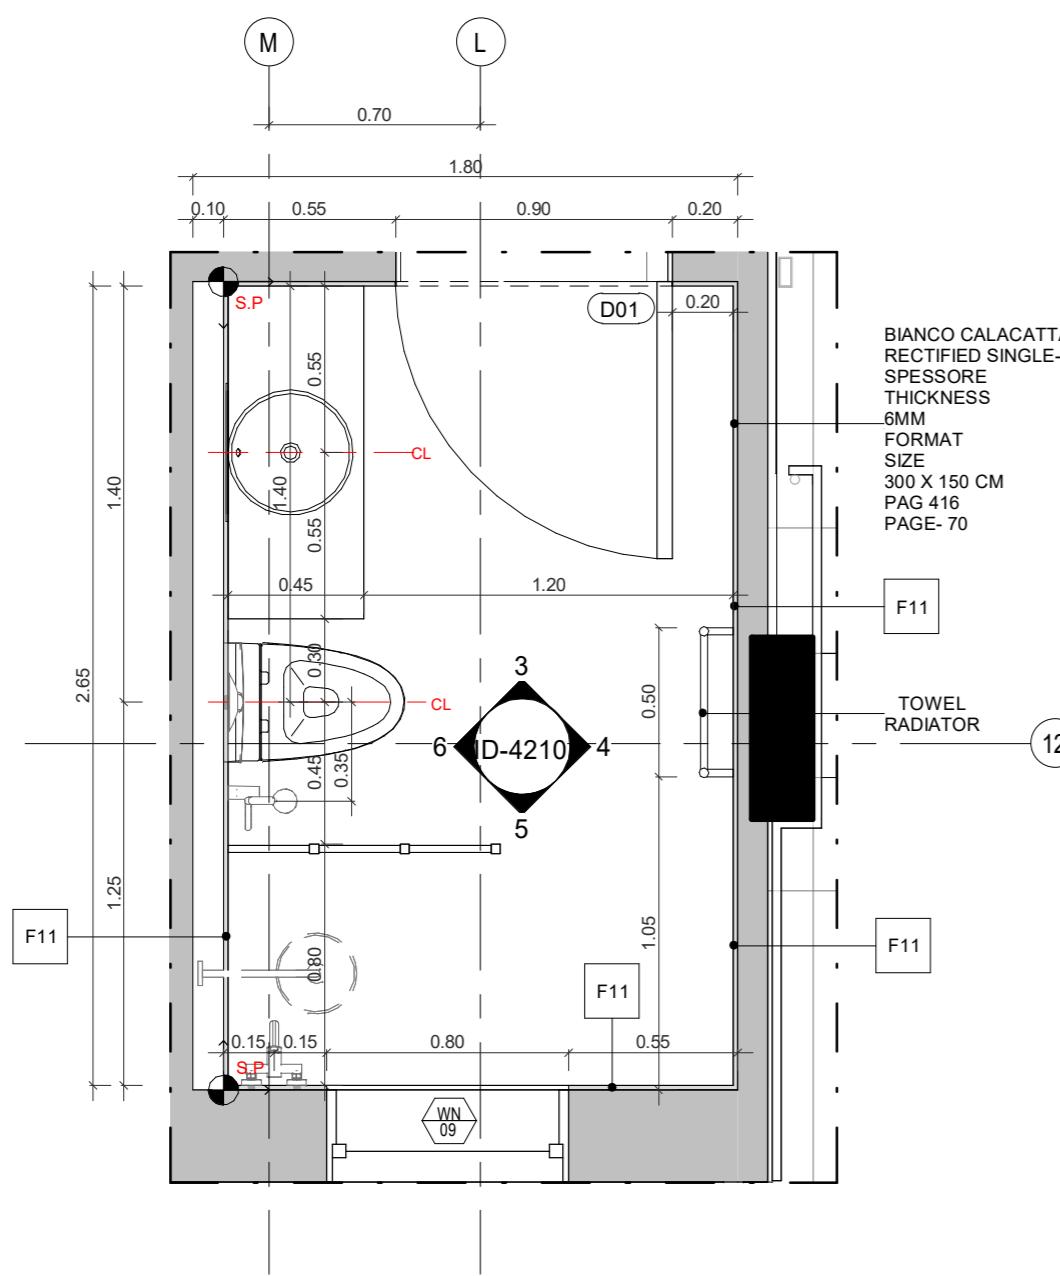


1 TILING PLAN-BATHROOM 1
1 : 25

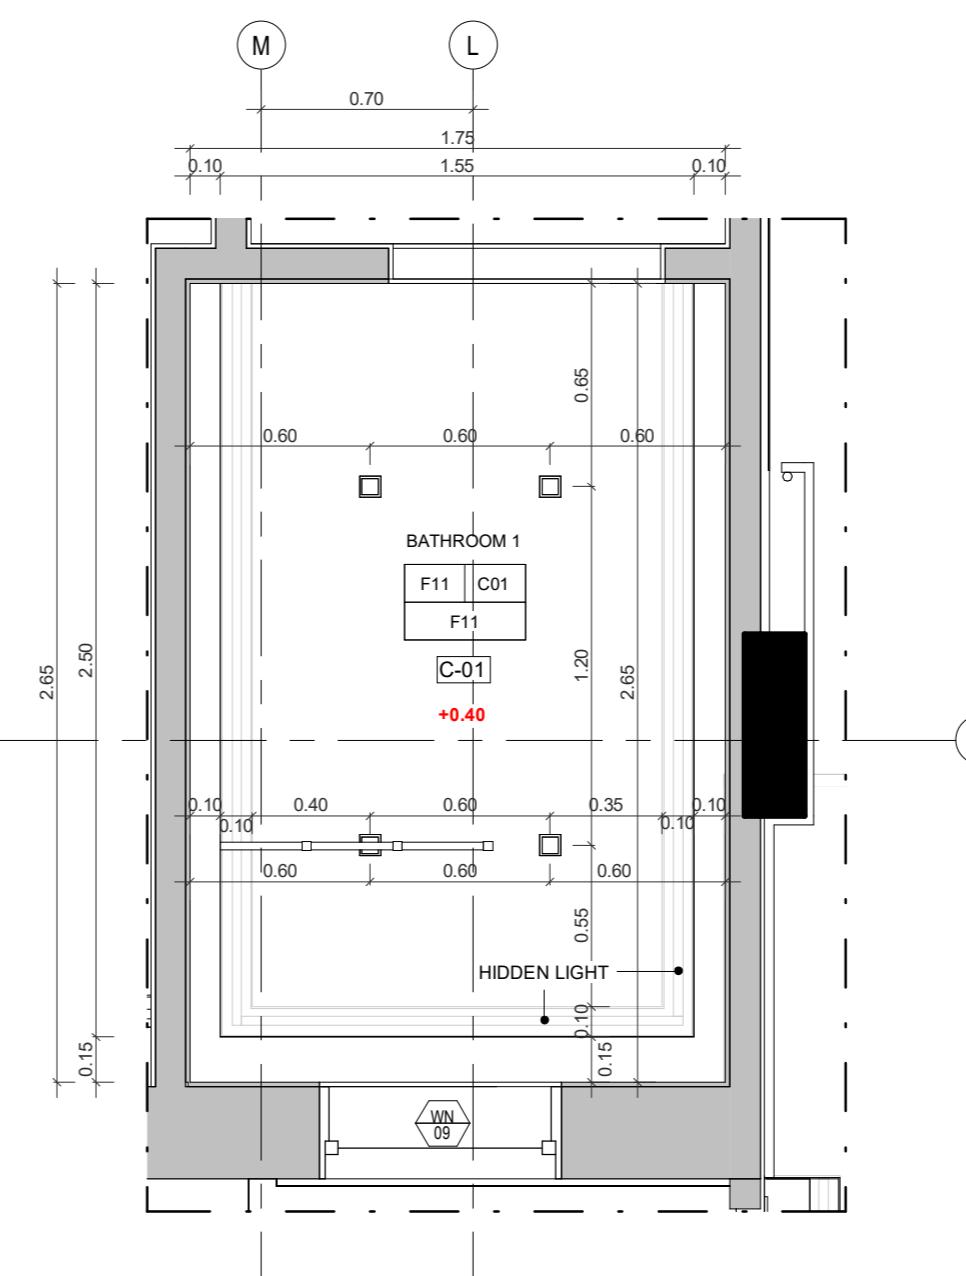

2 CEILING PLAN-BATHROOM 1
1 : 25

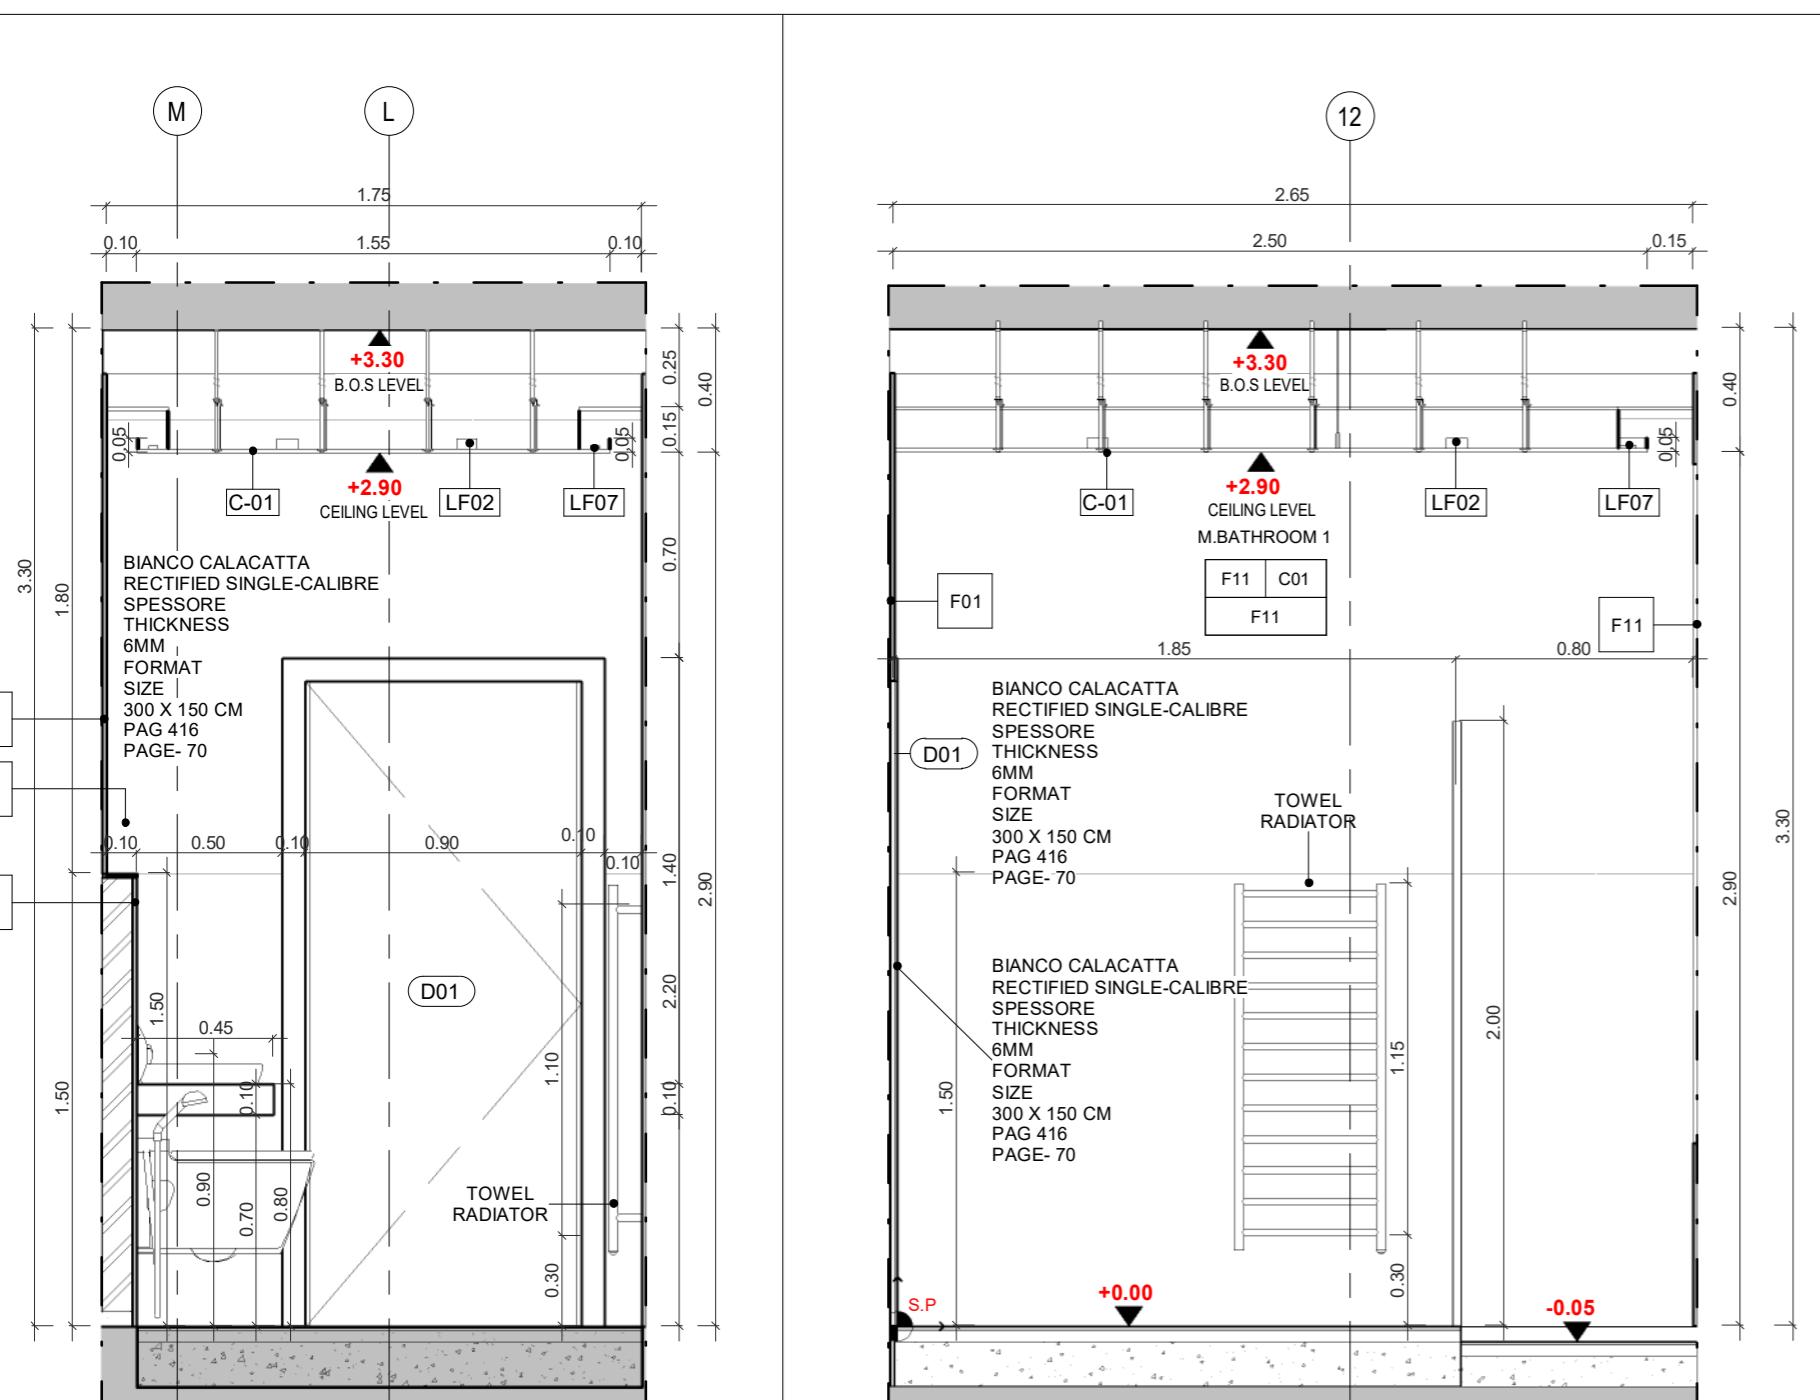

3 BATHROOM 1-ELEVATION 01
1 : 25

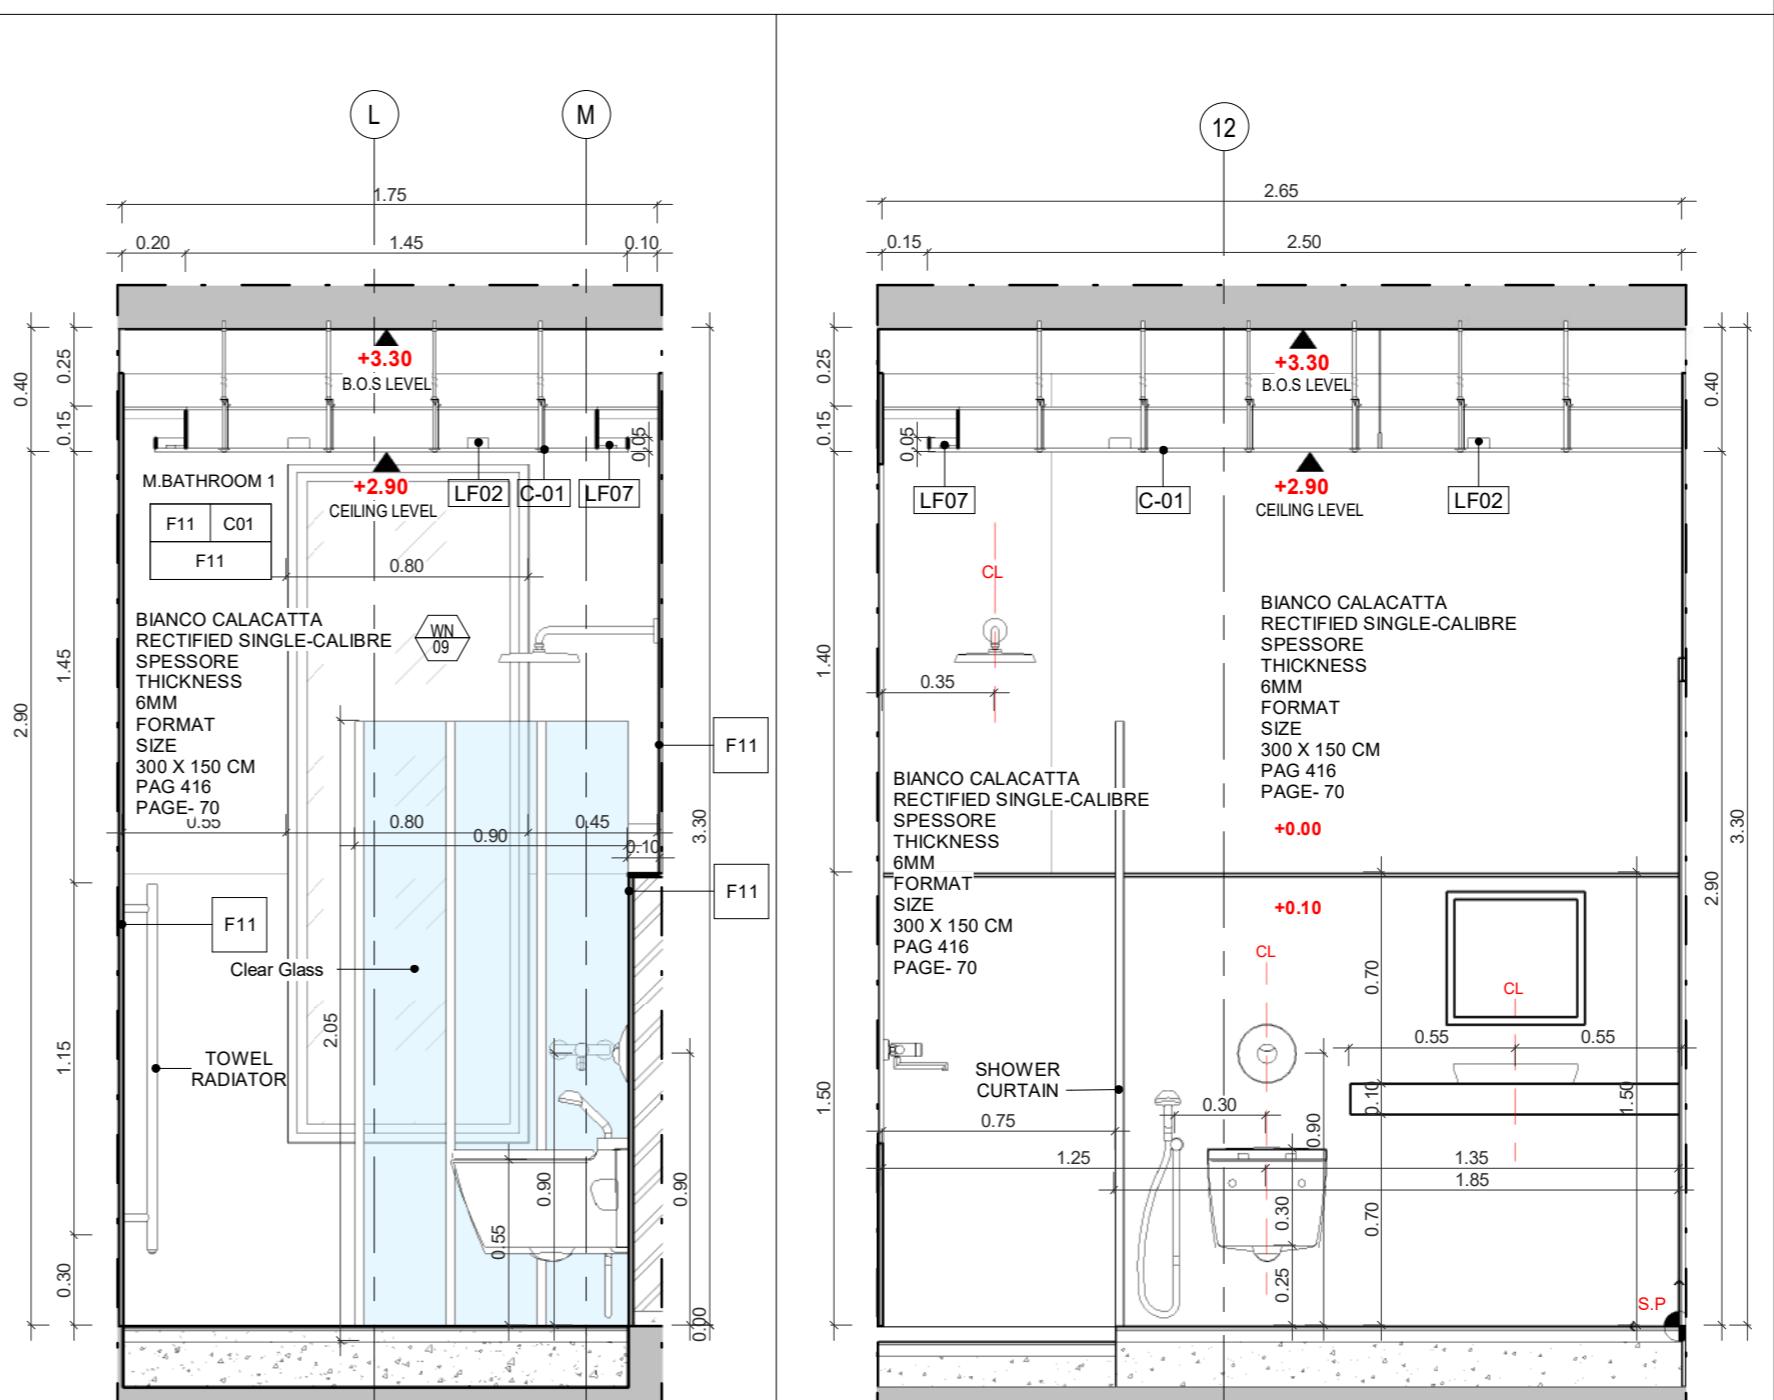

5 BATHROOM 1-ELEVATION 03
1 : 25





BIM Lab
Engineering Services

PROJECT NAME

NOTES

FOR FINISHES REFER TO SHEETS:
D-6000
D-6001

ROOM NAME

FLOOR FINISH	CEILING FINISH
--------------	----------------

FINISHES	
FINISH TAG	COMMENTS
F01	
F02	
F03	GOLD STONE
F04	DARK WOOD
F05	DARK WOOD
F06	WOOD
F07	BLACK MARBLE
F08	BEIGE MARBLE
F09	GREY STONE
F10	WALL PAPER
F11	
F12	
F13	BLACK PAINT
F14	CALACATTA
FINISHES	
FINISH TAG	COMMENTS
F16	
F17	LEATHER
F18	PAINT-GOLD METAL EFFECT
F19	
F20	GREY STONE
F21	CONCRETE FINISH
F22	
F23	SWIMMING POOL WALL FINISHES


- SPOT RECESSED LIGHT
- PENDANT LIGHT
- HIDDEN LIGHT
- CHANDELIER
- WALL MOUNTED
- NEON RECTANGULAR

Project Type	Residential
Owner	Khalid Khadir Hasan AL-Saeed
Location	Amman
Plot No.	1659
Basin No.	19
Designed by	A.Shaker Khulief 4809

FIRST FLOOR BATHROOM 2


ID-4220

Date 08/10/2019
Scale As indicated

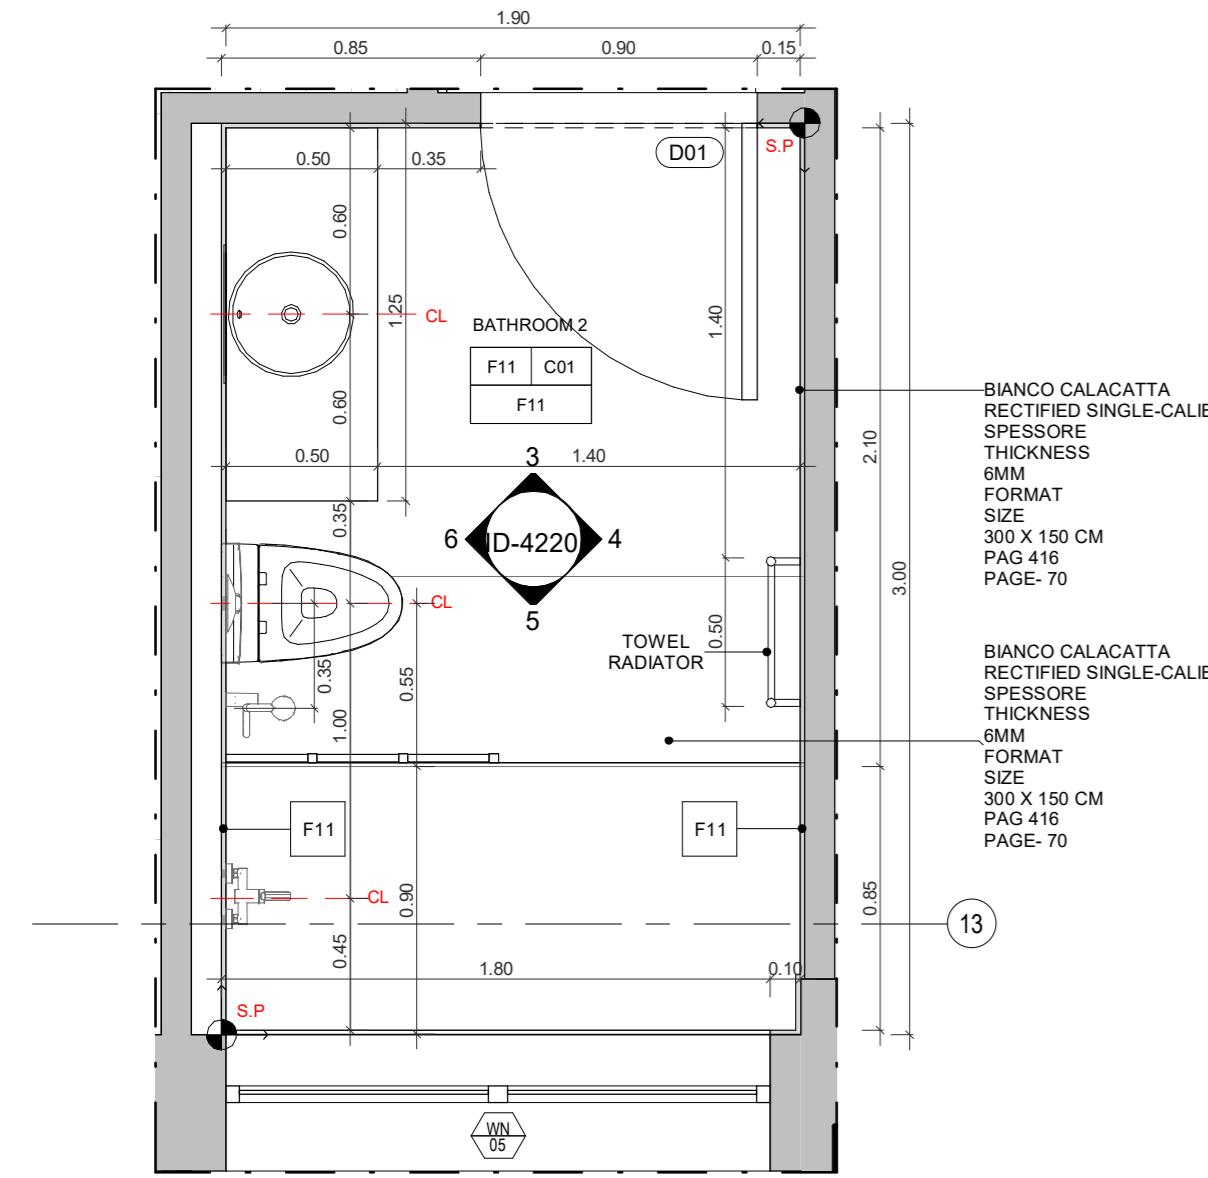


2 TILING PLAN-BATHROOM 2
1 - 25

1 : 25

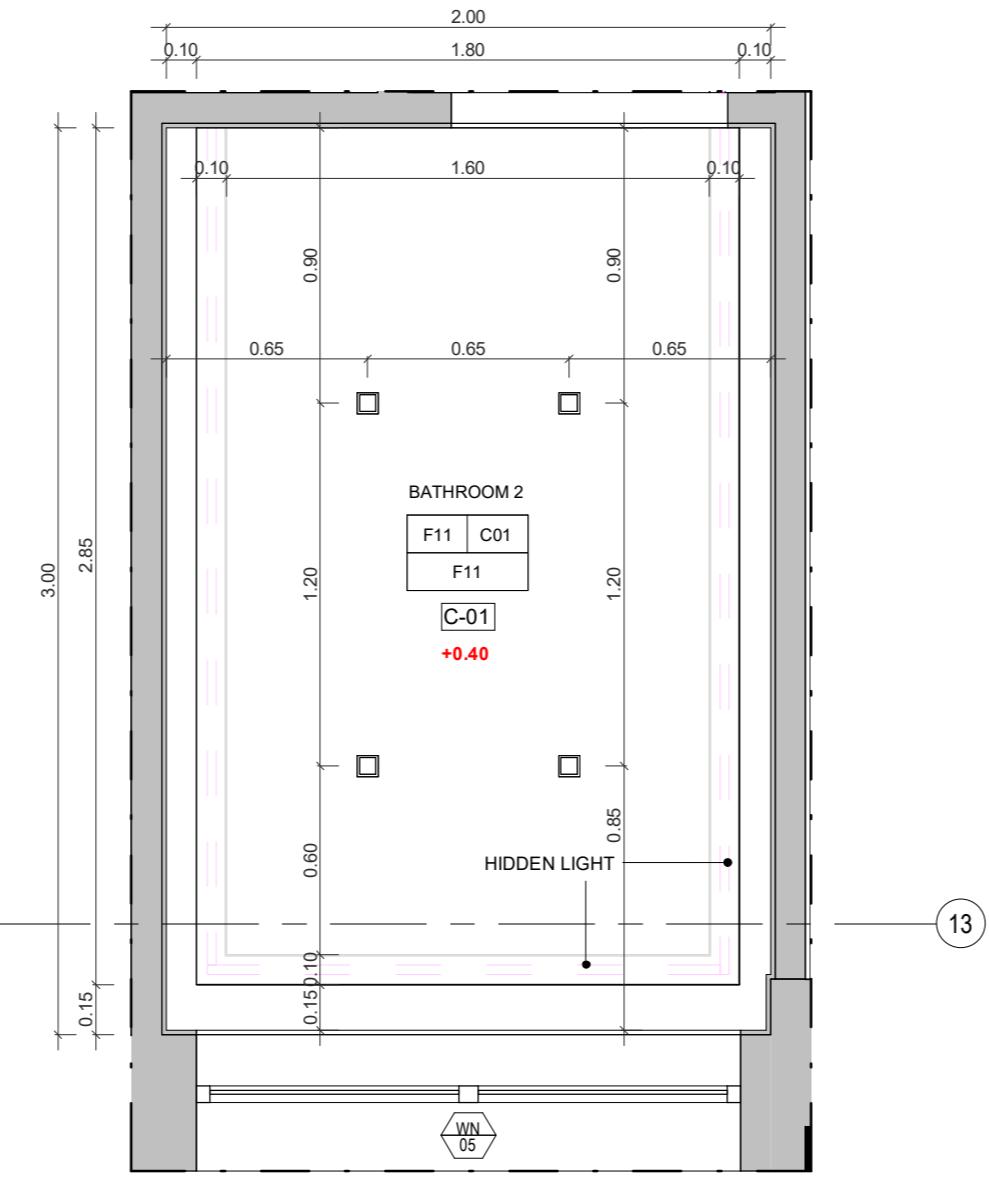


1 CEILING PLAN-BATHROOM 2
1 - 25

1 :

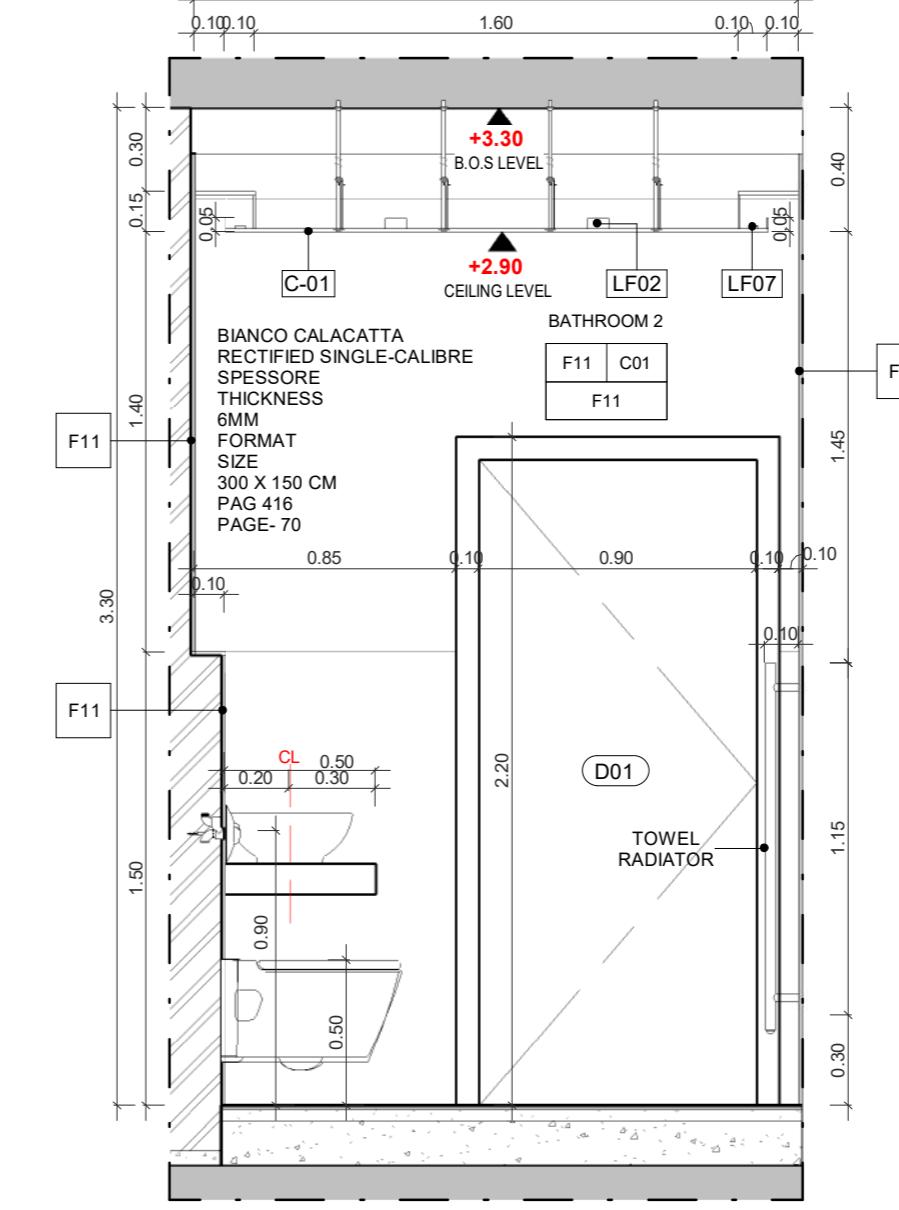


3 BATHROOM 2-ELEVATION 01
1 - 25

1 :

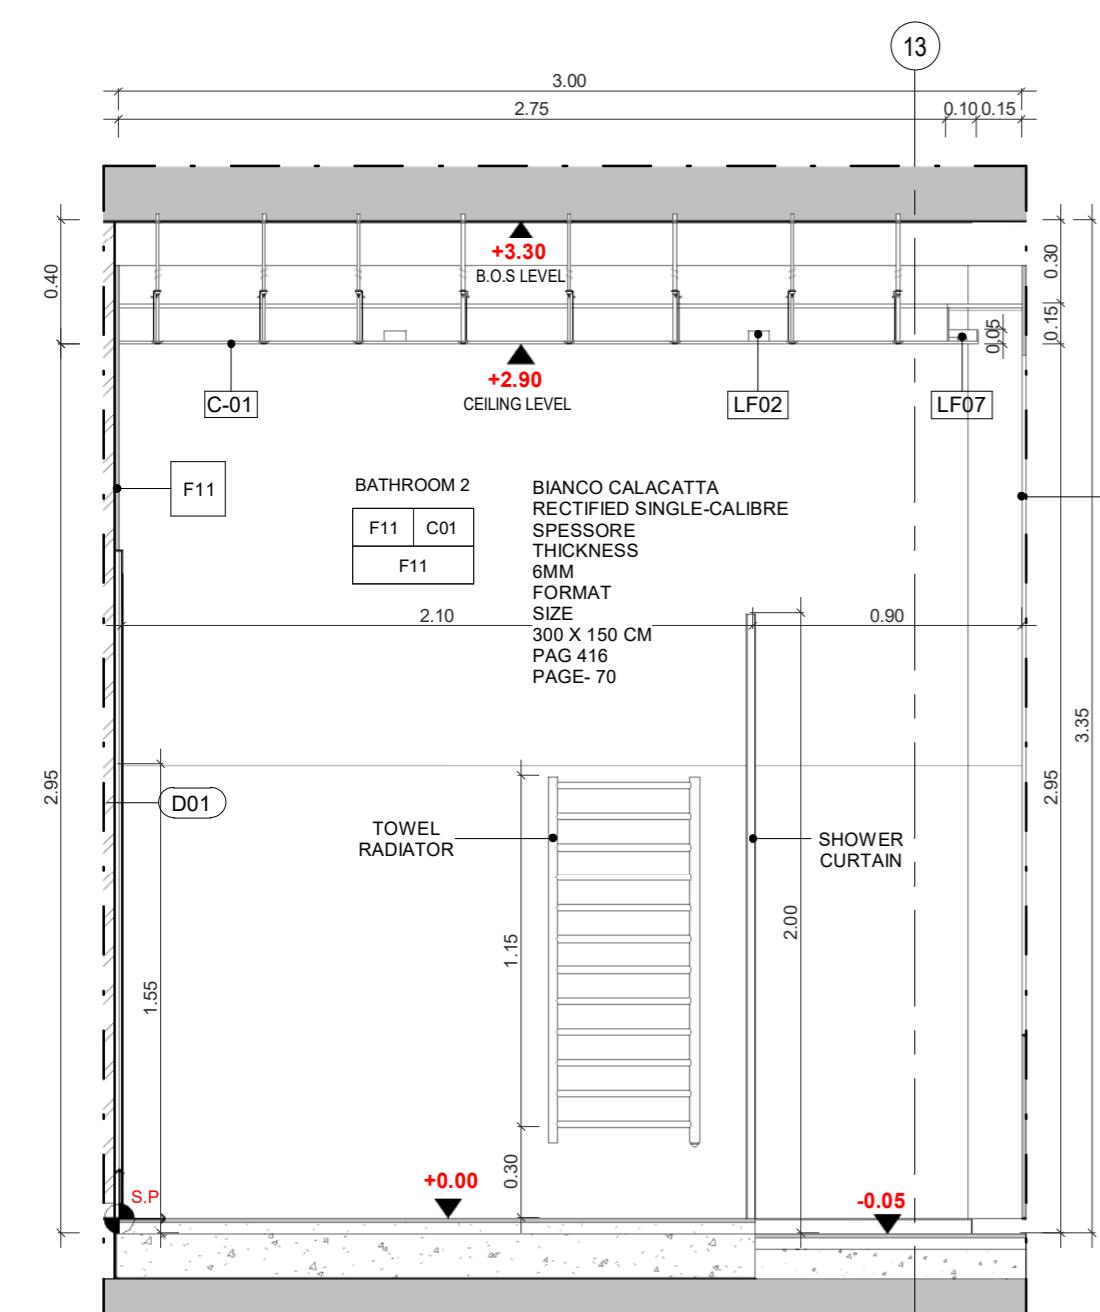


4 BATHROOM 2-ELEVATION 02
1 - 25

1 : 25

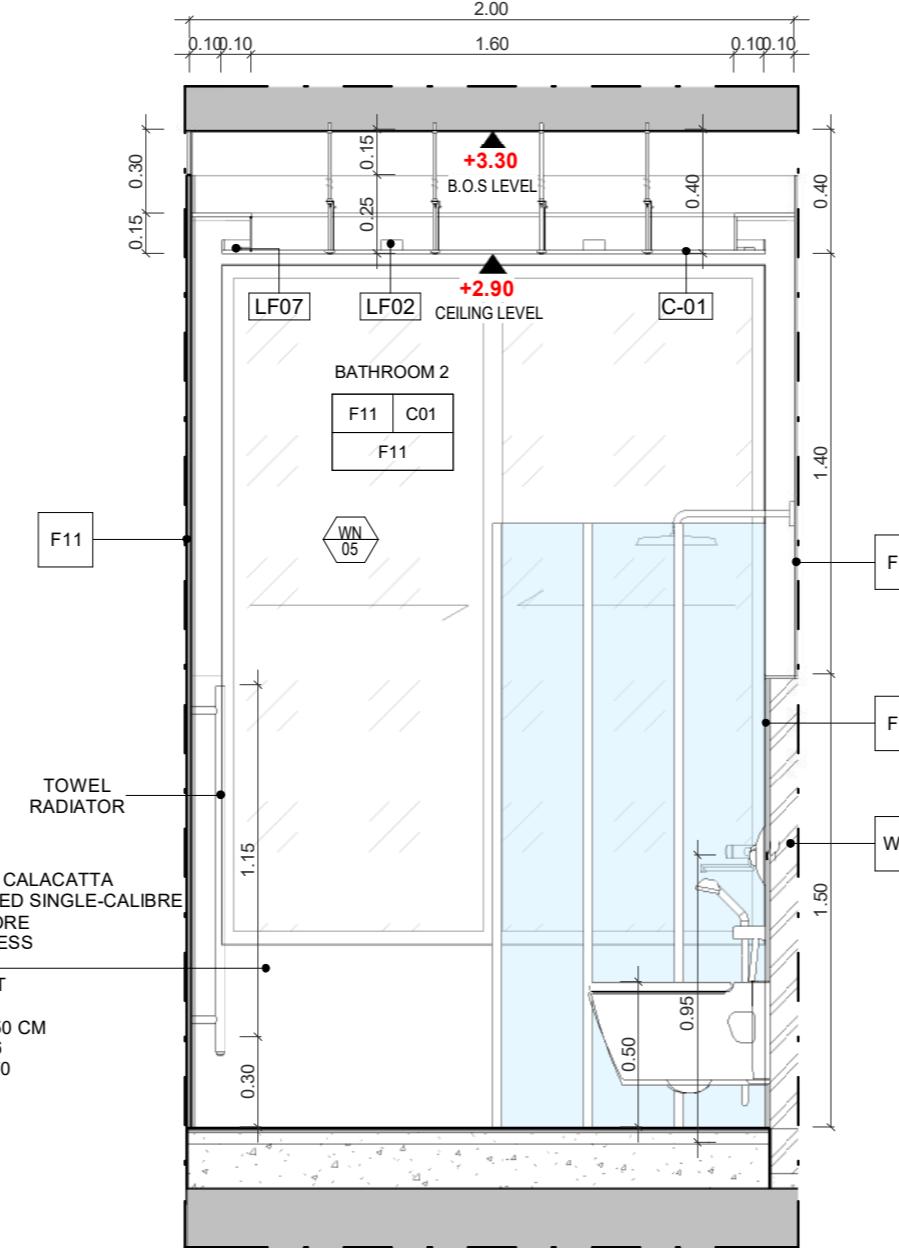

5 BATHROOM 2-ELEVATION 03
1 - 25

1 :

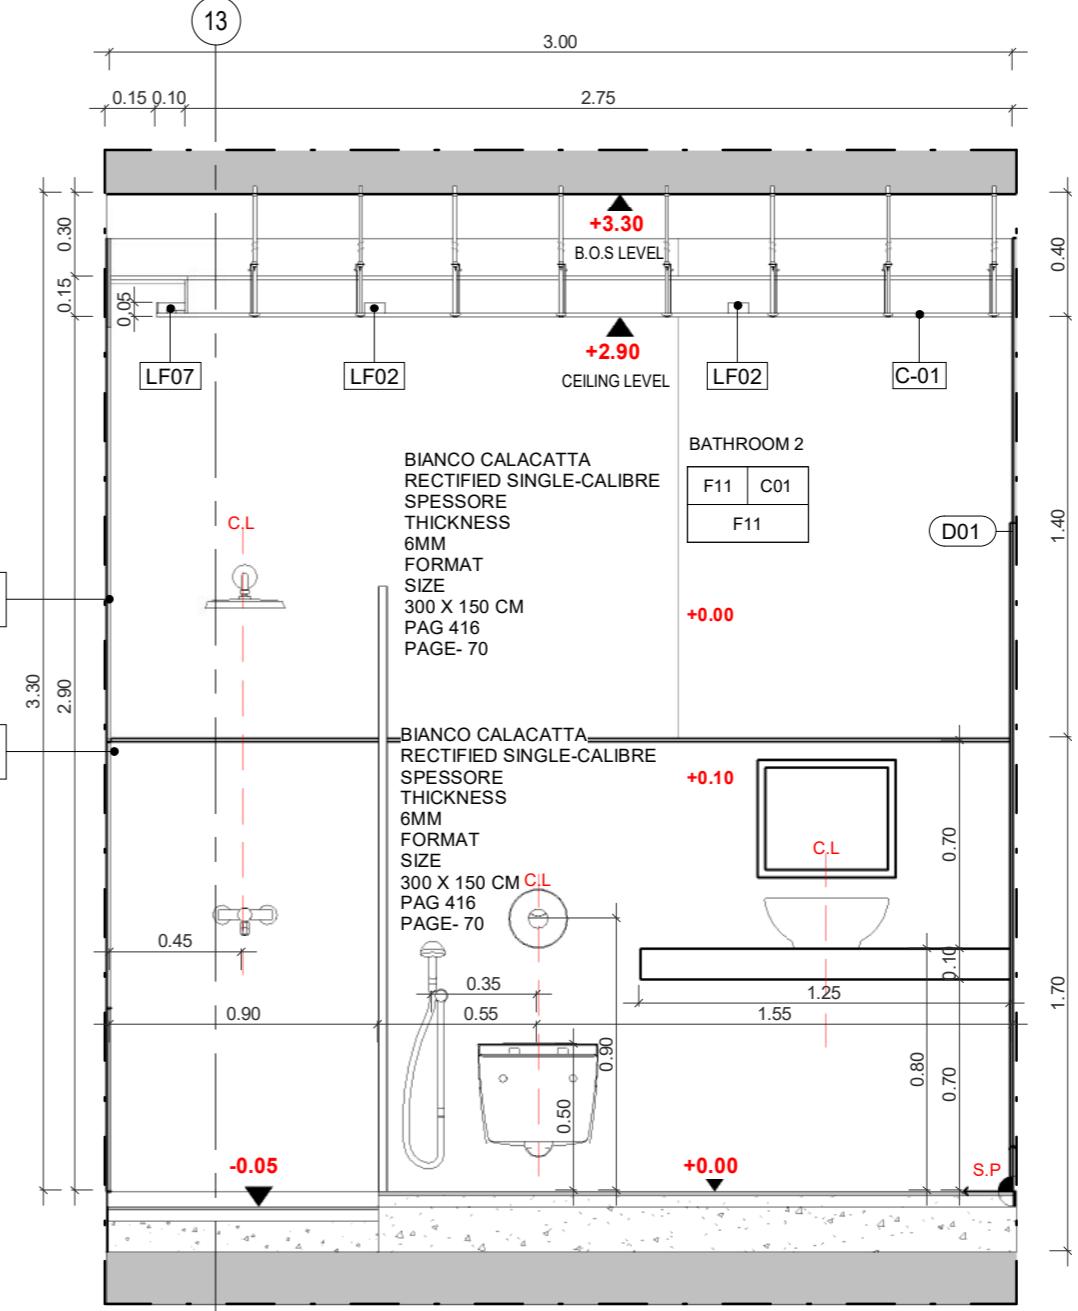

6 BATHROOM 2-ELEVATION 04
1 - 25

1





BIM Lab
Engineering Services

PROJECT NAME

APARTMENTS BUILDING

NOTES

FOR FINISHES REFER TO SHEETS:
ID-6000
ID-6001


ROOM NAME	
FLOOR FINISH	CEILING FINISH
WALL FINISH	
FINISHES	FINISHES
FINISH TAG	COMMENTS
F01	
F02	
F03	GOLD STONE
F04	DARK WOOD
F05	DARK WOOD
F06	WOOD
F07	BLACK MARBLE
F08	BEIGE MARBLE
F09	GREY STONE
F10	WALL PAPER
F11	
F12	
F13	BLACK PAINT
F14	CALACATTA
F15	BEIGE PAINT
	SPOT RECESSED LIGHT
	PENDANT LIGHT
	HIDDEN LIGHT
	CHANDELIER
	WALL MOUNTED
	NEON RECTANGULAR
Project Type	Residential
Owner	Khalid Khadir Hasan AL-Saeed
Location	Amman
Plot No.	1659
Basin No.	19
Designed by	A.Shaker Khulief 4809

SET NAME


FIRST FLOOR TOILET 1

ID-4230


Date	08/10/2011
Scale	As indicated

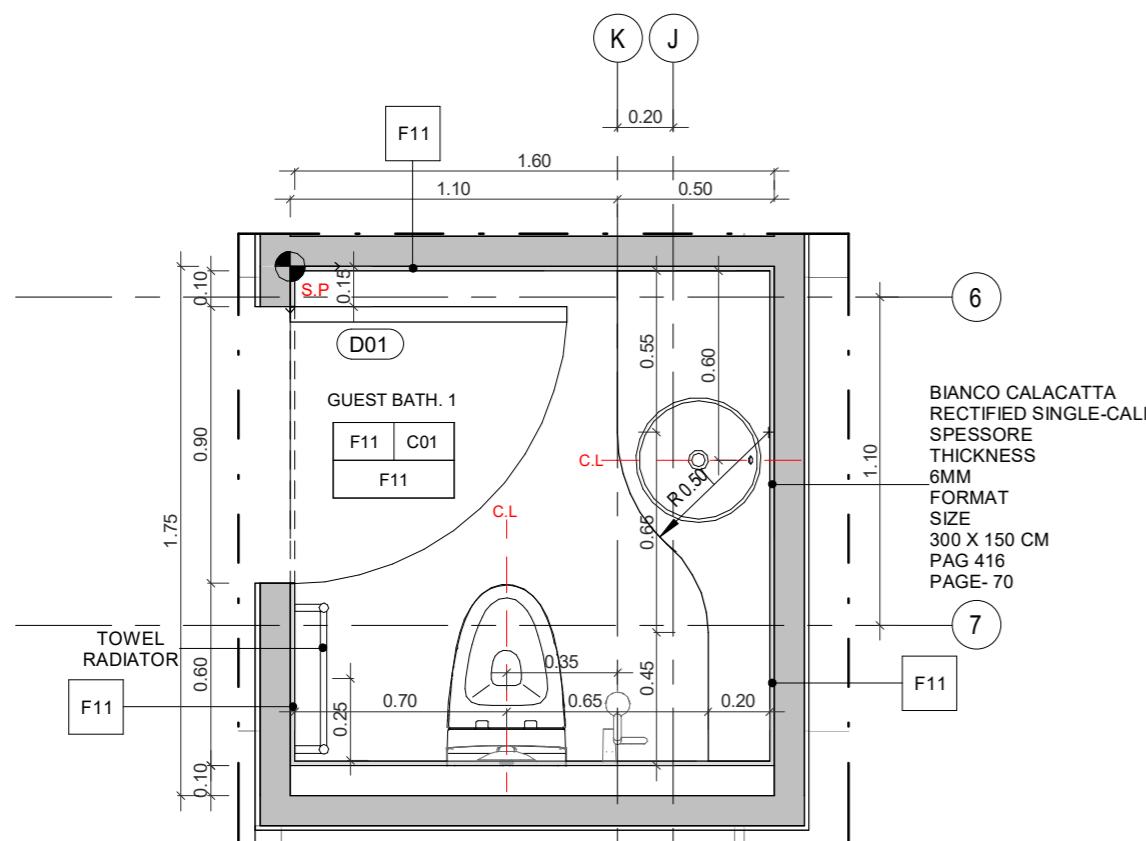


1 TILING PLAN-TOILET 1
1 : 25

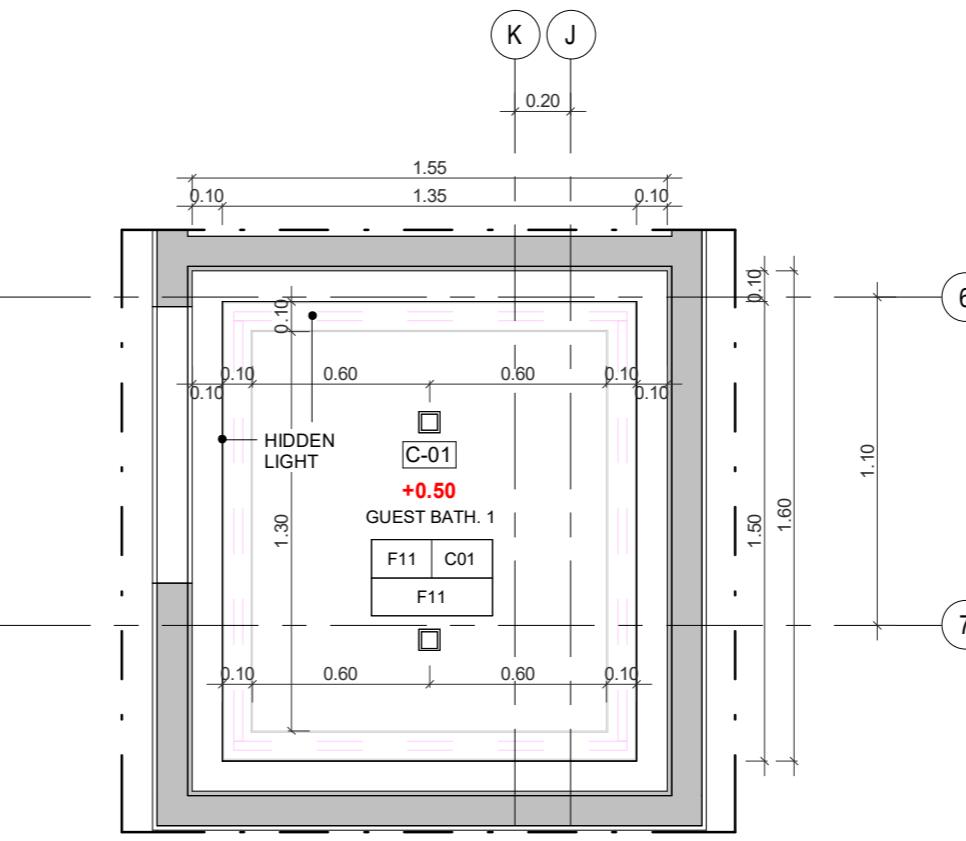


2 CEILING PLAN-TOILET 1
1 : 25

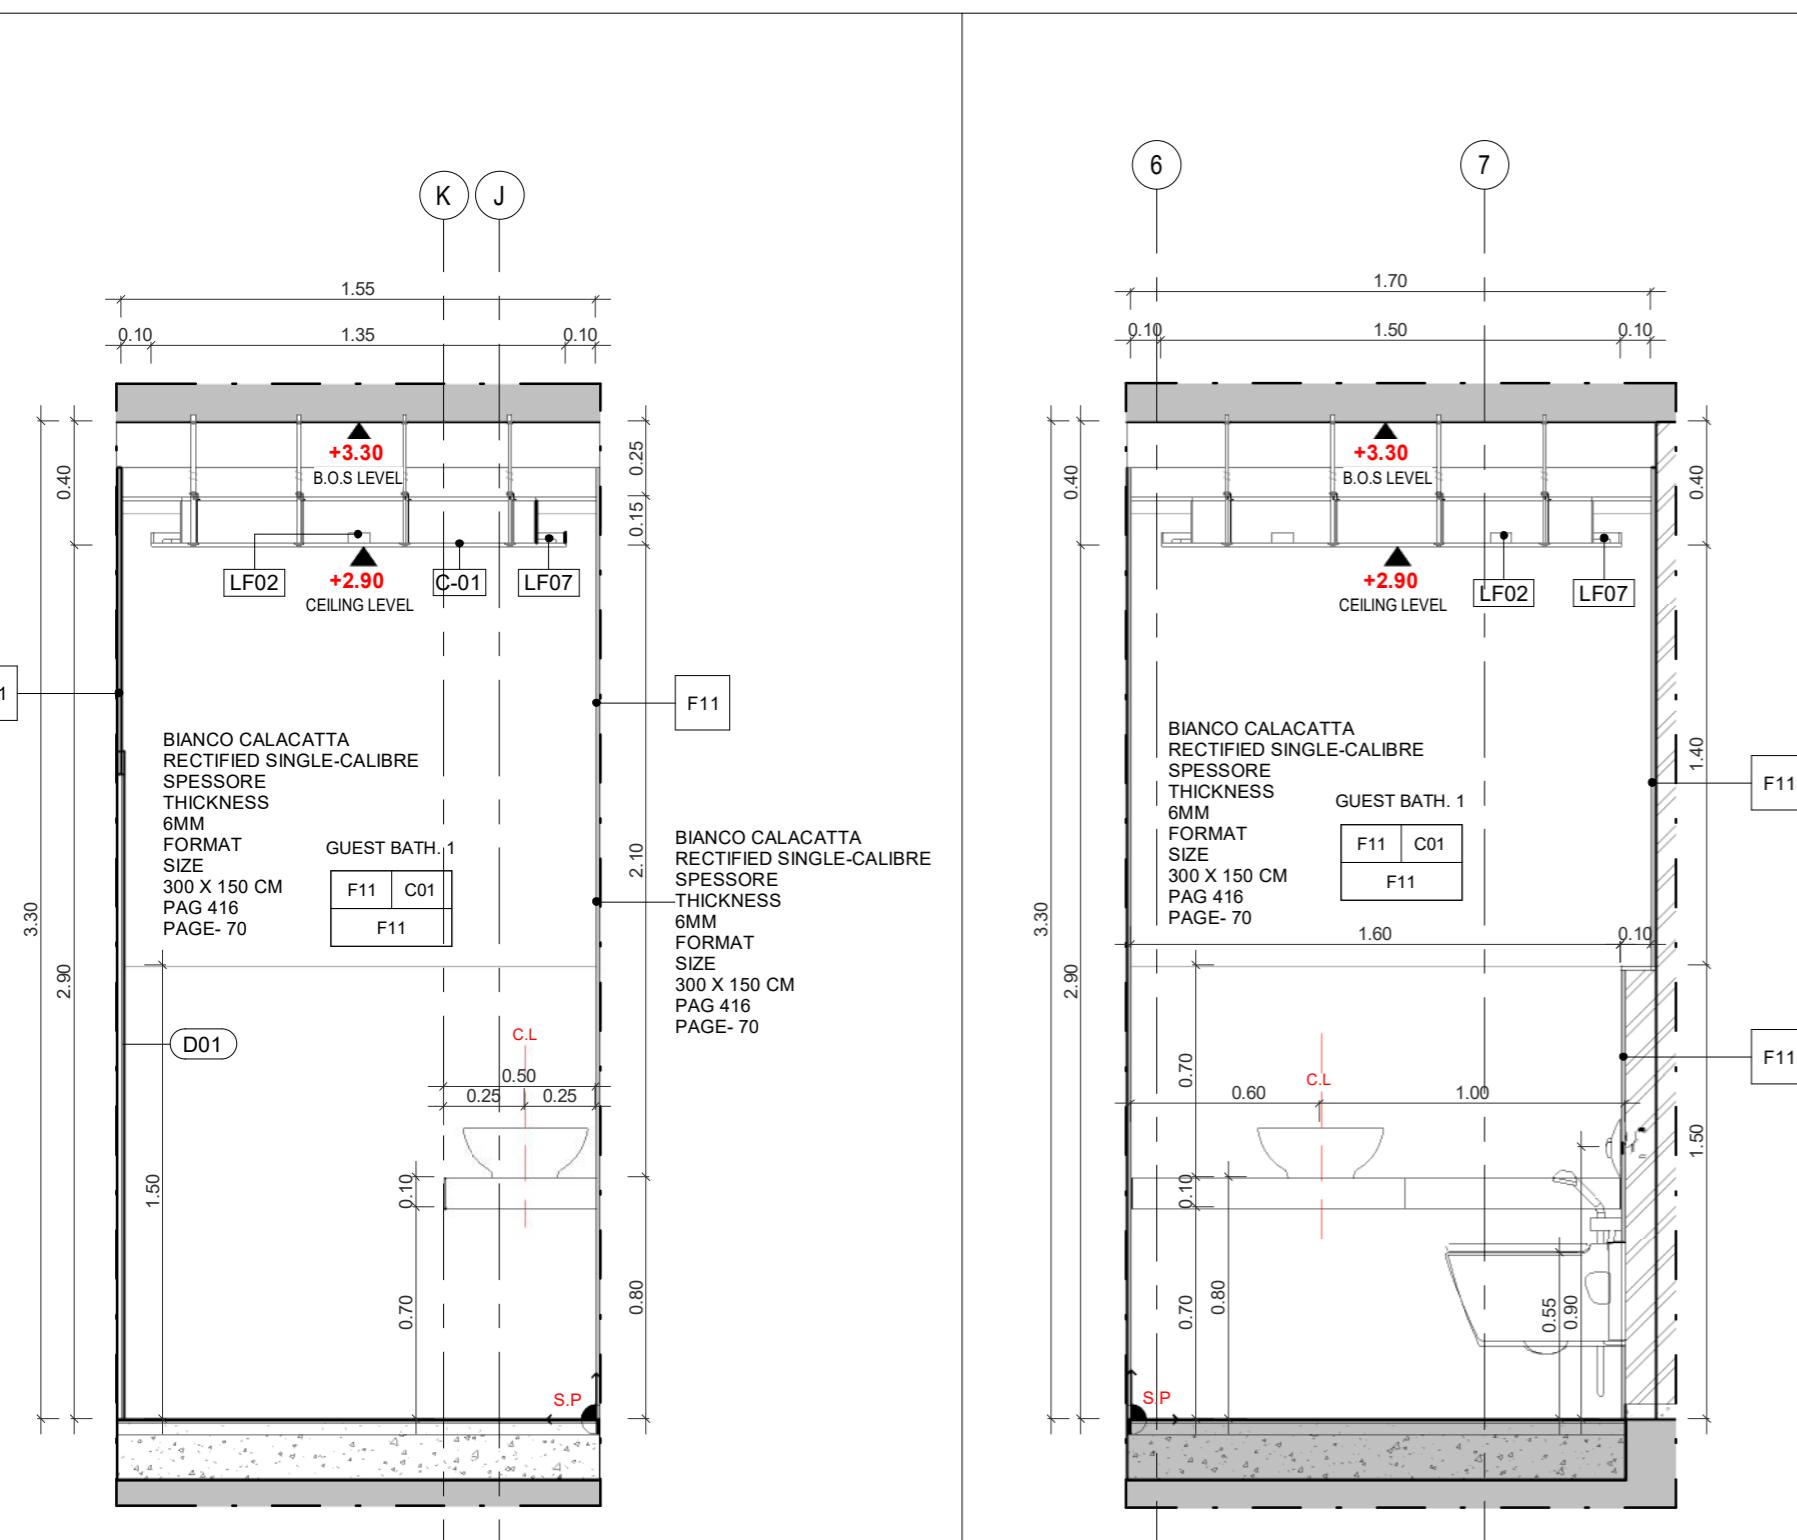

3 TOILET 1-ELEVATION 01
1 : 25

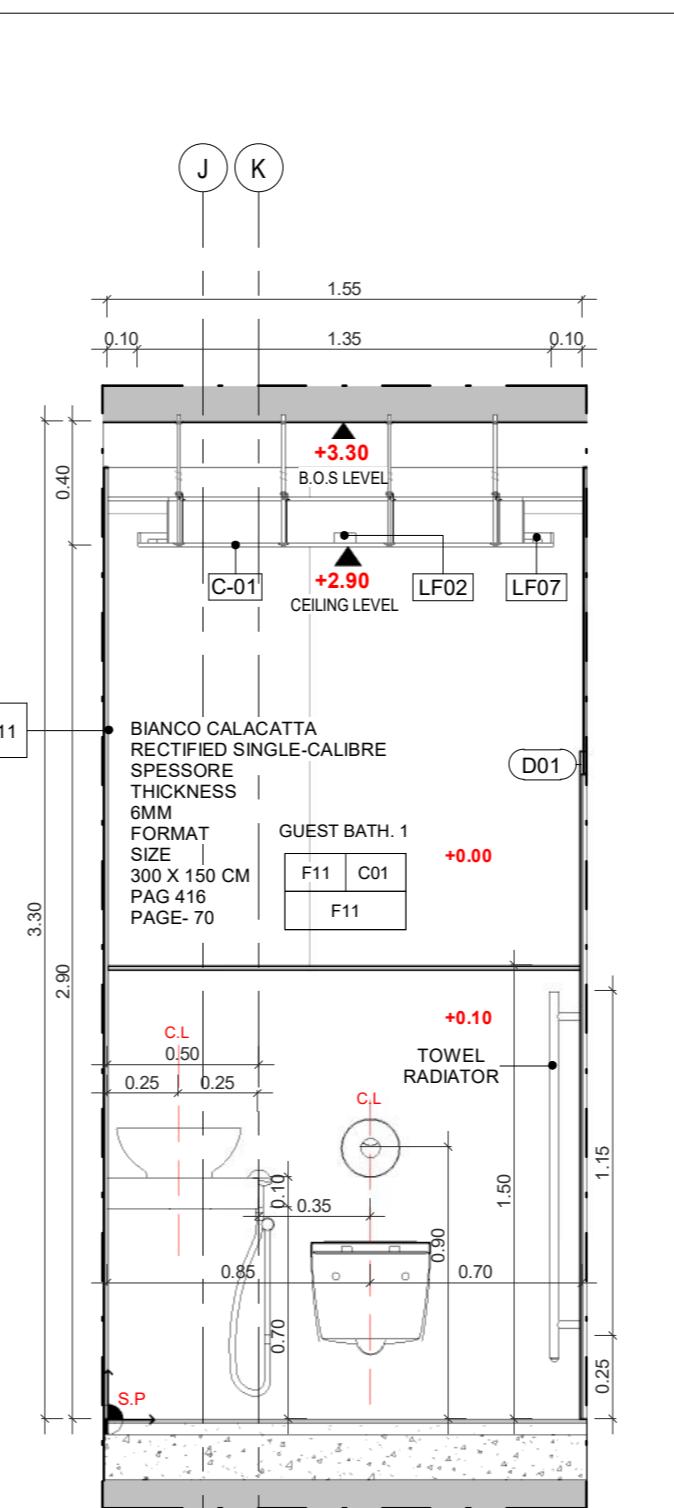

5 TOILET 1-ELEVATION 03
1 : 25

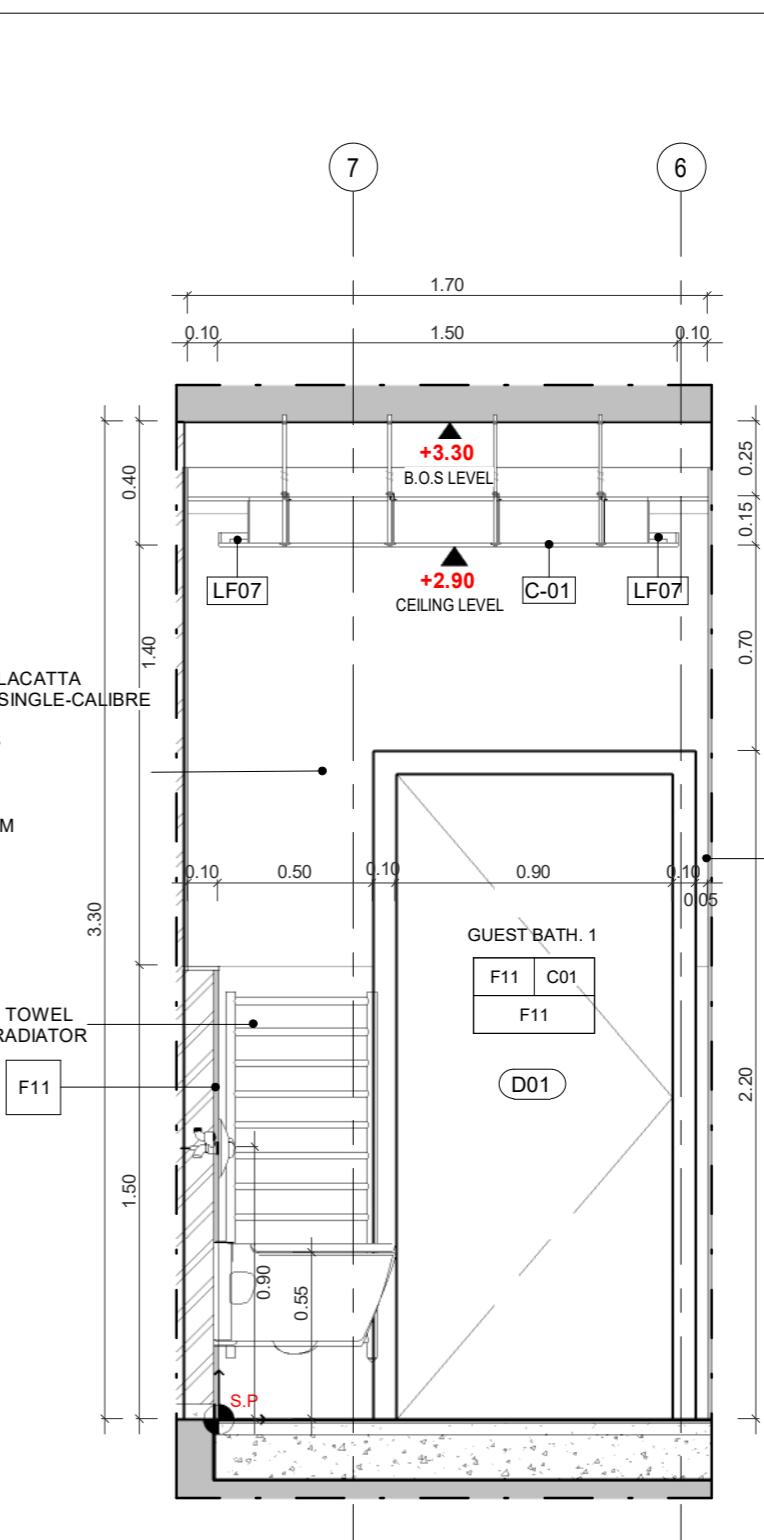

(6) TOILET 1-ELEVATION 04
1 : 25

PROJECT NAME

APARTMENTS BUILDING

NOTES

FOR FINISHES REFER TO SHEETS:
ID-6000
ID-6001

ROOM NAME

FLOOR FINISH	CEILING FINISH
--------------	----------------

WALL FINISH

FINISHES	
FINISH TAG	COMMENTS
F01	
F16	
F02	
F17	LEATHER
F03	GOLD STONE
F04	DARK WOOD
F05	DARK WOOD
F06	WOOD
F07	BLACK MARBLE
F08	BEIGE MARBLE
F09	GREY STONE
F10	WALL PAPER
F11	
F12	
F13	BLACK PAINT
F14	CALACATTA
F15	BEIGE PAINT
FINISHES	
FINISH TAG	COMMENTS
F16	
F17	
F18	PAINT-GOLD METAL EFFECT
F19	
F20	GREY STONE
F21	CONCRETE FINISH
F22	
F23	SWIMMING POOL WALL FINISHES

SPOT RECESSED LIGHT
 PENDANT LIGHT
 HIDDEN LIGHT
 CHANDELIER
 WALL MOUNTED
 NEON RECTANGULAR

Project Type Residential

Owner Khalid Khadir Hasan AL-Saeed

Location Amman

Plot No. 1659

Basin No. 19

Designed by A.Shaker Khulief 4809







SHEET NAME

FIRST FLOOR TOILET 2

ID-4240

Date 08/10/2019

Scale As indicated

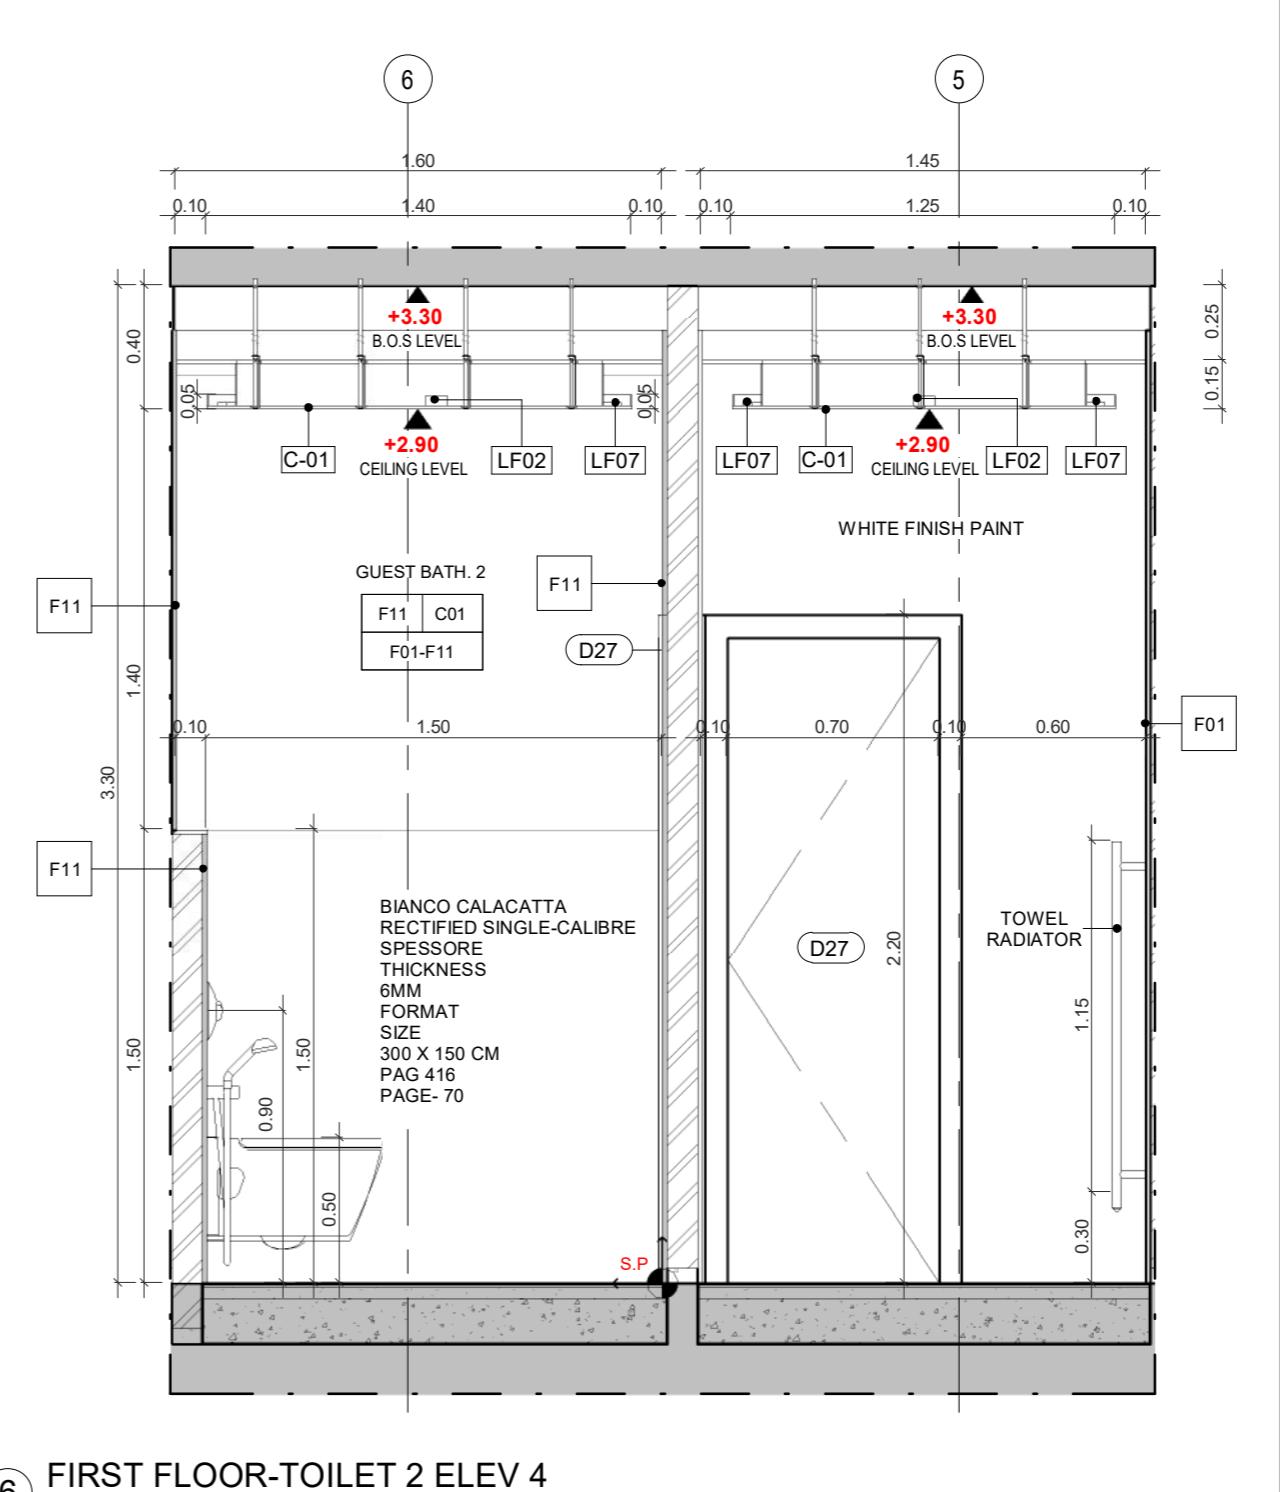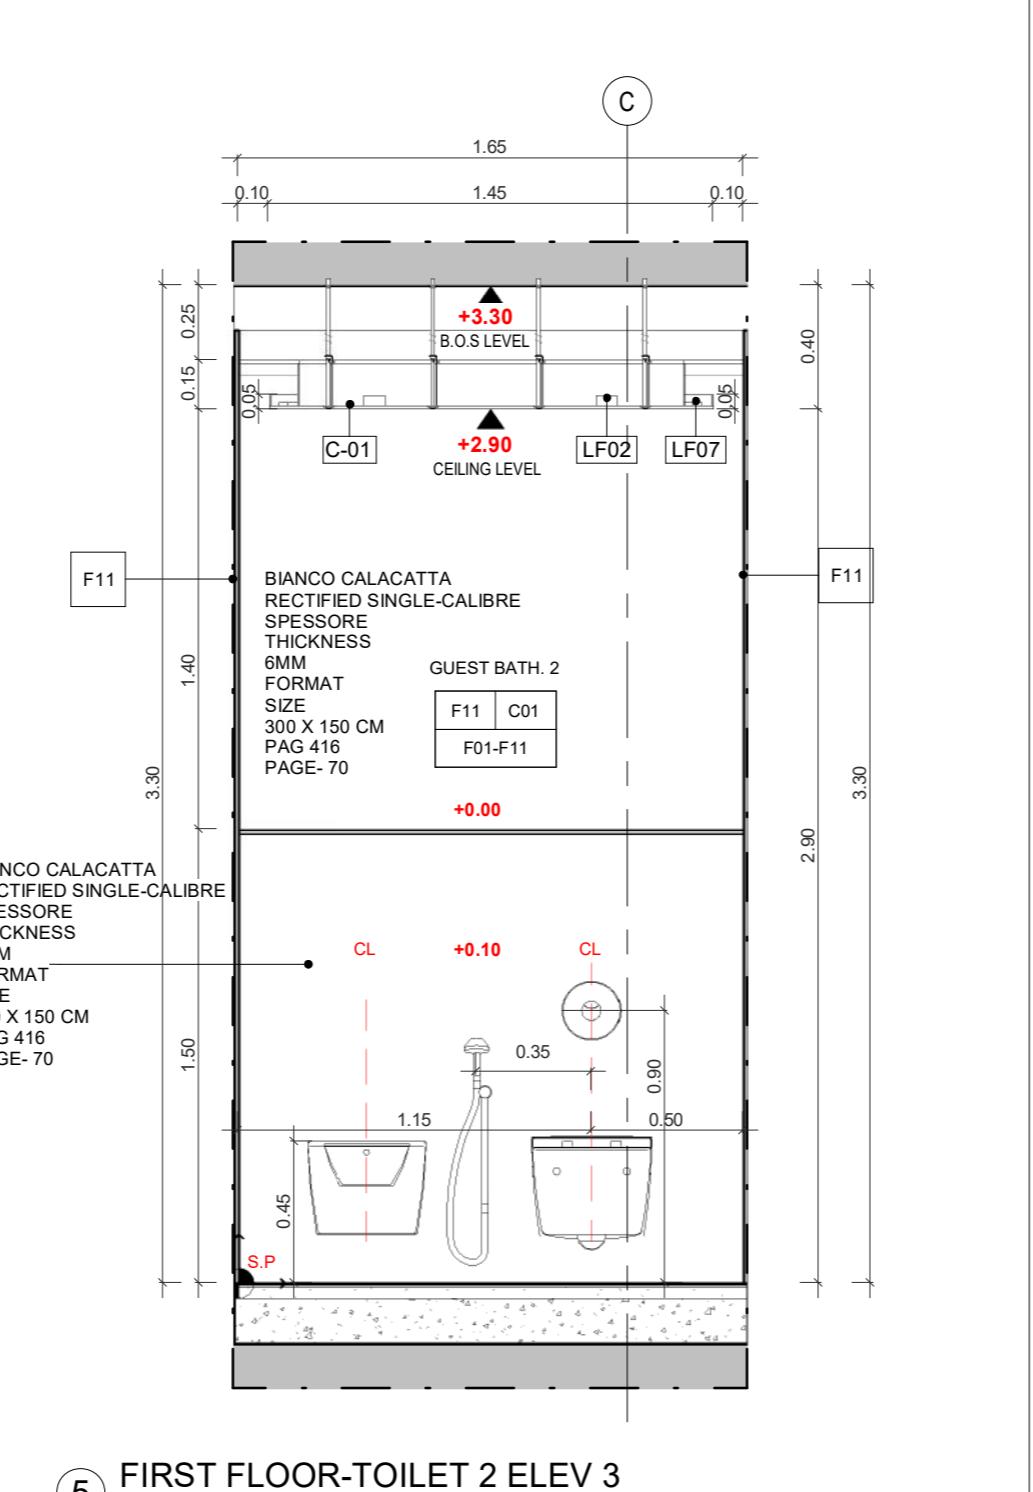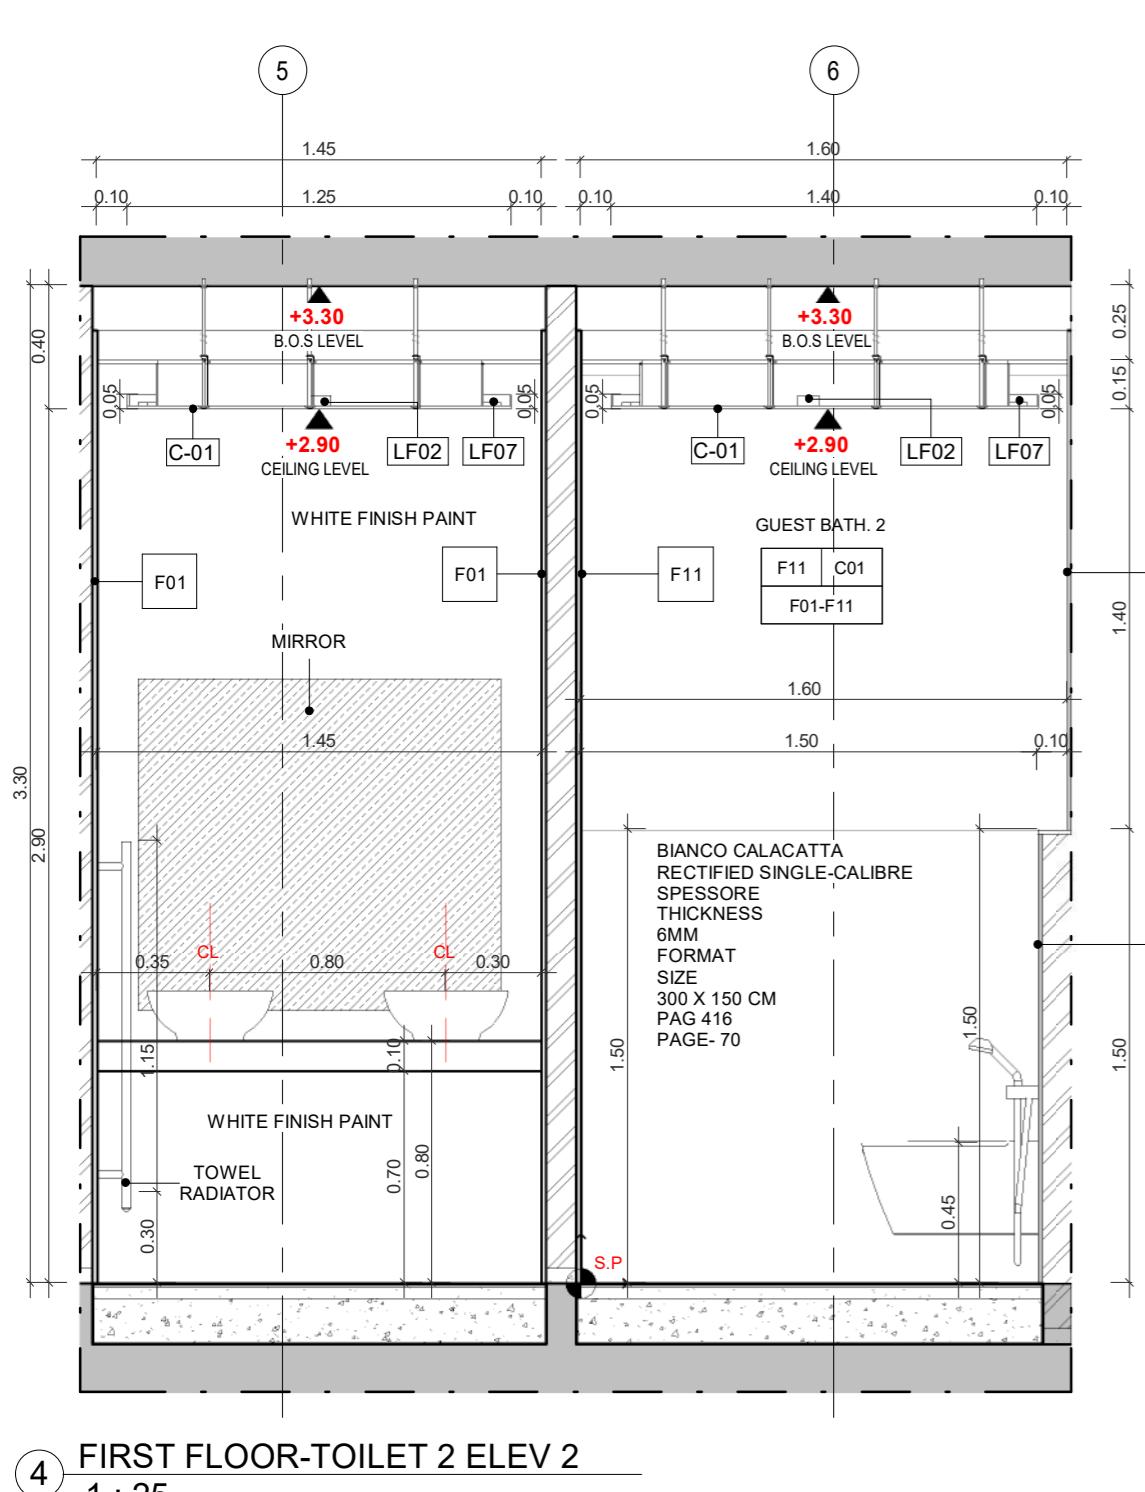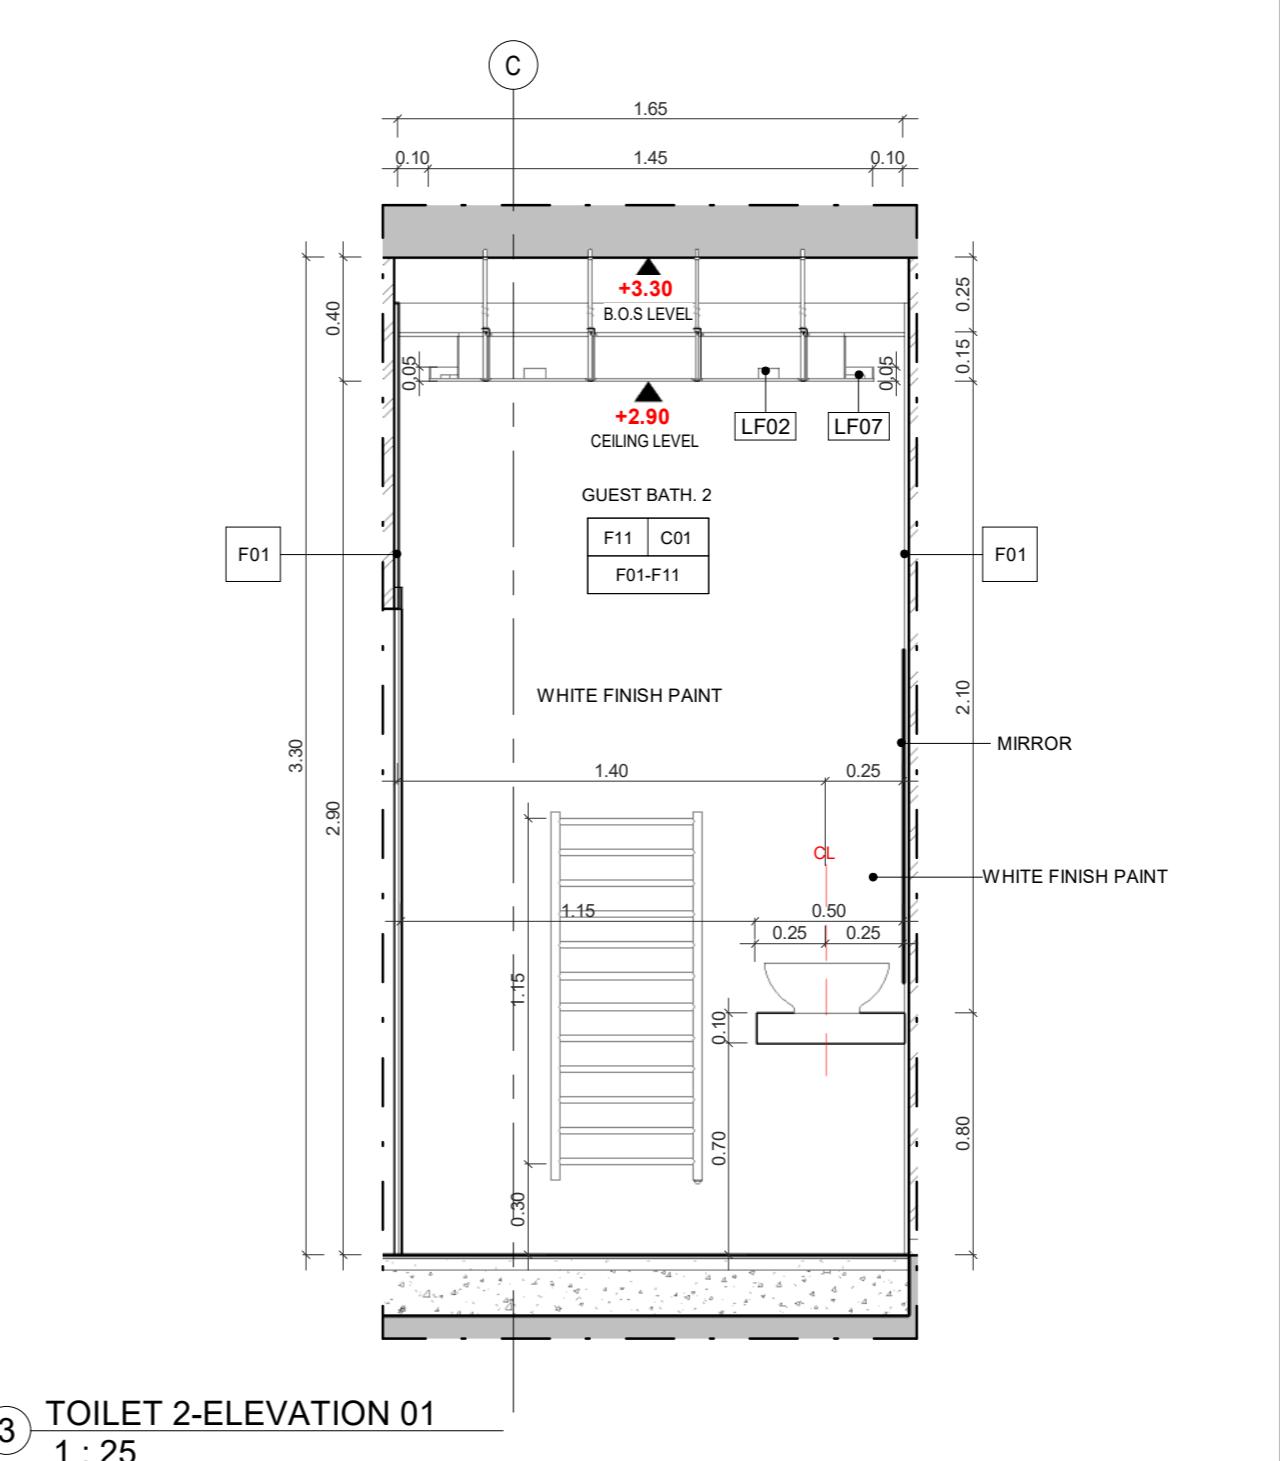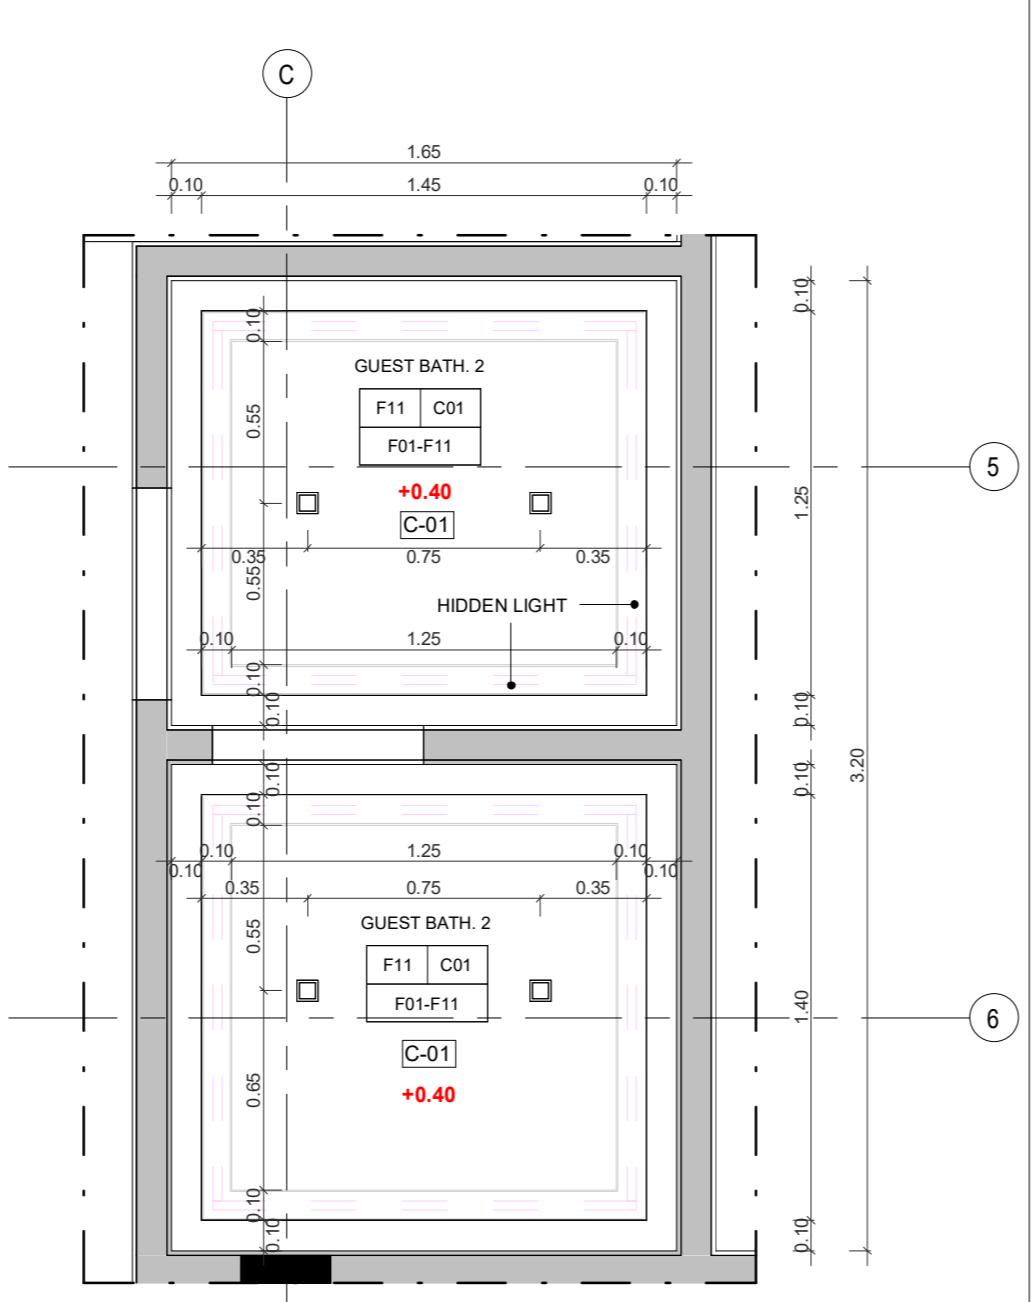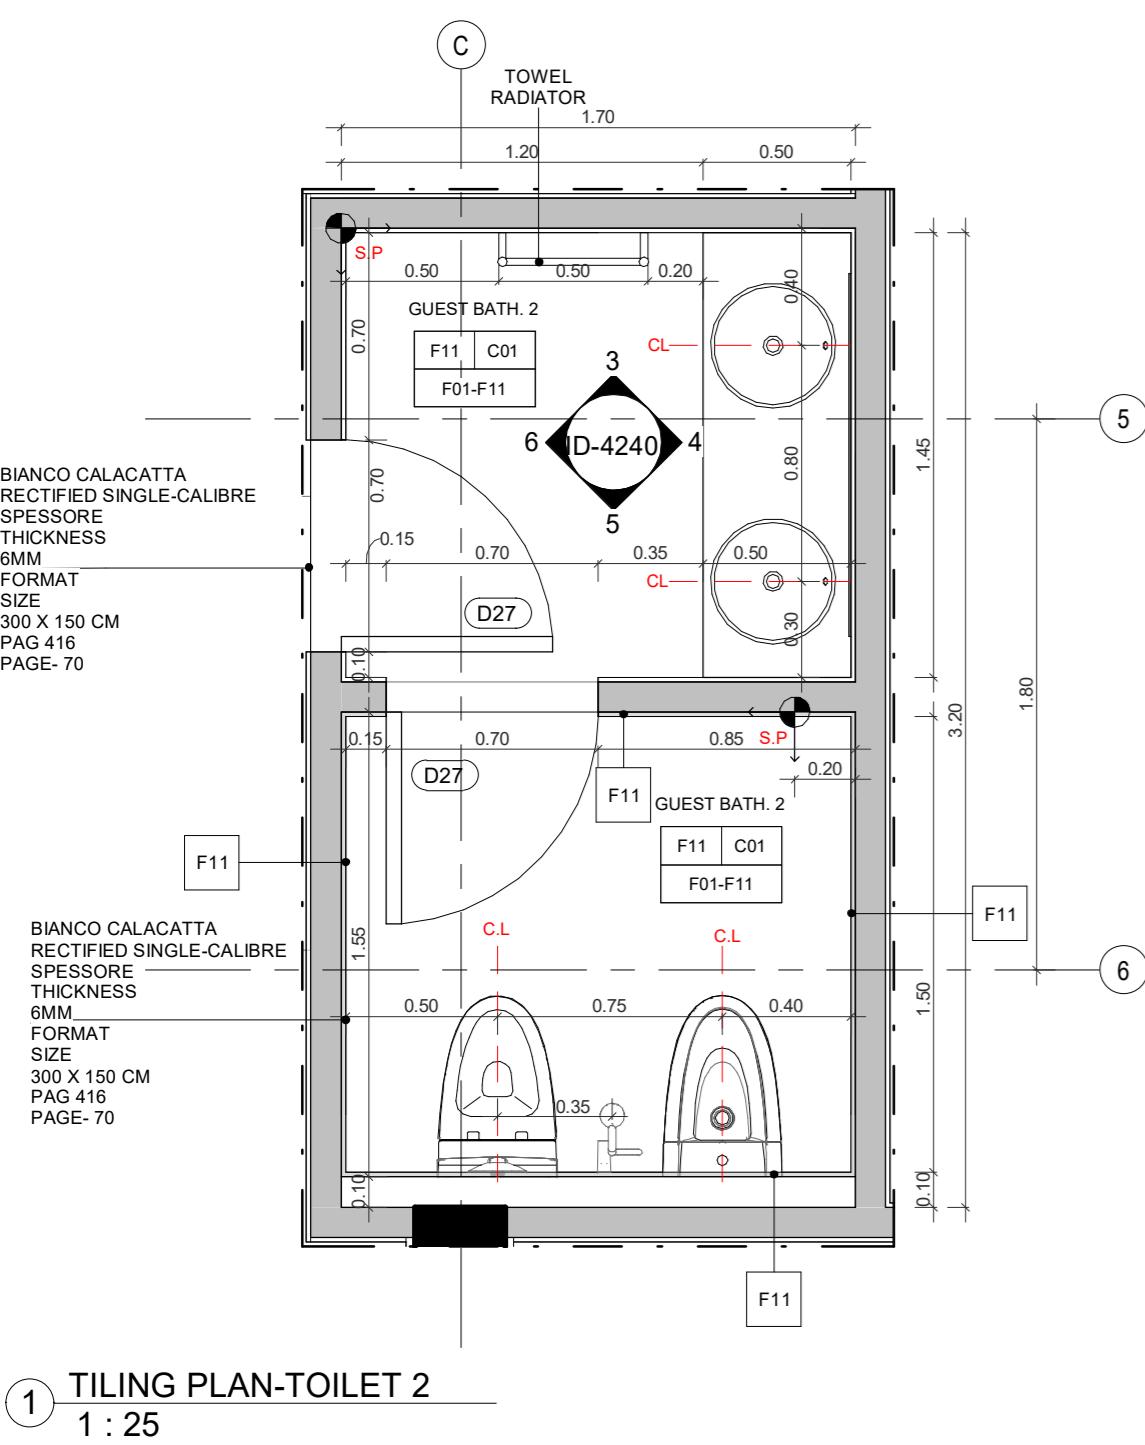

PROJECT NAME

APARTMENTS BUILDING

NOTES

Project Type	Residential
Owner	Khalid Khadir Hasan AL-Saeed
Location	Amman
Plot No.	1659
Basin No.	19
Designed by	A.Shaker Khulief 4809


SHEET NAME

MASTER BEDROOM-SHOT

ID-4250

Date 08/10/2019

Scale

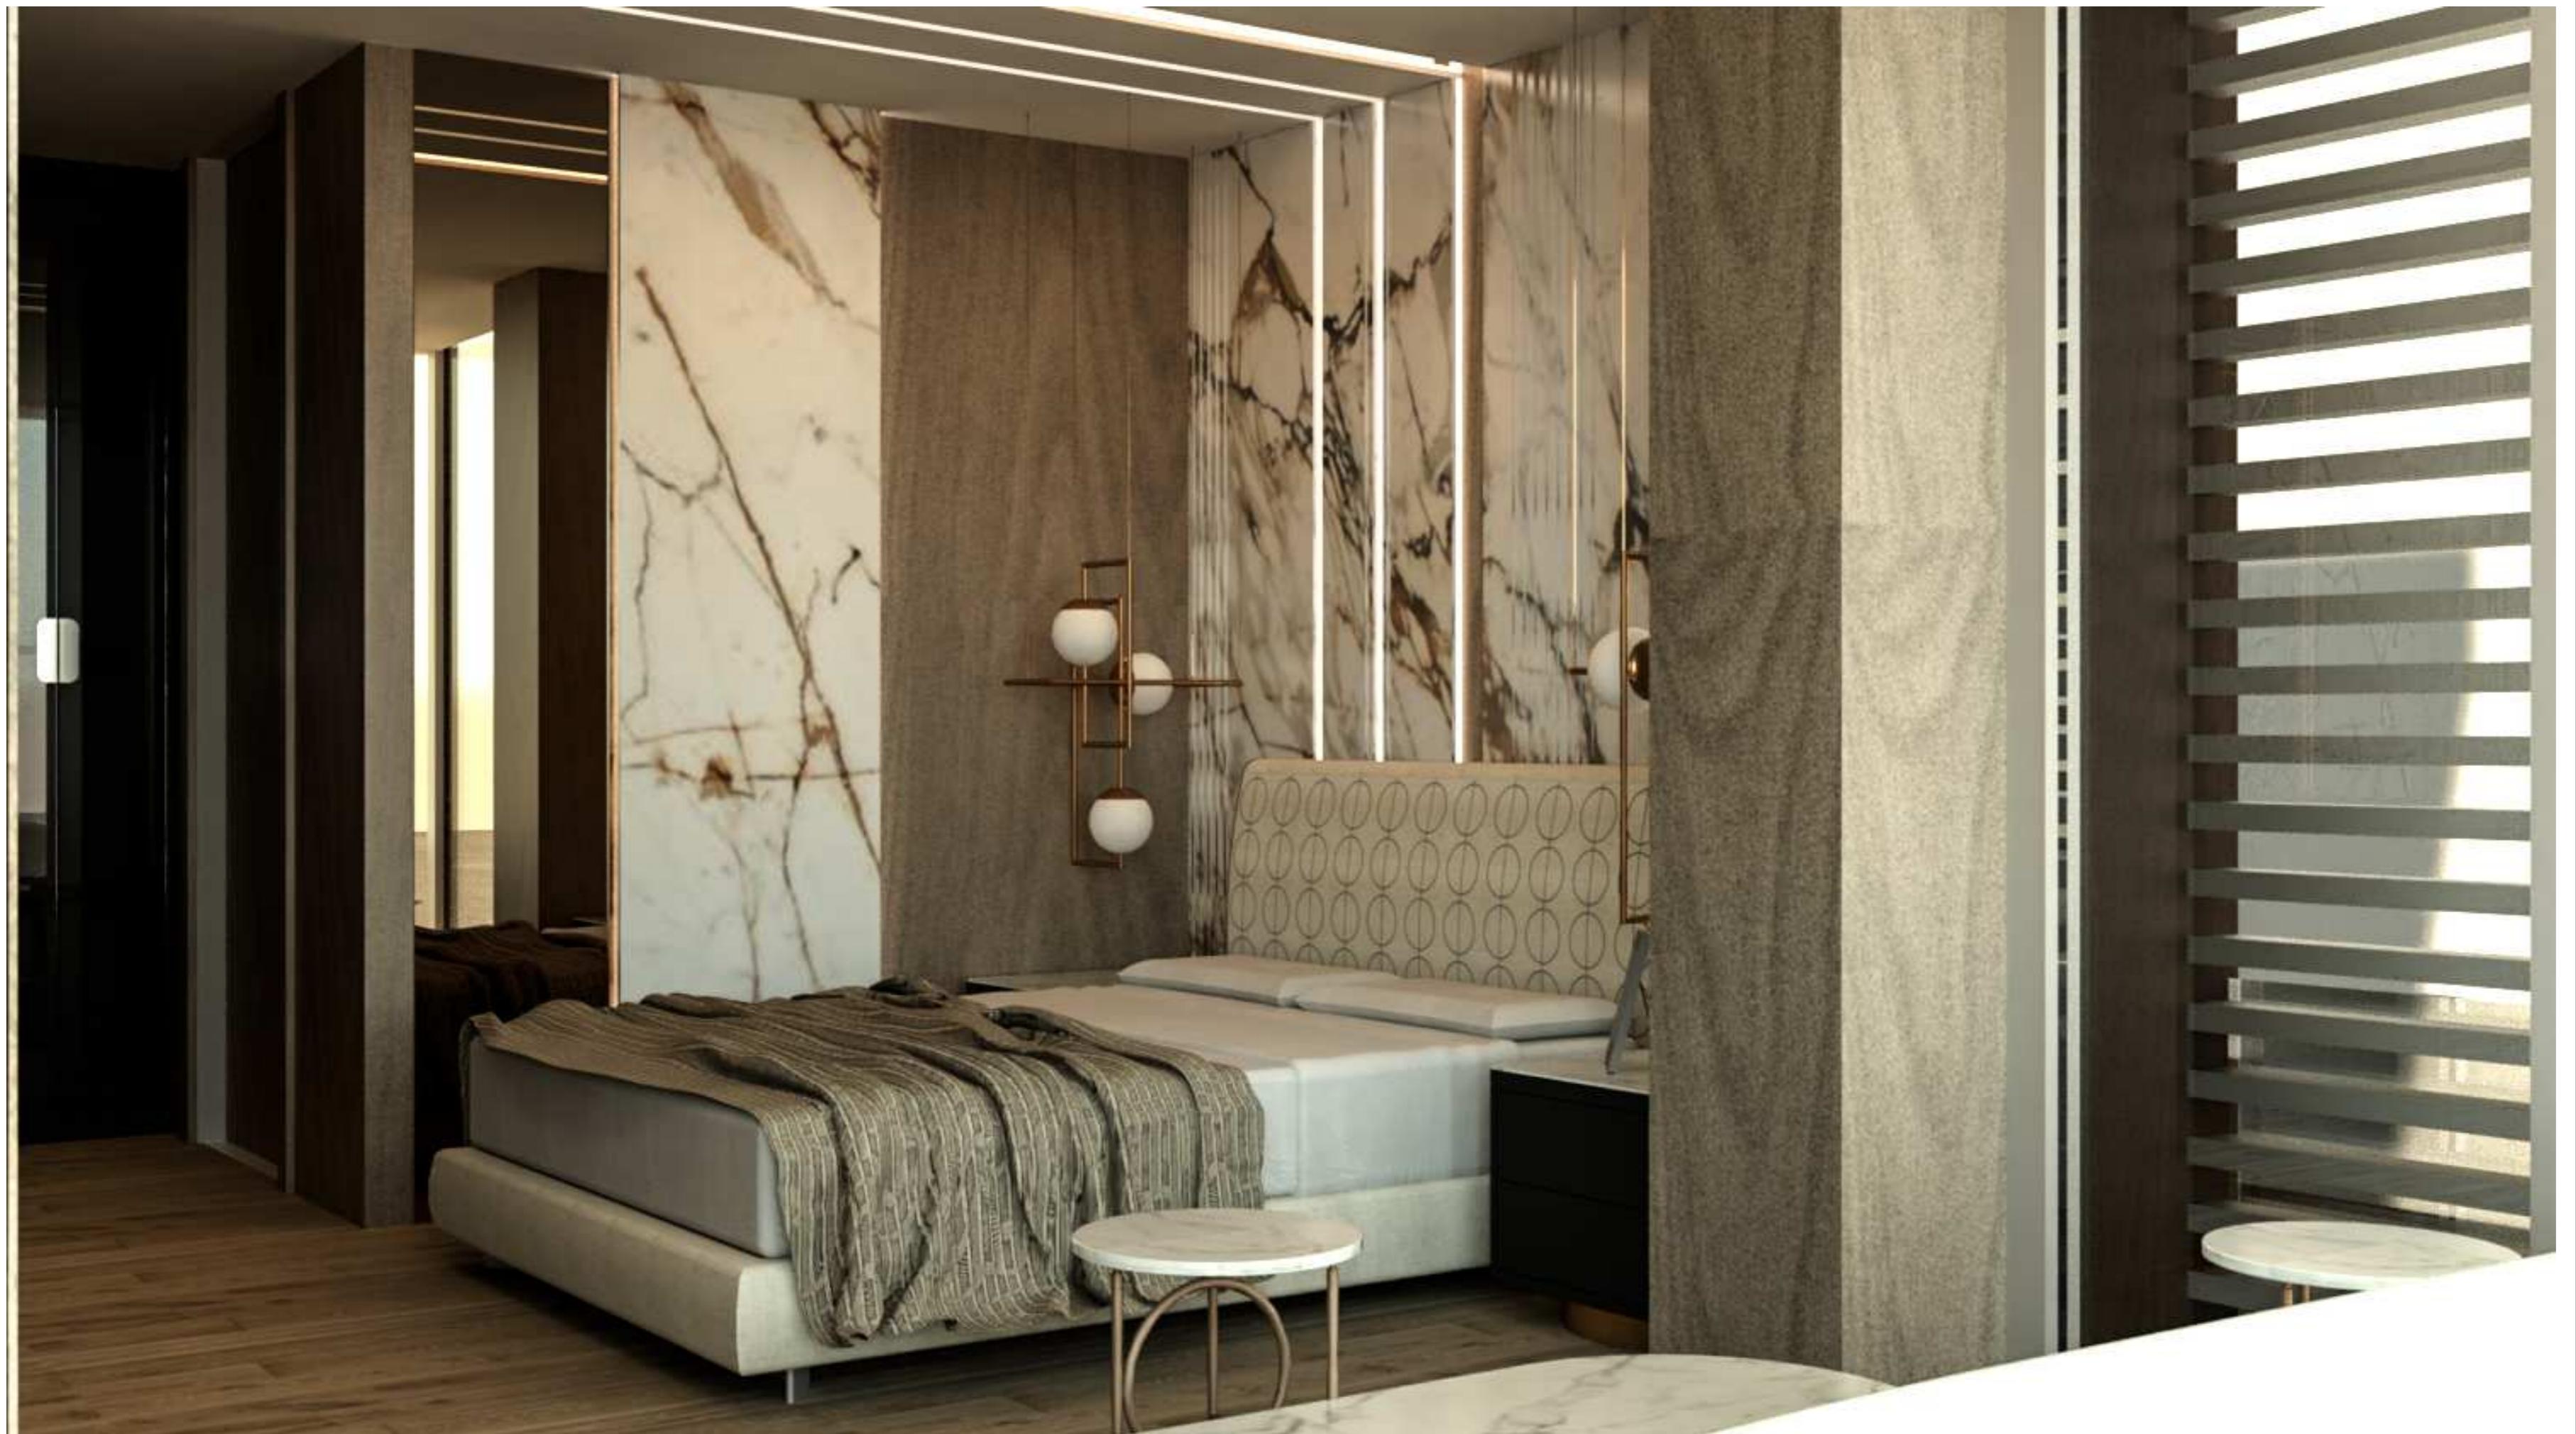

PROJECT NAME

APARTMENTS BUILDING

NOTES

FOR FINISHES REFER TO SHEETS:
ID-6000
ID-6001

ROOM NAME

FLOOR FINISH	CEILING FINISH
WALL FINISH	
FINISHES	FINISHES
FINISH TAG	COMMENTS
F01	
F02	
F03	GOLD STONE
F04	DARK WOOD
F05	DARK WOOD
F06	WOOD
F07	BLACK MARBLE
F08	BEIGE MARBLE
F09	GREY STONE
F10	WALL PAPER
F11	
F12	
F13	BLACK PAINT
F14	CALACATTA
F15	BEIGE PAINT


SPOT RECESSED LIGHT
PENDANT LIGHT
HIDDEN LIGHT
CHANDELIER
WALL MOUNTED
NEON RECTANGULAR

Project Type	Residential
Owner	Khalid Khadir Hasan AL-Saeed
Location	Amman
Plot No.	1659
Basin No.	19
Designed by	A.Shaker Khulief 4809

SHEET NAME
FIRST FLOOR- MASTER BEDROOM & BATHROOM 01

ID-4251

Date 08/10/2019
Scale As indicated

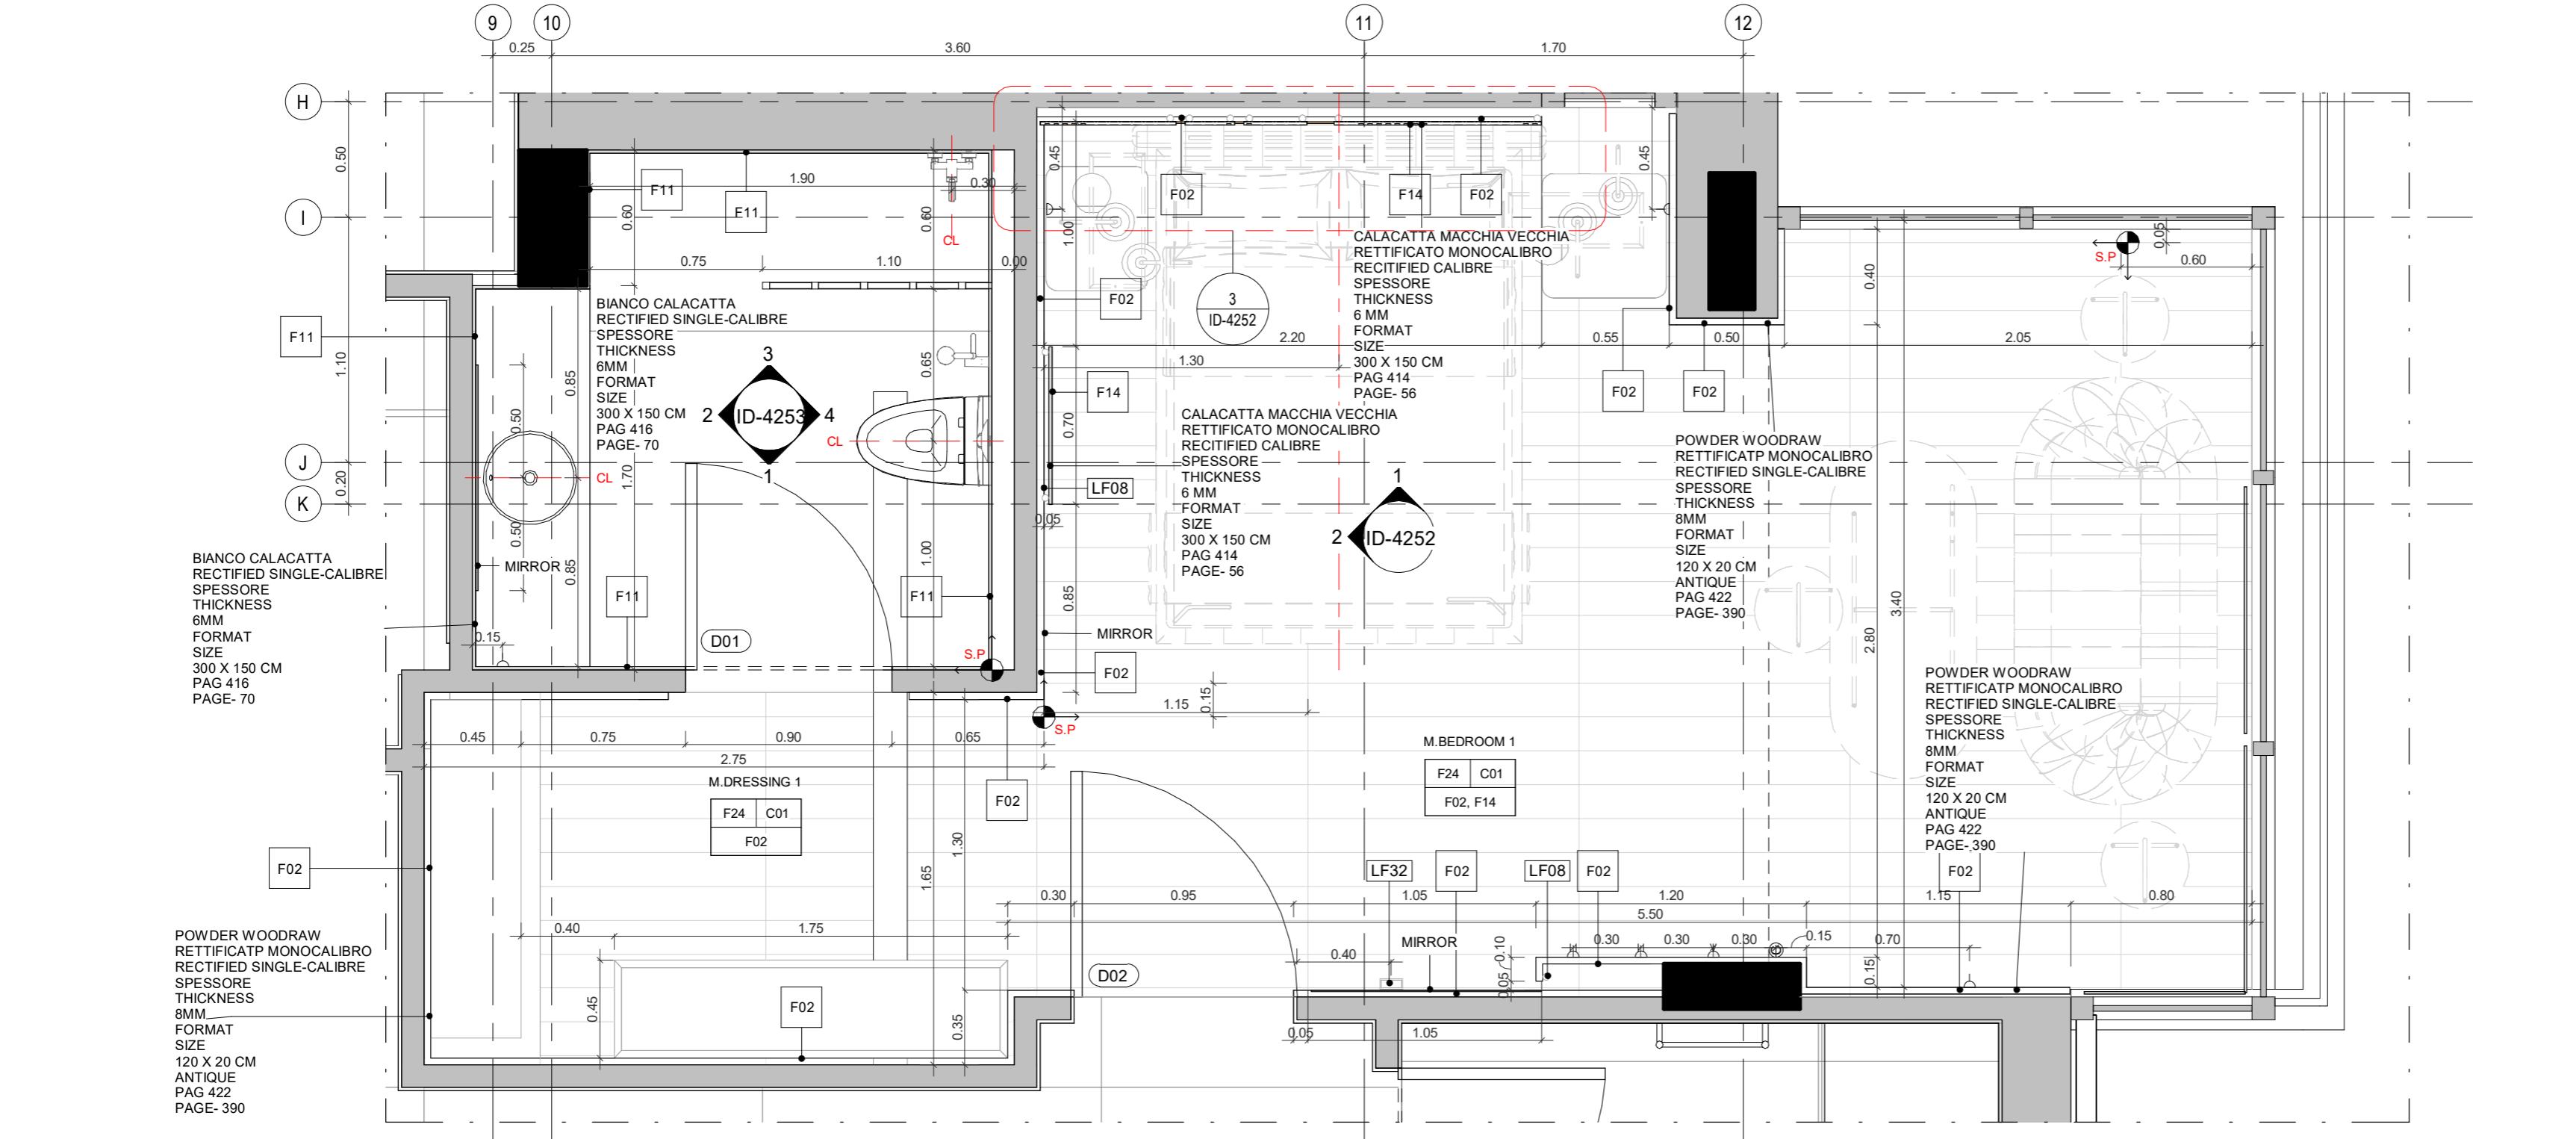

① TILING & FURNITURE PLAN - MASTER BEDROOM & BATHROOM
1 : 25

FINISHES	FINISHES
FINISH TAG	COMMENTS
F16	
F17	LEATHER
F18	PAINT-GOLD METAL EFFECT
F19	
F20	GREY STONE
F21	CONCRETE FINISH
F22	
F23	SWIMMING POOL WALL FINISHES

SPOT RECESSED LIGHT
PENDANT LIGHT
HIDDEN LIGHT
CHANDELIER
WALL MOUNTED
NEON RECTANGULAR





Project Type	Residential
Owner	Khalid Khadir Hasan AL-Saeed
Location	Amman
Plot No.	1659
Basin No.	19
Designed by	A.Shaker Khulief 4809

SHEET NAME	
FIRST FLOOR- MASTER BEDROOM & BATHROOM 01	
Date	08/10/2019
Scale	As indicated


② CEILING PLAN- MASTER BEDROOM & BATHROOM

1 : 25


PROJECT NAME	APARTMENTS BUILDING		
NOTES	FOR FINISHES REFER TO SHEETS: ID-6000 ID-6001		
ROOM NAME	FLOOR FINISH	CEILING FINISH	
WALL FINISH			
FINISHES	FINISHES		
FINISH TAG	COMMENTS	FINISH TAG	COMMENTS
F01		F16	
F02		F17	LEATHER
F03	GOLD STONE	F18	PAINT-GOLD METAL EFFECT
F04	DARK WOOD	F19	
F05	WOOD	F20	GREY STONE
F06	BLACK MARBLE	F21	CONCRETE FINISH
F07	BEIGE MARBLE	F22	
F08		F23	SWIMMING POOL WALL FINISHES
F09	GREY STONE		
F10	WALL PAPER		
F11			
F12			
F13	BLACK PAINT		
F14	CALACATTA		
F15	BEIGE PAINT		
SPOT RECESSED LIGHT			
PENDANT LIGHT			
HIDDEN LIGHT			
CHANDELIER			
WALL MOUNTED			
NEON RECTANGULAR			
Project Type	Residential		
Owner	Khalid Khadir Hasan AL-Saeed		
Location	Amman		
Plot No.	1659		
Basin No.	19		
Designed by	A.Shaker Khulief 4809		
SHEET NAME	FIRST FLOOR- MASTER BEDROOM & BATHROOM 01		
ID-4252			
Date	08/10/2019		
Scale	As indicated		

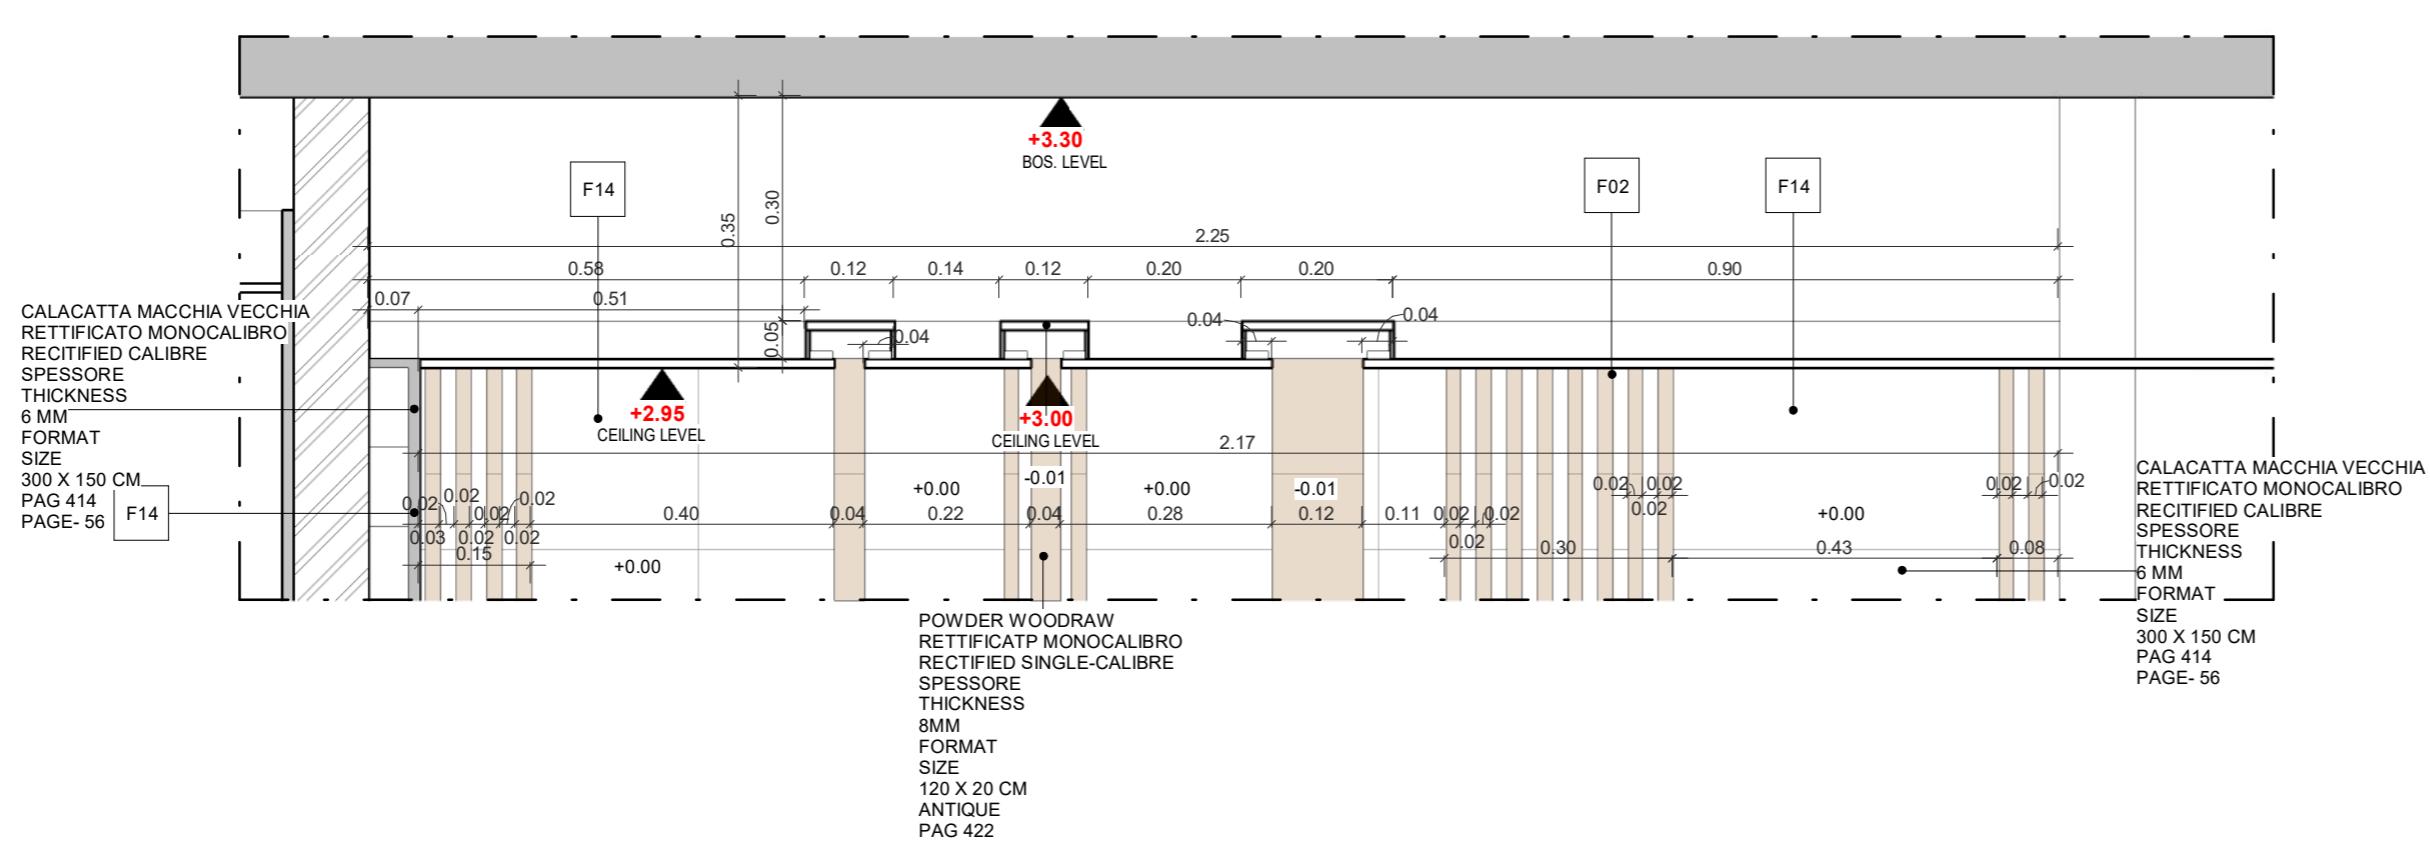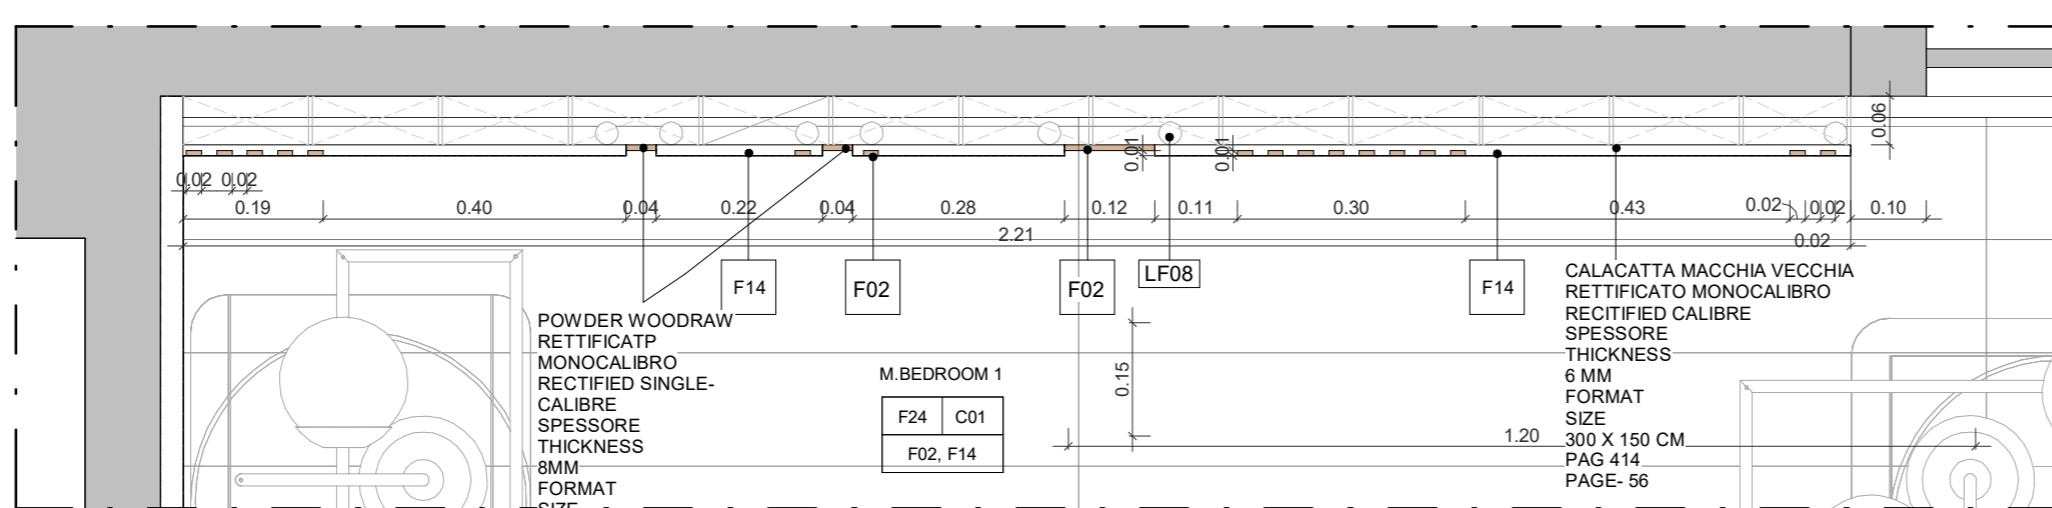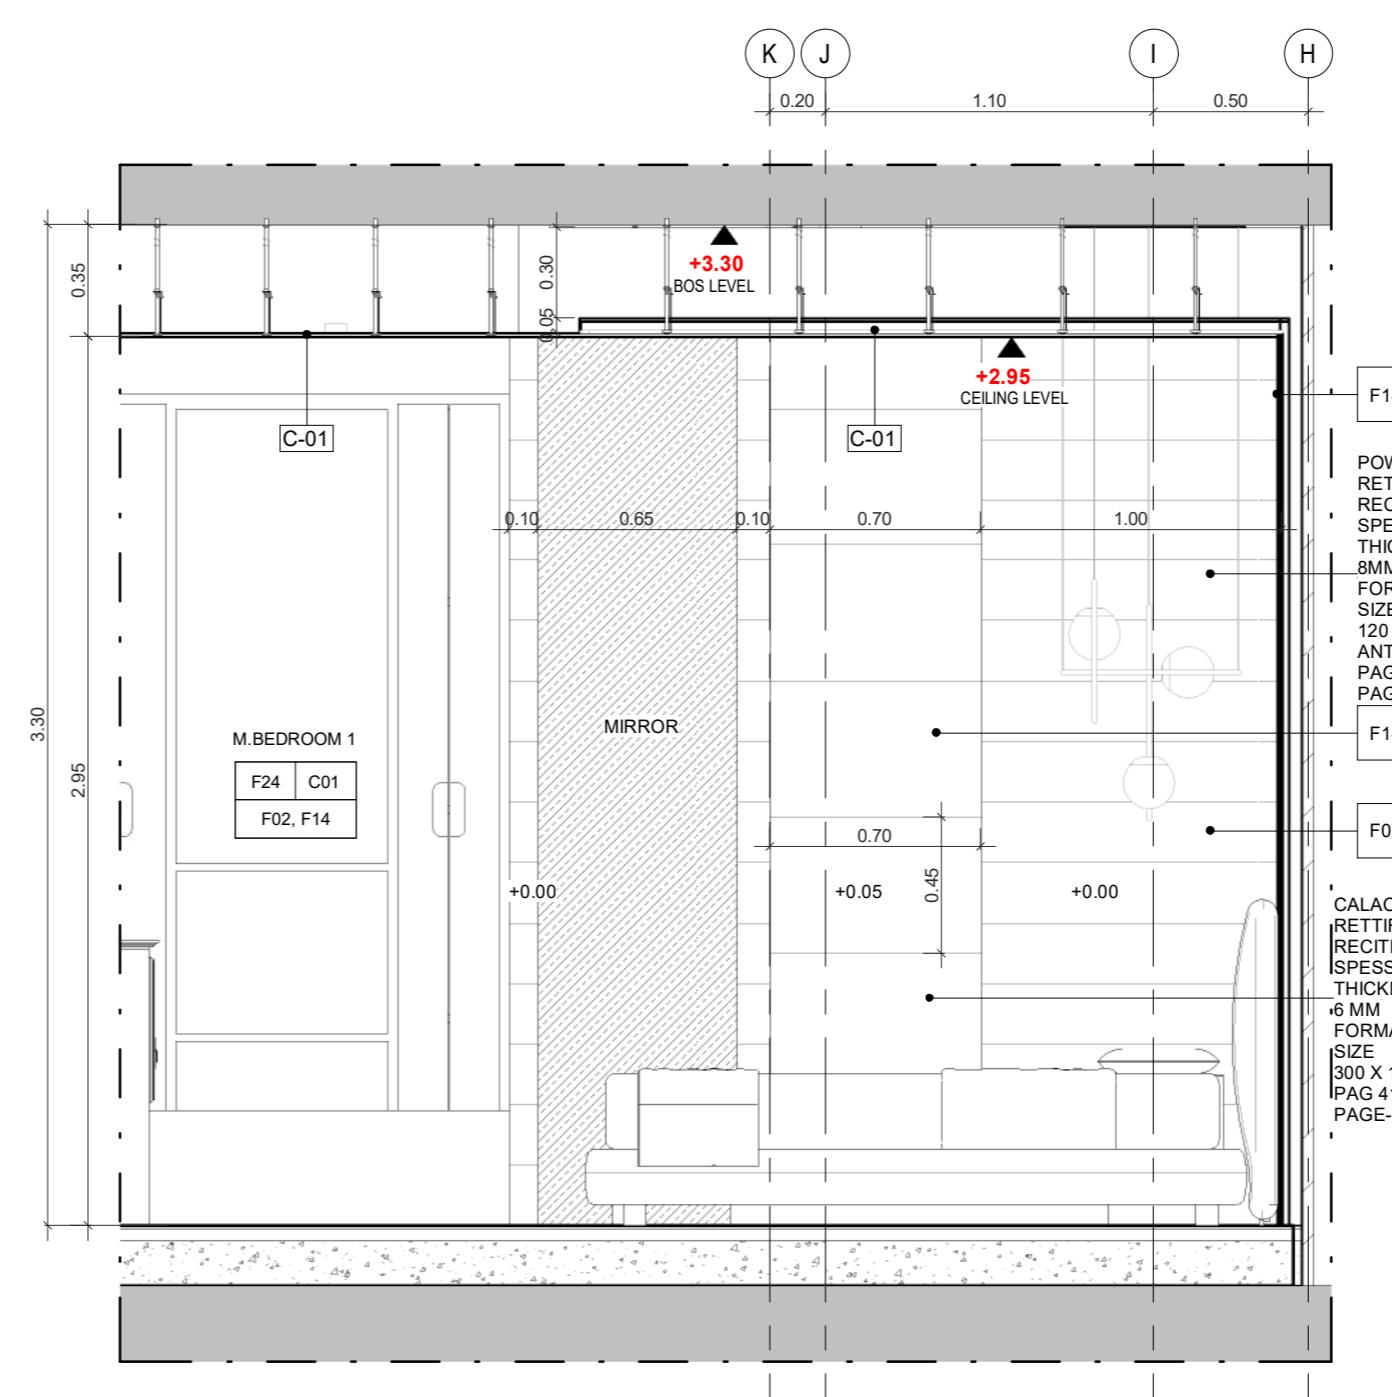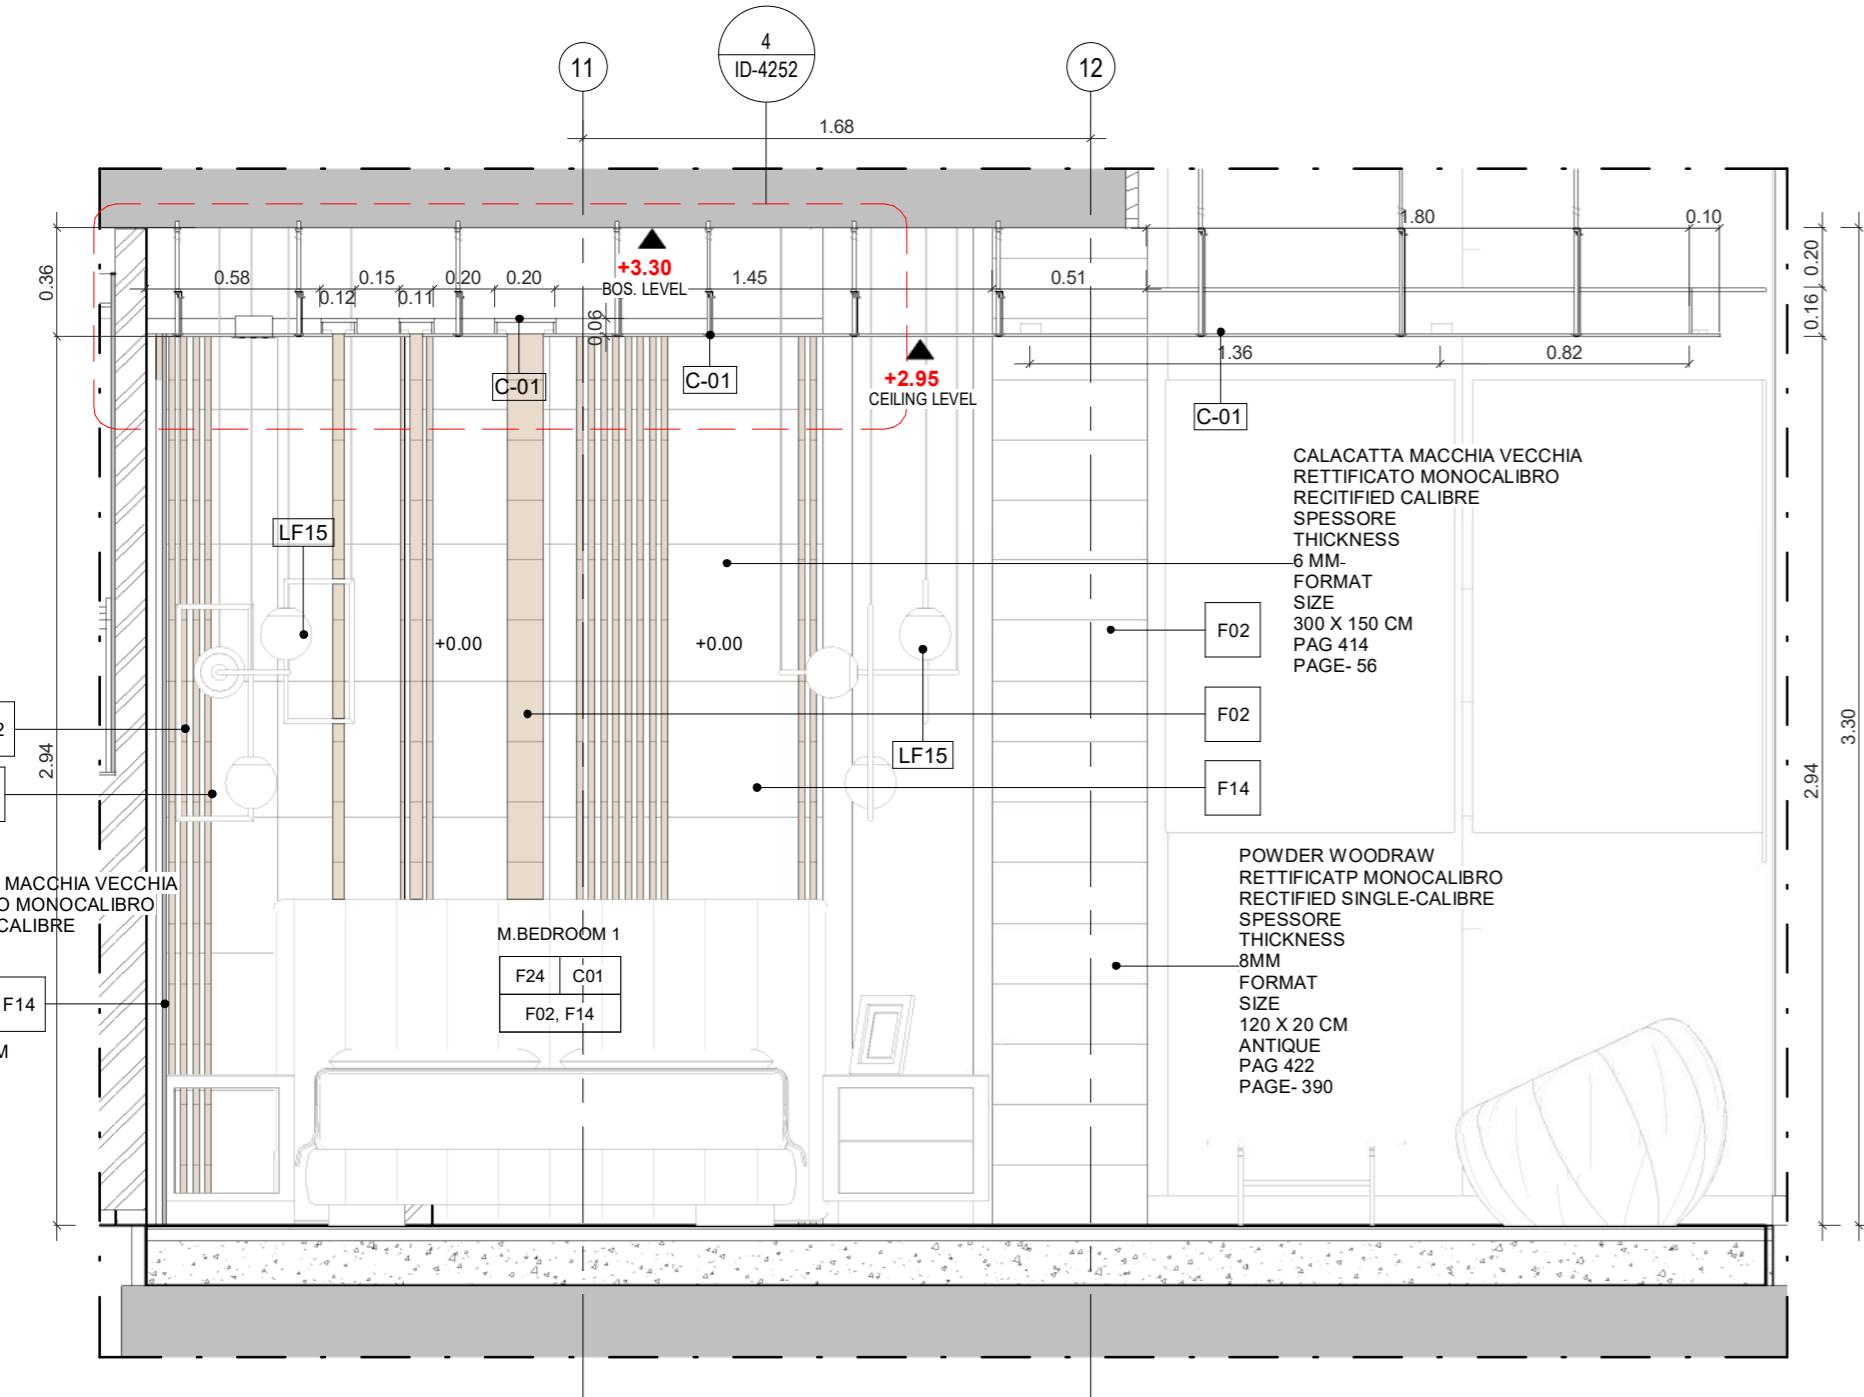


PROJECT NAME	APARTMENTS BUILDING																																			
NOTES	FOR FINISHES REFER TO SHEETS: ID-6000 ID-6001																																			
ROOM NAME																																				
FLOOR FINISH		CEILING FINISH																																		
WALL FINISH																																				
<table border="1"> <thead> <tr> <th>FINISHES</th><th>FINISHES</th></tr> </thead> <tbody> <tr> <td>FINISH TAG</td><td>COMMENTS</td></tr> <tr> <td>F01</td><td></td></tr> <tr> <td>F02</td><td></td></tr> <tr> <td>F03</td><td>GOLD STONE</td></tr> <tr> <td>F04</td><td>DARK WOOD</td></tr> <tr> <td>F05</td><td>DARK WOOD</td></tr> <tr> <td>F06</td><td>WOOD</td></tr> <tr> <td>F07</td><td>BLACK MARBLE</td></tr> <tr> <td>F08</td><td>BEIGE MARBLE</td></tr> <tr> <td>F09</td><td>GREY STONE</td></tr> <tr> <td>F10</td><td>WALL PAPER</td></tr> <tr> <td>F11</td><td></td></tr> <tr> <td>F12</td><td></td></tr> <tr> <td>F13</td><td>BLACK PAINT</td></tr> <tr> <td>F14</td><td>CALACATTA</td></tr> <tr> <td>F15</td><td>BEIGE PAINT</td></tr> </tbody> </table>		FINISHES	FINISHES	FINISH TAG	COMMENTS	F01		F02		F03	GOLD STONE	F04	DARK WOOD	F05	DARK WOOD	F06	WOOD	F07	BLACK MARBLE	F08	BEIGE MARBLE	F09	GREY STONE	F10	WALL PAPER	F11		F12		F13	BLACK PAINT	F14	CALACATTA	F15	BEIGE PAINT	FINISHES
FINISHES	FINISHES																																			
FINISH TAG	COMMENTS																																			
F01																																				
F02																																				
F03	GOLD STONE																																			
F04	DARK WOOD																																			
F05	DARK WOOD																																			
F06	WOOD																																			
F07	BLACK MARBLE																																			
F08	BEIGE MARBLE																																			
F09	GREY STONE																																			
F10	WALL PAPER																																			
F11																																				
F12																																				
F13	BLACK PAINT																																			
F14	CALACATTA																																			
F15	BEIGE PAINT																																			
<table border="1"> <thead> <tr> <th>FINISH TAG</th><th>COMMENTS</th></tr> </thead> <tbody> <tr> <td>F16</td><td></td></tr> <tr> <td>F17</td><td>LEATHER</td></tr> <tr> <td>F18</td><td>PAINT-GOLD METAL EFFECT</td></tr> <tr> <td>F19</td><td></td></tr> <tr> <td>F20</td><td>GREY STONE</td></tr> <tr> <td>F21</td><td>CONCRETE FINISH</td></tr> <tr> <td>F22</td><td></td></tr> <tr> <td>F23</td><td>SWIMMING POOL WALL FINISHES</td></tr> </tbody> </table>		FINISH TAG	COMMENTS	F16		F17	LEATHER	F18	PAINT-GOLD METAL EFFECT	F19		F20	GREY STONE	F21	CONCRETE FINISH	F22		F23	SWIMMING POOL WALL FINISHES	FINISHES																
FINISH TAG	COMMENTS																																			
F16																																				
F17	LEATHER																																			
F18	PAINT-GOLD METAL EFFECT																																			
F19																																				
F20	GREY STONE																																			
F21	CONCRETE FINISH																																			
F22																																				
F23	SWIMMING POOL WALL FINISHES																																			
<table border="1"> <thead> <tr> <th>Project Type</th><th>Residential</th></tr> <tr> <th>Owner</th><td>Khalid Khadir Hasan AL-Saeed</td></tr> <tr> <th>Location</th><td>Amman</td></tr> <tr> <th>Plot No.</th><td>1659</td></tr> <tr> <th>Basin No.</th><td>19</td></tr> <tr> <th>Designed by</th><td>A.Shaker Khulief 4809</td></tr> </thead> </table>			Project Type	Residential	Owner	Khalid Khadir Hasan AL-Saeed	Location	Amman	Plot No.	1659	Basin No.	19	Designed by	A.Shaker Khulief 4809																						
Project Type	Residential																																			
Owner	Khalid Khadir Hasan AL-Saeed																																			
Location	Amman																																			
Plot No.	1659																																			
Basin No.	19																																			
Designed by	A.Shaker Khulief 4809																																			
SHEET NAME																																				
FIRST FLOOR- MASTER BEDROOM & BATHROOM 01																																				
ID-4253																																				
Date	08/10/2019																																			
Scale	1 : 25																																			

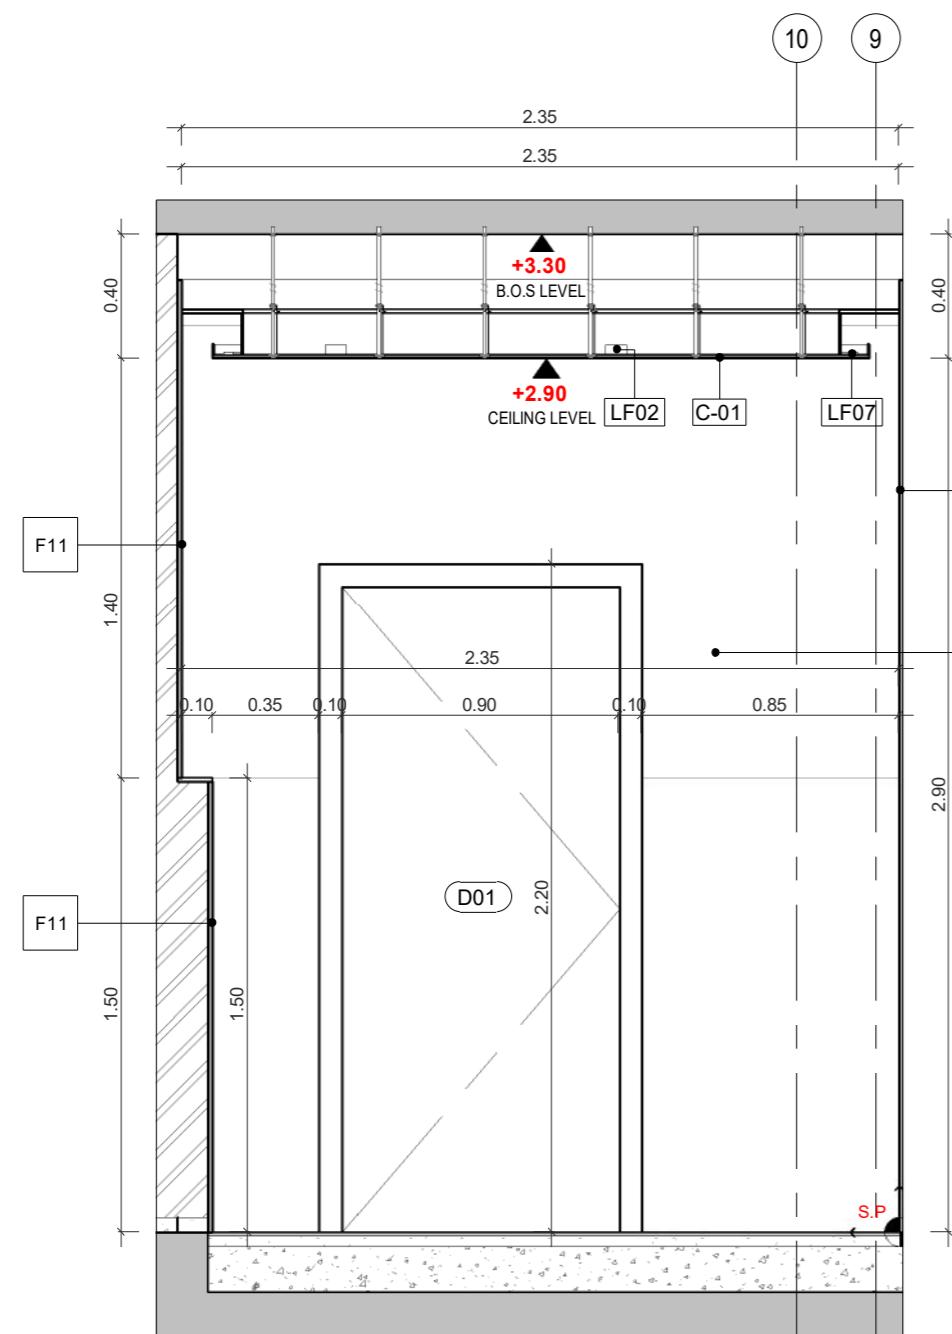


① MASTER BEDROOM 1-ELEVATION 01
1 : 25

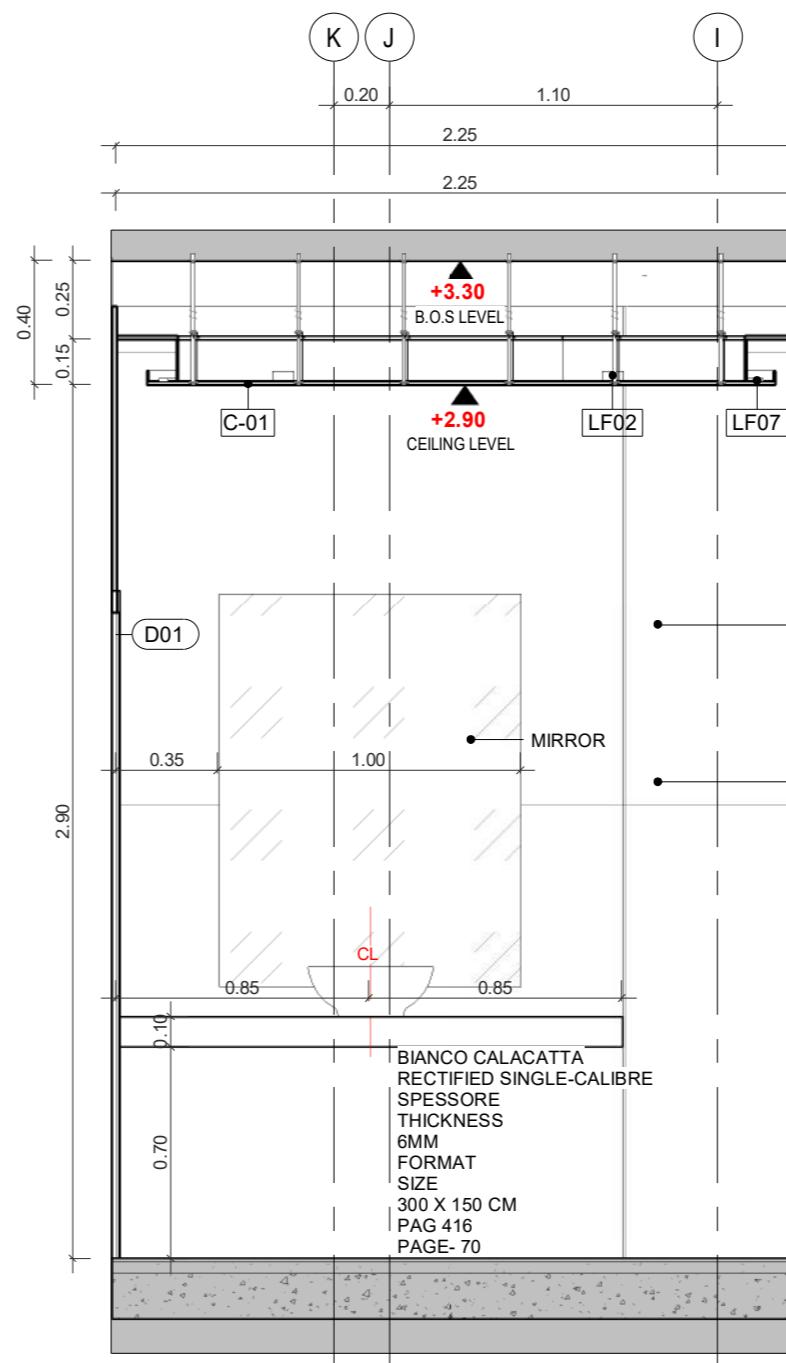

② MASTER BDEROOM 1-ELEVATION 02
1 : 25

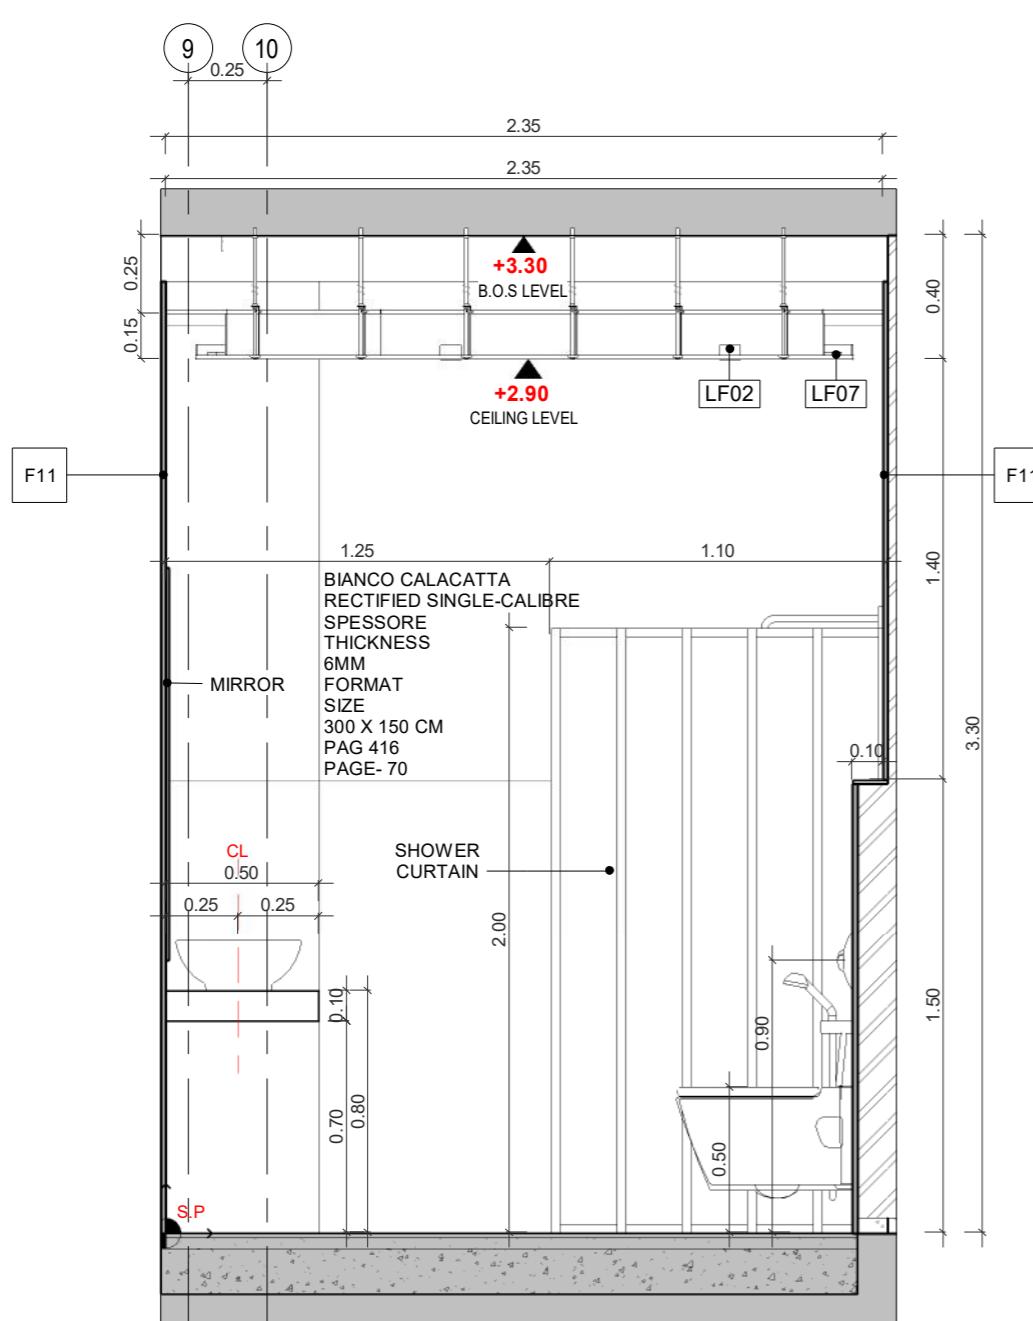

③ MASTER BEDROOM 1-ELEVATION 03
1 : 25

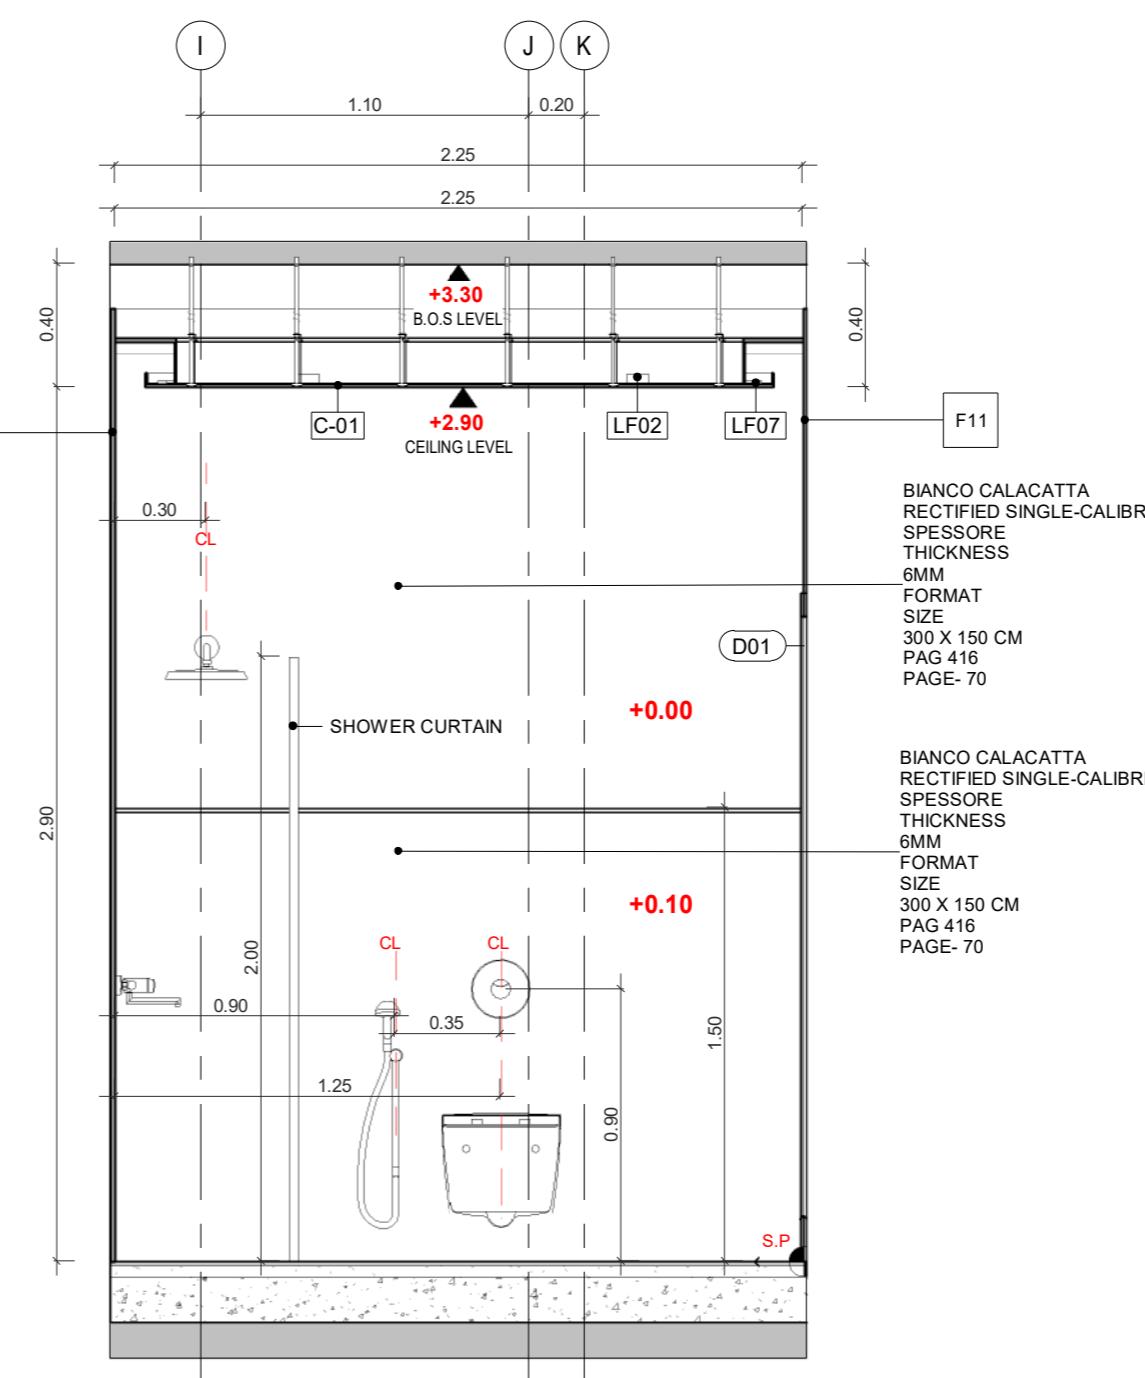

④ MASTER BEDROOM 1-ELEVATION 04
1 : 25

PROJECT NAME

APARTMENTS BUILDING

NOTES



Project Type	Residential
Owner	Khalid Khadir Hasan AL-Saeed
Location	Amman
Plot No.	1659
Basin No.	19
Designed by	A.Shaker Khulief 4809

SHEET NAME
LIVING ROOM & SALON-SHOT

ID-4300


Date 08/10/2019

Scale


PROJECT NAME

APARTMENTS BUILDING


NOTES

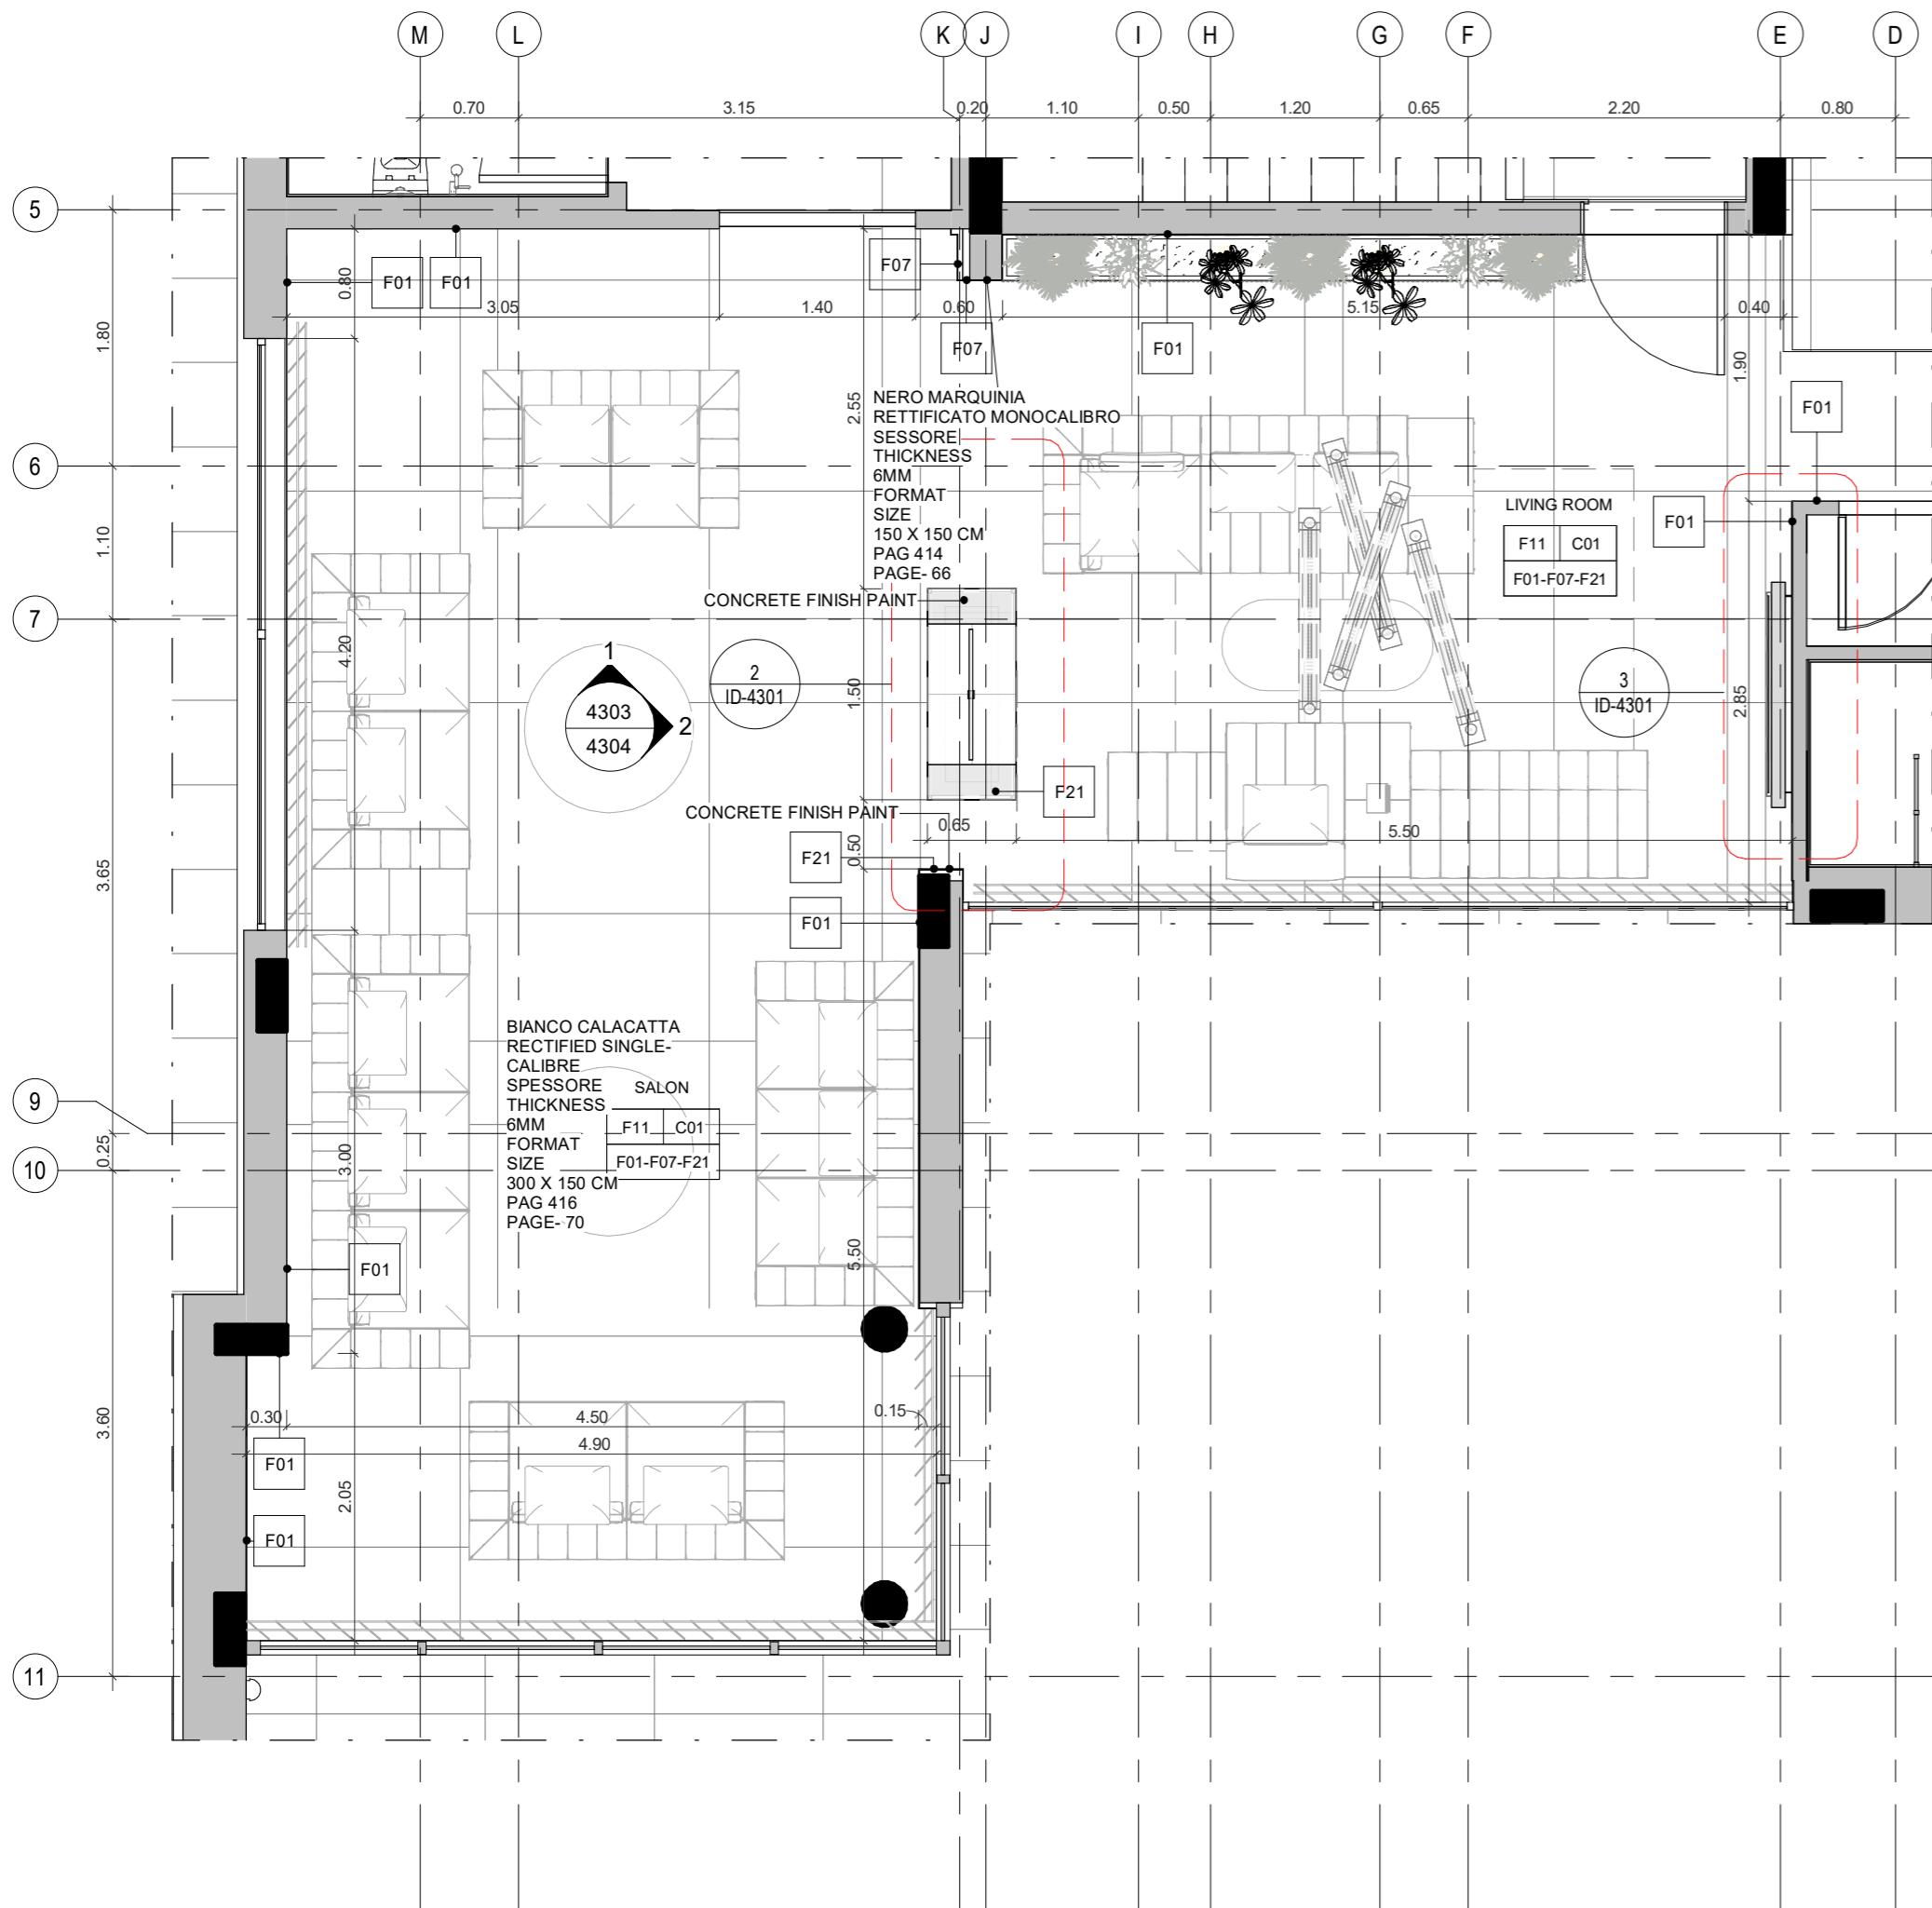

1 TILING & FURNITURE PLAN - ROOF LIVING ROOM & SALON
1 : 50

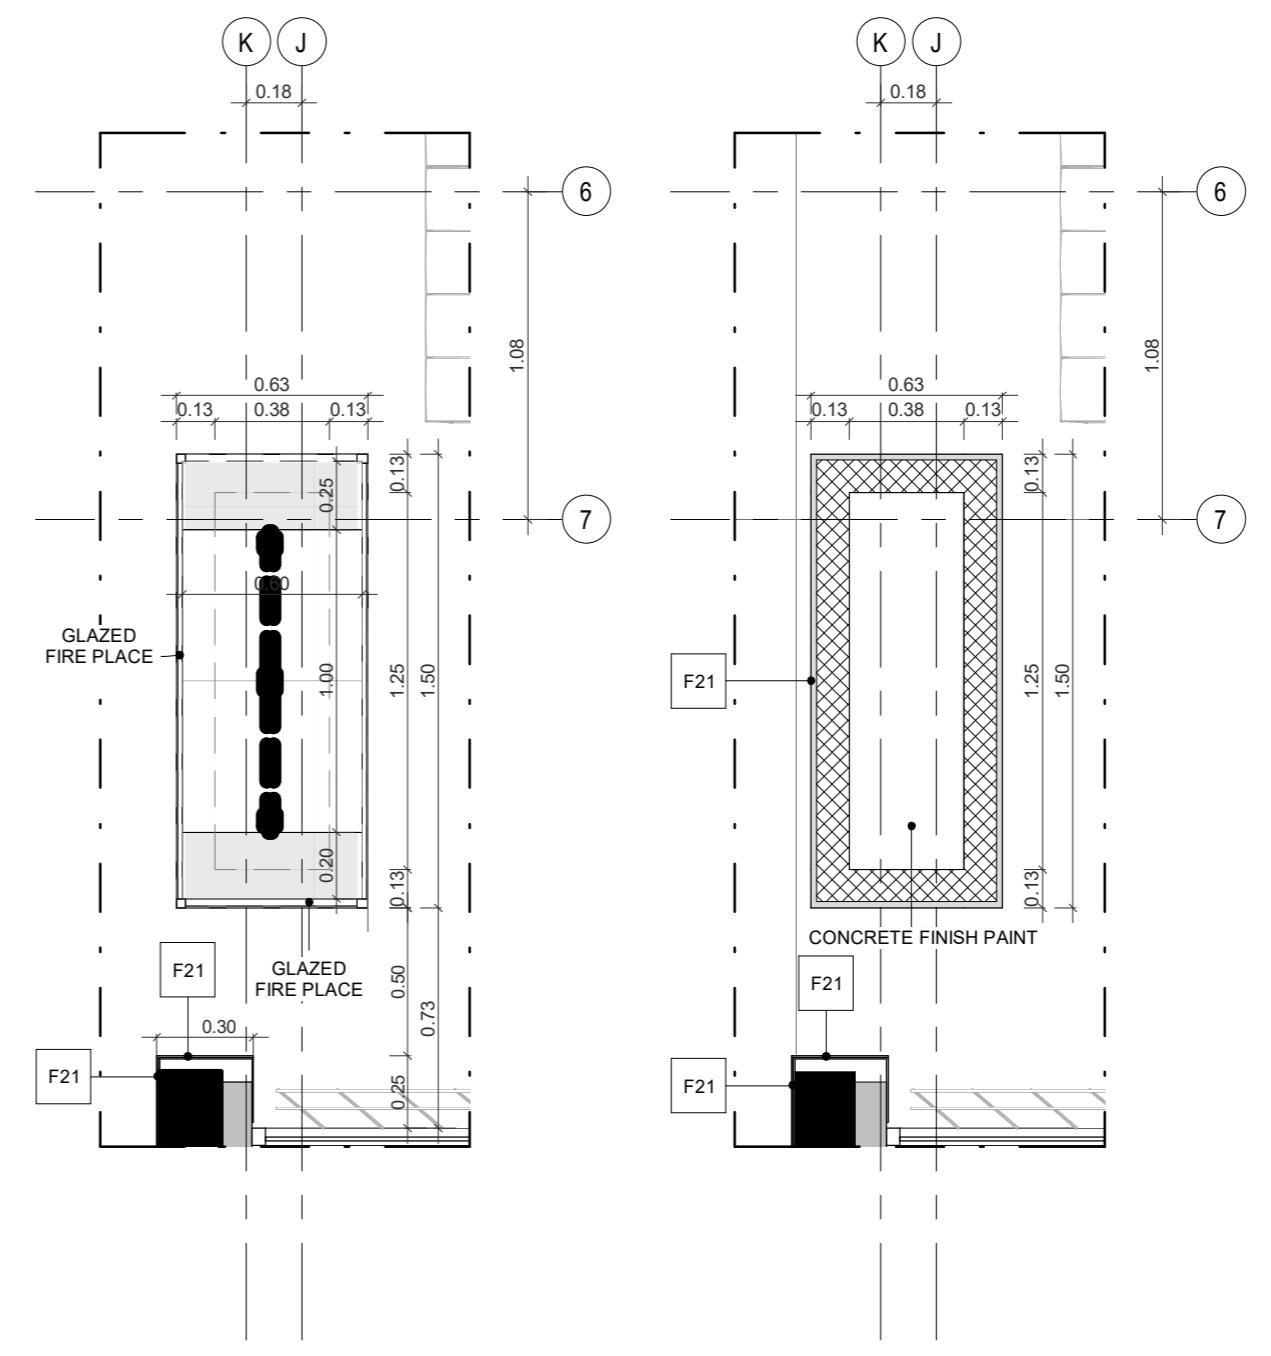

2 PLAN DETAIL
1 : 25

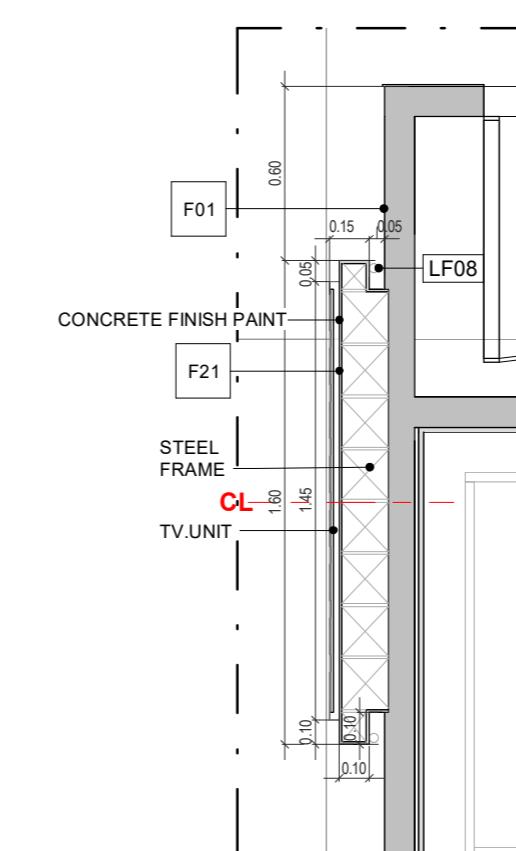

3 PLAN DETAIL
1 : 25

Project Type	Residential
Owner	Khalid Khadir Hasan AL-Saeed
Location	Amman
Plot No.	1659
Basin No.	19
Designed by	A.Shaker Khulief 4809

SHEET NAME

**ROOF FLOOR -LIVING ROOM
AND SALON**

ID-4301

Date	08/10/2019
Scale	As indicated

PROJECT NAME

APARTMENTS BUILDING

NOTES


FOR FINISHES REFER TO SHEETS:
ID-6000
ID-6001

Project Type	Residential
Owner	Khalid Khadir Hasan AL-Saeed
Location	Amman
Plot No.	1659
Basin No.	19
Designed by	A.Shaker Khulief 4809

SHEET NAME
ROOF FLOOR -LIVING ROOM & SALON CEILING PLAN

ID-4302




Date	08/10/2019
Scale	1 : 50

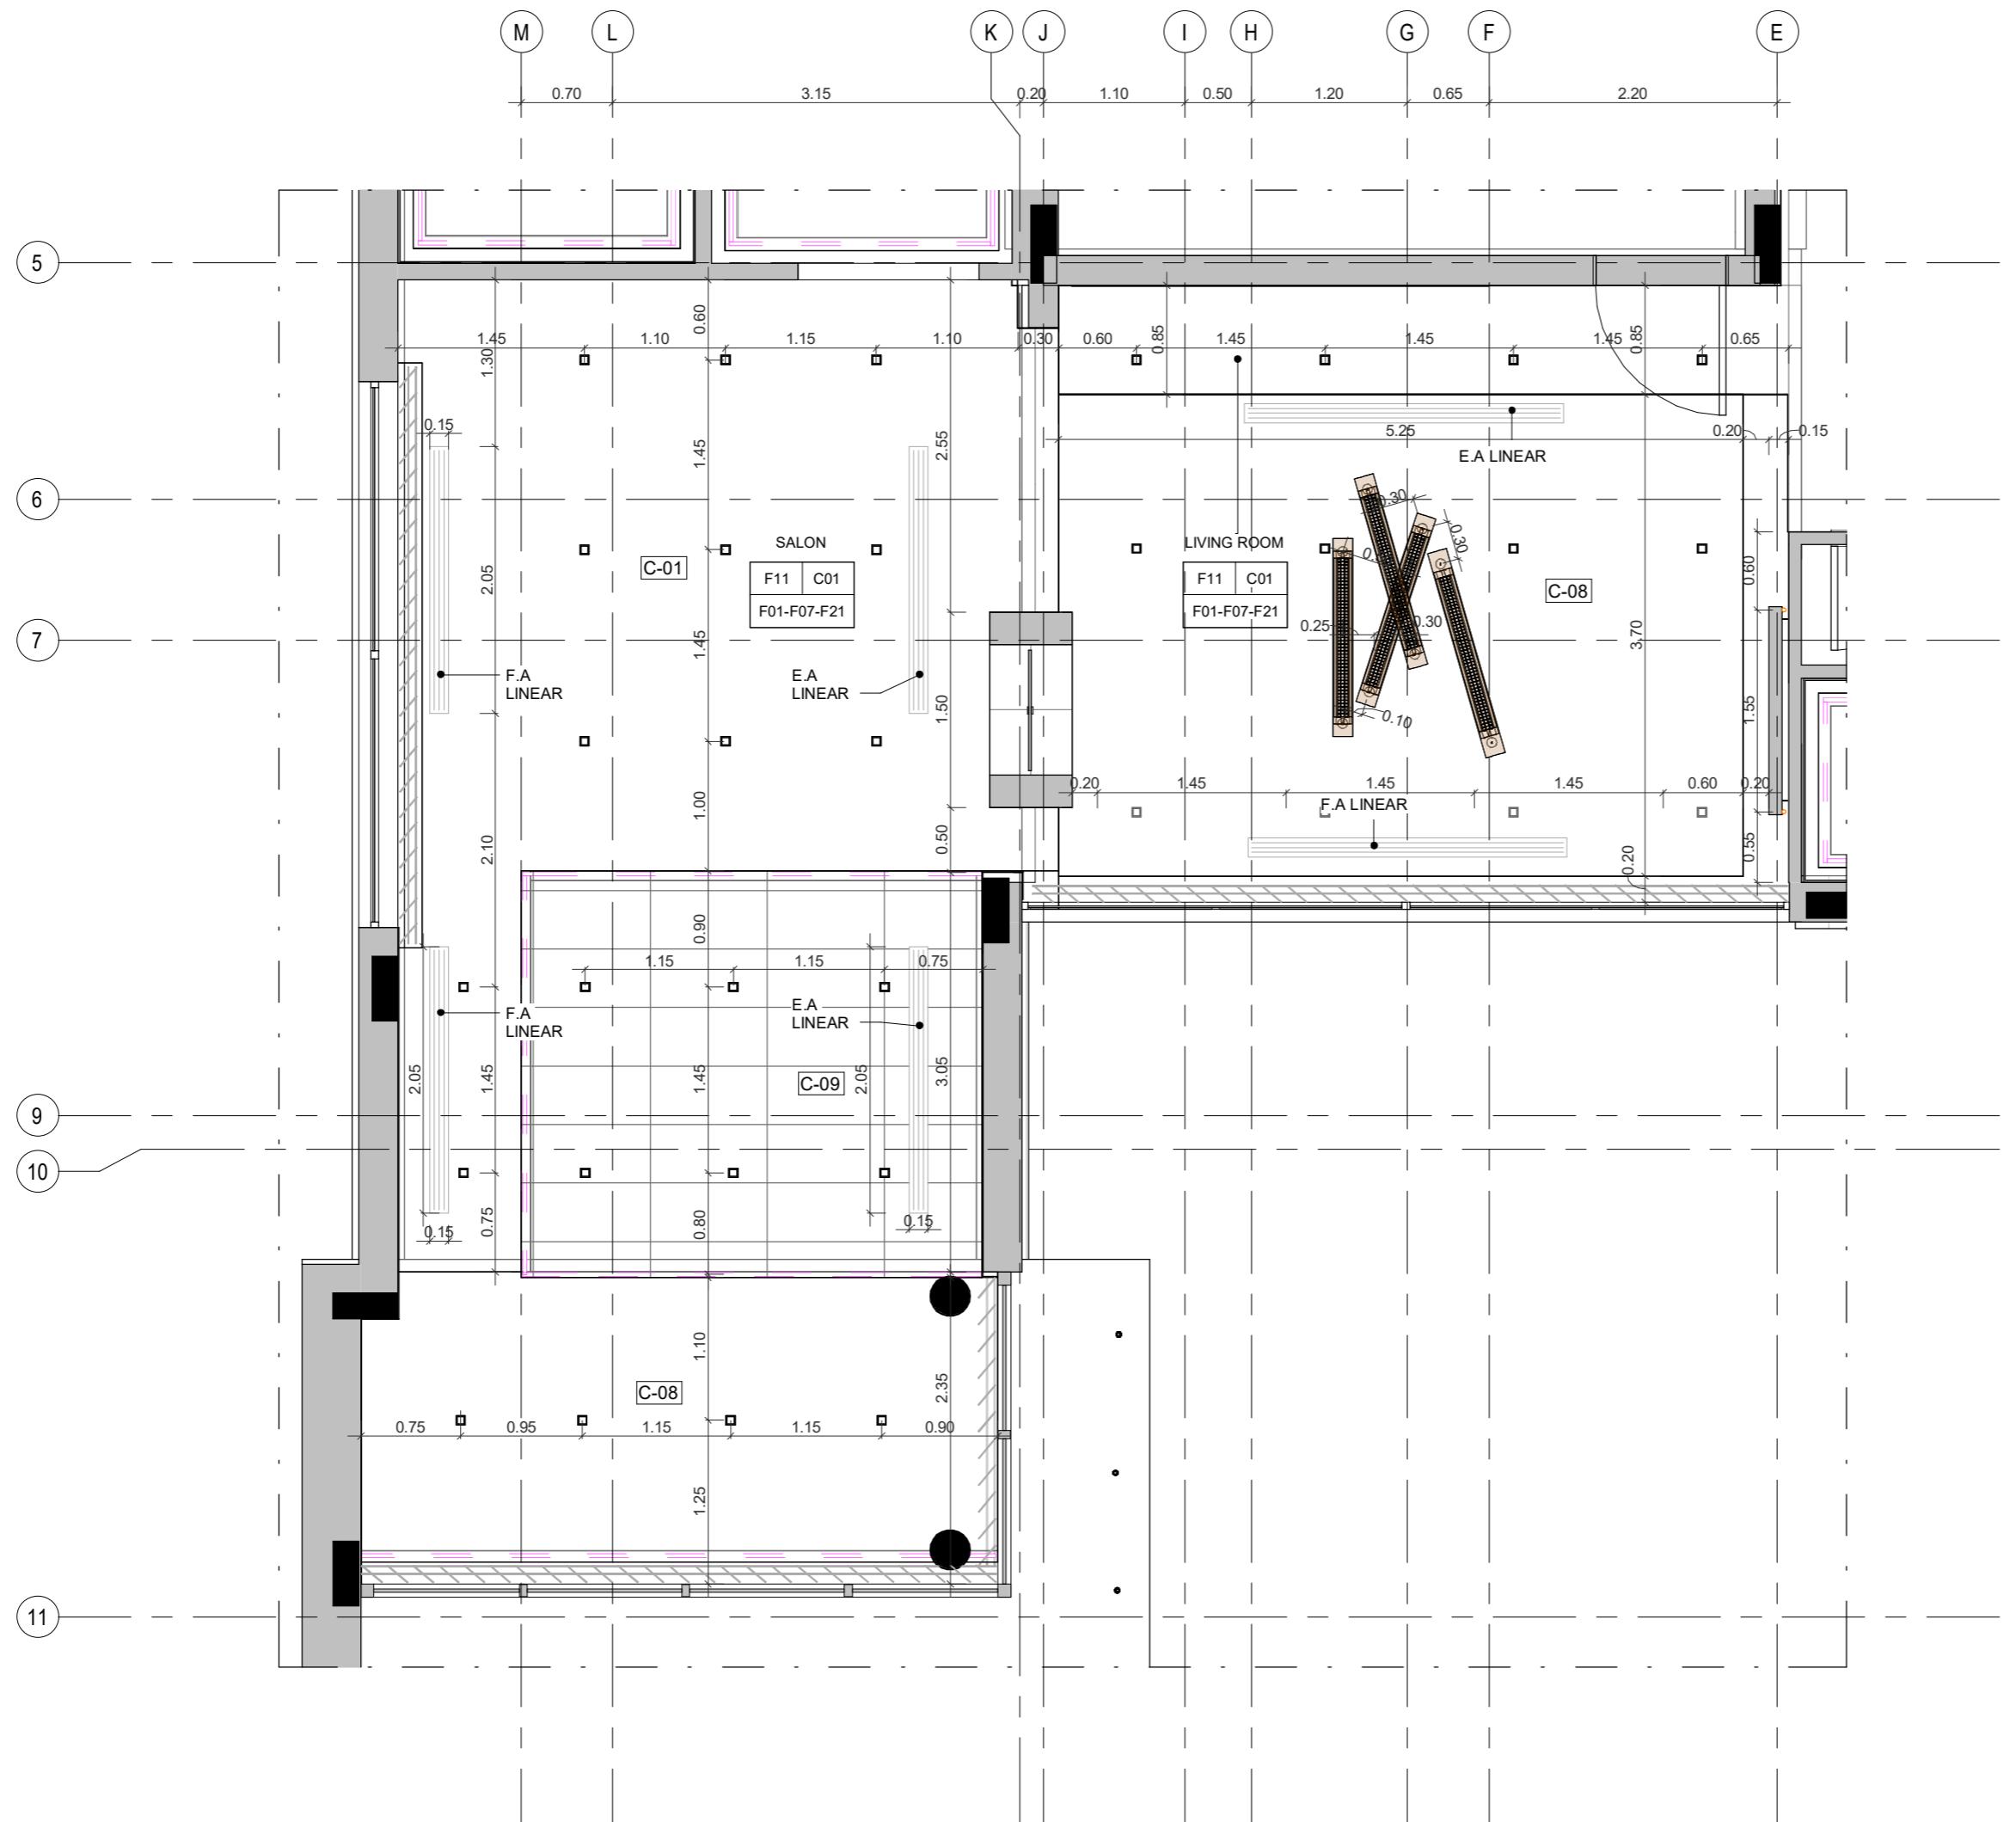

PROJECT NAME

APARTMENTS BUILDING

NOTES

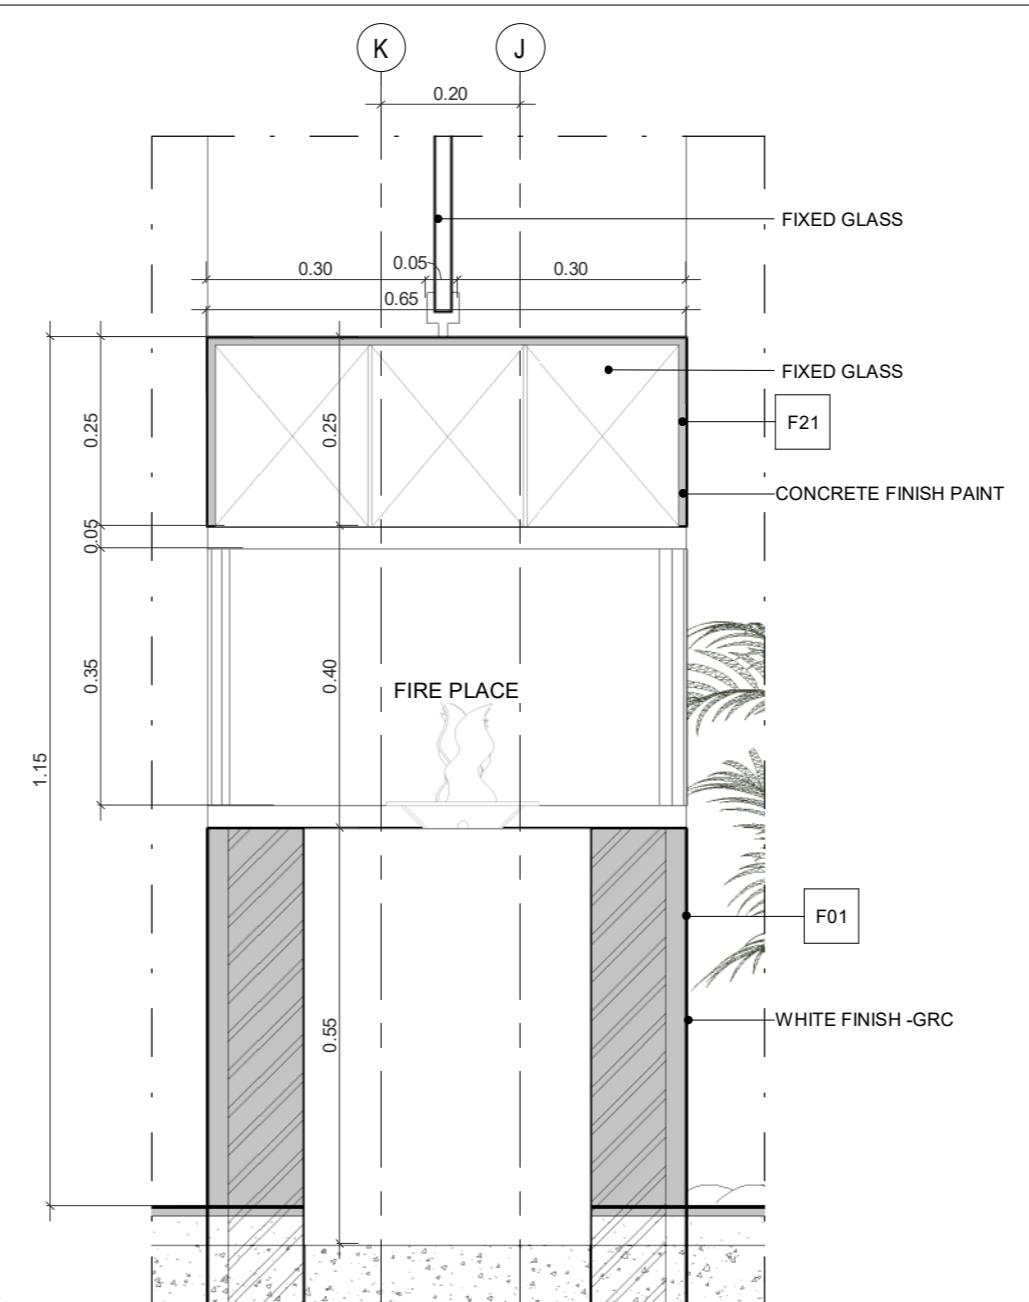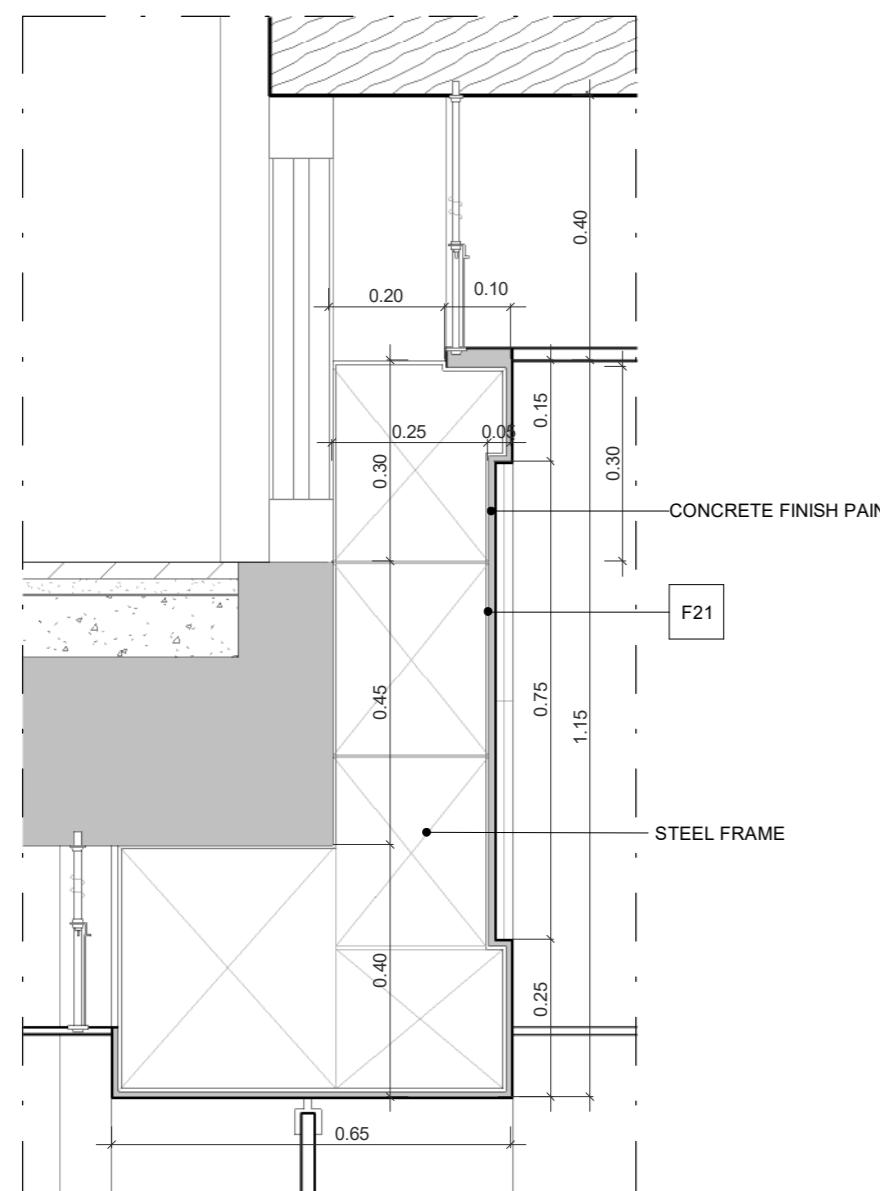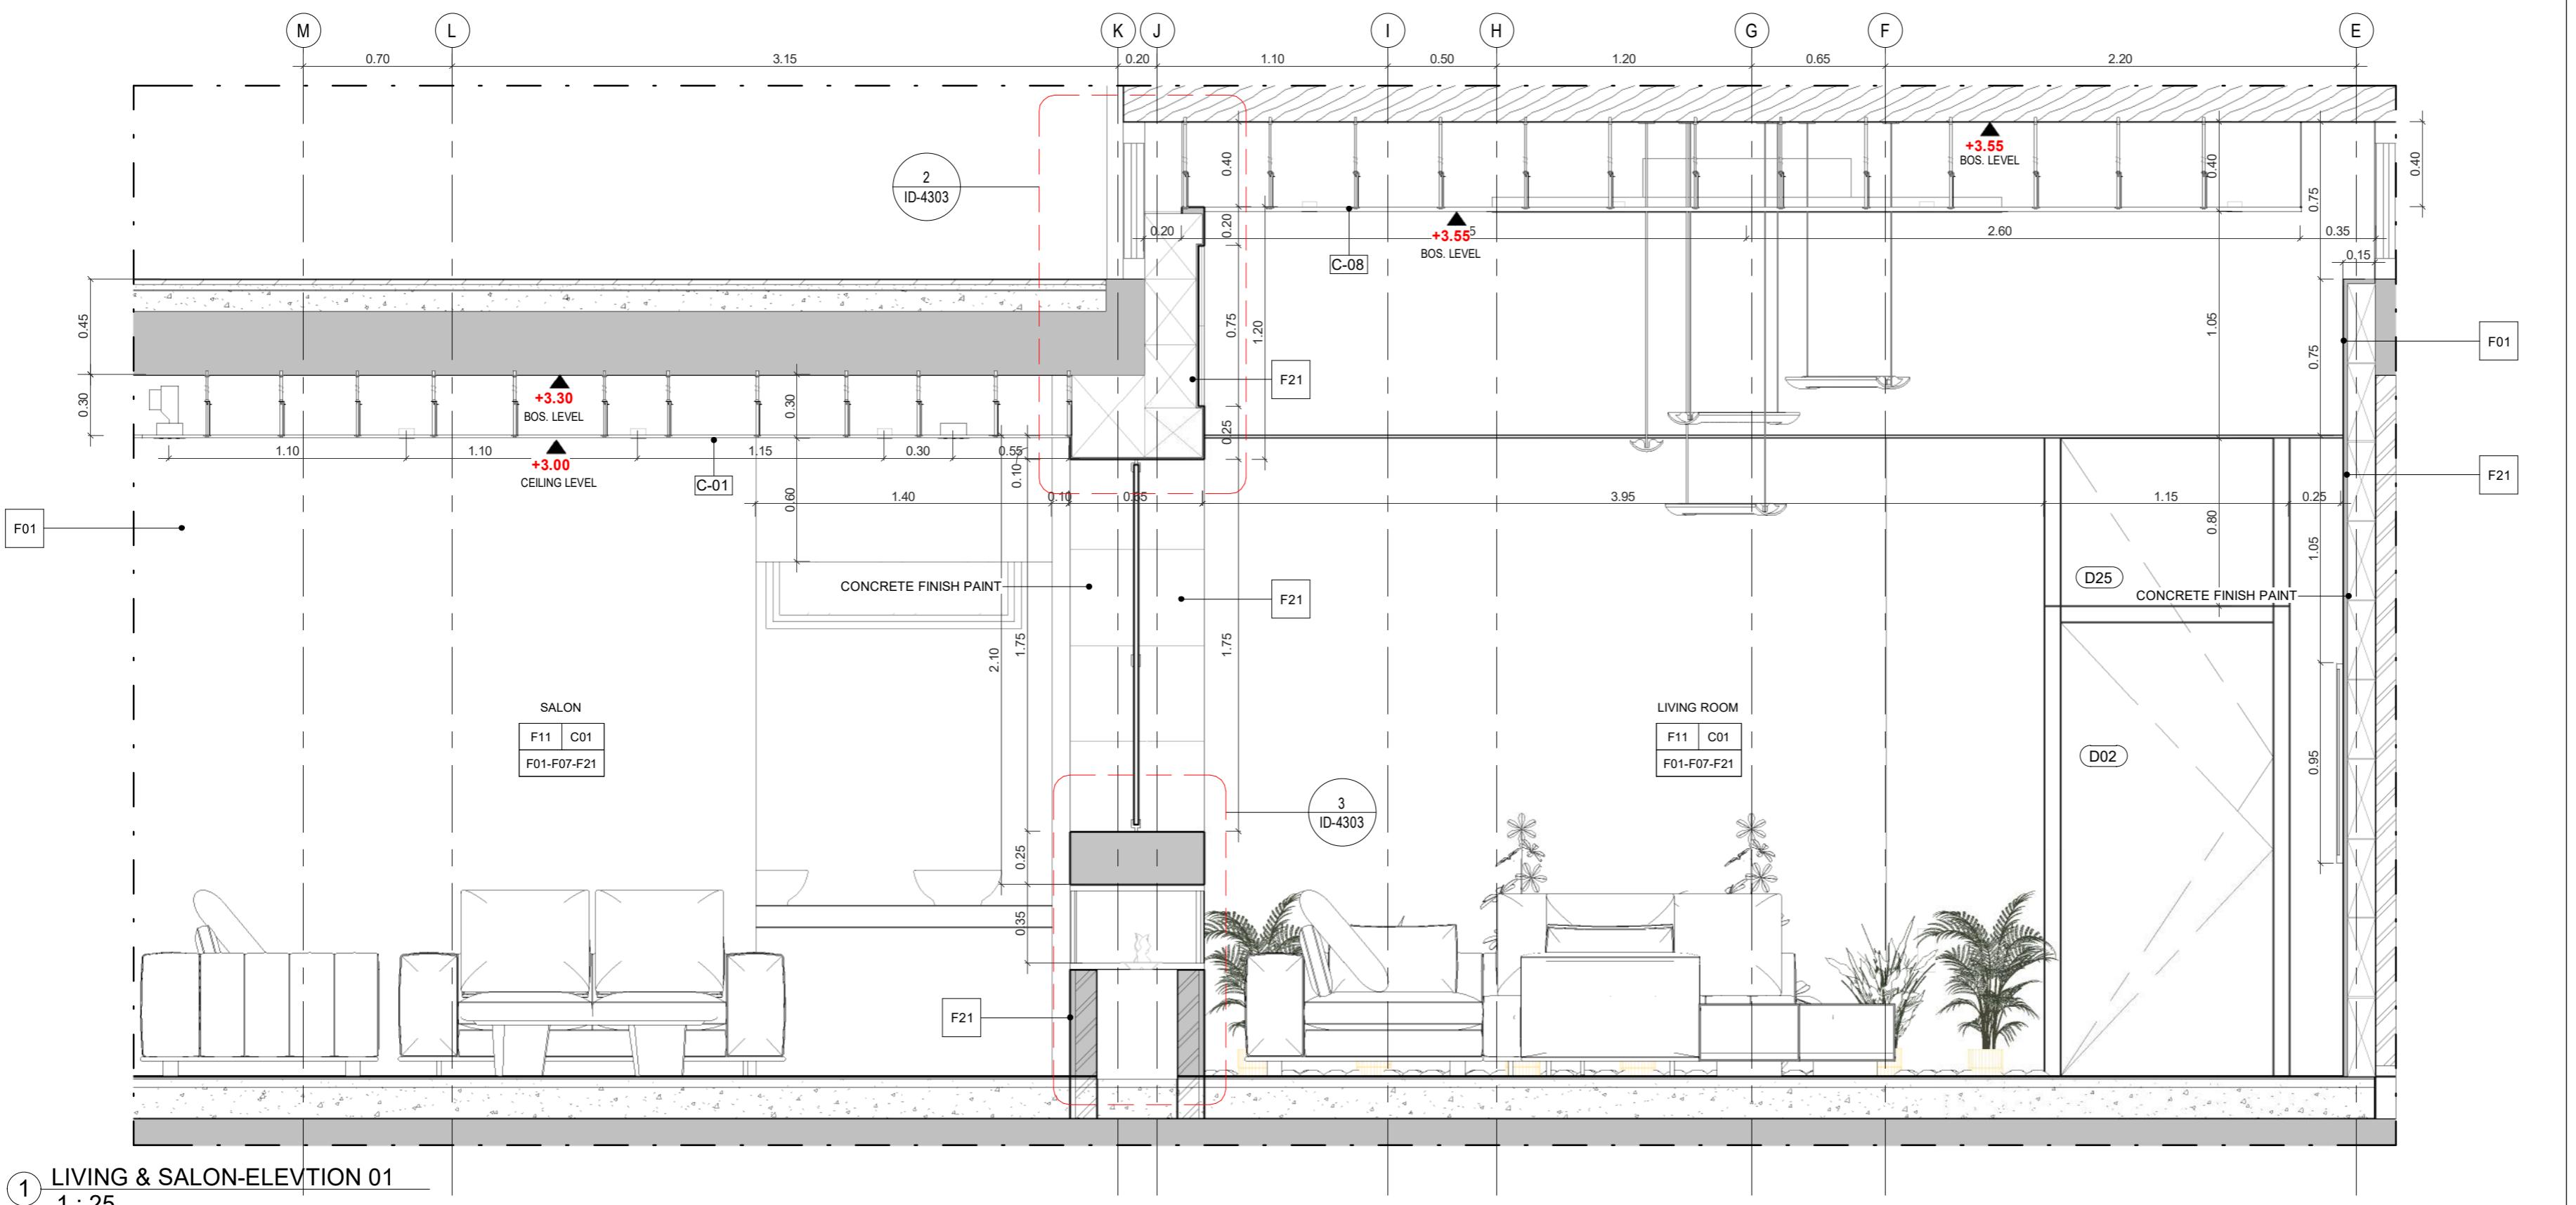


Project Type	Residential
Owner	Khalid Khadir Hasan AL-Saeed
Location	Amman
Plot No.	1659
Basin No.	19
Designed by	A.Shaker Khulief 4809


SHEET NAME
ROOF FLOOR LIVING ROOM
AND SALOON

ID-4303

Date 08/10/2019
Scale As indicated

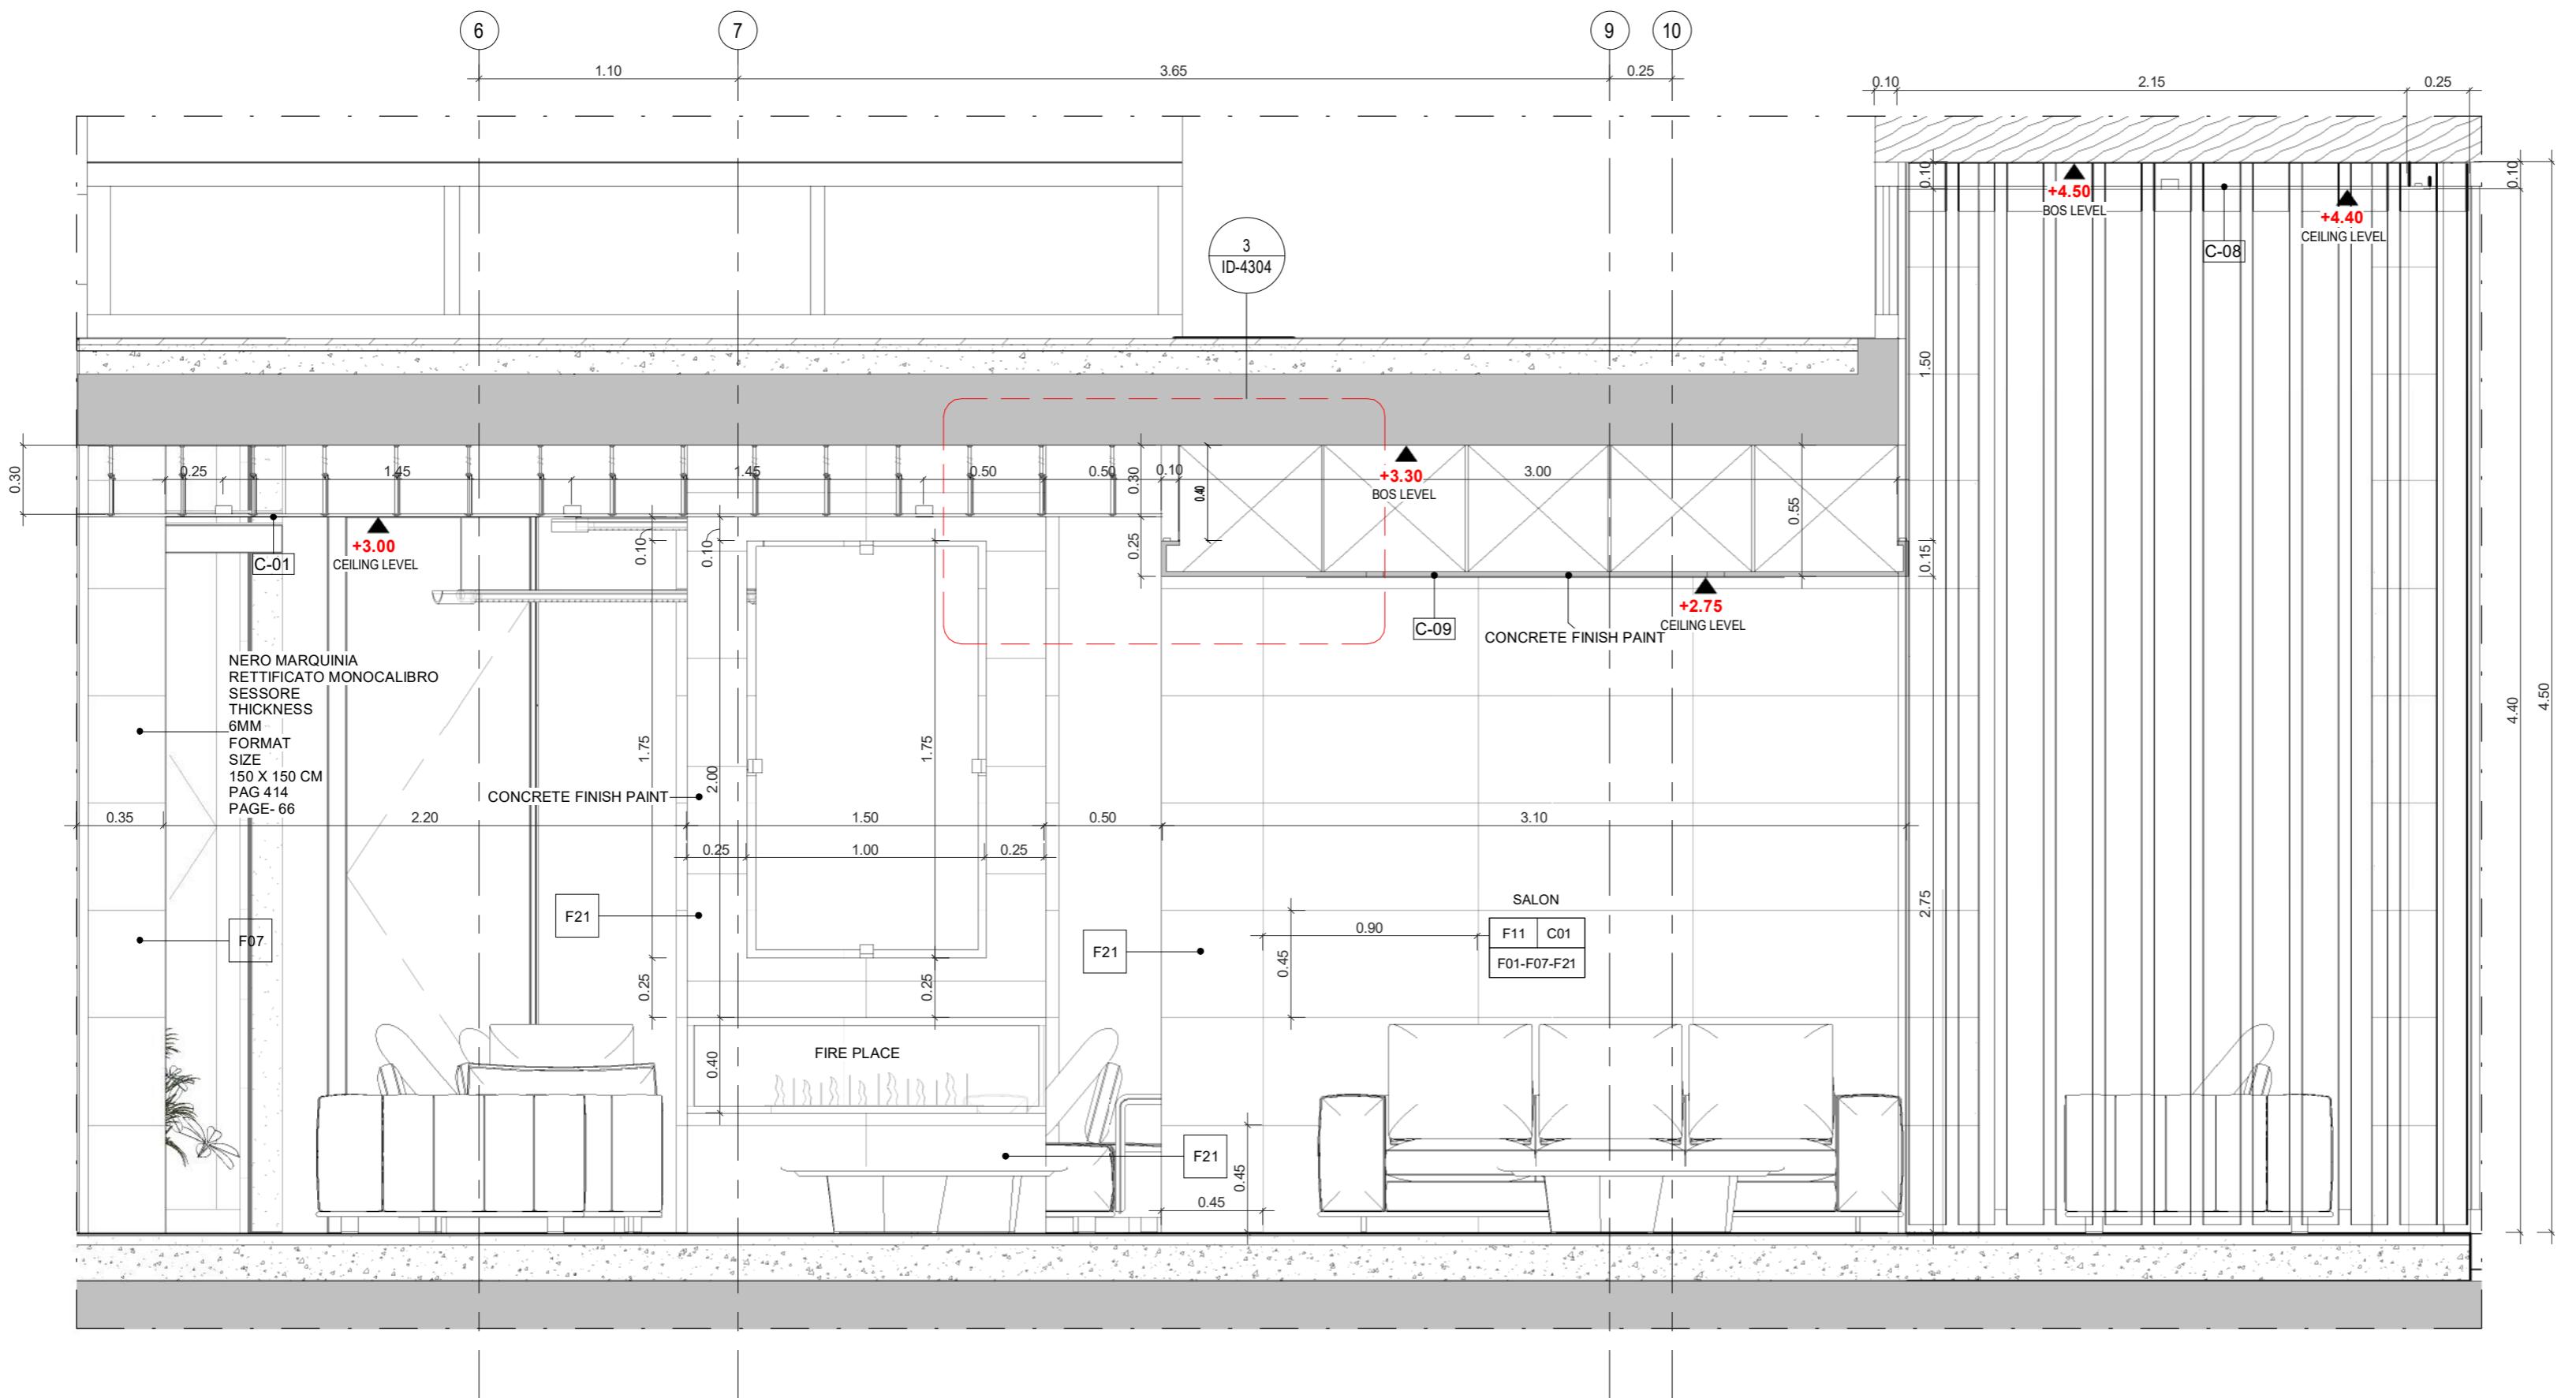

2 LIVING & SALON-ELEVATION 02
1 : 25

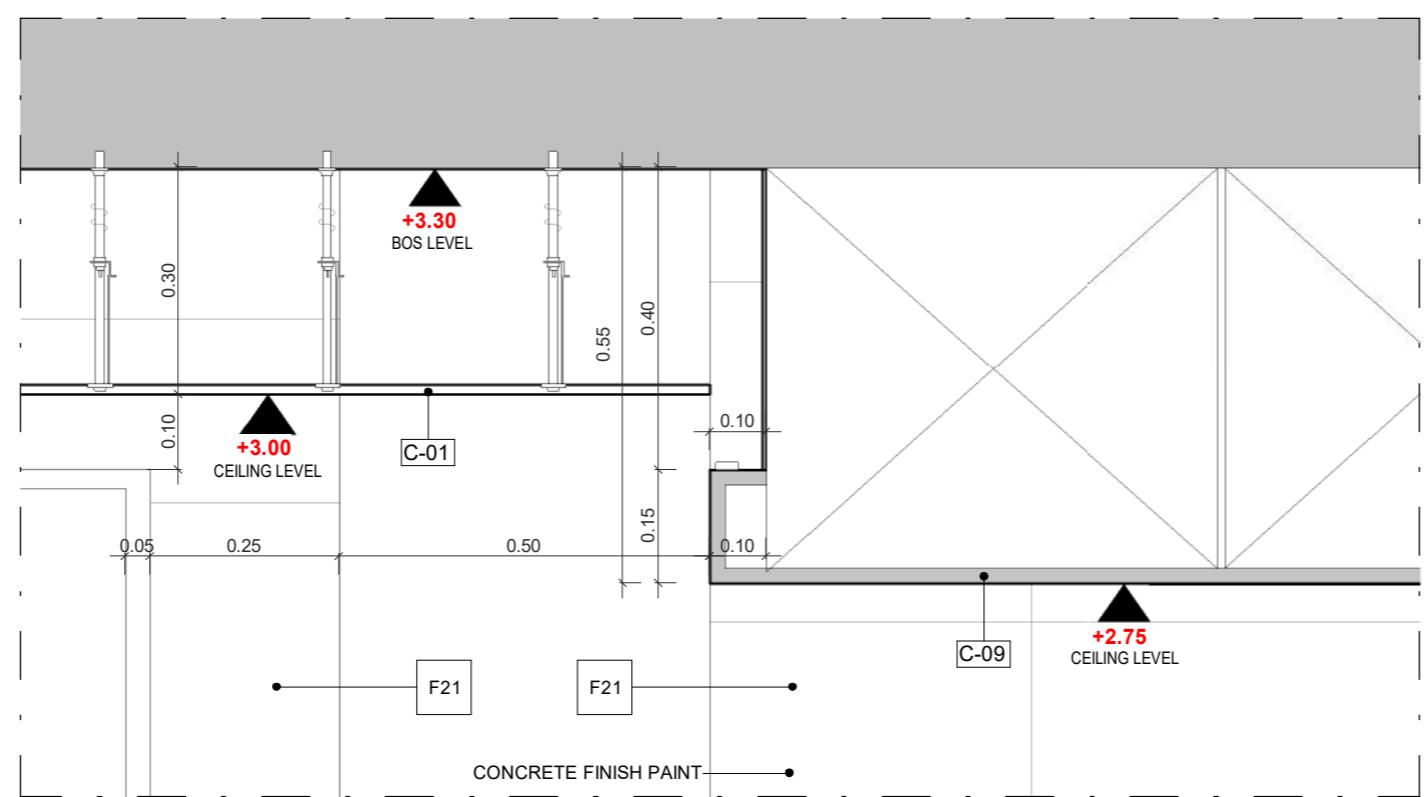

3 DETAIL 03
1 : 10

AL-BOUCA'I
ENGINEERING CONSULTING BUREAU

مكتب البقاعي
للاستشارات الهندسية



BIM Lab

Engineering Services

PROJECT NAME

APARTMENTS BUILDING

NOTES

Project Type	Residential
Owner	Khalid Khadir Hasan AL-Saeed
Location	Amman
Plot No.	1659
Basin No.	19
Designed by	A.Shaker Khulief 4809

**ROOF FLOOR LIVING ROOM
AND SALOON**

ID-4304

Date 08/10/2019
Scale As indicated

PROJECT NAME

APARTMENTS BUILDING

NOTES

FOR FINISHES REFER TO SHEETS:
ID-6000
ID-6001

Project Type	Residential
Owner	Khalid Khadir Hasan AL-Saeed
Location	Amman
Plot No.	1659
Basin No.	19
Designed by	A.Shaker Khulief 4809

SHEET NAME
MASTER BEDROOM -SHOT

ID-4310

Date	08/10/2019
Scale	



PROJECT NAME

APARTMENTS BUILDING

NOTES

FOR FINISHES REFER TO SHEETS:
ID-6000
ID-6001

ROOM NAME

FLOOR FINISH	CEILING FINISH
--------------	----------------

WALL FINISH

FINISHES	FINISHES
FINISH TAG	COMMENTS
F01	
F02	
F03	GOLD STONE
F04	DARK WOOD
F05	DARK WOOD
F06	WOOD
F07	BLACK MARBLE
F08	BEIGE MARBLE
F09	GREY STONE
F10	WALL PAPER
F11	
F12	
F13	BLACK PAINT
F14	CALACATTA
F15	BEIGE PAINT

SPOT RECESSED LIGHT

PENDANT LIGHT

HIDDEN LIGHT

CHANDELIER

WALL MOUNTED

NEON RECTANGULAR

Project Type	Residential
Owner	Khalid Khadir Hasan AL-Saeed
Location	Amman
Plot No.	1659
Basin No.	19
Designed by	A.Shaker Khulief 4809


SHEET NAME

ROOF FLOOR MASTER BEDROOM PLAN

ID-4311

Date 08/10/2019

Scale As indicated

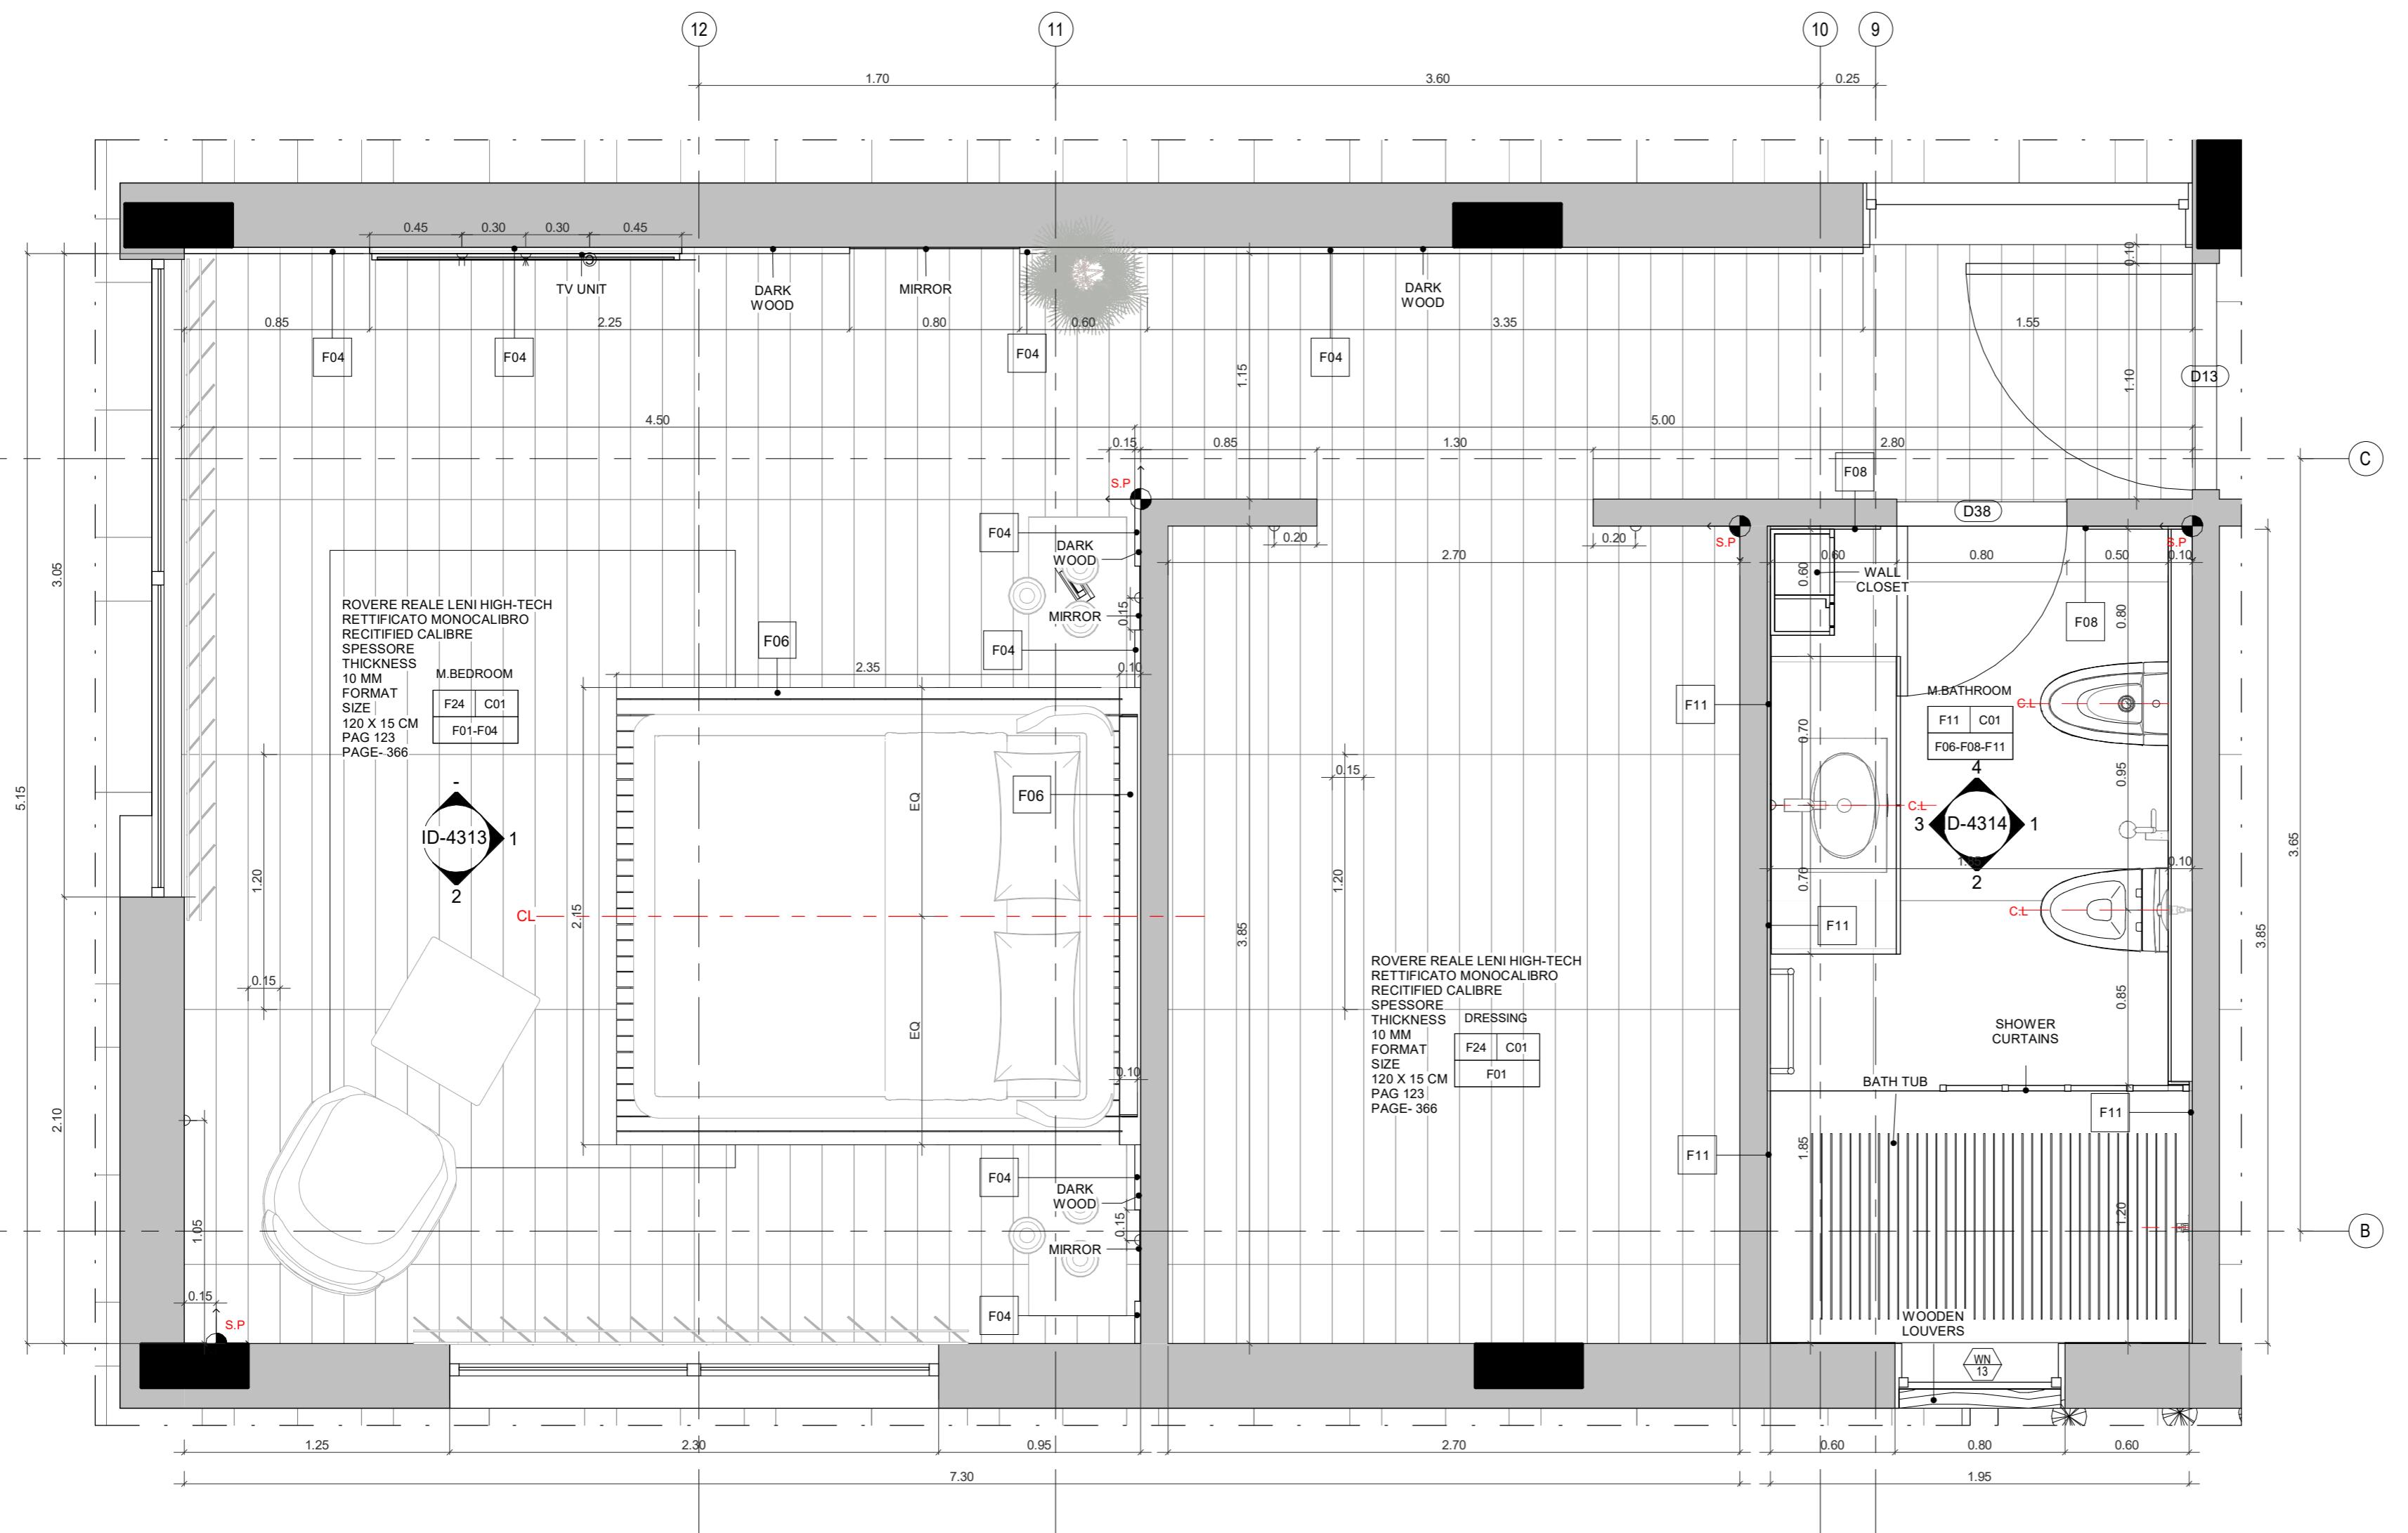

PROJECT NAME

APARTMENTS BUILDING

NOTES

FOR FINISHES REFER TO SHEETS:
ID-6000
ID-6001

ROOM NAME

FLOOR FINISH	CEILING FINISH
--------------	----------------

WALL FINISH




FINISHES		FINISHES	
FINISH TAG	COMMENTS	FINISH TAG	COMMENTS
F01		F16	
F02		F17	LEATHER
F03	GOLD STONE	F18	PAINT-GOLD METAL EFFECT
F04	DARK WOOD	F19	
F05	DARK WOOD	F20	GREY STONE
F06	WOOD	F21	CONCRETE FINISH
F07	BLACK MARBLE	F09	GREY STONE
F08	BEIGE MARBLE	F10	WALL PAPER
F09		F11	
F10		F12	
F11		F13	BLACK PAINT
F12		F14	CALACATTA
F13		F15	BEIGE PAINT
F14		F16	
F15		F17	
F16		F18	
F17		F19	
F18		F20	
F19		F21	
F20		F09	
F21		F10	
F22		F11	
F23		F12	
		F13	
		F14	
		F15	
		F16	
		F17	
		F18	
		F19	
		F20	
		F21	
		F09	
		F10	
		F11	
		F12	
		F13	
		F14	
		F15	
		F16	
		F17	
		F18	
		F19	
		F20	
		F21	
		F09	
		F10	
		F11	
		F12	
		F13	
		F14</td	

PROJECT NAME

APARTMENTS BUILDING

NOTES

FOR FINISHES REFER TO SHEETS:
ID-6000
ID-6001

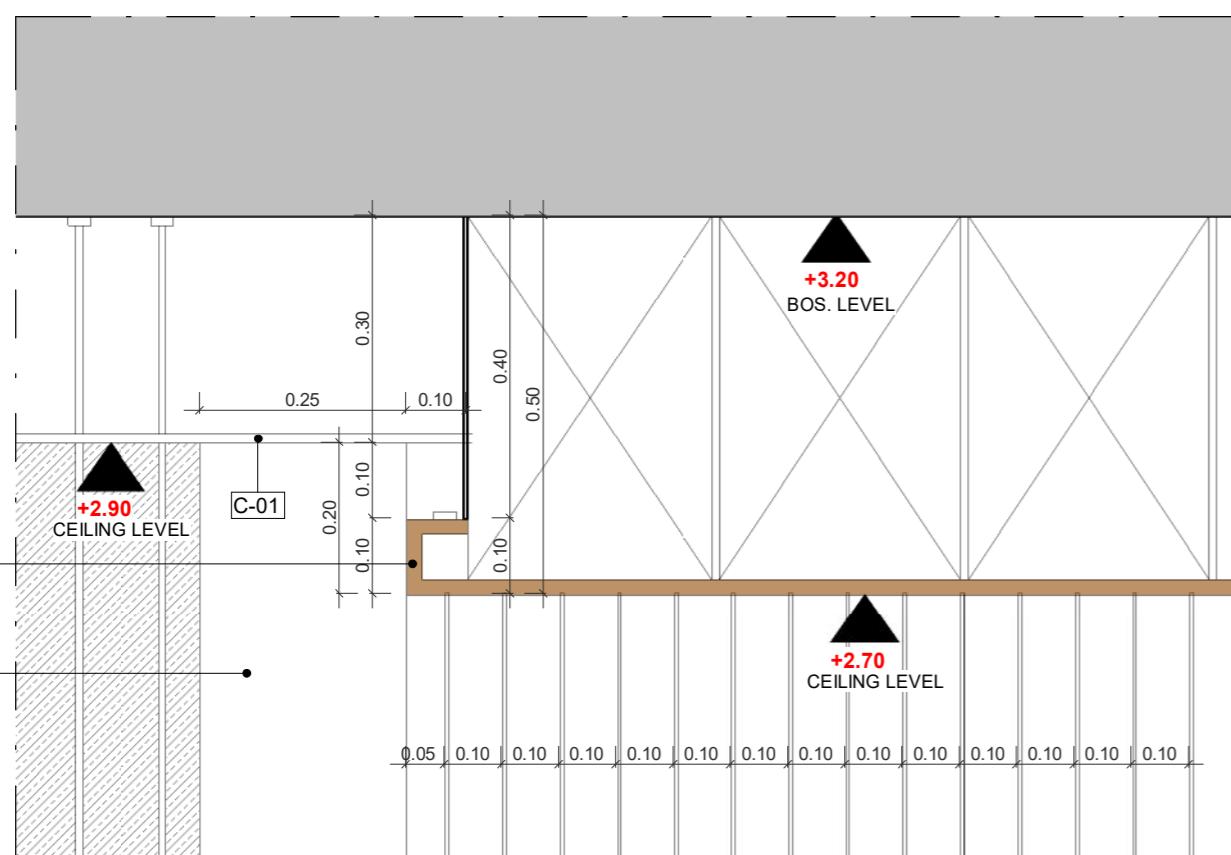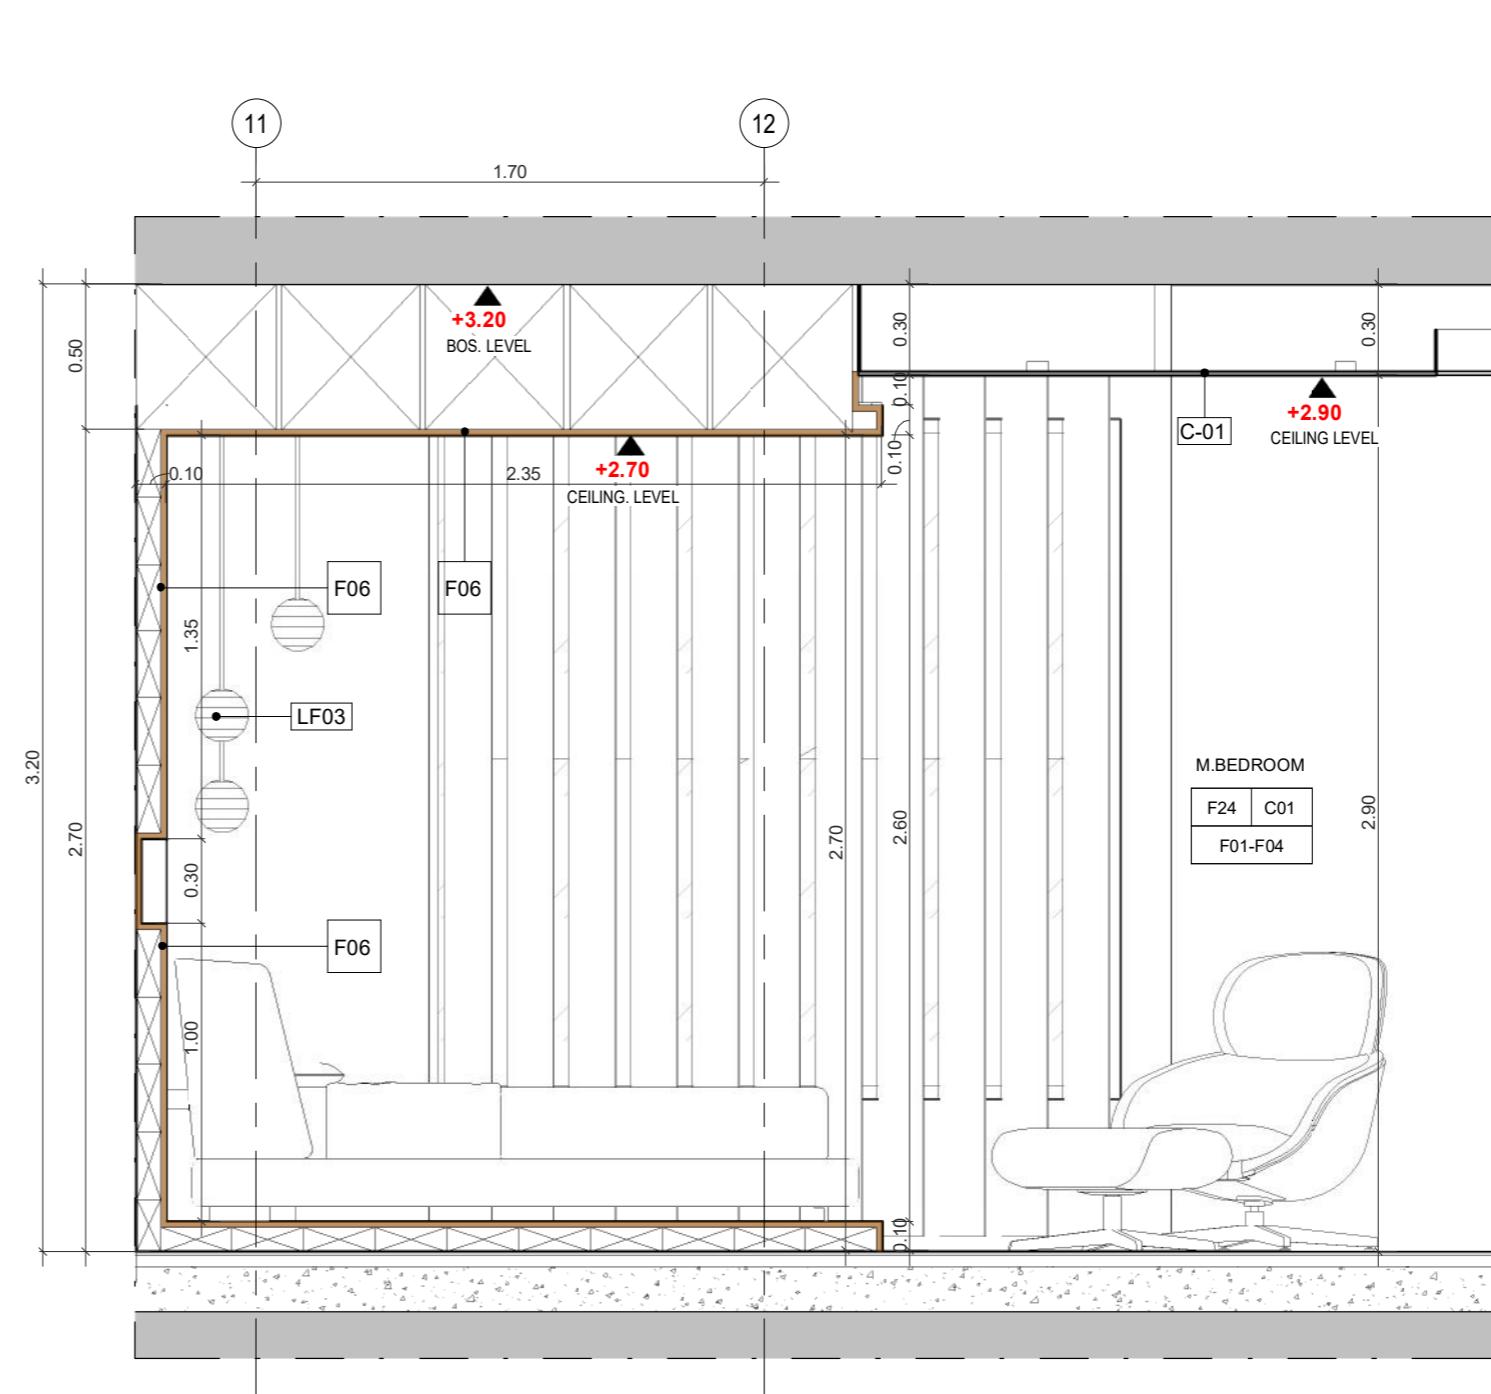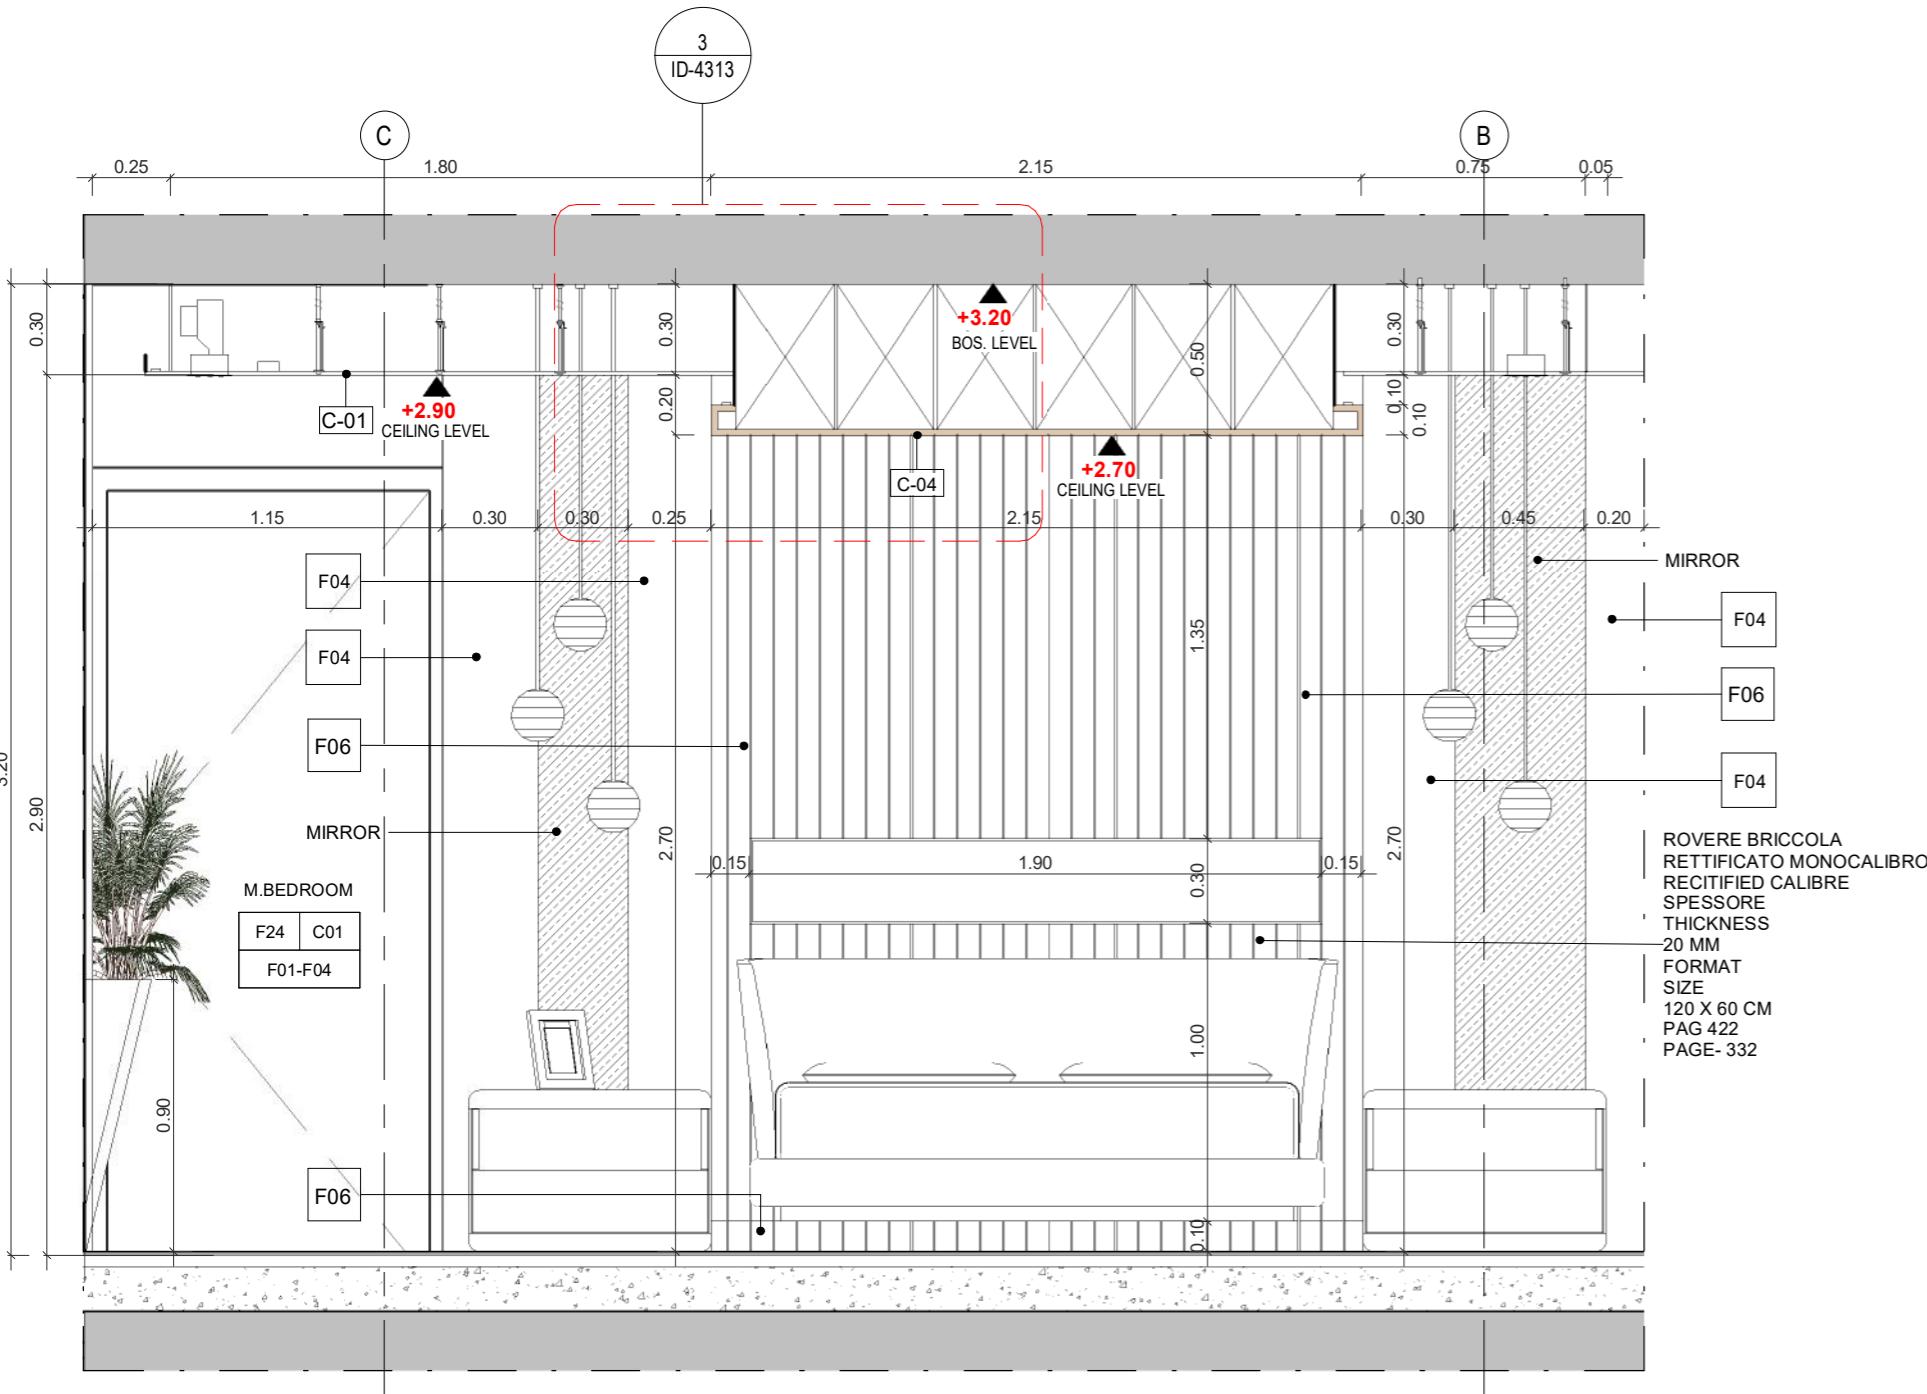

Project Type	Residential
Owner	Khalid Khadir Hasan AL-Saeed
Location	Amman
Plot No.	1659
Basin No.	19
Designed by	A.Shaker Khulief 4809

SHEET NAME
**ROOF FLOOR MASTER
BEDROOM
ELEVATIONS-PART 01**

ID-4313

Date 08/10/2019
Scale As indicated





BIM Lab
Engineering Services

PROJECT NAME

NOTES

FOR FINISHES REFER TO SHEETS:
ID-6000
ID-6001

ROOM NAME

FLOOR FINISH CEILING FINISH

WALL FINISH

FINISHES	
FINISH TAG	COMMENTS
F01	
F02	
F03	GOLD STONE
F04	DARK WOOD
F05	DARK WOOD
F06	WOOD
F07	BLACK MARBLE
F08	BEIGE MARBLE
F09	GREY STONE
F10	WALL PAPER
F11	
F12	
F13	BLACK PAINT
F14	CALACATTA
F15	BEIGE PAINT
FINISHES	
FINISH TAG	COMMENTS
F16	
F17	LEATHER
F18	PAINT-GOLD METAL EFFECT
F19	
F20	GREY STONE
F21	CONCRETE FINISH
F22	
F23	SWIMMING POOL WALL FINISHES


Project Type	Residential
Owner	Khalid Khadir Hasan AL-Saeed
Location	Amman
Plot No.	1659
Basin No.	19
Designed by	A.Shaker Khulief 4809

SHEET NAME

**ROOF FLOOR MASTER
BEDROOM
ELEVATIONS-PART 02**


ID-4314

Date 08/10/2019
Scale 1 : 25

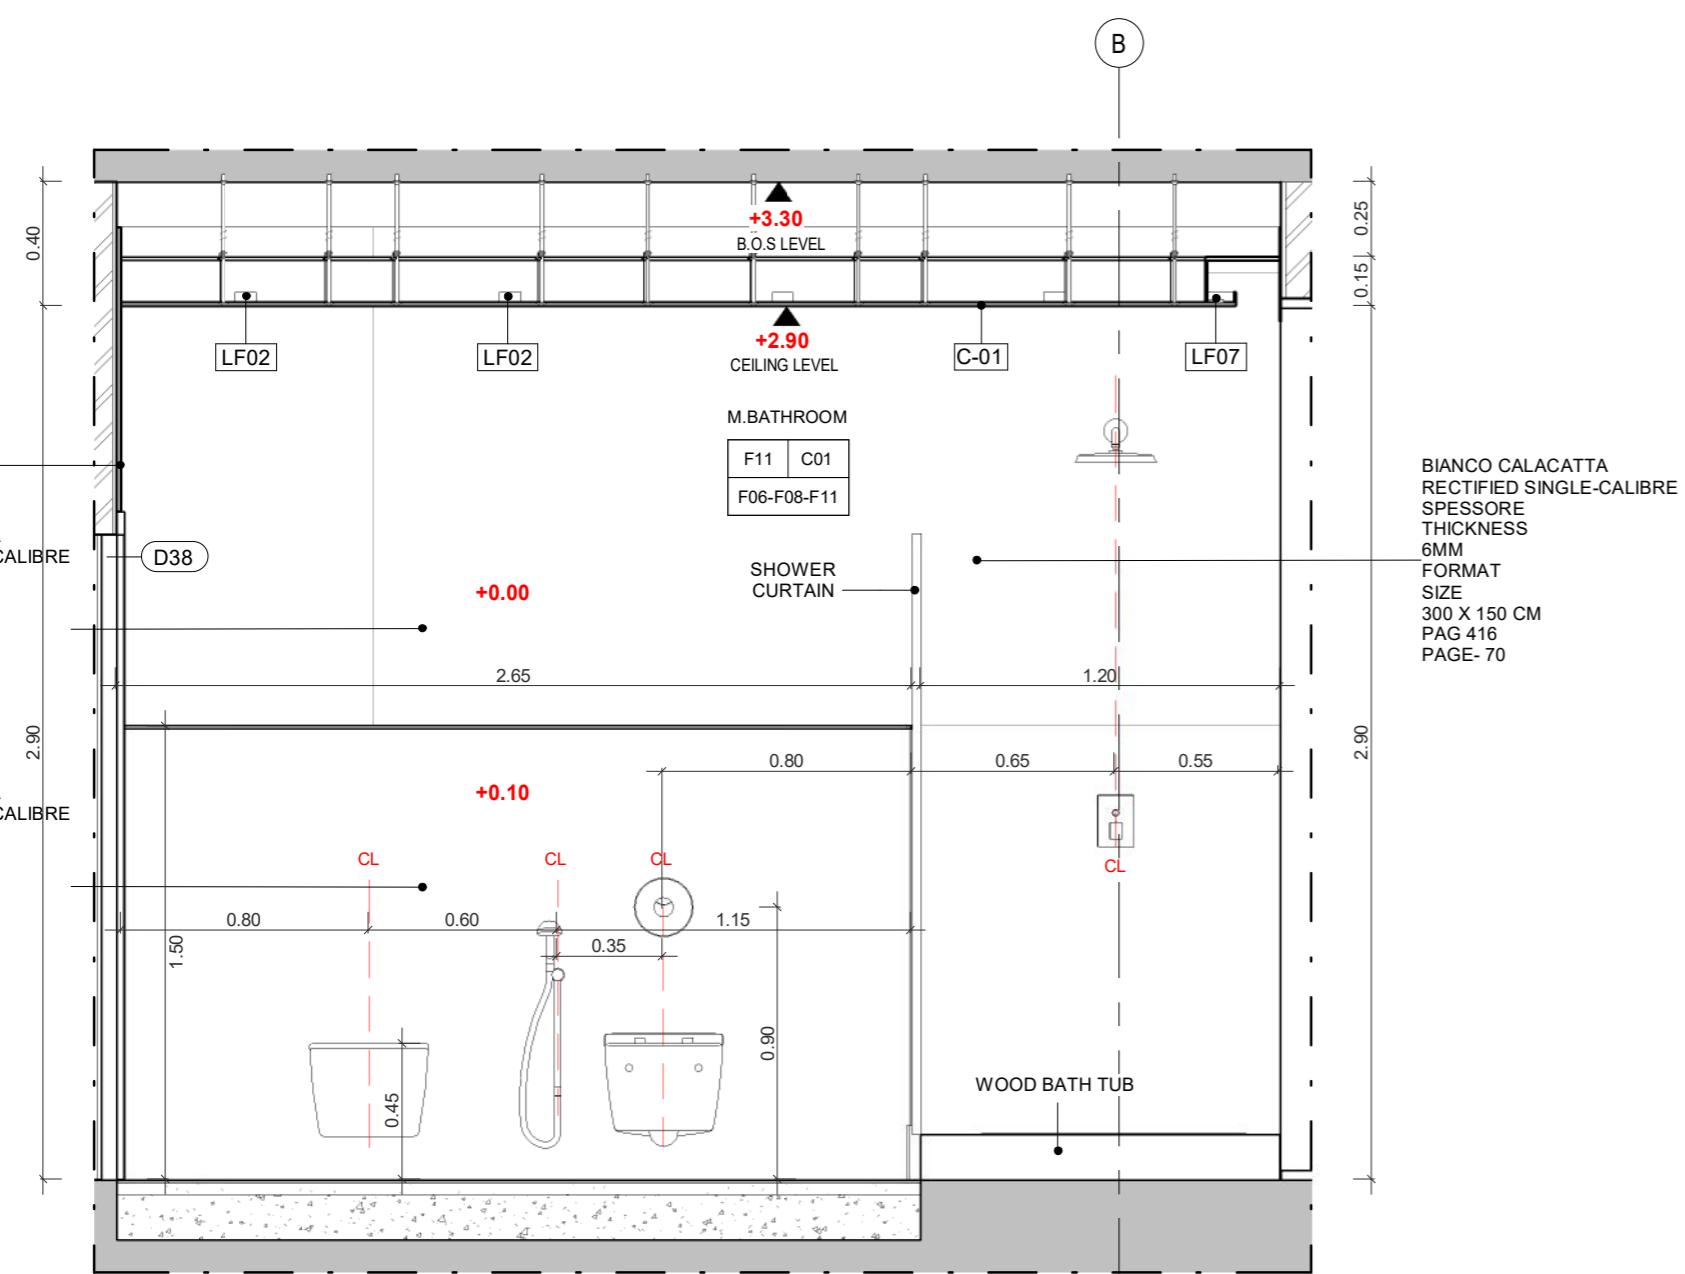


MASTER BATHROOM-ELEVATION 01

1 : 25

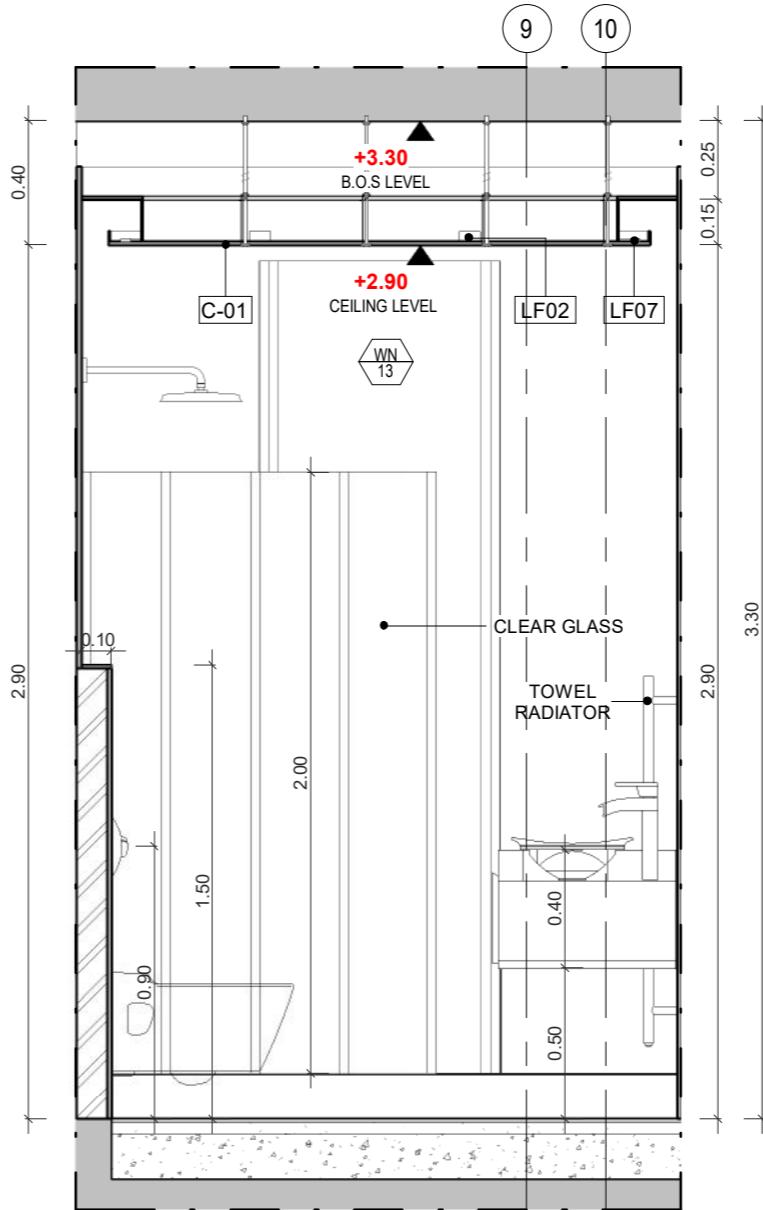


MASTER BATHROOM-ELEVATION 02

1 : 25

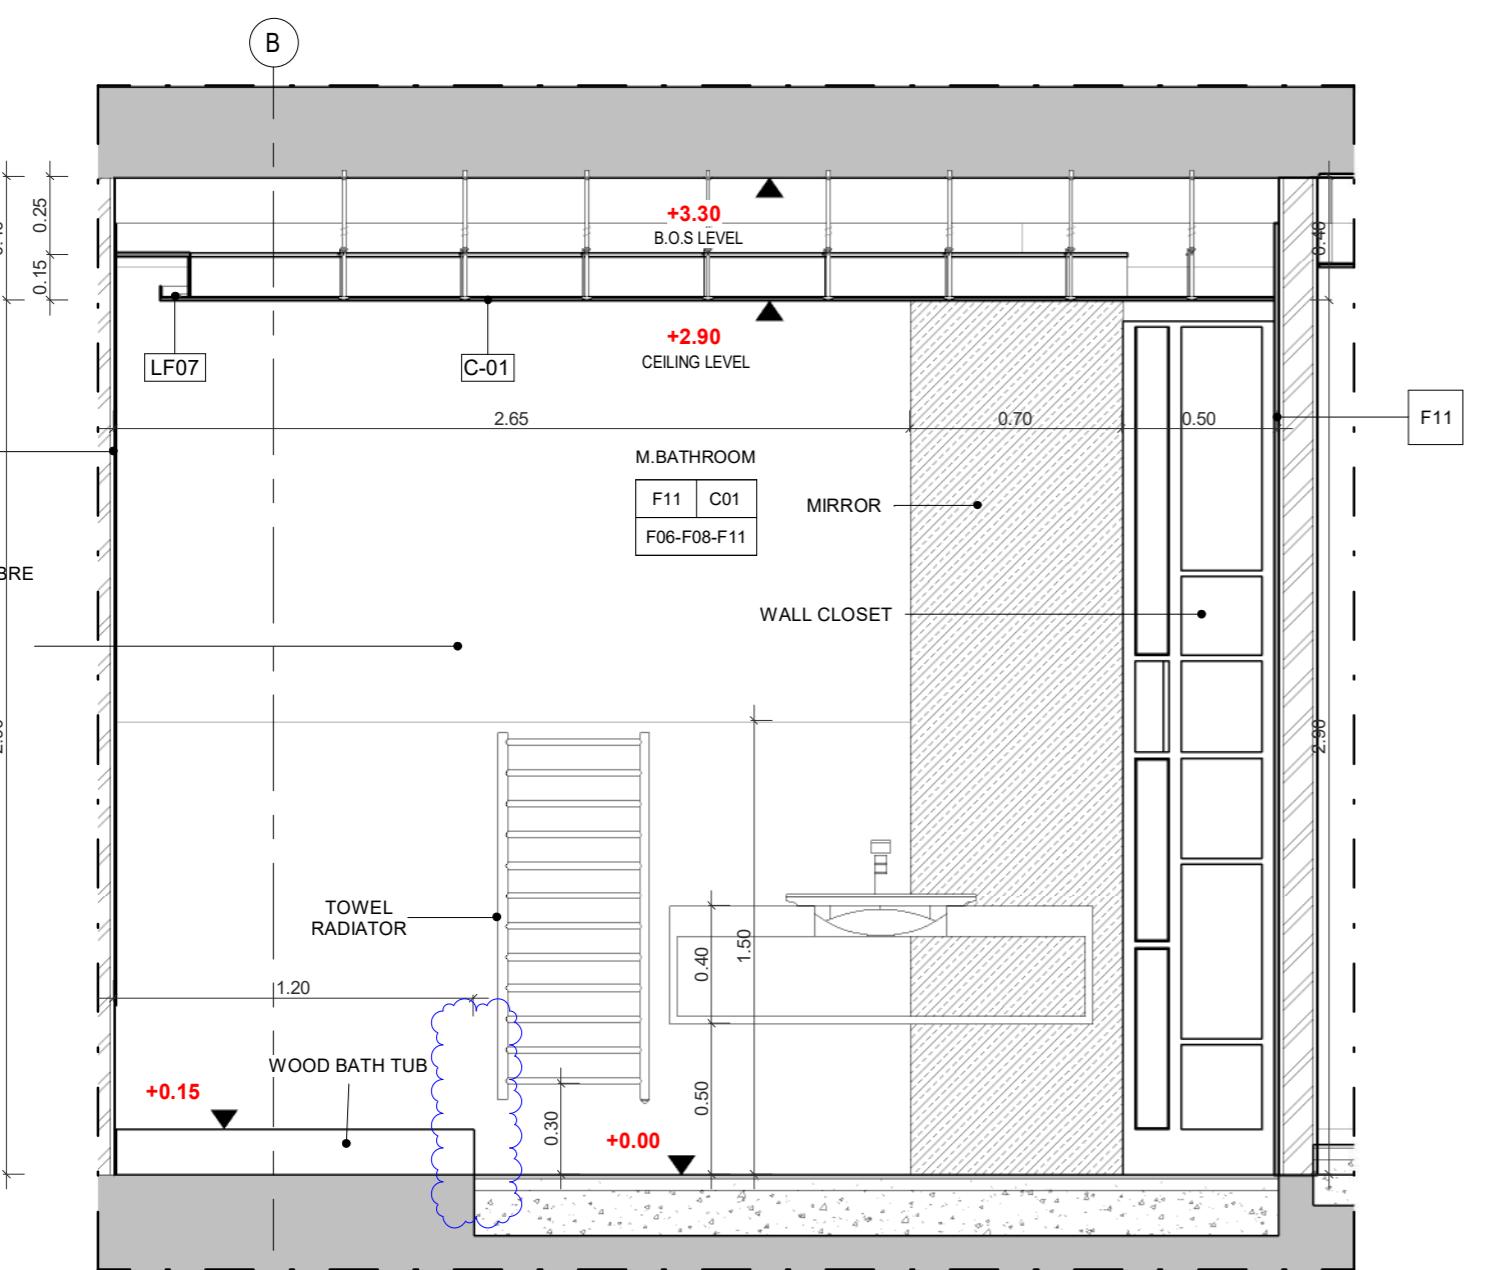

MASTER BATHROOM-ELEVATION 03

3
1 : 25

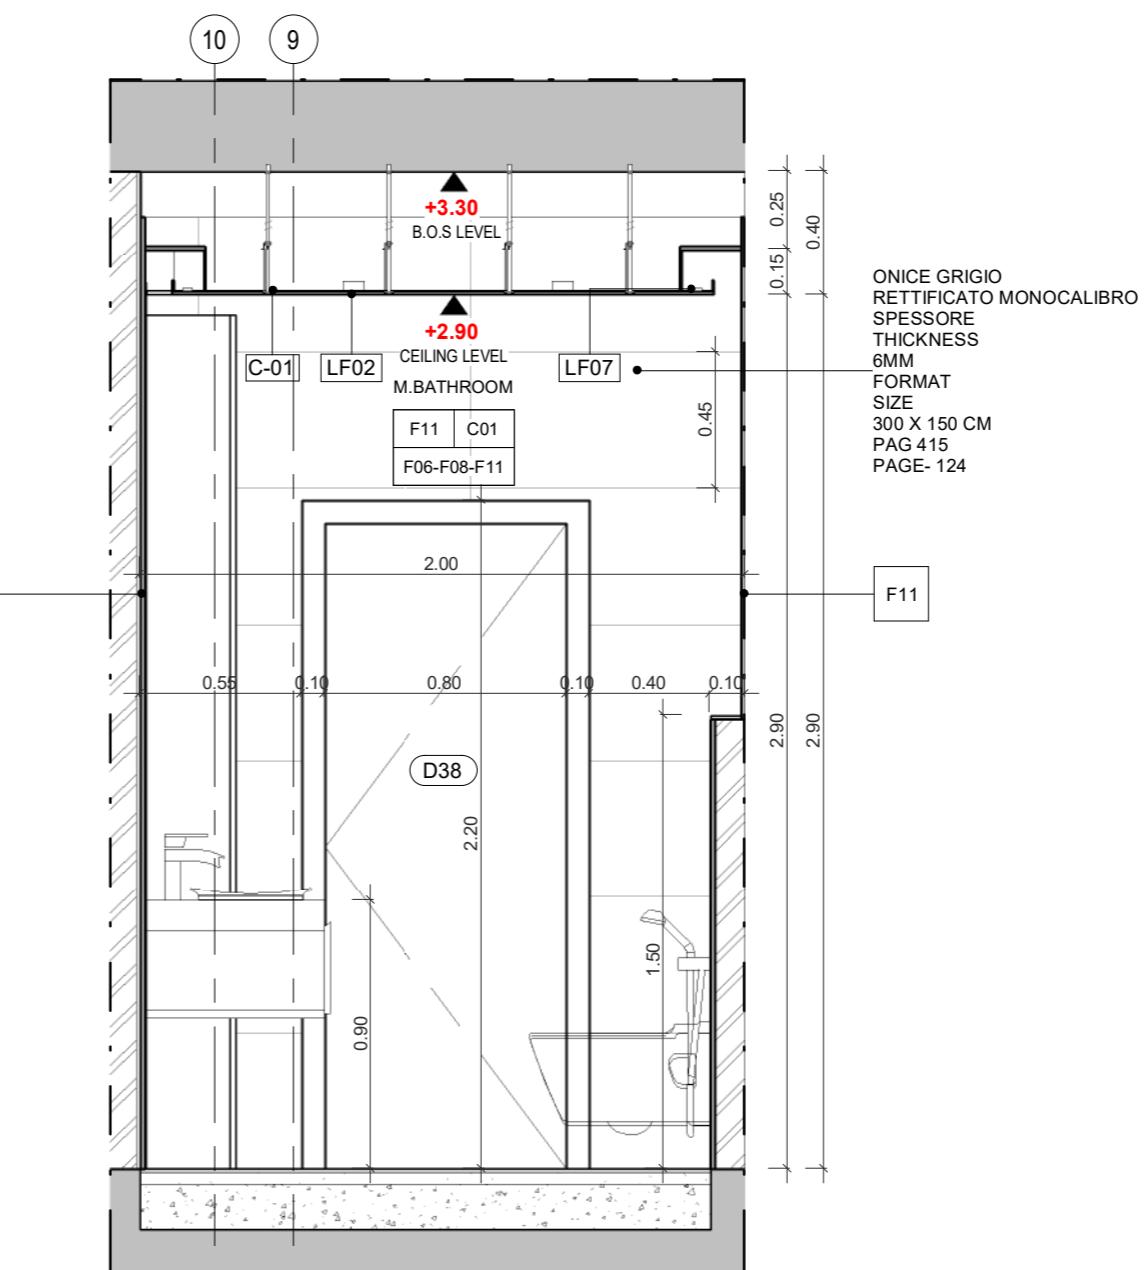

4 MASTER BATHROOM-ELEVATION 04

4 1 : 25

PROJECT NAME

APARTMENTS BUILDING

NOTES

FOR FINISHES REFER TO SHEETS:
ID-6000
ID-6001

ROOM NAME

FLOOR FINISH	CEILING FINISH
--------------	----------------

WALL FINISH

FINISHES		FINISHES	
FINISH TAG	COMMENTS	FINISH TAG	COMMENTS
F01		F16	
F02		F17	LEATHER
F03	GOLD STONE	F18	PAINT-GOLD METAL EFFECT
F04	DARK WOOD	F19	
F05	DARK WOOD	F20	GREY STONE
F06	WOOD	F21	CONCRETE FINISH
F07	BLACK MARBLE	F22	
F08	BEIGE MARBLE	F23	SWIMMING POOL WALL FINISHES
F09	GREY STONE	F10	WALL PAPER
F11		F11	
F12		F12	
F13	BLACK PAINT	F13	
F14	CALACATTA	F14	
F15	BEIGE PAINT	F15	

SPOT RECESSED LIGHT

PENDANT LIGHT

HIDDEN LIGHT

CHANDELIER

WALL MOUNTED

NEON RECTANGULAR

Project Type	Residential
Owner	Khalid Khadir Hasan AL-Saeed
Location	Amman
Plot No.	1659
Basin No.	19
Designed by	A.Shaker Khulief 4809

SHEET NAME



ROOF FLOOR BATHROOM

ID-4320


Date 08/10/2019

Scale As indicated



① TILING PLAN-BATHROOM
1 : 25

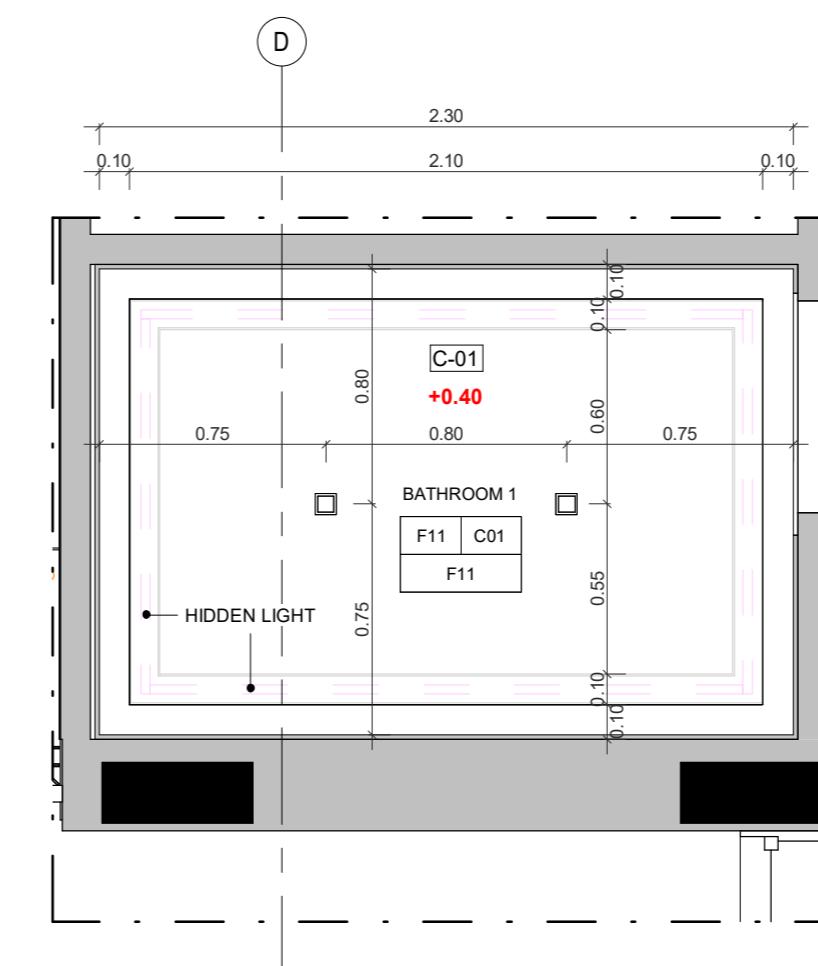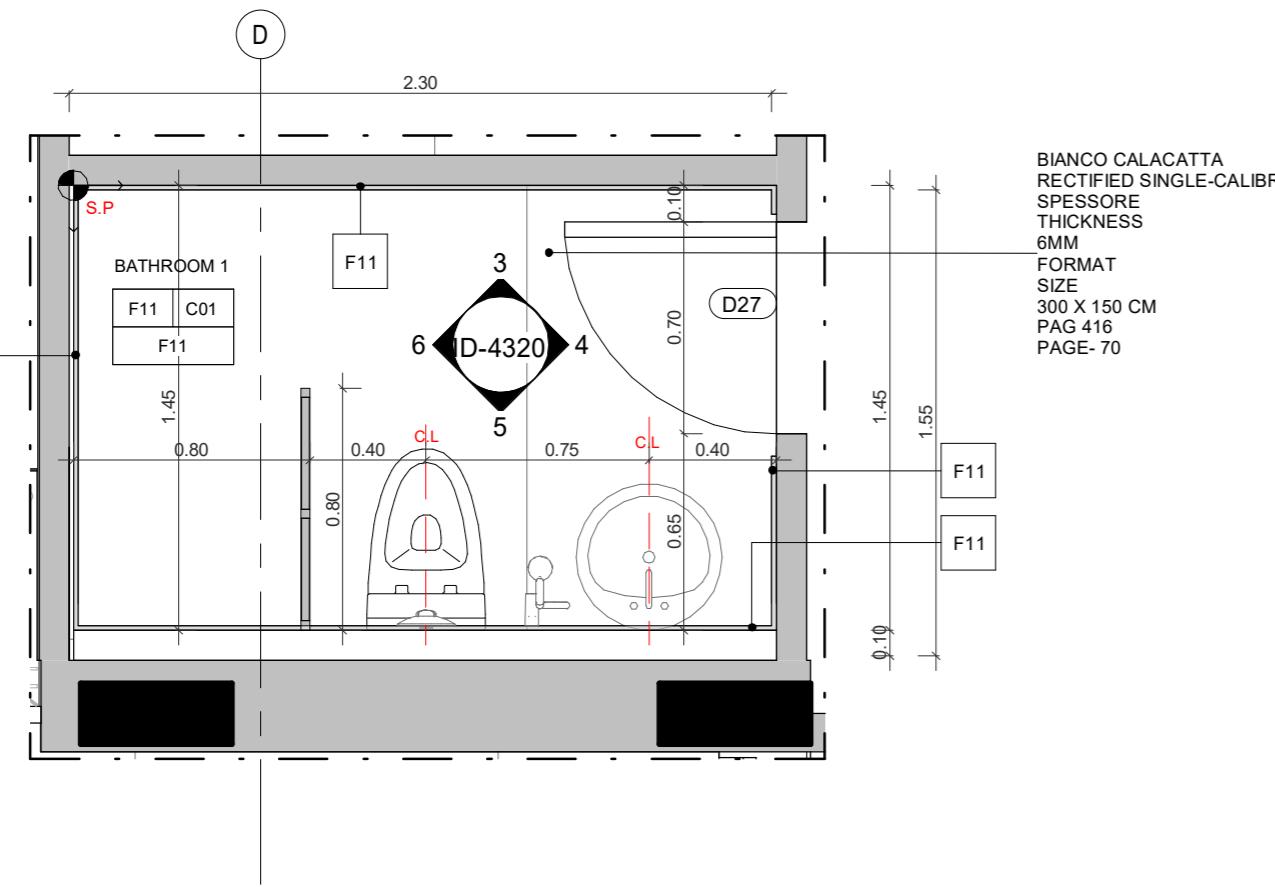

② CEILING PLAN-BATHROOM
1 : 25

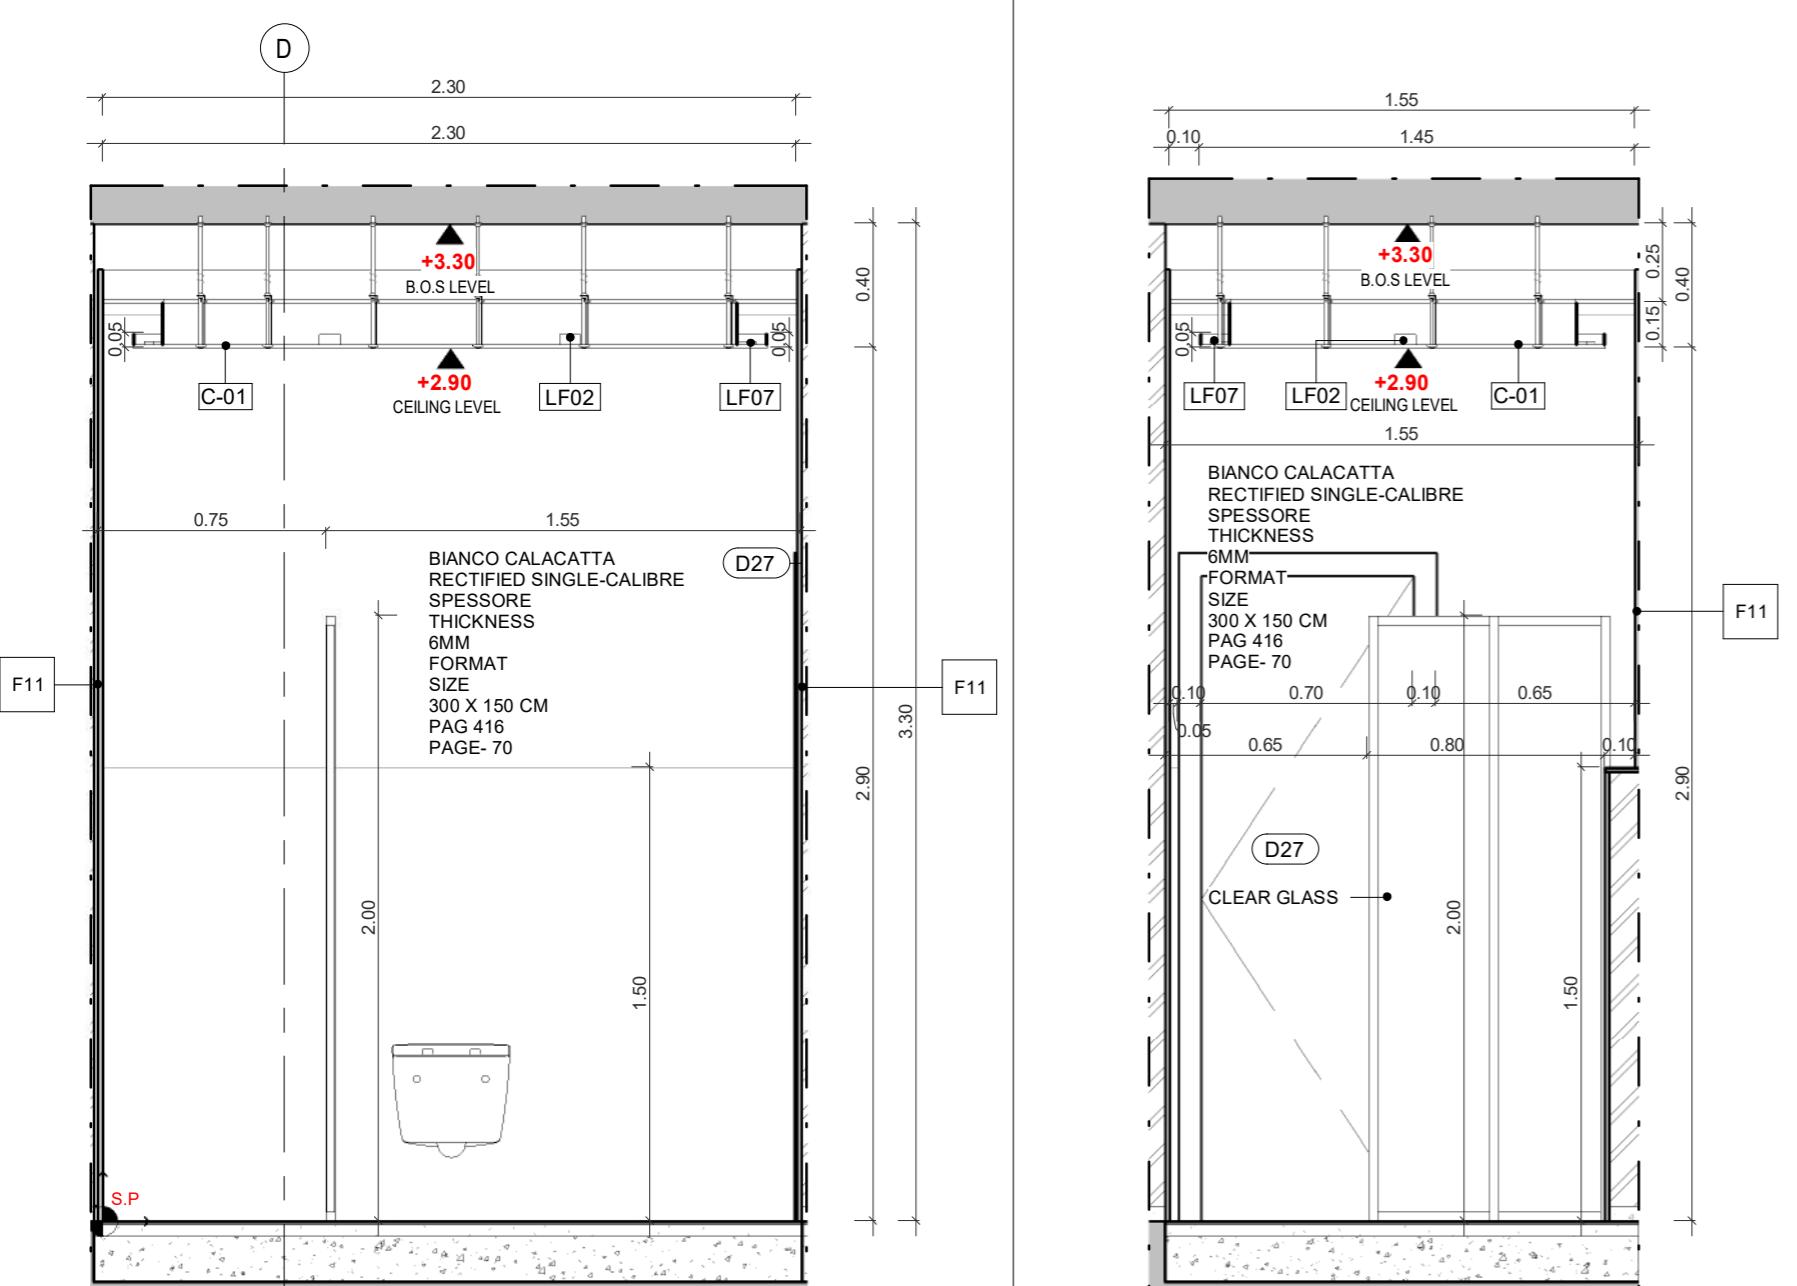

③ BATHROOM-ELEVATION 01
1 : 25

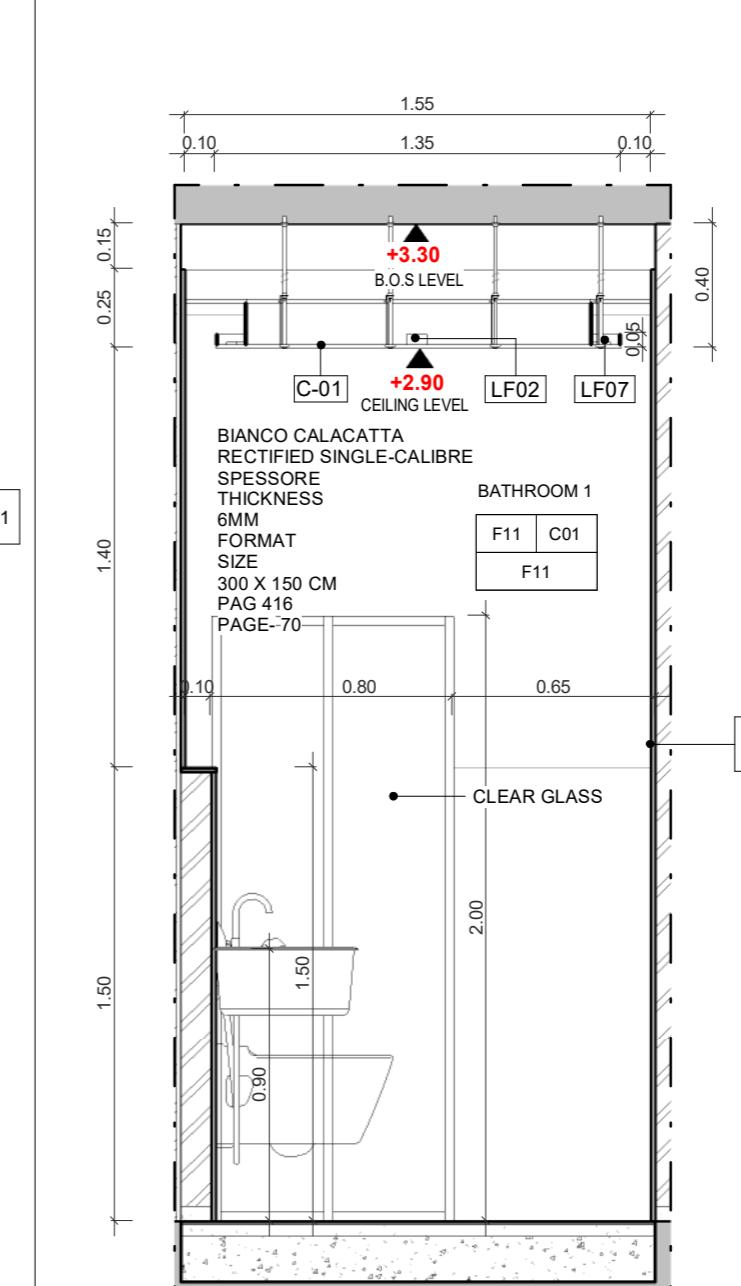
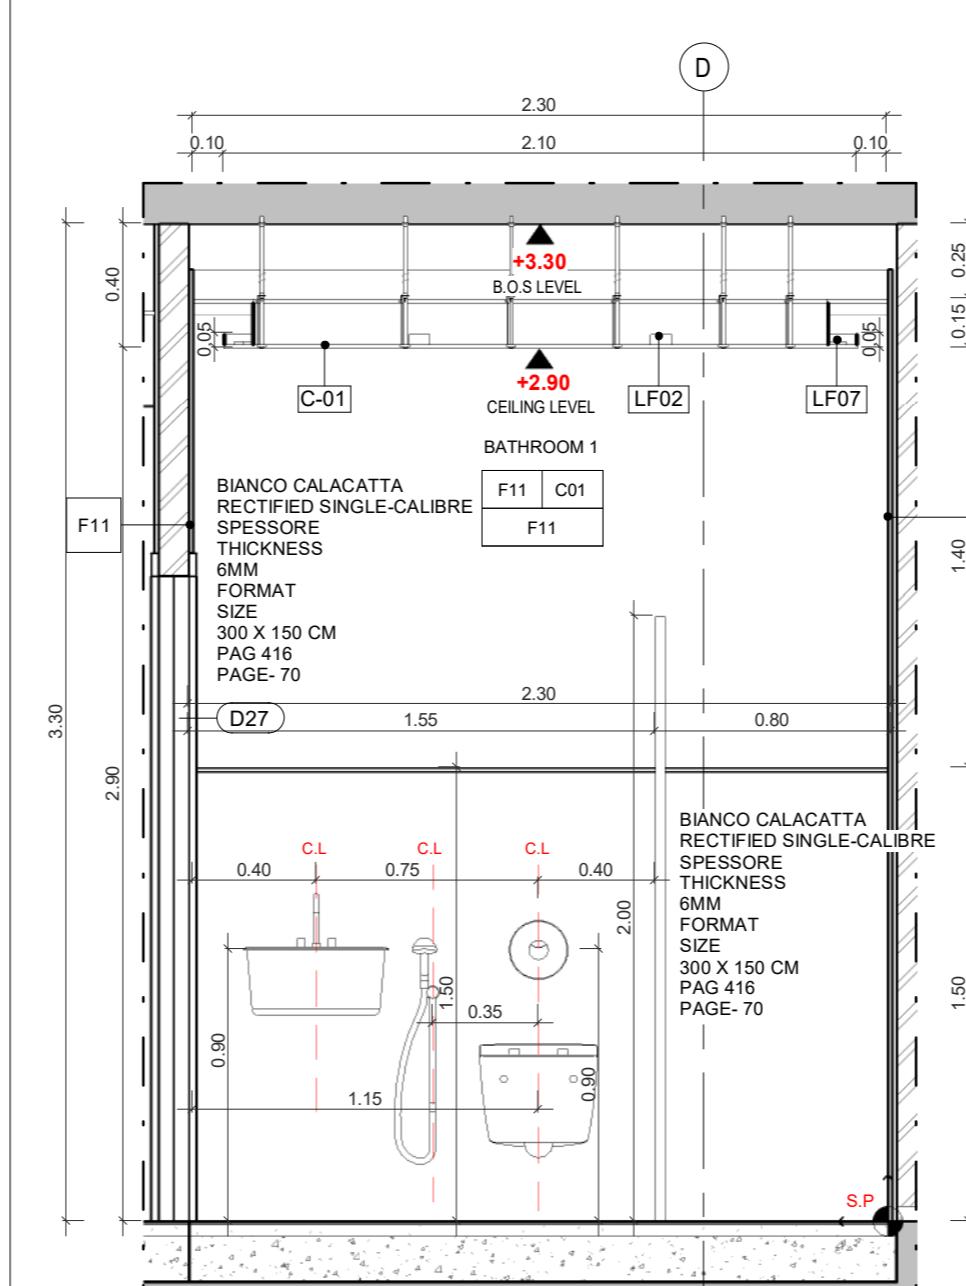


④ BATHROOM-ELEVATION 02
1 : 25

⑤ BATHROOM-ELEVATION 03
1 : 25

⑥ BATHROOM-ELEVATION 04
1 : 25

PROJECT NAME																																			
APARTMENTS BUILDING																																			
NOTES																																			
FOR FINISHES REFER TO SHEETS: ID-6000 ID-6001																																			
ROOM NAME																																			
FLOOR FINISH	CEILING FINISH																																		
WALL FINISH																																			
<table border="1"> <thead> <tr> <th colspan="2">FINISHES</th> </tr> <tr> <th>FINISH TAG</th> <th>COMMENTS</th> </tr> </thead> <tbody> <tr><td>F01</td><td></td></tr> <tr><td>F02</td><td></td></tr> <tr><td>F03</td><td>GOLD STONE</td></tr> <tr><td>F04</td><td>DARK WOOD</td></tr> <tr><td>F05</td><td>DARK WOOD</td></tr> <tr><td>F06</td><td>WOOD</td></tr> <tr><td>F07</td><td>BLACK MARBLE</td></tr> <tr><td>F08</td><td>BEIGE MARBLE</td></tr> <tr><td>F09</td><td>GREY STONE</td></tr> <tr><td>F10</td><td>WALL PAPER</td></tr> <tr><td>F11</td><td></td></tr> <tr><td>F12</td><td></td></tr> <tr><td>F13</td><td>BLACK PAINT</td></tr> <tr><td>F14</td><td>CALACATTA</td></tr> <tr><td>F15</td><td>BEIGE PAINT</td></tr> </tbody> </table>		FINISHES		FINISH TAG	COMMENTS	F01		F02		F03	GOLD STONE	F04	DARK WOOD	F05	DARK WOOD	F06	WOOD	F07	BLACK MARBLE	F08	BEIGE MARBLE	F09	GREY STONE	F10	WALL PAPER	F11		F12		F13	BLACK PAINT	F14	CALACATTA	F15	BEIGE PAINT
FINISHES																																			
FINISH TAG	COMMENTS																																		
F01																																			
F02																																			
F03	GOLD STONE																																		
F04	DARK WOOD																																		
F05	DARK WOOD																																		
F06	WOOD																																		
F07	BLACK MARBLE																																		
F08	BEIGE MARBLE																																		
F09	GREY STONE																																		
F10	WALL PAPER																																		
F11																																			
F12																																			
F13	BLACK PAINT																																		
F14	CALACATTA																																		
F15	BEIGE PAINT																																		
<table border="1"> <thead> <tr> <th colspan="2">FINISHES</th> </tr> <tr> <th>FINISH TAG</th> <th>COMMENTS</th> </tr> </thead> <tbody> <tr><td>F16</td><td></td></tr> <tr><td>F17</td><td>LEATHER</td></tr> <tr><td>F18</td><td>PAINT-GOLD METAL EFFECT</td></tr> <tr><td>F19</td><td></td></tr> <tr><td>F20</td><td>GREY STONE</td></tr> <tr><td>F21</td><td>CONCRETE FINISH</td></tr> <tr><td>F22</td><td></td></tr> <tr><td>F23</td><td>SWIMMING POOL WALL FINISHES</td></tr> </tbody> </table>		FINISHES		FINISH TAG	COMMENTS	F16		F17	LEATHER	F18	PAINT-GOLD METAL EFFECT	F19		F20	GREY STONE	F21	CONCRETE FINISH	F22		F23	SWIMMING POOL WALL FINISHES														
FINISHES																																			
FINISH TAG	COMMENTS																																		
F16																																			
F17	LEATHER																																		
F18	PAINT-GOLD METAL EFFECT																																		
F19																																			
F20	GREY STONE																																		
F21	CONCRETE FINISH																																		
F22																																			
F23	SWIMMING POOL WALL FINISHES																																		
 SPOT RECESSED LIGHT  PENDANT LIGHT  HIDDEN LIGHT  CHANDELIER  WALL MOUNTED  NEON RECTANGULAR																																			
Project Type	Residential																																		
Owner	Khalid Khadir Hasan AL-Saeed																																		
Location	Amman																																		
Plot No.	1659																																		
Basin No.	19																																		
Designed by	A.Shaker Khulief 4809																																		
SHEET NAME																																			
ROOF FLOOR TOILET																																			
ID-4330																																			
Date	08/10/2019																																		
Scale	As indicated																																		

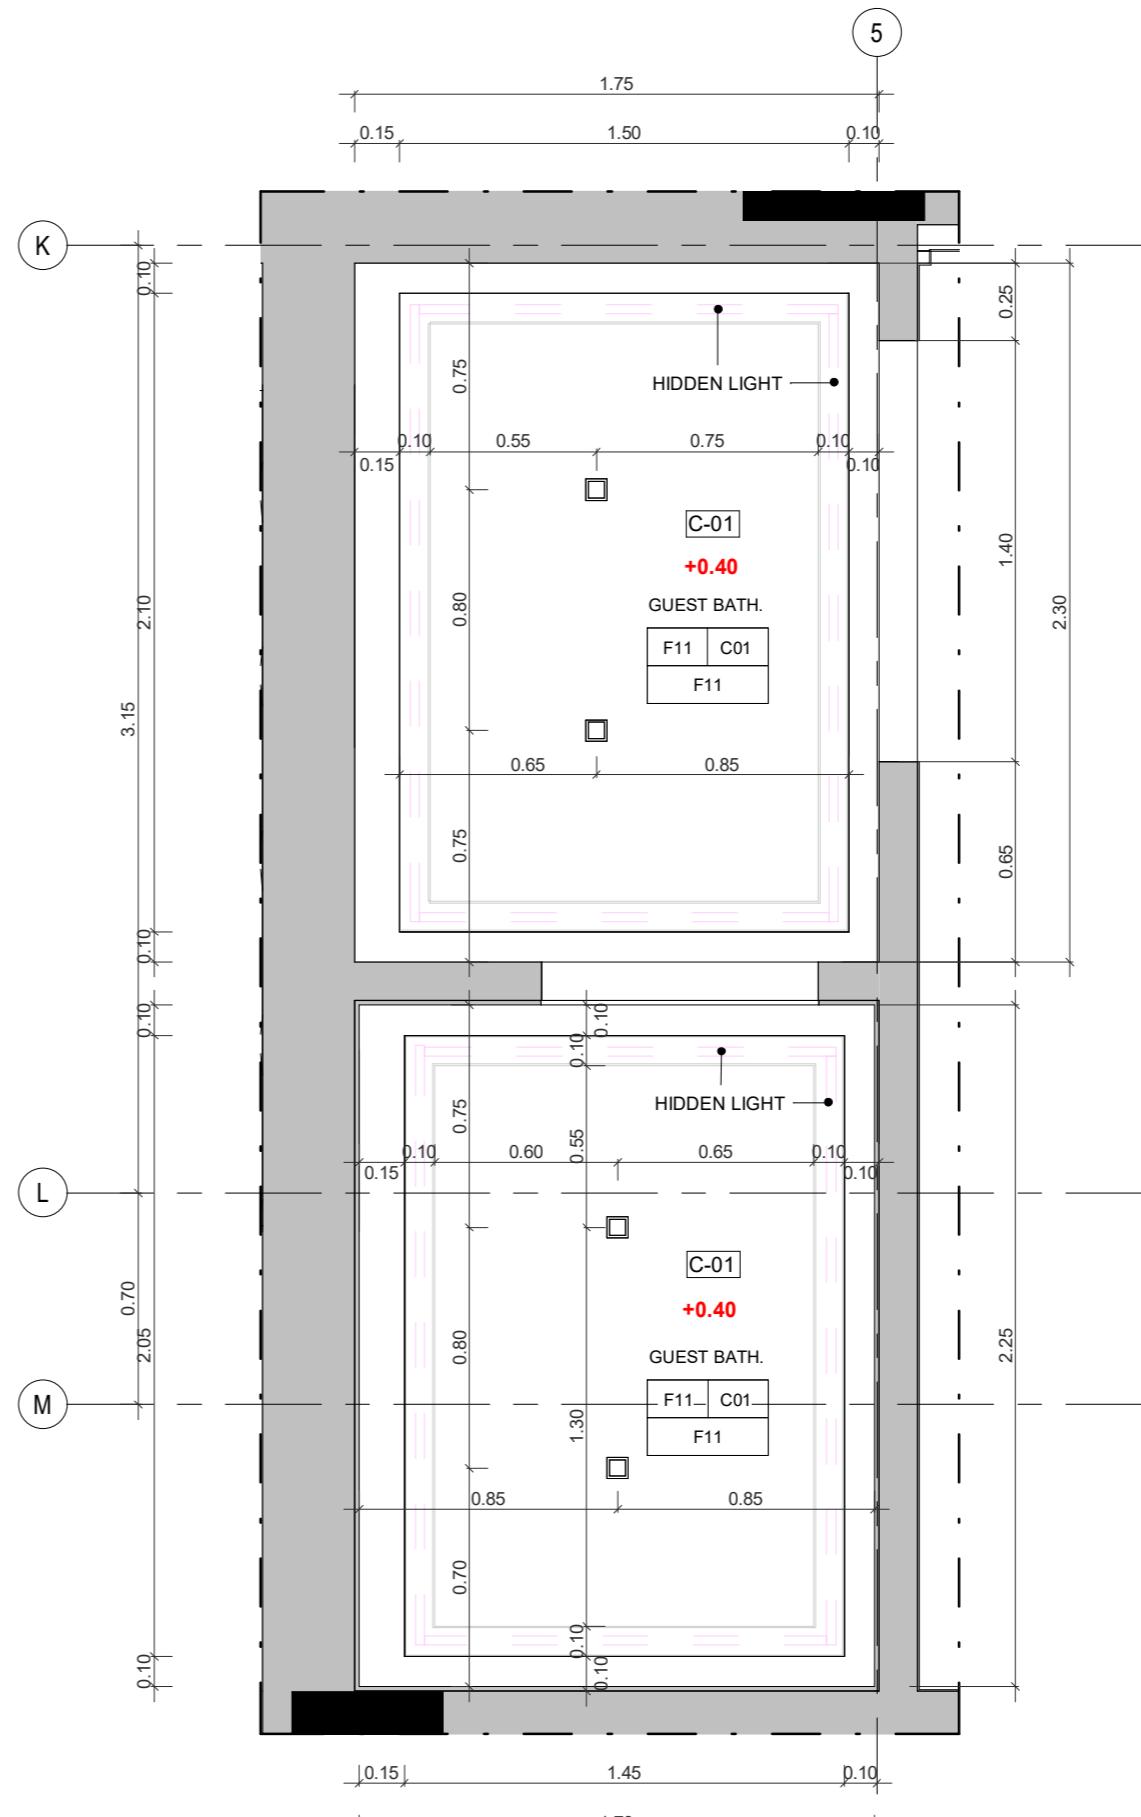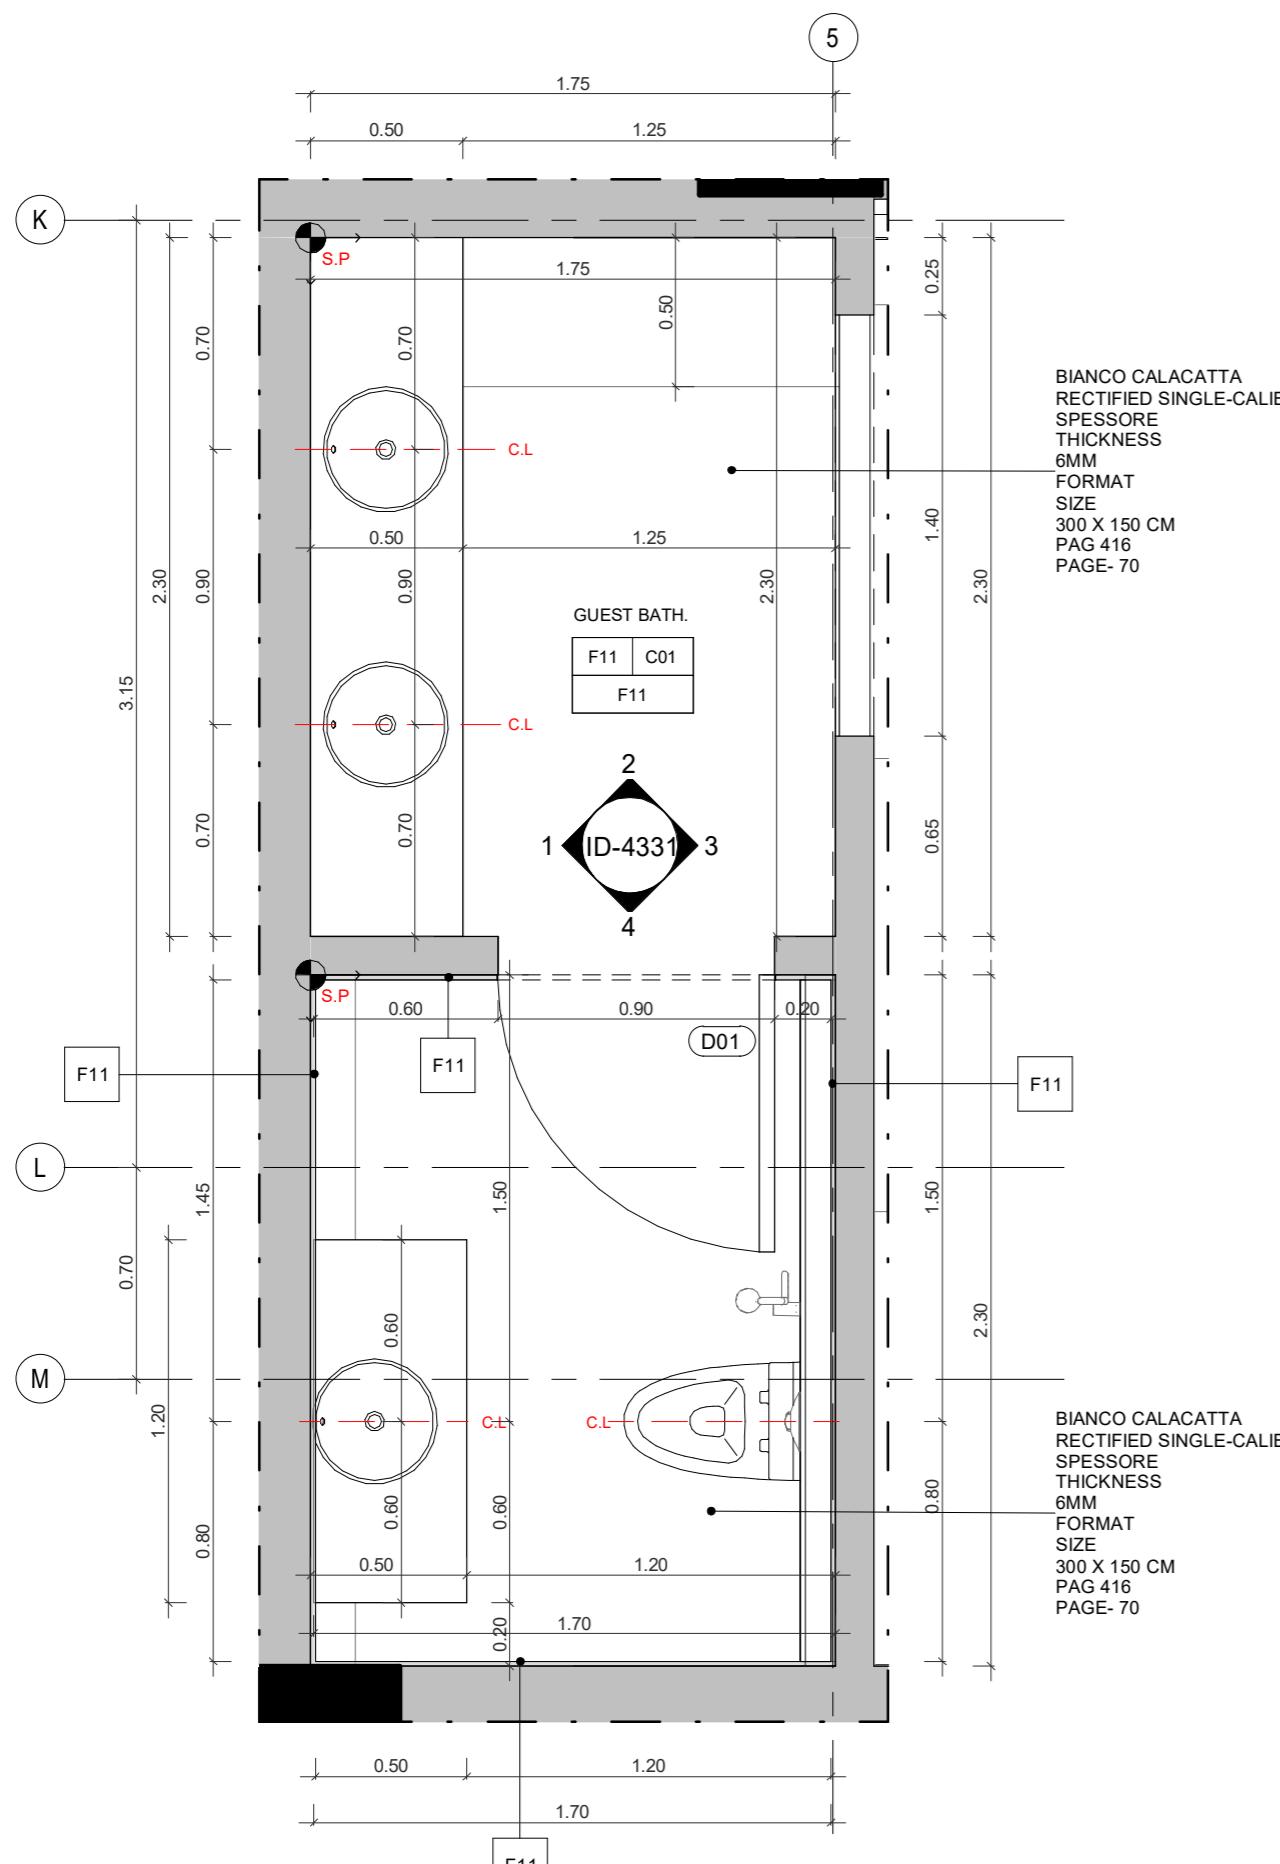

1 TILING PLAN-TOILET
1 : 25

2 CEILING PLAN-TOILET
1 : 25

PROJECT NAME

APARTMENTS BUILDING

NOTES

FOR FINISHES REFER TO SHEETS:
ID-6000
ID-6001

ROOM NAME

FLOOR FINISH	CEILING FINISH
--------------	----------------

WALL FINISH

FINISHES	
FINISH TAG	COMMENTS
F01	
F02	
F03	GOLD STONE
F04	DARK WOOD
F05	DARK WOOD
F06	WOOD
F07	BLACK MARBLE
F08	BEIGE MARBLE
F09	GREY STONE
F10	WALL PAPER
F11	
F12	
F13	BLACK PAINT
F14	CALACATTA
F15	BEIGE PAINT

Project Type Residential

Owner Khalid Khadir Hasan AL-Saeed

Location Amman

Plot No. 1659

Basin No. 19

Designed by A.Shaker Khulief 4809





SHEET NAME

ROOF FLOOR TOILET ELEVATIONS

ID-4331

Date 08/10/2019

Scale 1 : 25

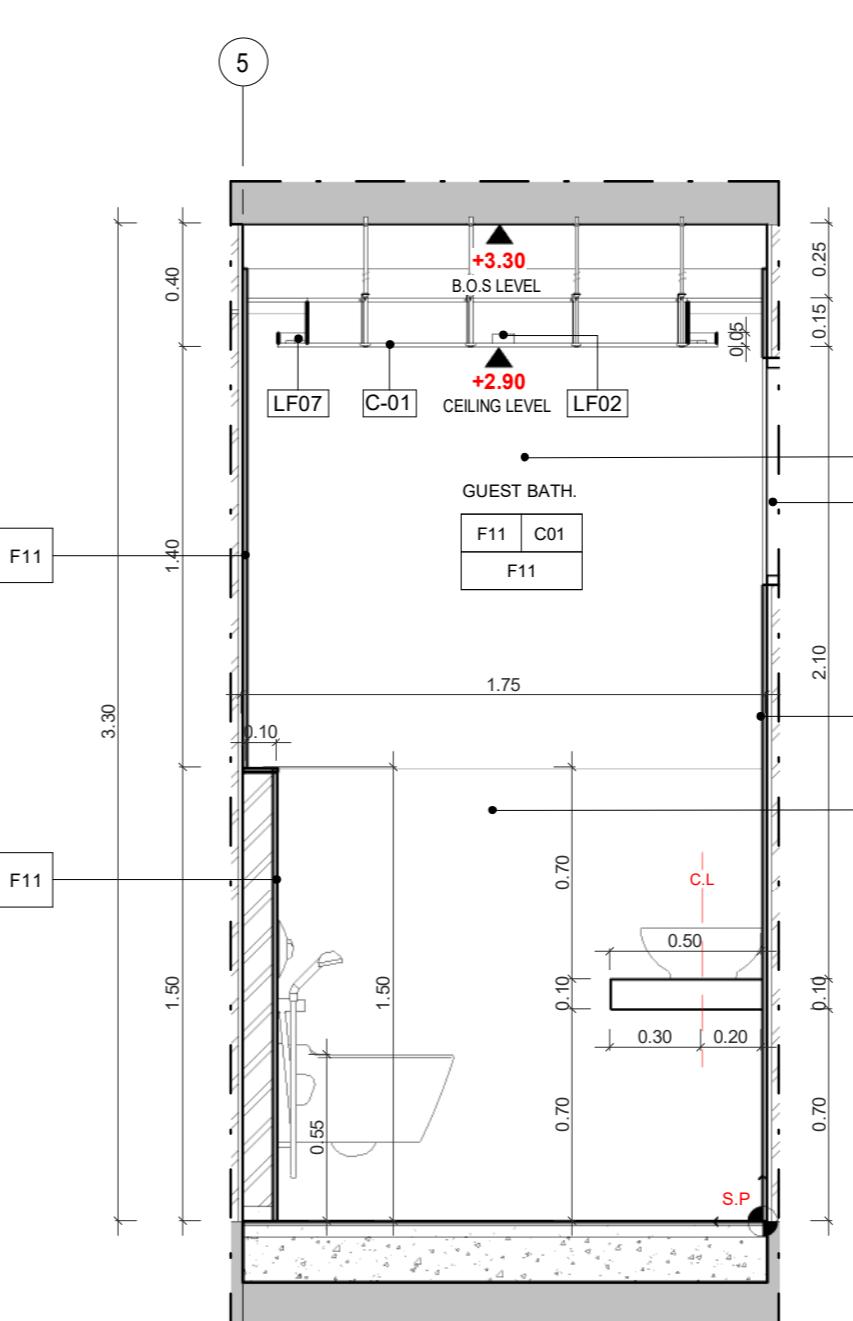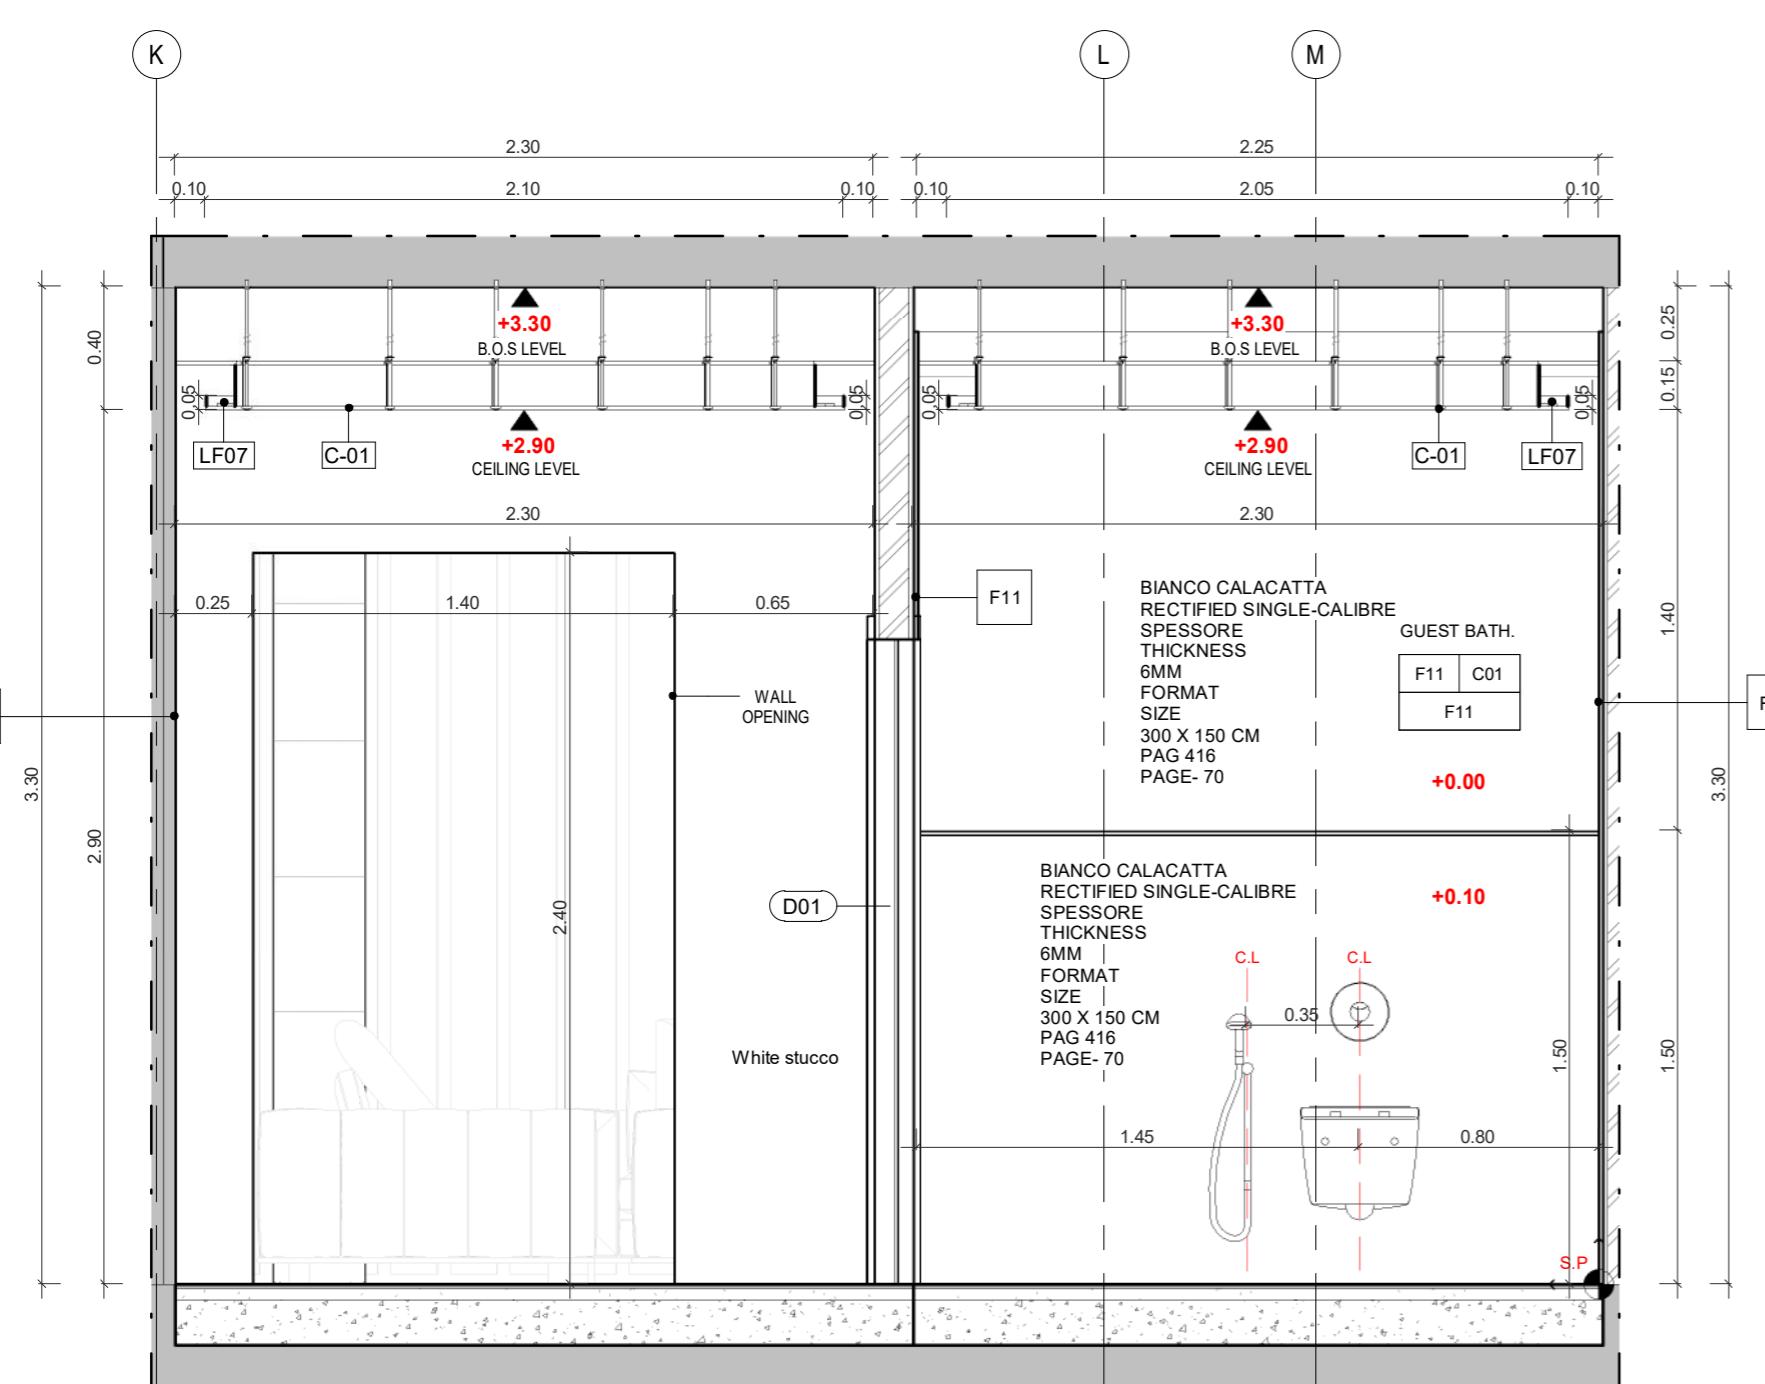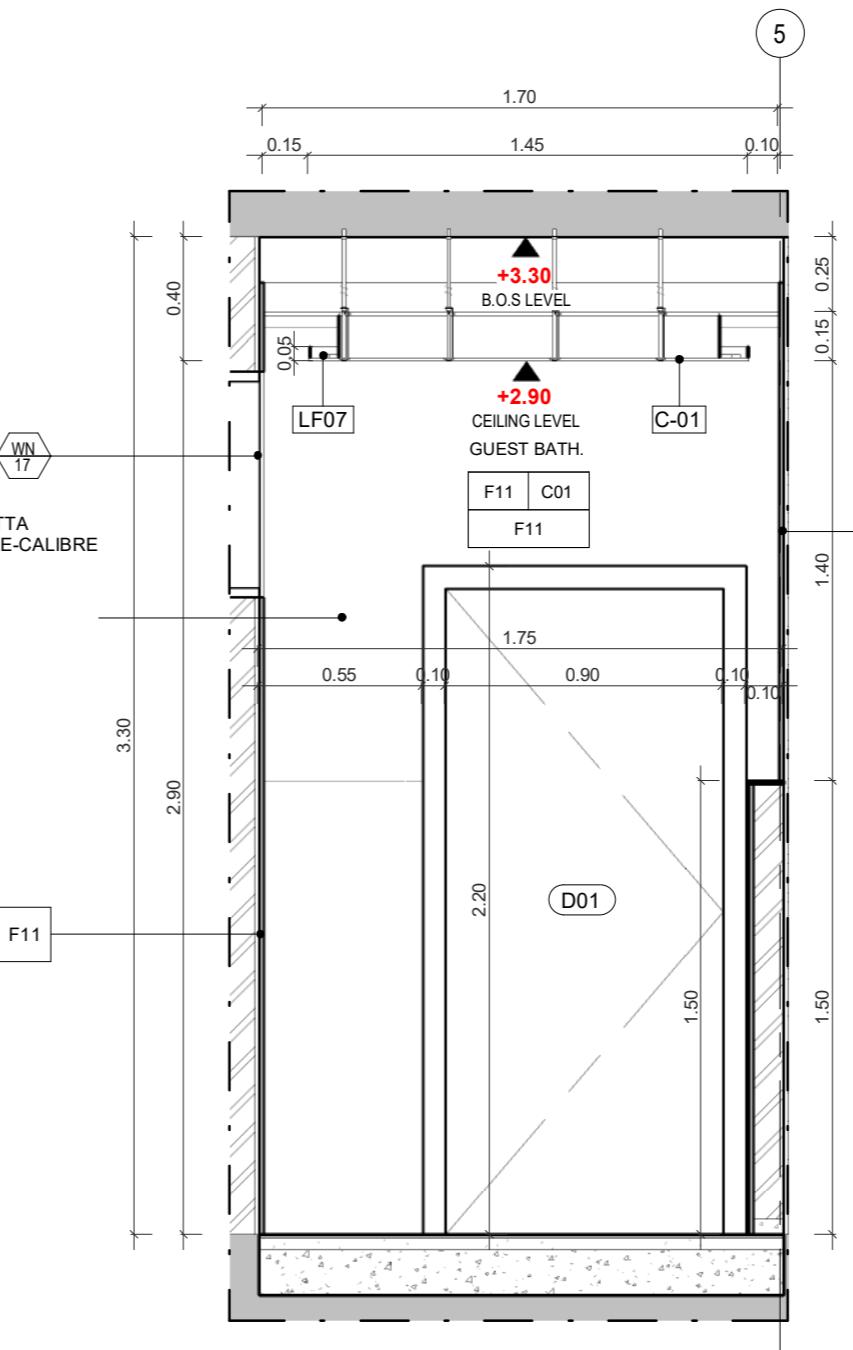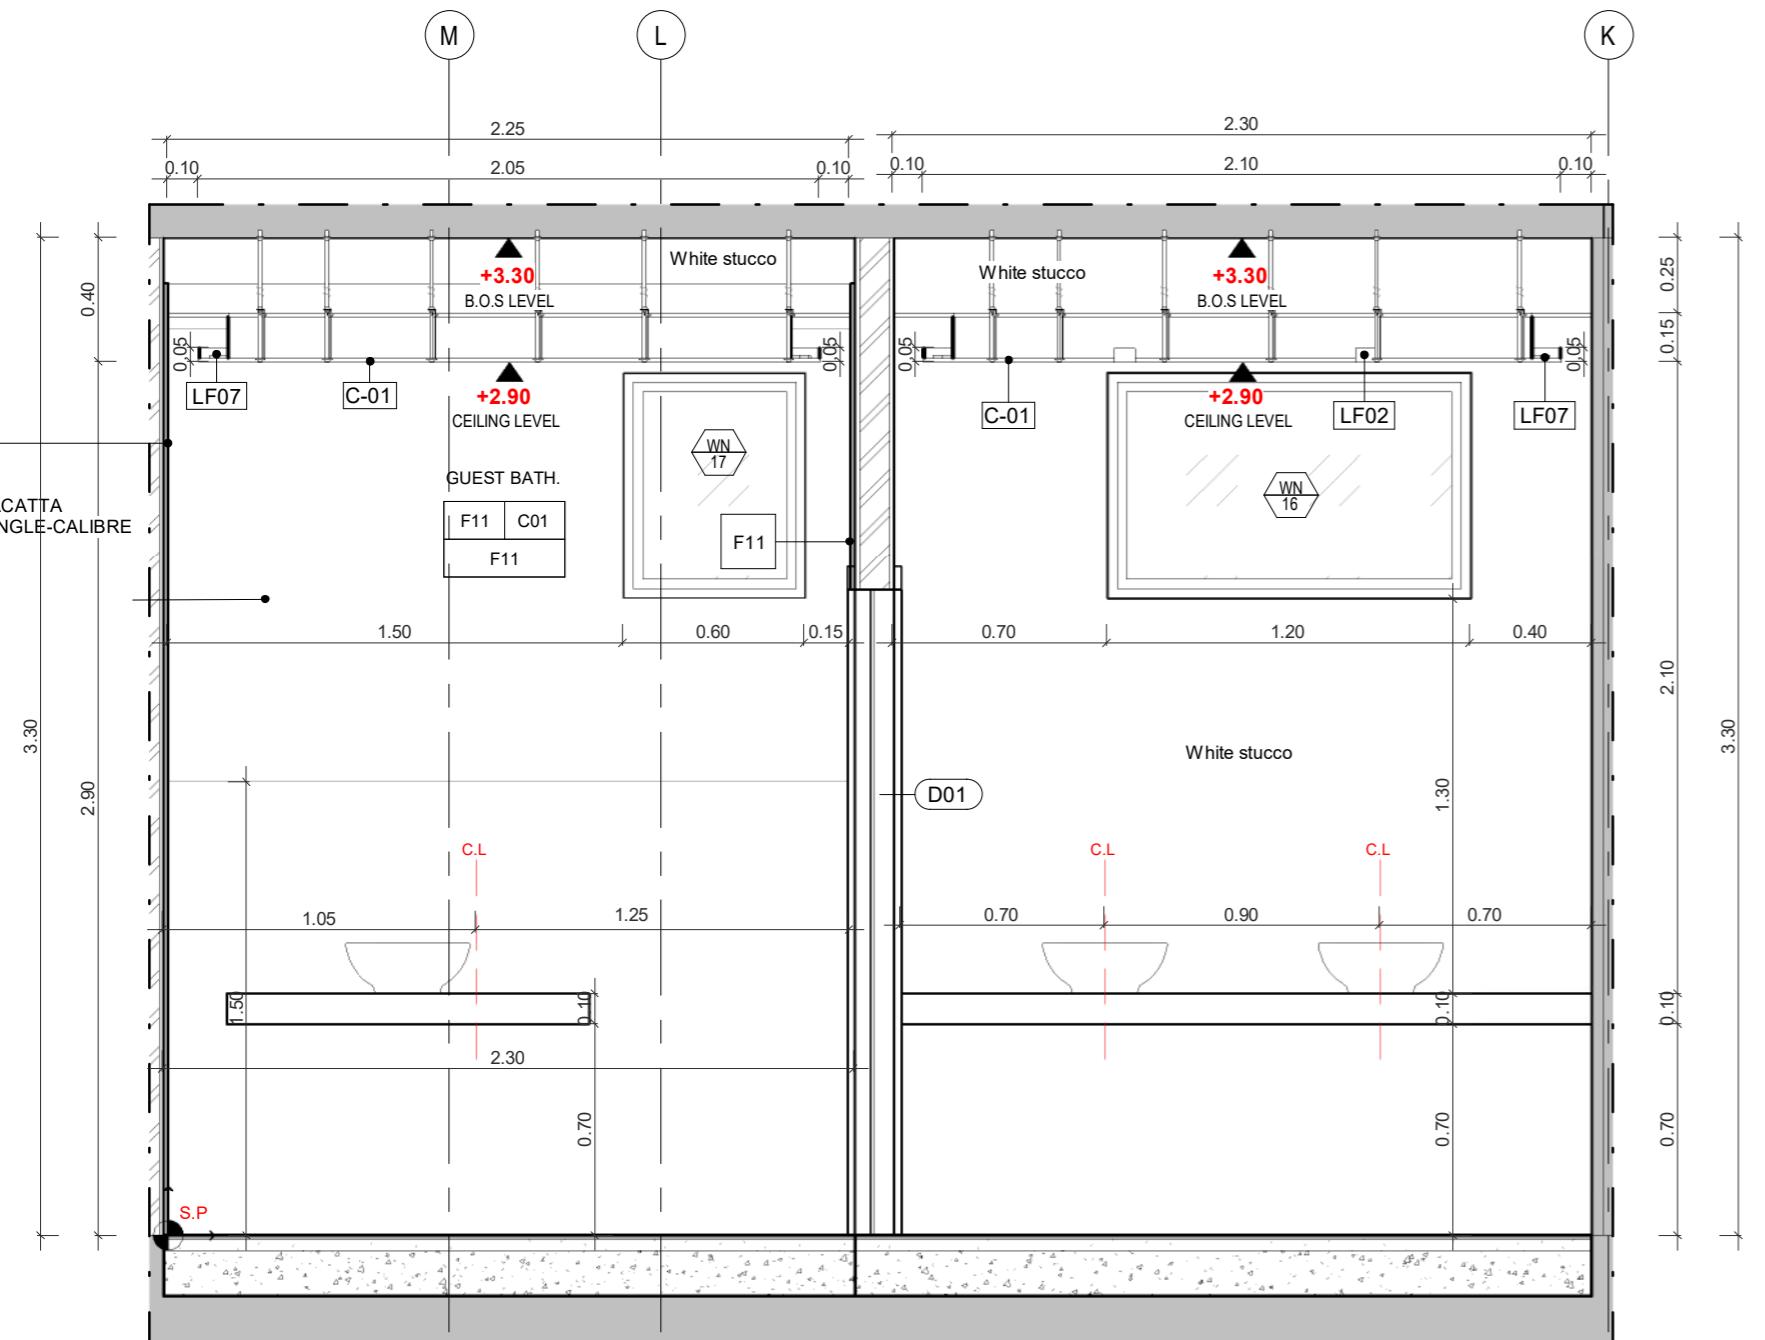

PROJECT NAME
**KHALID AL-SAEED-ID
MODEL**

NOTES

Project Type	Residential
Owner	AL-OLA
Location	NA'OR-AMMAN
Plot No.	
Basin No.	
Designed by	

SHEET NAME

FINISHES QUANTITIES

ID-6000

Date	06/16/19
Scale	

WALL FINISHES				
Description	Material Tag	Material: Area	Material: Model	Area + 15%
WALL FINISH	F01	1199 m ²	WHITE PAINT	1379 m ²
PATTERN FINISH	F02	5 m ²	GOLD WOOD	6 m ²
WALL FINISH	F02	190 m ²	GOLD WOOD	218 m ²
WALL FINISH	F03	38 m ²	GOLD STONE	44 m ²
WALL FINISH	F04	47 m ²	DARK WOOD	54 m ²
WALL FINISH	F05	8 m ²	DECORATIVE STONE	9 m ²
WALL FINISH	F06	39 m ²	WOOD	45 m ²
WALL FINISH	F07	7 m ²	BLACK MARBLE	8 m ²
WALL FINISH	F08	42 m ²	BEIGE MARBLE	48 m ²
WALL FINISH	F09	11 m ²	GREY STONE	13 m ²
WALL FINISH	F10	13 m ²	WALL PAPER	14 m ²
WALL FINISH	F11	392 m ²	CALCATTAA	450 m ²
WALL FINISH	F12	158 m ²	SWIMMING POOL MARBLE	181 m ²
WALL FINISH	F13	11 m ²	BLACK PAINT	12 m ²
WALL FINISH	F14	19 m ²	CALCATTAA	21 m ²
WALL FINISH	F15	10 m ²	BEIGE PAINT	12 m ²
WALL FINISH	F16	84 m ²	TRAVERTINO MARBLE	96 m ²
WALL FINISH	F18	21 m ²	PAINT GOLD METAL EFFECT	24 m ²
PATTERN FINISH	F19	44 m ²	DECORATIVE WOOD	51 m ²
WALL FINISH	F19	2 m ²	DECORATIVE WOOD	3 m ²
WALL FINISH	F20	32 m ²	GREY STONE	37 m ²
WALL FINISH	F21	51 m ²	CONCRETE FINISH	59 m ²
WALL FINISH	F22	7 m ²	KITCHENNE TE WOOD	8 m ²
WALL FINISH	F23	22 m ²	SWIMMING POOL WALL FINISH	25 m ²
WALL FINISH	F25	233 m ²	WHITE FINISH GRC	267 m ²
PATTERN FINISH	F ISLAMIC	11 m ²	DECORATIVE PATTERN	12 m ²

FLOOR FINISHES					
Description	Material Tag	Material: Area	Material: Model	Surface By Room	AREA +15%
FLOOR FINISH	F03	13 m ²	GOLD STONE	MATTE	15 m ²
FLOOR FINISH	F04	3 m ²	DARK WOOD	SOFT	4 m ²
FLOOR FINISH	F06	2 m ²	WOOD	MATTE	3 m ²
FLOOR FINISH	F08	2 m ²	BEIGE MARBLE	MATTE	2 m ²
FLOOR FINISH	F11	142 m ²	CALCATTAA	MATTE	163 m ²
FLOOR FINISH	F11	467 m ²	CALCATTAA	SOFT	538 m ²
FLOOR FINISH	F12	7 m ²	SWIMMING POOL MARBLE	SOFT	8 m ²
FLOOR FINISH	F16	332 m ²	TRAVERTINO MARBLE	MATTE	382 m ²
FLOOR FINISH	F23	57 m ²	SWIMMING POOL WALL FINISH	MATTE	66 m ²
FLOOR FINISH	F24	262 m ²	PARQUET	SOFT	302 m ²

CEILING FINISHES				
Description	Material Tag	Material: Area	Material: Model	Area + 15%
CEILING FINISH	F01	1208.43 m ²	WHITE PAINT	1389.69 m ²
CEILING FINISH	F02	0.40 m ²	GOLD WOOD	0.46 m ²
CEILING FINISH	F04	108.88 m ²	DARK WOOD	125.21 m ²
CEILING FINISH	F11	10.32 m ²	CALCATTAA	11.87 m ²
CEILING FINISH	F15	10.36 m ²	BEIGE PAINT	11.91 m ²
CEILING FINISH	F18	2.65 m ²	PAINT GOLD METAL EFFECT	3.05 m ²
CEILING FINISH	F19	23.21 m ²	DECORATIVE WOOD	26.69 m ²
PATTERN CEILING FINISH	F19	11.75 m ²	DECORATIVE WOOD	13.52 m ²
CEILING FINISH	F20	23.49 m ²	GREY STONE	27.02 m ²
CEILING FINISH	F21	32.51 m ²	CONCRETE FINISH	37.39 m ²
CEILING FINISH	F22	13.80 m ²	KITCHENNE TE WOOD	15.87 m ²
CEILING FINISH	F25	6.82 m ²	WHITE FINISH GRC	7.84 m ²

PROJECT NAME

APARTMENTS BUILDING

NOTES

Door schedule					
Level	Width	Moving Height	Fixed Height	Comments	Count
BASEMENT FLOOR					
BASEMENT FLOOR	700.00	2400.00	450.00	Indoor	1
BASEMENT FLOOR	900.00	2400.00	450.00	Indoor	7
BASEMENT FLOOR	1000.00	2400.00	450.00	Indoor	7
BASEMENT FLOOR	2100.00	3400.00	450.00	Gate Basement	1
GROUND FLOOR					
GROUND FLOOR	800.00	2400.00	750.00	Indoor	3
GROUND FLOOR	900.00	2400.00	750.00	Indoor	4
GROUND FLOOR	1000.00	2400.00	750.00	Indoor	5
GROUND FLOOR	1250.00	2400.00	750.00	Stair Outdoor	1
GROUND FLOOR	1800.00	2400.00	750.00	Entrance Outdoor	1
GROUND FLOOR	2300.00	2400.00	750.00	Gate Door	1
WIP FIRST FLOOR					
WIP FIRST FLOOR	700.00	2400.00	600.00	Indoor	2
WIP FIRST FLOOR	900.00	2400.00	600.00	Indoor	9
WIP FIRST FLOOR	900.00	2400.00	600.00	Terrace Outdoor	1
WIP FIRST FLOOR	1000.00	2400.00	600.00	Indoor	6
WIP ROOF FLOOR-MASTER BATHROOM					
WIP ROOF FLOOR-MASTER BATHROOM	800.00	2400.00	600.00	Indoor	3
WIP ROOF FLOOR-MASTER BATHROOM	900.00	2400.00	600.00	Indoor	1
WIP ROOF FLOOR-MASTER BATHROOM	1000.00	2400.00	600.00	Indoor	2
WIP ROOF FLOOR-MASTER BATHROOM	1000.00	2400.00	600.00	Indoor Glass	1
WIP ROOF FLOOR-MASTER BATHROOM	1000.00	2400.00	600.00	Terrace outdoor	1

Project Type	Residential
Owner	Khalid Khadir Hasan AL-Saeed
Location	Amman
Plot No.	1659
Basin No.	19
Designed by	A.Shaker Khulief 4809

SHEET NAME
DOORS SCHEDULE
ID-6100
Date 10/14/19
Scale